

10 EXTERIOR WALL MOUNTED LIGHT - SEE ELECTRICAL DRAWINGS.

1. SEE SHEET A2.1 AND A2.2 FOR LAY-IN CEILING DETAILS.
2. FOR RECESSED LIGHTING STRIP DETAIL AT T-BAR CEILING IN OFFICES AND CONFERENCE ROOMS, SEE DETAILS ON SHEET A2.1. COORDINATE WITH ELECTRICAL DRAWINGS.

1. SUSPENDED 2'X4' ACOUSTICAL CEILING SYSTEM

2. SUSPENDED 2'X4' ACOUSTICAL CEILING SYSTEM WITH LAY-IN BATT SOUND INSULATION ABOVE. SEE 11A2.1 FOR MODIFICATIONS AT RECESSED STRIP LIGHTING IN OFFICES AND CONFERENCE ROOMS.

3. SUSPENDED 2'X2' ACOUSTICAL CEILING SYSTEM

4. SUSPENDED WOOD SLAT CEILING SYSTEM. SEE 2/A2.1 FOR MODIFICATIONS AT CEILING ACCESSORIES.

5. HARDLID GYPSUM CEILING (PAINT GREAT WHITE KMW49 U.O.N.)

6. CEMENTITIOUS SOFFIT BOARDS

7. EXPOSED ROOF FRAMING / TJIS (PAINT STONE HEARTH KM4896 U.O.N.)

8. CORRUGATED METAL SIDING/ SOFFIT PANELS

9. XX" SEE SPEC SECTION 09 53 00.

10. CORRUGATED METAL SIDING/ SOFFIT PANELS


11. SUSPENDED ACOUSTICAL BLADES. # INDICATES PANEL LENGTH. SEE SPEC SECTION 09 53 00.

12. SUSPENDED ACOUSTICAL BLADES. # INDICATES PANEL LENGTH. SEE SPEC SECTION 09 53 00.


13. SUSPENDED ACOUSTICAL BLADES. # INDICATES PANEL LENGTH. SEE SPEC SECTION 09 53 00.

14. SUSPENDED ACOUSTICAL BLADES. # INDICATES PANEL LENGTH. SEE SPEC SECTION 09 53 00.

	HVAC SUPPLY UNIT, SEE MECHANICAL DRAWINGS.
	HVAC CONSOLE UNIT, SEE MECHANICAL DRAWINGS.
	HVAC RETURN UNIT, SEE MECHANICAL DRAWINGS.
	PENDANT LIGHT FIXTURE, SEE ELECTRICAL DRAWINGS.
	PENDANT LIGHT FIXTURE, SEE ELECTRICAL DRAWINGS.
	RECESSED LIGHT FIXTURE, SEE ELECTRICAL DRAWINGS.
	LIGHT FIXTURE, SEE ELECTRICAL DRAWINGS.
	ILLUMINATED EXIT SIGN, SEE ELECTRICAL DRAWINGS.
	UNIT SKYLIGHT.
	1-HR FOR RATED OCCUPANCY SEPARATION.

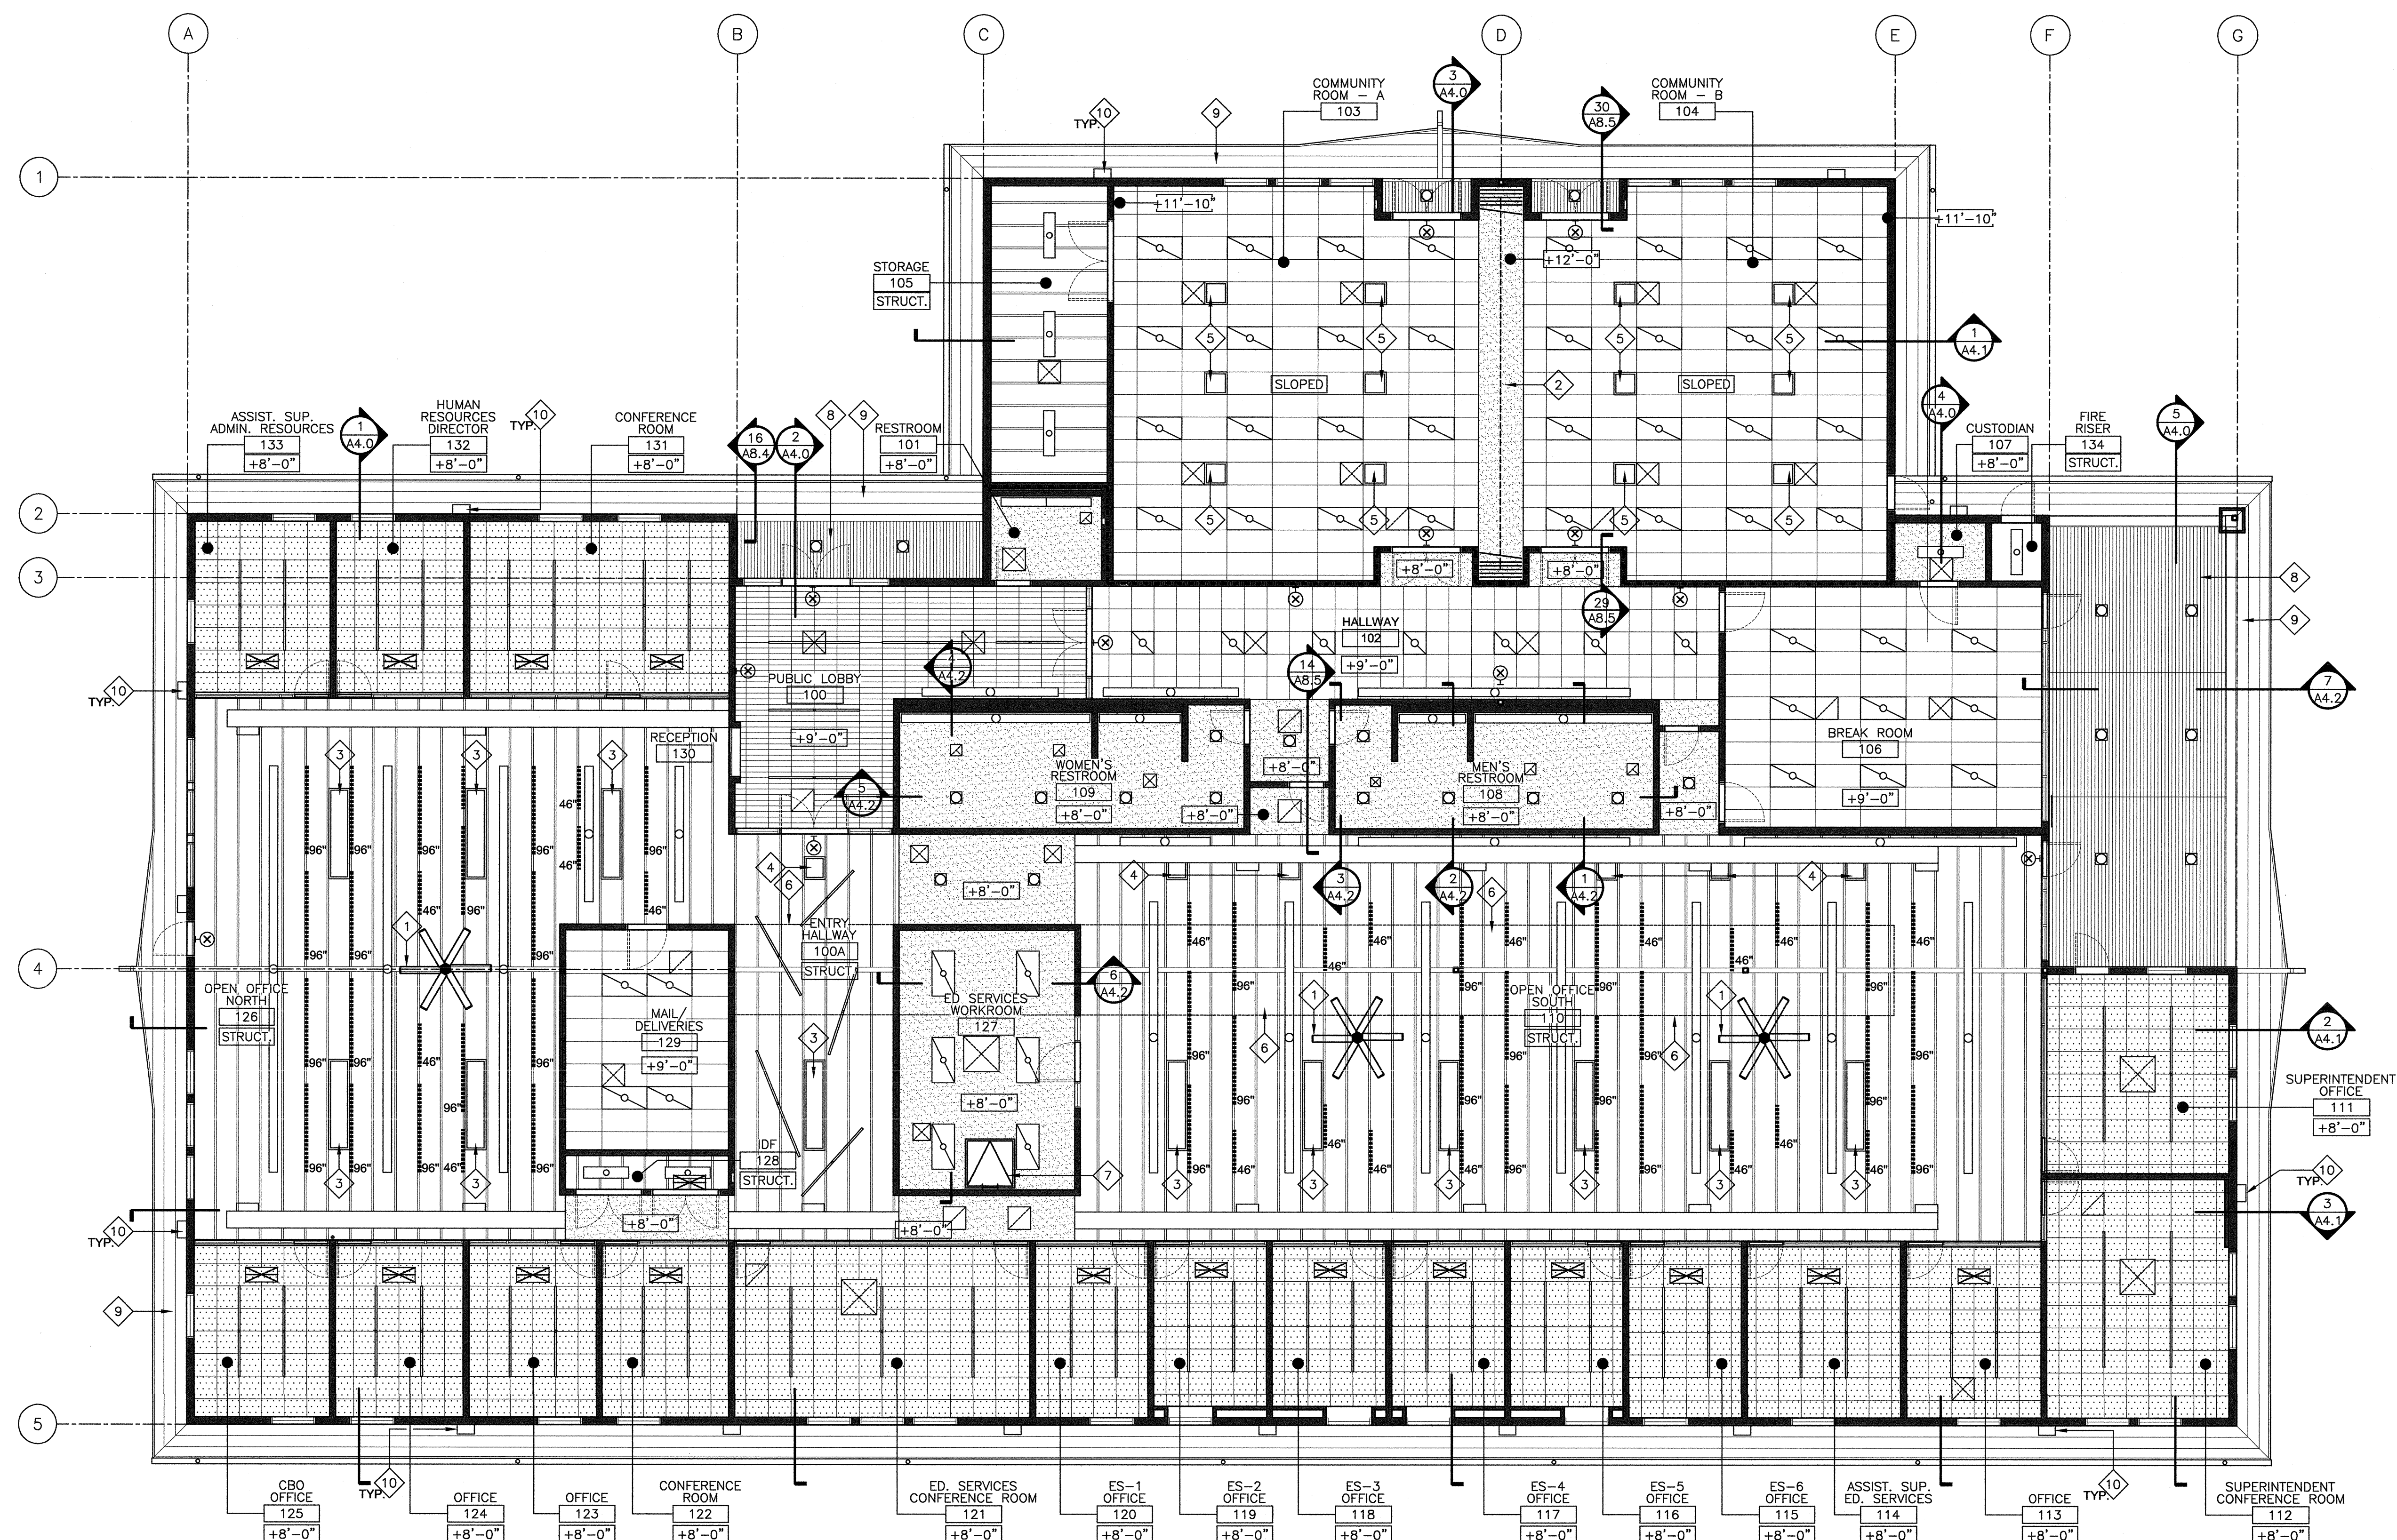

1 Reflected Ceiling Plan
SCALE: 1/8" = 1'-0"



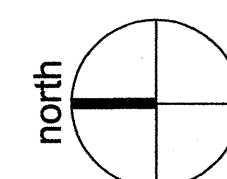


**Dry Creek Joint Elementary School District
District Education Center**

8849 Cook Riolo Road, Roseville, CA 95747

Dry Creek Joint Elementary School District

ONE INCH = TWENTY FEET
ONE-SIXTEENTH INCH = ONE FOOT
ONE-EIGHTH INCH = ONE FOOT
ONE-FOURTH INCH = ONE FOOT
ONE-HALF INCH = ONE FOOT
THREE-QUARTERS INCH = ONE FOOT
ONE INCH = ONE FOOT
ONE AND ONE-HALF INCH = ONE FOOT

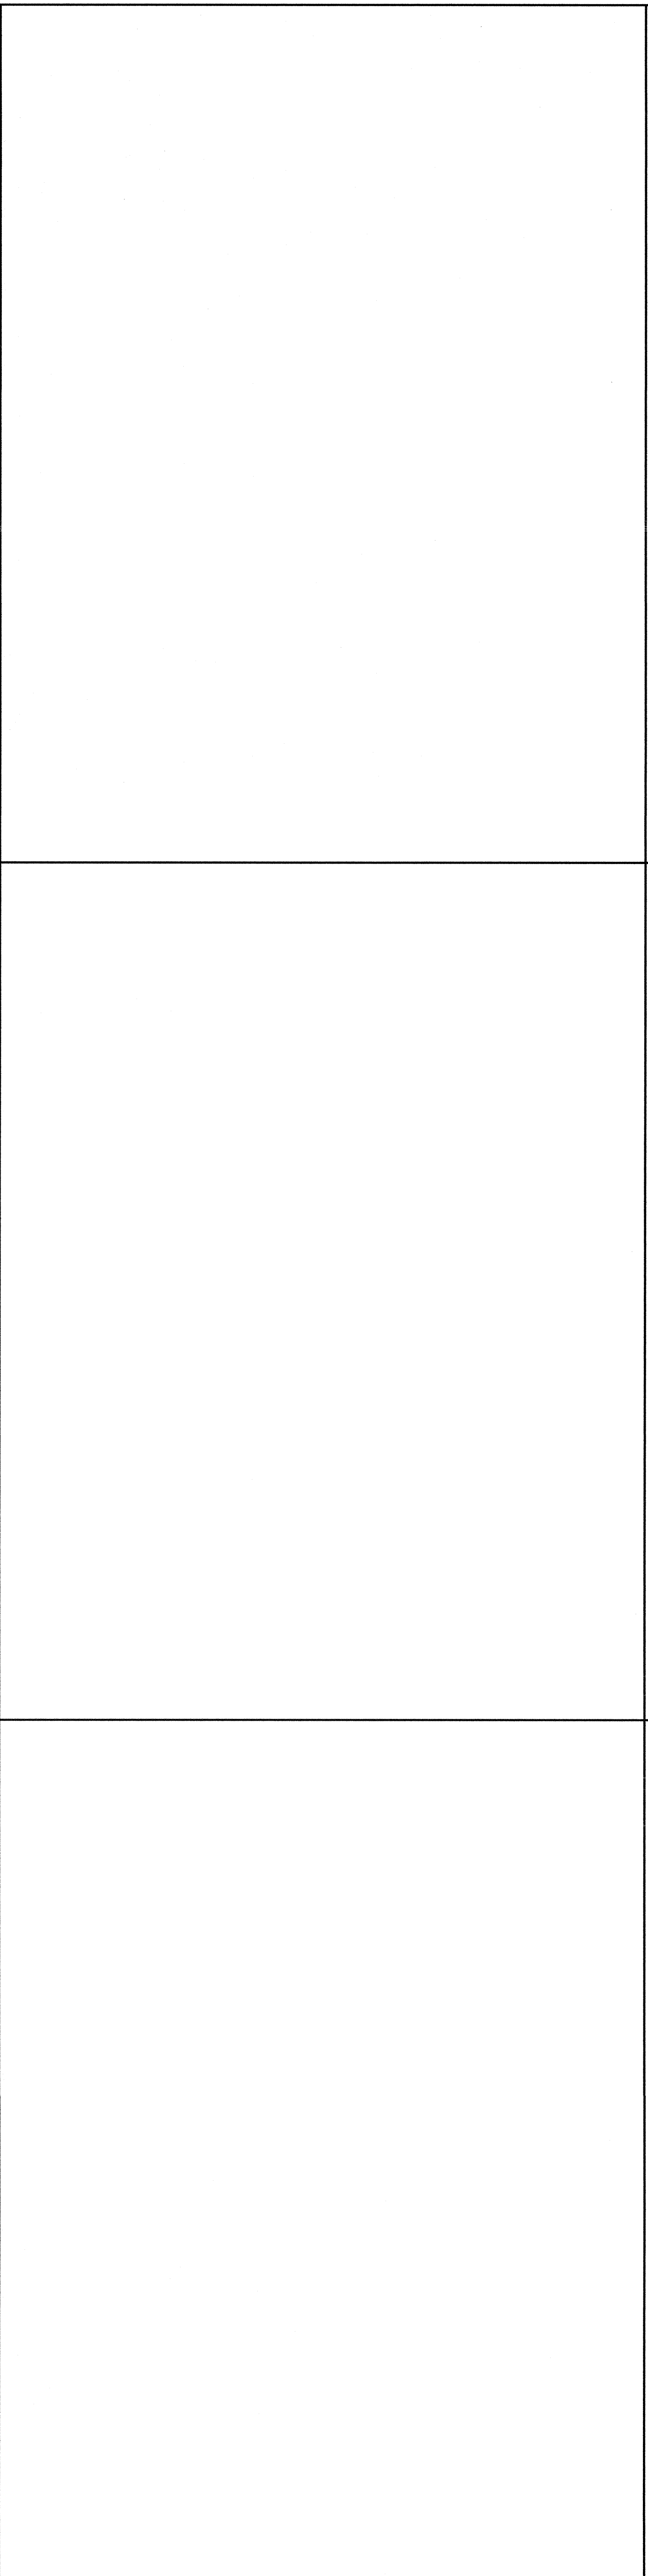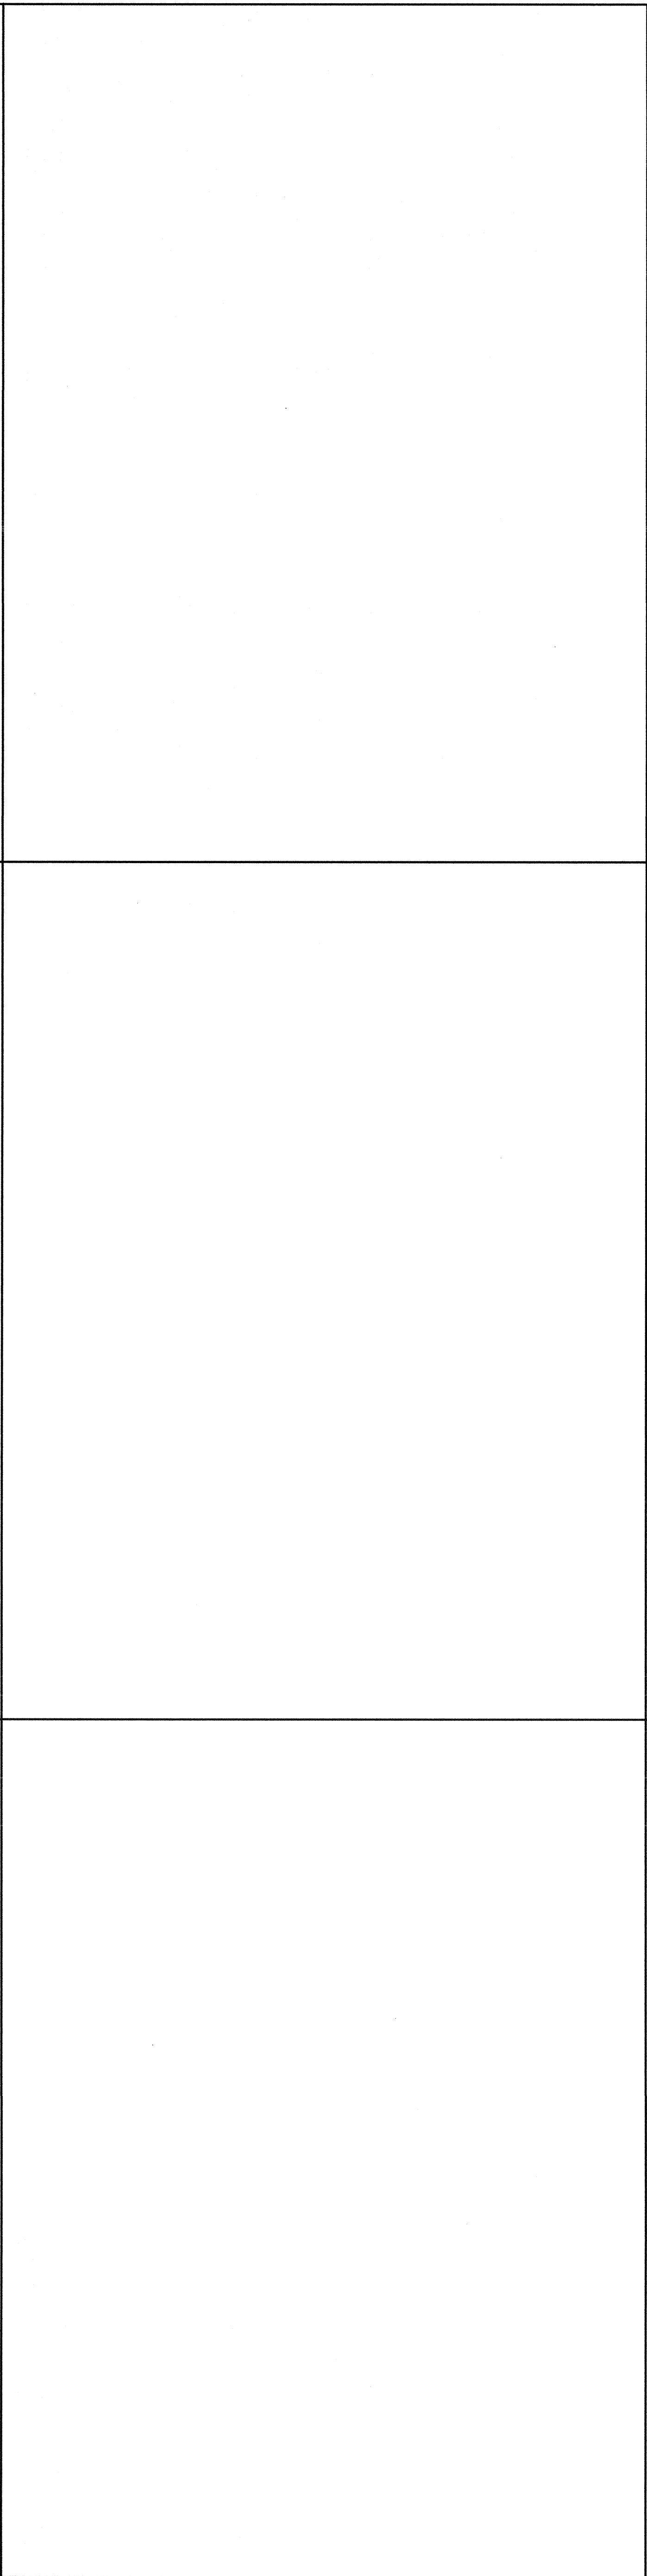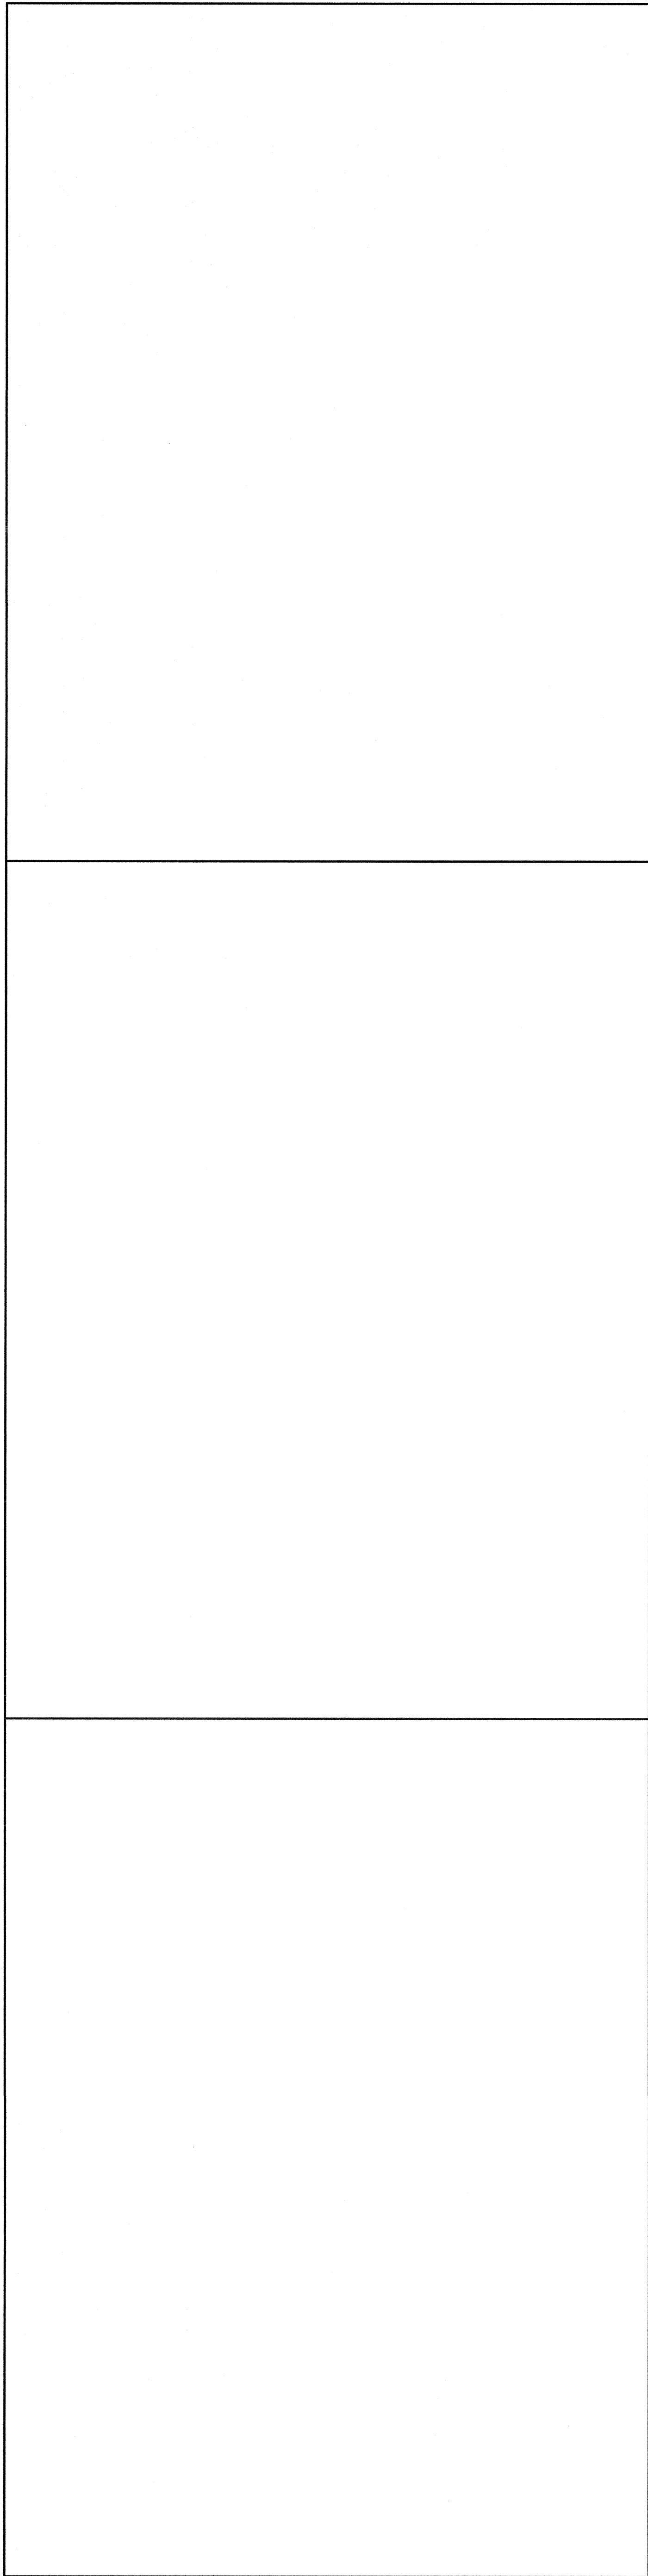

9/14/2015 2:10:07 PM

STRUCTURAL CONDITION OF FLOOR/ ROOF ABOVE COMPRESSION STRUT	APPLICABLE DETAIL
METAL DECK	5.20
CONCRETE OVER METAL DECK	5.21
CONCRETE SLAB, BEAM, OR JOIST	5.30
STRUCTURAL STEEL	5.40
SAWN TIMBER WITH GYPSUM BOARD	5.50
SAWN TIMBER WITHOUT GYPSUM BOARD	5.60

Basic Document : DSA IR 25-2.13

Sheet Title : COMPRESSION STRUT CONNECTION TO STRUCTURE - CONNECTION MATRIX

rev. 09-21-15

Sheet No: 5.10

DSA IR 25-2.13 - Appendix A (rev 02/10/16)44 of 51

9/14/2015 2:10:04 PM

STRUCTURAL CONDITION OF FLOOR/ ROOF ABOVE SUSPENDED CEILING	APPLICABLE HANGER WIRE DETAIL	APPLICABLE BRACING WIRE DETAIL
-METAL DECK	4.20	4.30
CONCRETE OVER METAL DECK	4.21	4.31
CONCRETE SLAB, BEAM, OR JOIST	4.22	4.32
-STRUCTURAL STEEL	4.23	4.33
-METAL STUD WALL	4.24	4.34
SAWN TIMBER	4.25, 4.29	4.35
WOOD JOIST	4.26	4.36, 4.37
WOOD CHORD TRUSS	4.27, 4.29	4.38, 4.29
-OPEN WEB STEEL JOIST	4.28, 4.29	4.39, 4.29

Basic Document : DSA IR 25-2.13

Sheet Title : HANGER AND BRACING WIRE CONNECTION MATRIX

rev. 09-21-15

Sheet No: 4.11

DSA IR 25-2.13 - Appendix A (rev 02/10/16)23 of 51

9/14/2015 2:10:08 PM

#12 GAGE HANGER WIRES (3) TIGHT TURNS WITHIN 3" AT BRACE WIRE PROVIDE (4) TIGHT TURNS WITHIN 1 1/2".

SADDLE TIE REQUIRED FOR ALL WIDTHS GREATER THAN 1 1/2"

MAIN CHANNEL SHOWN (WOOD FRAMING SIMILAR)

SADDLE TIE HAS DOUBLE LOOP AT SUPPORT

WHEN MULTIPLE SADDLE TIES ARE REQUIRED THEY SHALL ALTERNATE BACK AND FORTH TO PREVENT TWISTING

TYPICAL SADDLE TIE DETAIL
HANGER WIRE CONDITION SHOWN. BRACE WIRE CONDITION SIMILAR

Basic Document : DSA IR 25-2.13

Sheet Title : TYPICAL SADDLE TIE DETAIL

rev. 09-21-15

Sheet No: 4.29

DSA IR 25-2.13 - Appendix A (rev 02/10/16)33 of 51

Dry Creek Joint Elementary School District
District Education Center

8849 Cook Riolo Road, Roseville, CA 95747

Dry Creek Joint Elementary School District

FILE NO. 31-15

IDENTIFICATION STAMP DIV. OF THE
STATE ARCHITECT OFFICE OF
REGULATION SERVICES

APPLICATION NO.
02-115456

AC TM FLS HMS SS BL

DATE 4/22/17 CCB

DIVISION OF THE STATE ARCHITECT
revision date: _____ by: _____

CONSULTANT

nacht&lewis

600 O Street, Suite 100
Sacramento, CA 95811
www.nachtlewis.com
916.329.4000

ARCHITECT

INITIAL BOX

NO.	DWG BY	DATE	REVIEWED

REVISIONS

NO.	DESCRIPTION	DATE	REV'D
	100% design development	7/9/16	
	75% construction documents	9/20/16	
	DSA submittal	12/31/16	
	DSA approval	02/23/17	

DATE February 23, 2017

JOB NO. Y1538.00

SHEET TITLE

Acoustic Ceiling
Details

SHEET NO.

A2.2

SHEET ____ OF ____ TOTAL

ONE AND ONE-HALF INCH = ONE FOOT
ONE INCH = ONE FOOT
THREE-QUARTERS INCH = ONE FOOT
ONE-HALF INCH = ONE FOOT
ONE-QUARTER INCH = ONE FOOT
ONE-EIGHTH INCH = ONE FOOT
ONE-SIXTEENTH INCH = ONE FOOT
ONE INCH = TWENTY FEET

KEYNOTES:

THESE KEYNOTES APPLY TO THIS SHEET ONLY.

- 1

RAIN WATER LEADER.
- 2

CEMENTITIOUS CEDARMILL 9-1/4" LAP SIDING.
- 2A

CEMENTITIOUS SMOOTH 6-1/4" LAP SIDING.
- 3

CEMENTITIOUS CEDARMILL VERTICAL SIDING.
- 3A

CEMENTITIOUS SMOOTH VERTICAL SIDING.
- 4

CEMENTITIOUS TRIM BOARD.
- 5

CEMENTITIOUS BATTEN BOARDS @ 24" O.C. ± AS SHOWN FOR BEST SYMMETRY AT WINDOW OPENINGS.
- 6

STANDING SEAM METAL ROOFING.
- 7

CORRUGATED METAL WALL PANEL.
- 8

UNIT SKYLIGHTS.
- 9

GLULAM BEAM WITH METAL WEATHER CAP, SEE DETAIL 14/A8.2.
- 10

HORIZONTAL AND VERTICAL CEMENTITIOUS BATTEN BOARDS @ 24" O.C. ± AS SHOWN FOR BEST SYMMETRY.
- 11

GRAPHIC BUILDING SIGN TYPE S-11 - SEE SPEC SECTION 10 14 00.
- 12

CEMENTITIOUS SHINGLE SIDING.
- 13

PRE-FINISHED METAL GUTTER.
- 14

WOOD PERGOLA, SEE DETAIL SHEETS A0.7 AND A0.8.
- 15

DECORATIVE FENCING ENCLOSURE AT MECHANICAL EQUIPMENT YARD.
- 16

VINYL WINDOW.
- 17

ARCHITECTURAL STORM-PROOF VENT LOUVER - SEE DETAIL 6A7/A8.5 AND SPEC SECTION 08 91 00. SEE ELEVATIONS FOR SIZING.
- 18

FURNACE VENT - SEE MECHANICAL.
- 19

TUBULAR SKYLIGHT.
- 20


ACCESS DOOR INTO CUPLOA SPACE. FULLY FLASH ACCESS DOOR INTO WEATHER BARRIER SYSTEM. FASTEN PIECE OF CORRUGATED METAL WALL PANEL TO FACE OF ACCESS DOOR. SEE SPEC SECTION 08 31 13 AND DETAILS 11&12/A8.5.
- 21

ARCHITECTURAL EXTERIOR GRILLE - SEE SPEC SECTION 08 91 00. SEE ELEVATIONS FOR SIZING. SEE DETAILS 6&8/A8.1.
- 22


UPPER DOWNSPOUT TO SPILL TO LOWER ROOF.

GENERAL SHEET NOTES:


1. ALL METAL WALL AND ROOF PANELS AND GUTTERS SHALL BE FACTORY FINISHED.
2. ALL CEMENTITIOUS PANELING AND TRIM SHALL BE PAINTED. PROVIDE FOR UP TO THREE WALL COLORS AND TWO TRIM COLORS. ARCHITECT TO PROVIDE COLOR CODED ELEVATIONS AT TIME OF SUBMITTAL.
3. FOR TYPICAL CORNER AND TRIM DETAILS FOR CEMENTITIOUS SIDING, SEE DETAILS 13/A8.4, 2&3/A8.5 AND OTHER EXTERIOR DETAILS ON SHEETS A8.1, A8.2, A8.3, A8.4, AND A8.5.
4. AT ALL EXTERIOR LIGHTS, FIRE ALARM DEVICES, ACCESSORIES, ETC. LOCATED IN LAP SIDING SHALL BE INSTALLED PER DETAIL 8/A8.5.

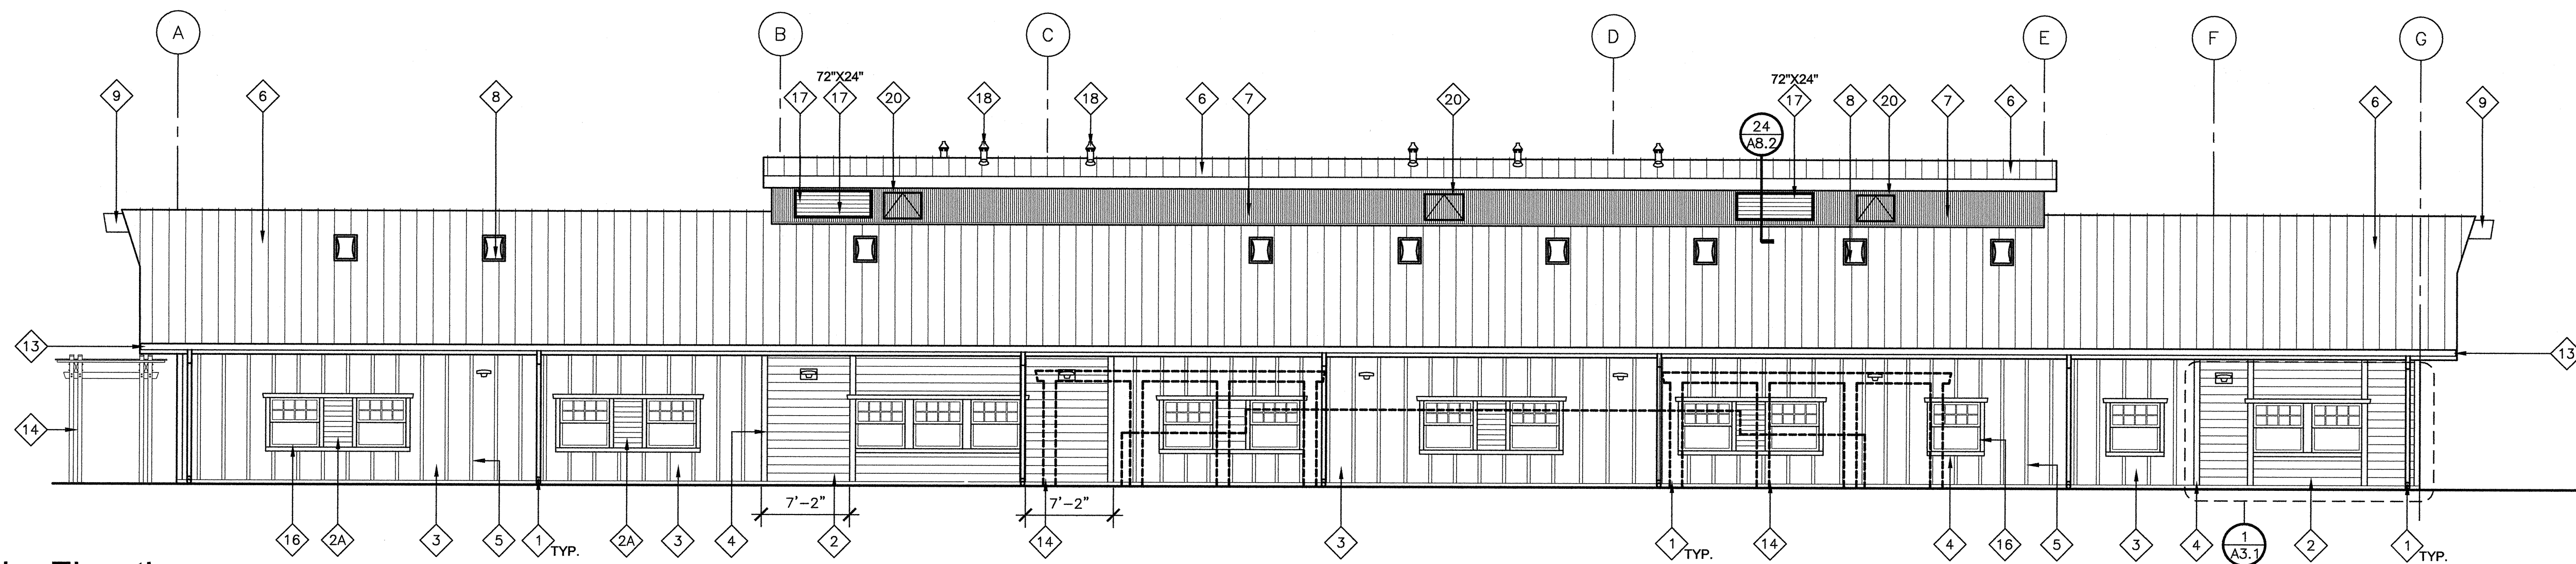


4 West Exterior Elevation
SCALE: 1/8" = 1'-0"

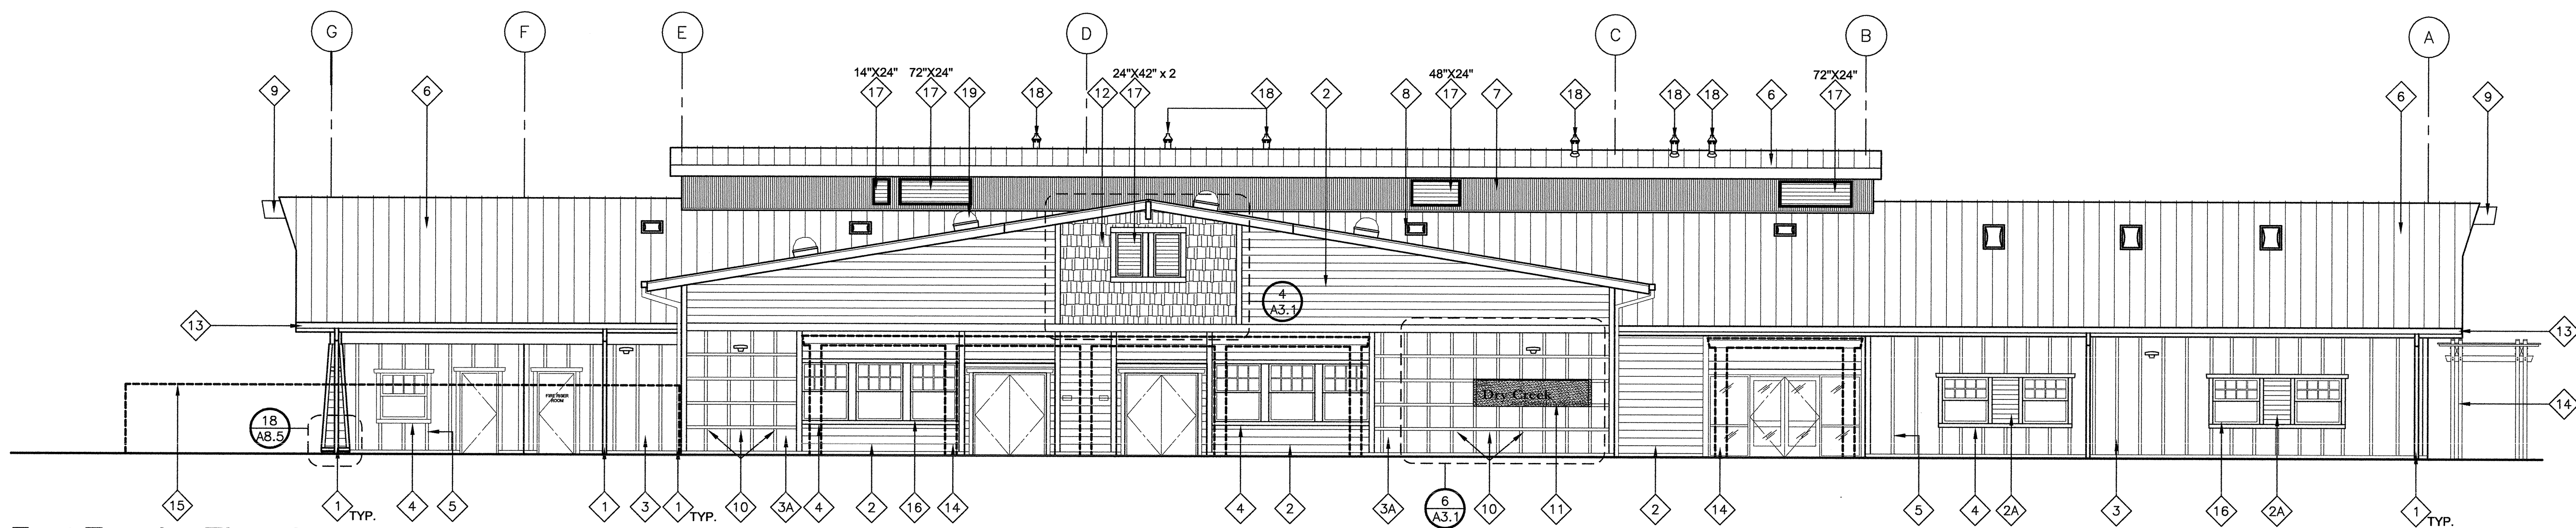

3 East Exterior Elevation
SCALE: 1/8" = 1'-0"

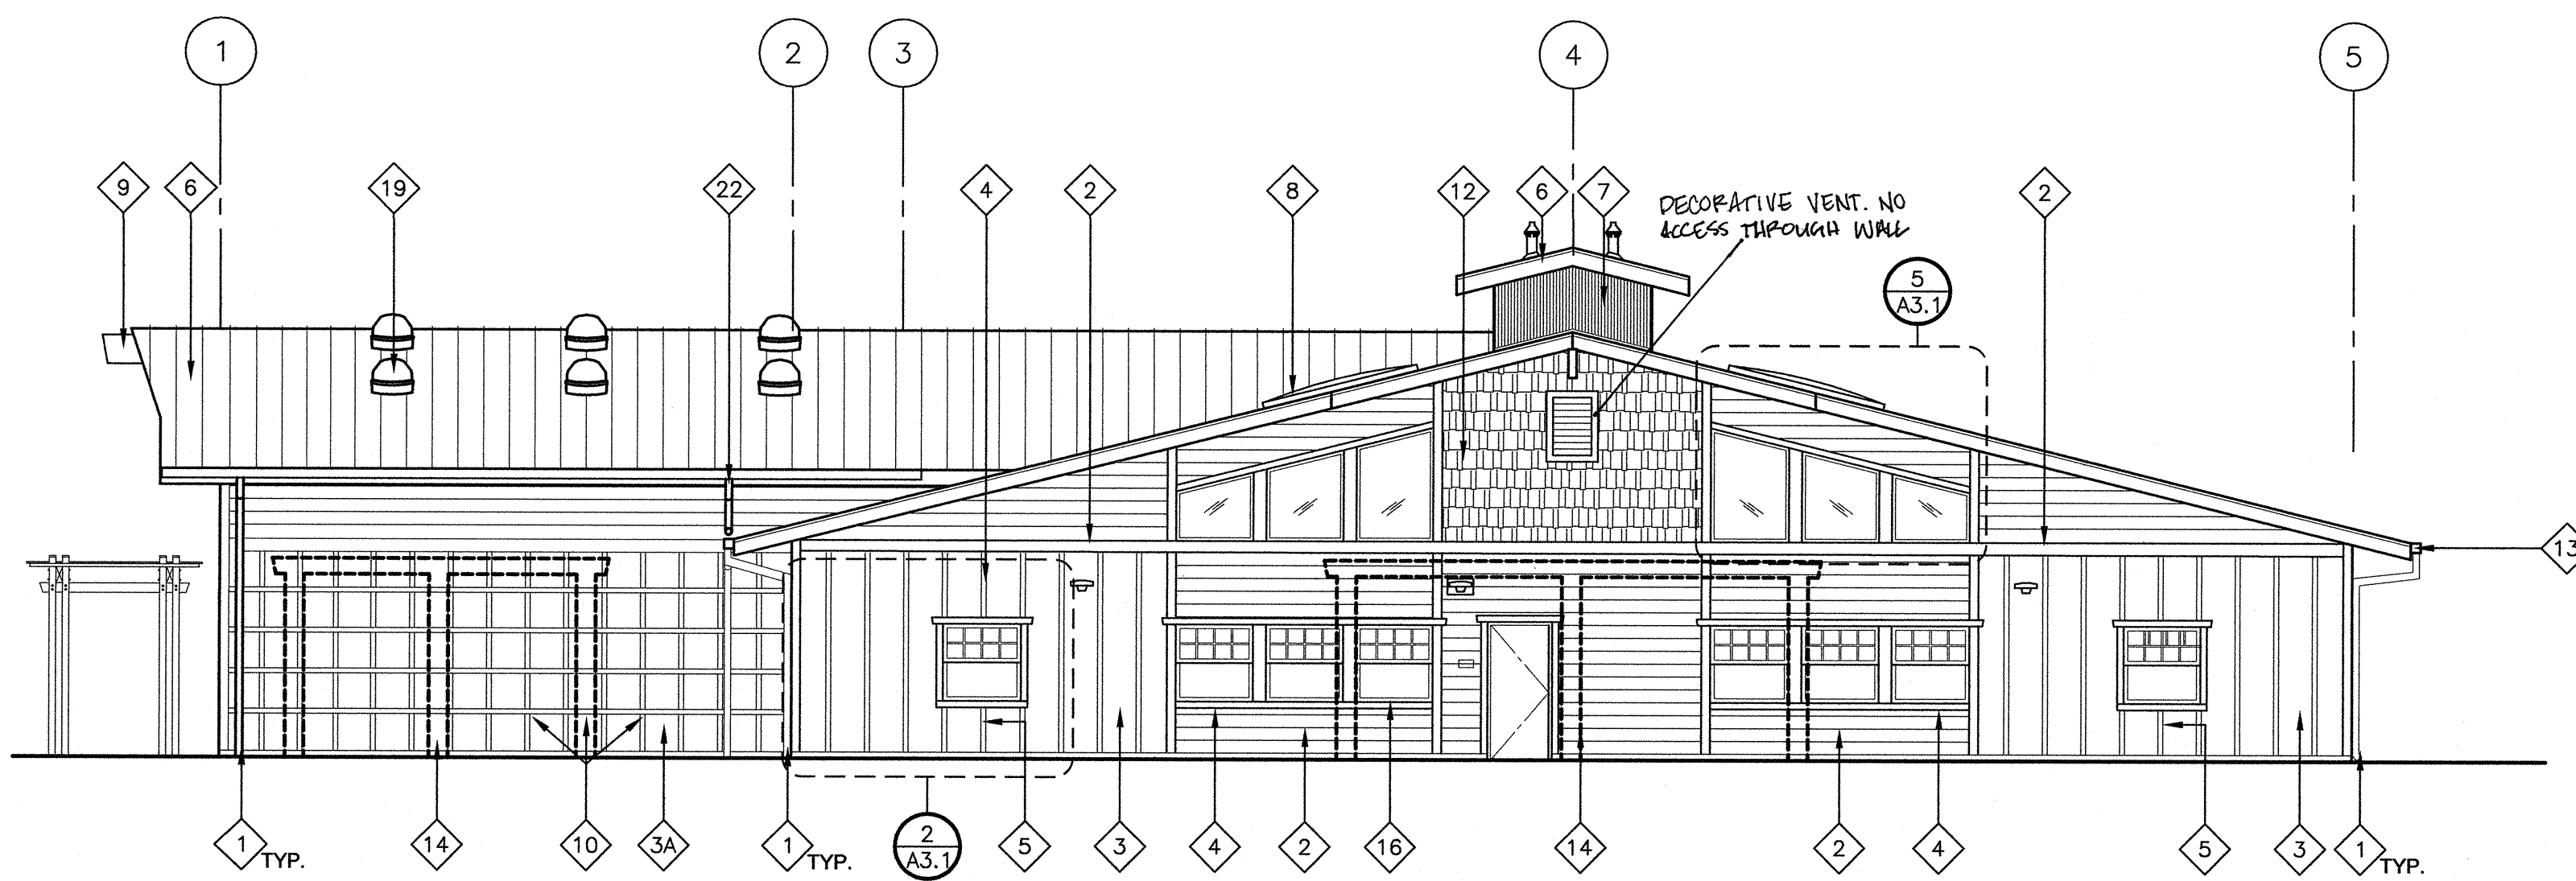

1 North Exterior Elevation
SCALE: 1/8" = 1'-0"

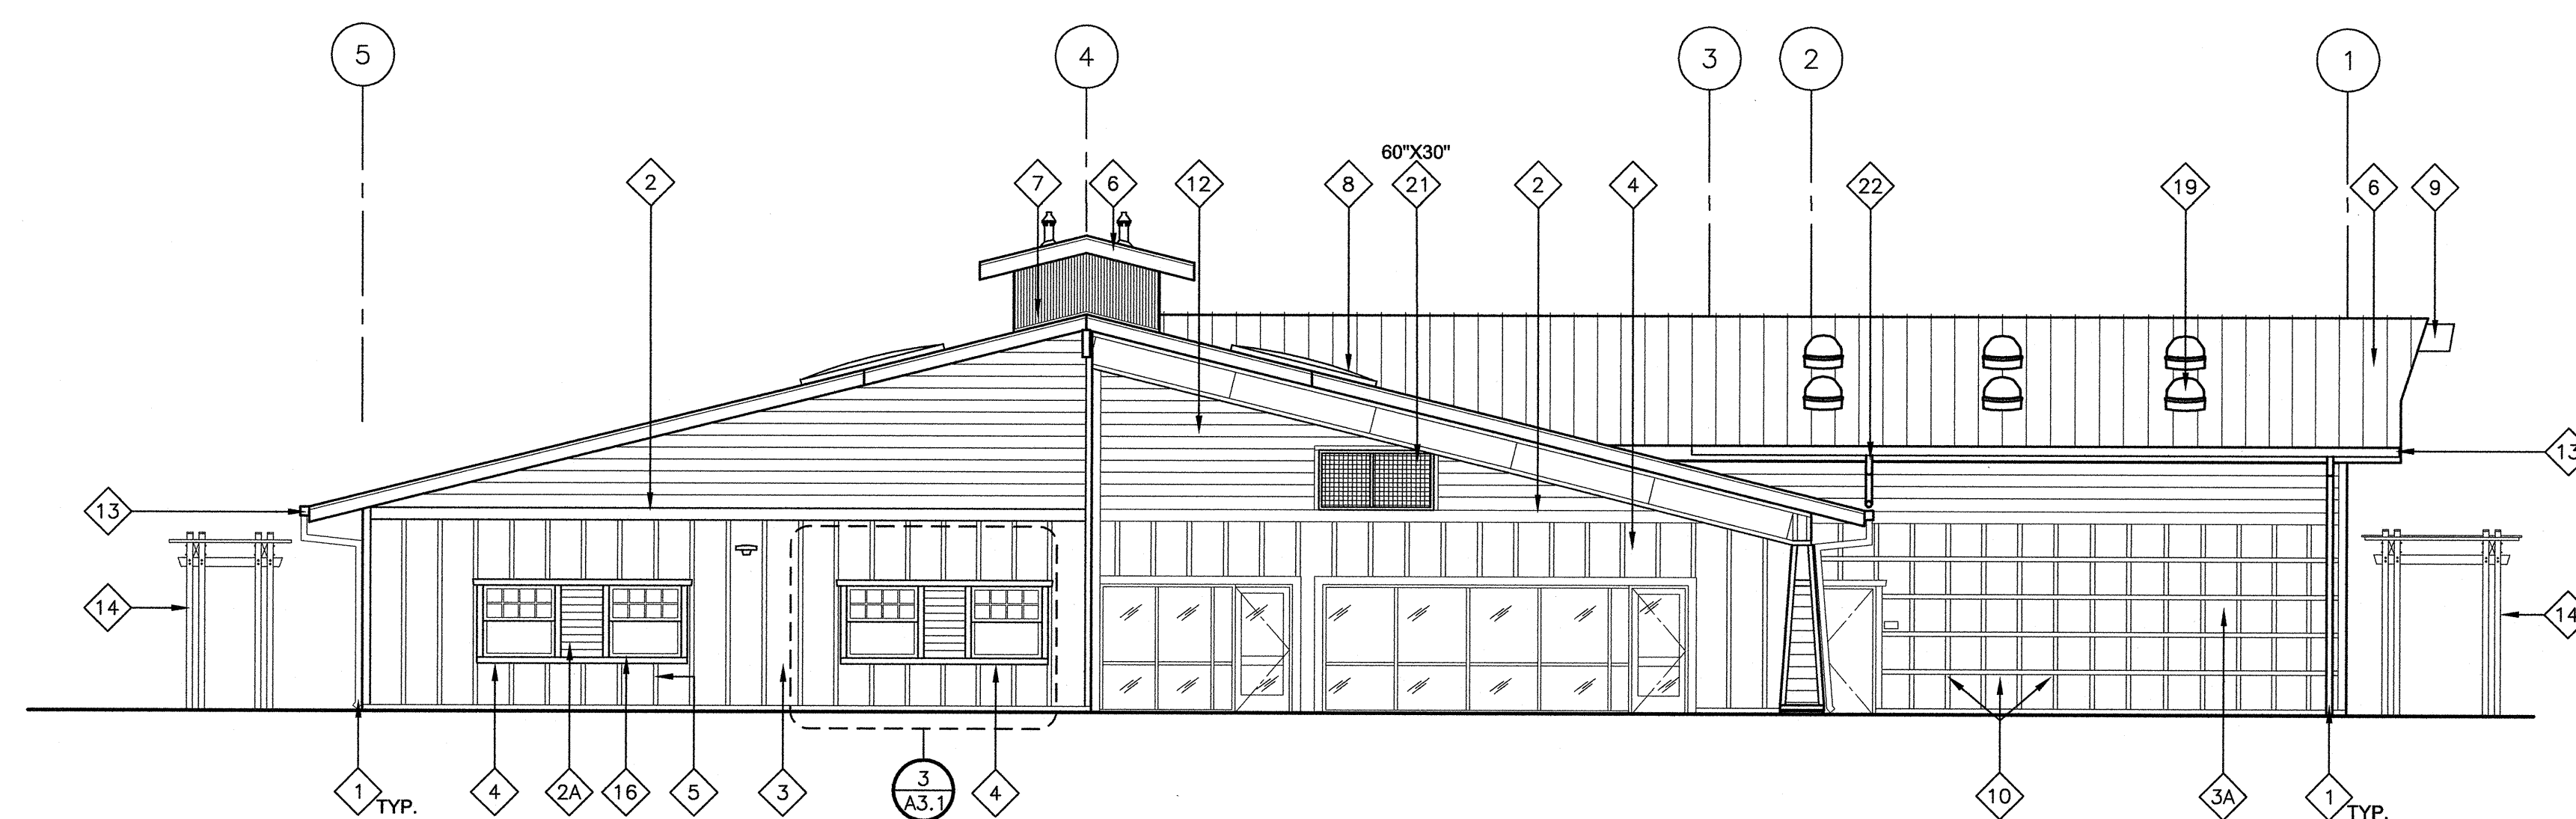


2 South Exterior Elevation
SCALE: 1/8" = 1'-0"

Dry Creek Joint Elementary School District
District Education Center

8849 Cook Riolo Road, Roseville, CA 95747

Dry Creek Joint Elementary School District

FILE NO. 31-15

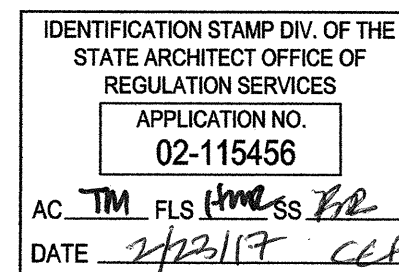


DIVISION OF THE STATE ARCHITECT

revision date: by:

CONSULTANT

nacht&lewis

600 Q Street, Suite 100
Sacramento, CA 95811
www.nachtandlewis.com
916.329.4000

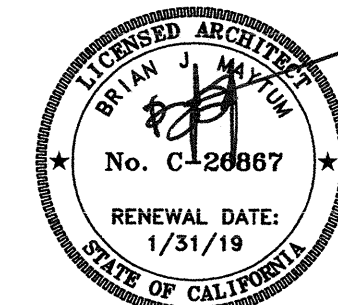

ARCHITECT

INITIAL BOX

NO.	DWG BY	DATE	REVIEWED

REVISIONS

NO.	DESCRIPTION	DATE	REV

DATE February 23, 2017

JOB NO. Y1538.00

SHEET TITLE

Exterior
Elevations

SHEET NO.

A3.0

SHEET ____ OF ____ TOTAL

ONE INCH = TWENTY FEET
ONE-SIXTEENTH INCH = ONE FOOT
ONE-EIGHTH INCH = ONE FOOT
ONE-FOURTH INCH = ONE FOOT
ONE-HALF INCH = ONE FOOT
THREE-QUARTERS INCH = ONE FOOT
ONE INCH = ONE FOOT
ONE AND ONE-HALF INCH = ONE FOOT

KEYNOTES:

THESE KEYNOTES APPLY TO THIS SHEET ONLY.

- 1

MECHANICAL VENT LOUVER.
- 2

CEMENTITIOUS CEDARMILL 9-1/4" LAP SIDING.
- 2A

CEMENTITIOUS SMOOTH 6-1/4" LAP SIDING.
- 3

CEMENTITIOUS CEDARMILL VERTICAL SIDING PANEL.
- 3A

CEMENTITIOUS SMOOTH VERTICAL SIDING PANEL.
- 4

7.5" CEMENTITIOUS TRIM BOARD
- 5

CEMENTITIOUS BATTEN BOARDS @ 24" O.C.± AS SHOWN FOR BEST SYMMETRY.
- 6

STANDING SEAM METAL ROOFING
- 7

CORRUGATED METAL WALL PANEL
- 8

SKYLIGHT
- 9

GLULAM BEAM WITH METAL WEATHER CAP
- 10

HORIZONTAL AND VERTICAL CEMENTITIOUS BATTEN BOARDS @ 24" O.C.± AS SHOWN FOR BEST SYMMETRY.
- 11

3.5" CEMENTITIOUS TRIM BOARD
- 12

CEMENTITIOUS SHINGLE SIDING
- 13

EXTERIOR COMPOSITE ALUMINUM GRAPHIC SIGNAGE PANEL - SIGN TYPE S-11 - SEE SPEC SECTION 10 14 00 AND DETAIL 30/A8.3 FOR MOUNTING.
- 14

5.5" CEMENTITIOUS TRIM BOARD
- 15

NOT USED
- 16

VINYL WINDOW.
- 17


CONCRETE CURB.
- 18

4" CEMENTITIOUS LAP SIDING.
- 19

EXTERIOR WALL MOUNTED ACCESSORY WHERE OCCURS - SEE DETAIL 8/A8.5 FOR FLUSH BACKING DETAIL WHERE OCCURS AT SHIP LAP SIDING.


GENERAL SHEET NOTES:

1. ALL METAL WALL AND ROOF PANELS SHALL BE FACTORY FINISHED.
2. ALL CEMENTITIOUS PANELING AND TRIM SHALL BE PAINTED. PROVIDE FOR UP TO THREE WALL COLORS AND TWO TRIM COLORS. ARCHITECT TO PROVIDE COLOR CODED ELEVATIONS AT TIME OF SUBMITTAL.
3. ALL HORIZONTAL TRIM BOARDS SHALL HAVE G.S.M. FLASHING.

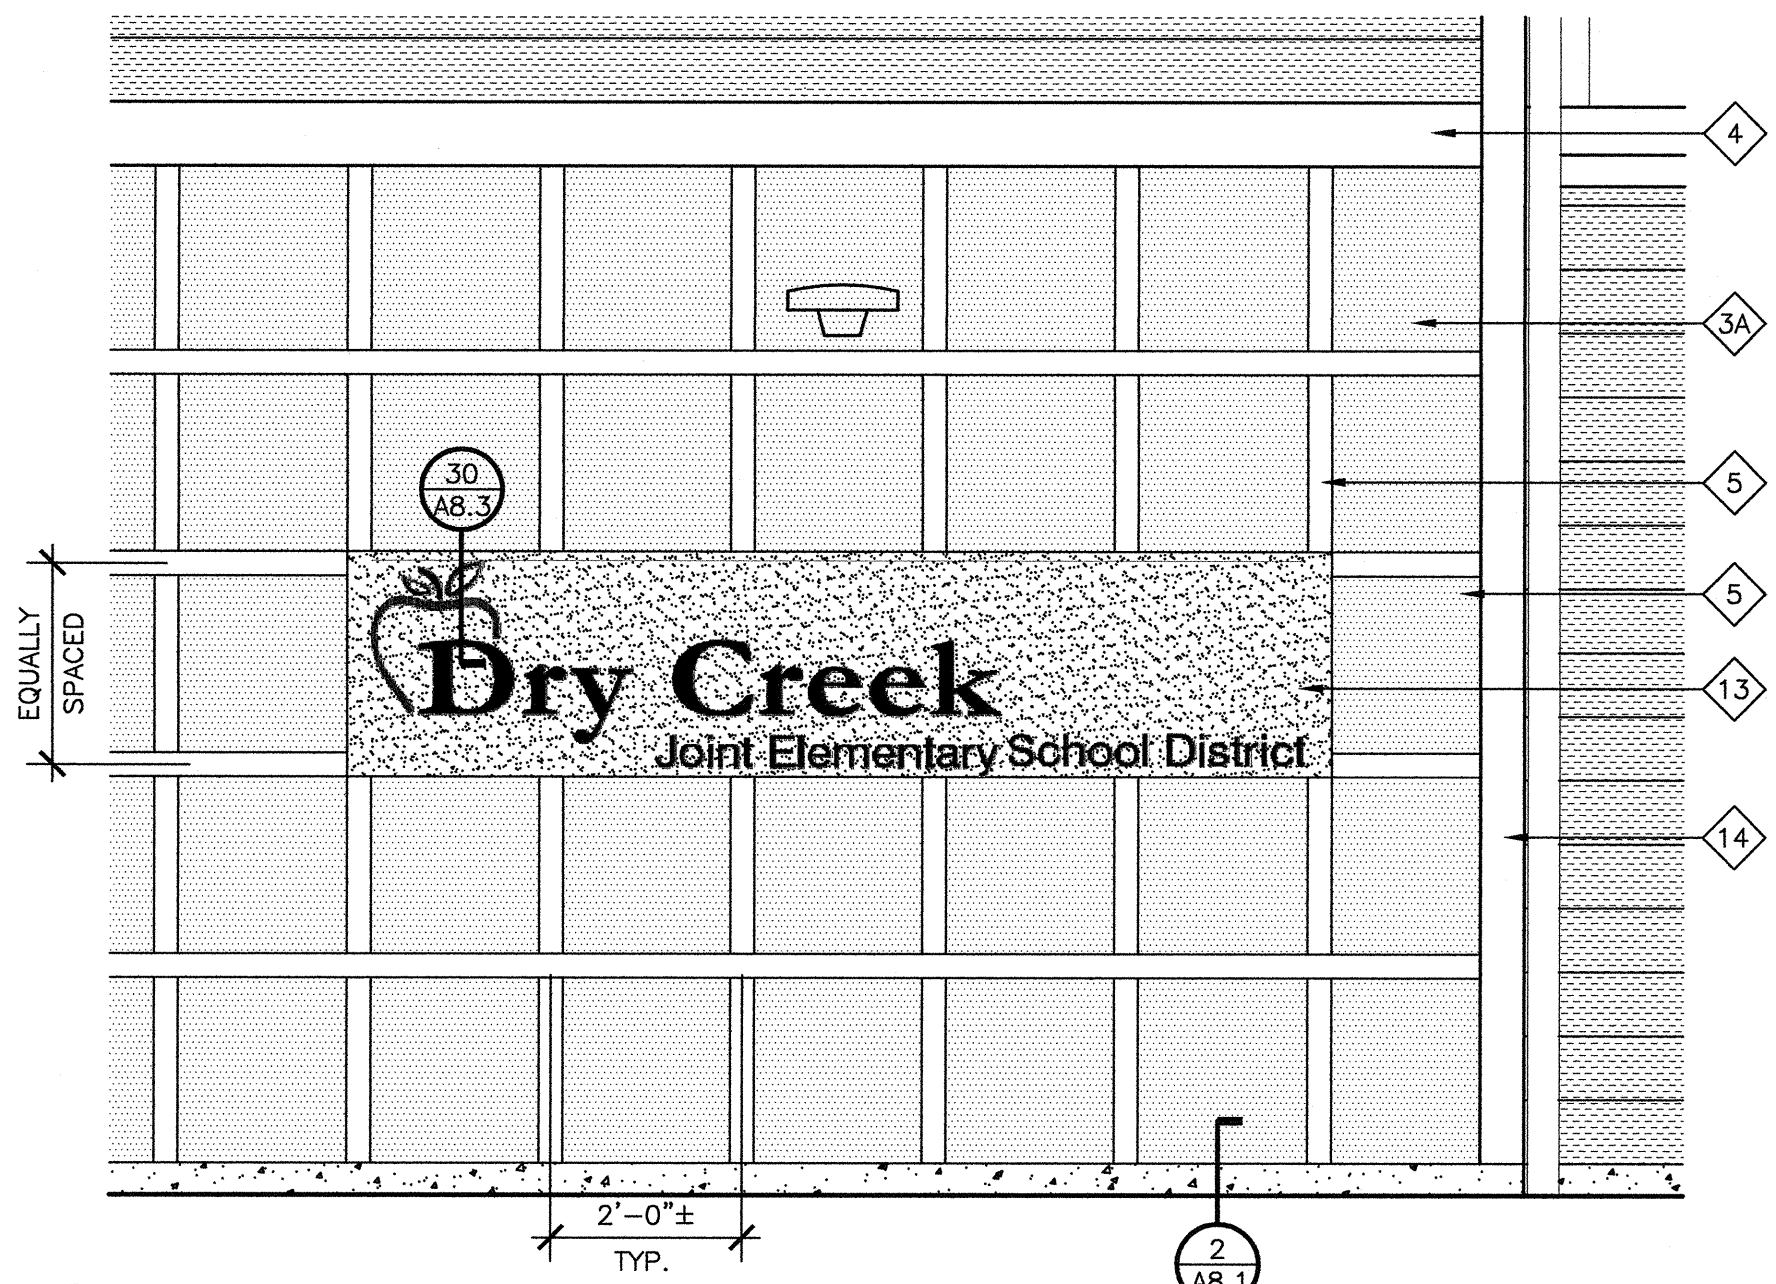


6 Partial Enlarged Elevation

SCALE: 1/2" = 1'-0"

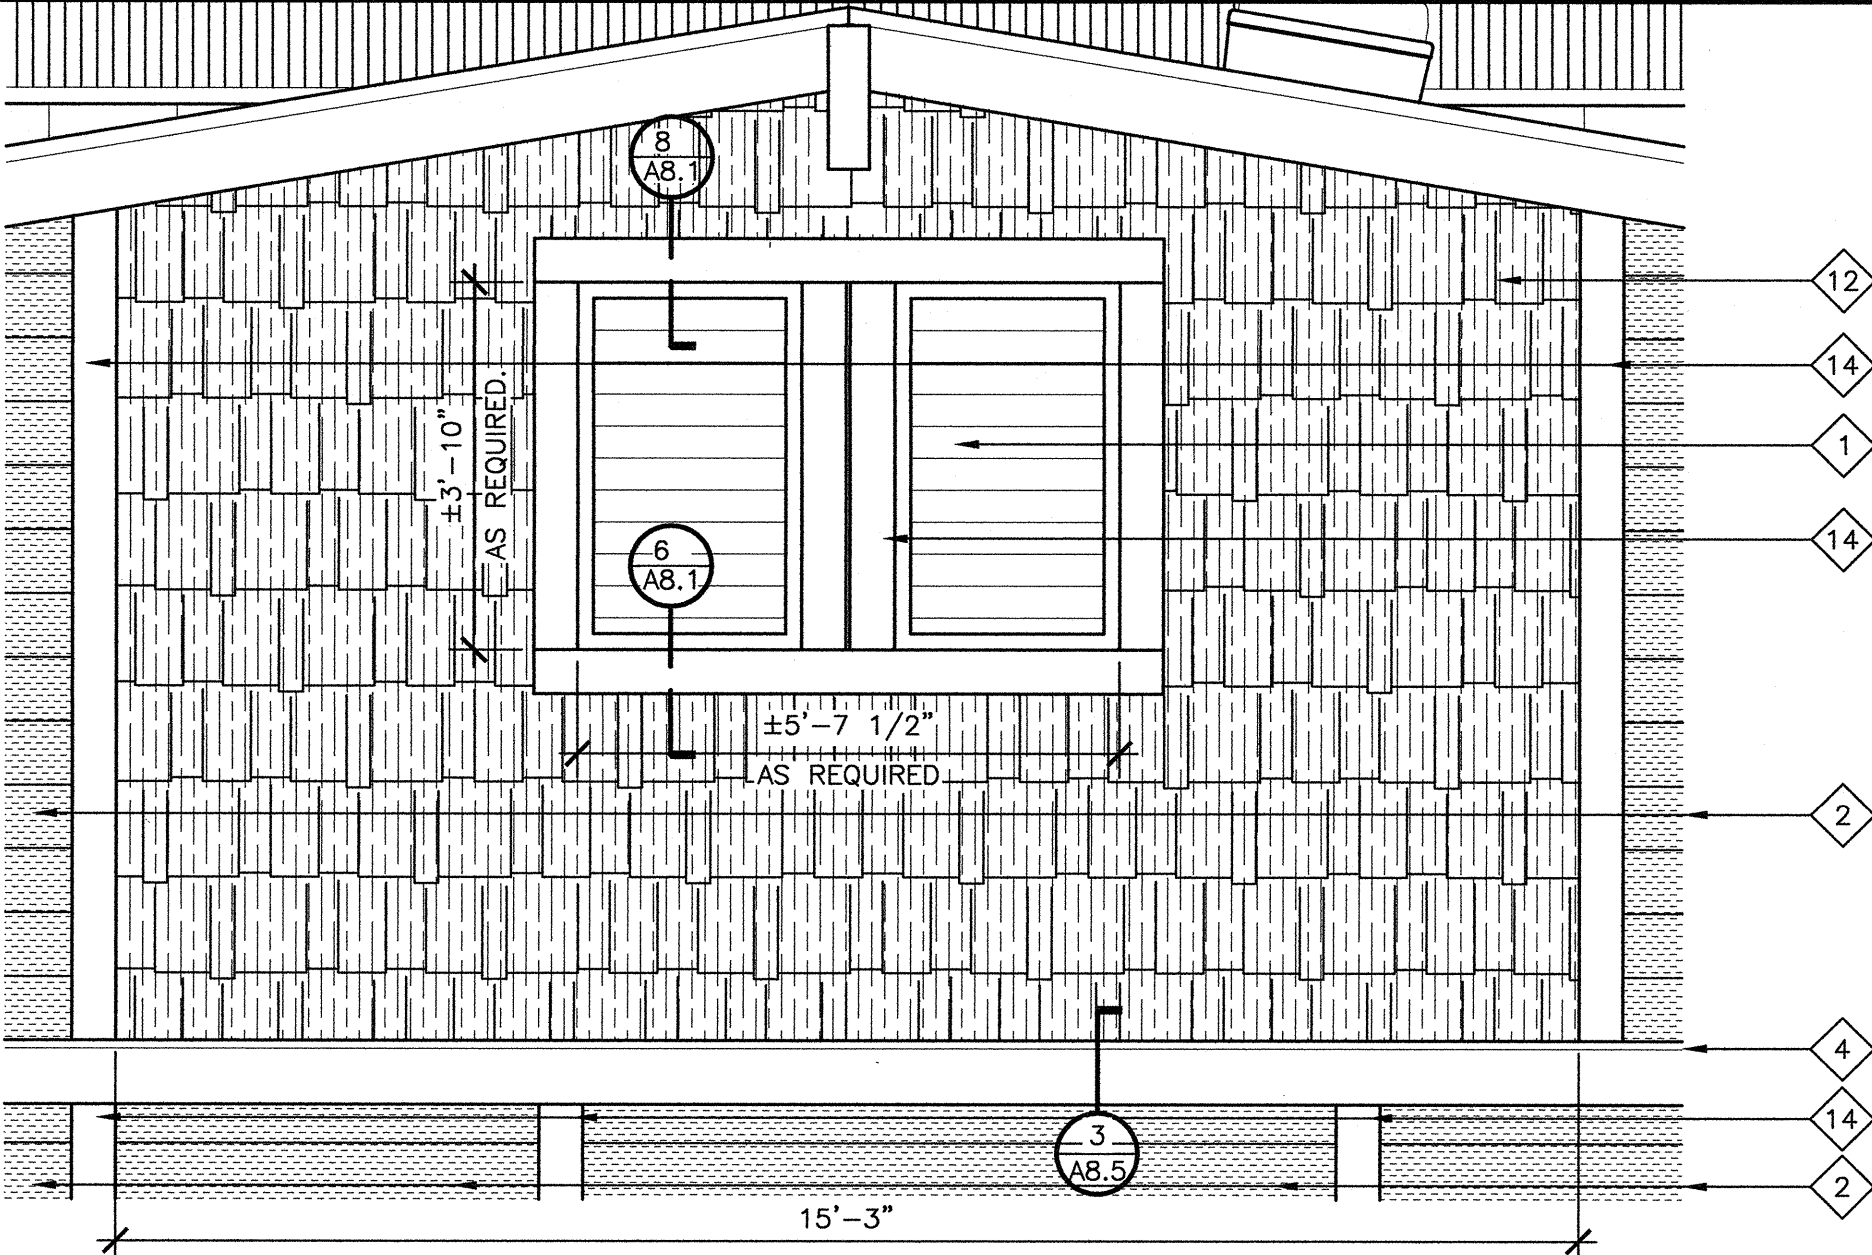


4 Partial Enlarged Elevation

SCALE: 1/2" = 1'-0"

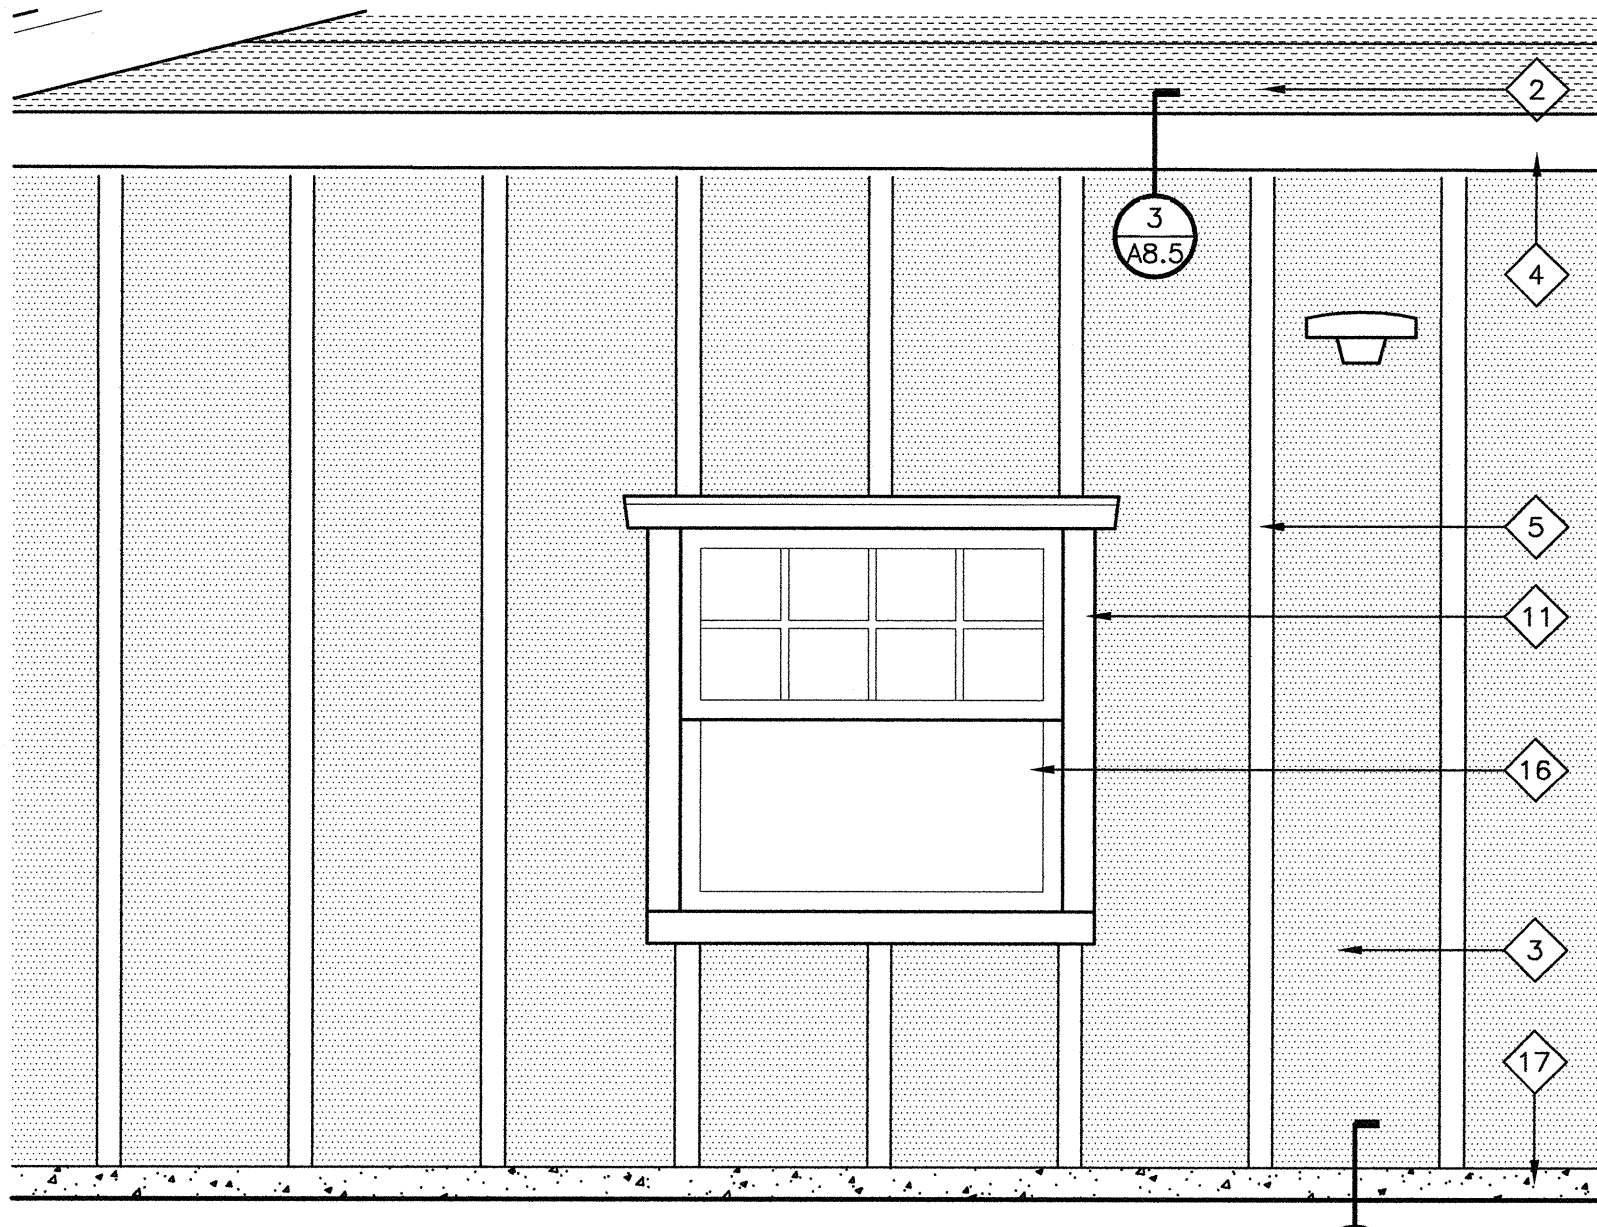


2 Partial Enlarged Elevation

SCALE: 1/2" = 1'-0"

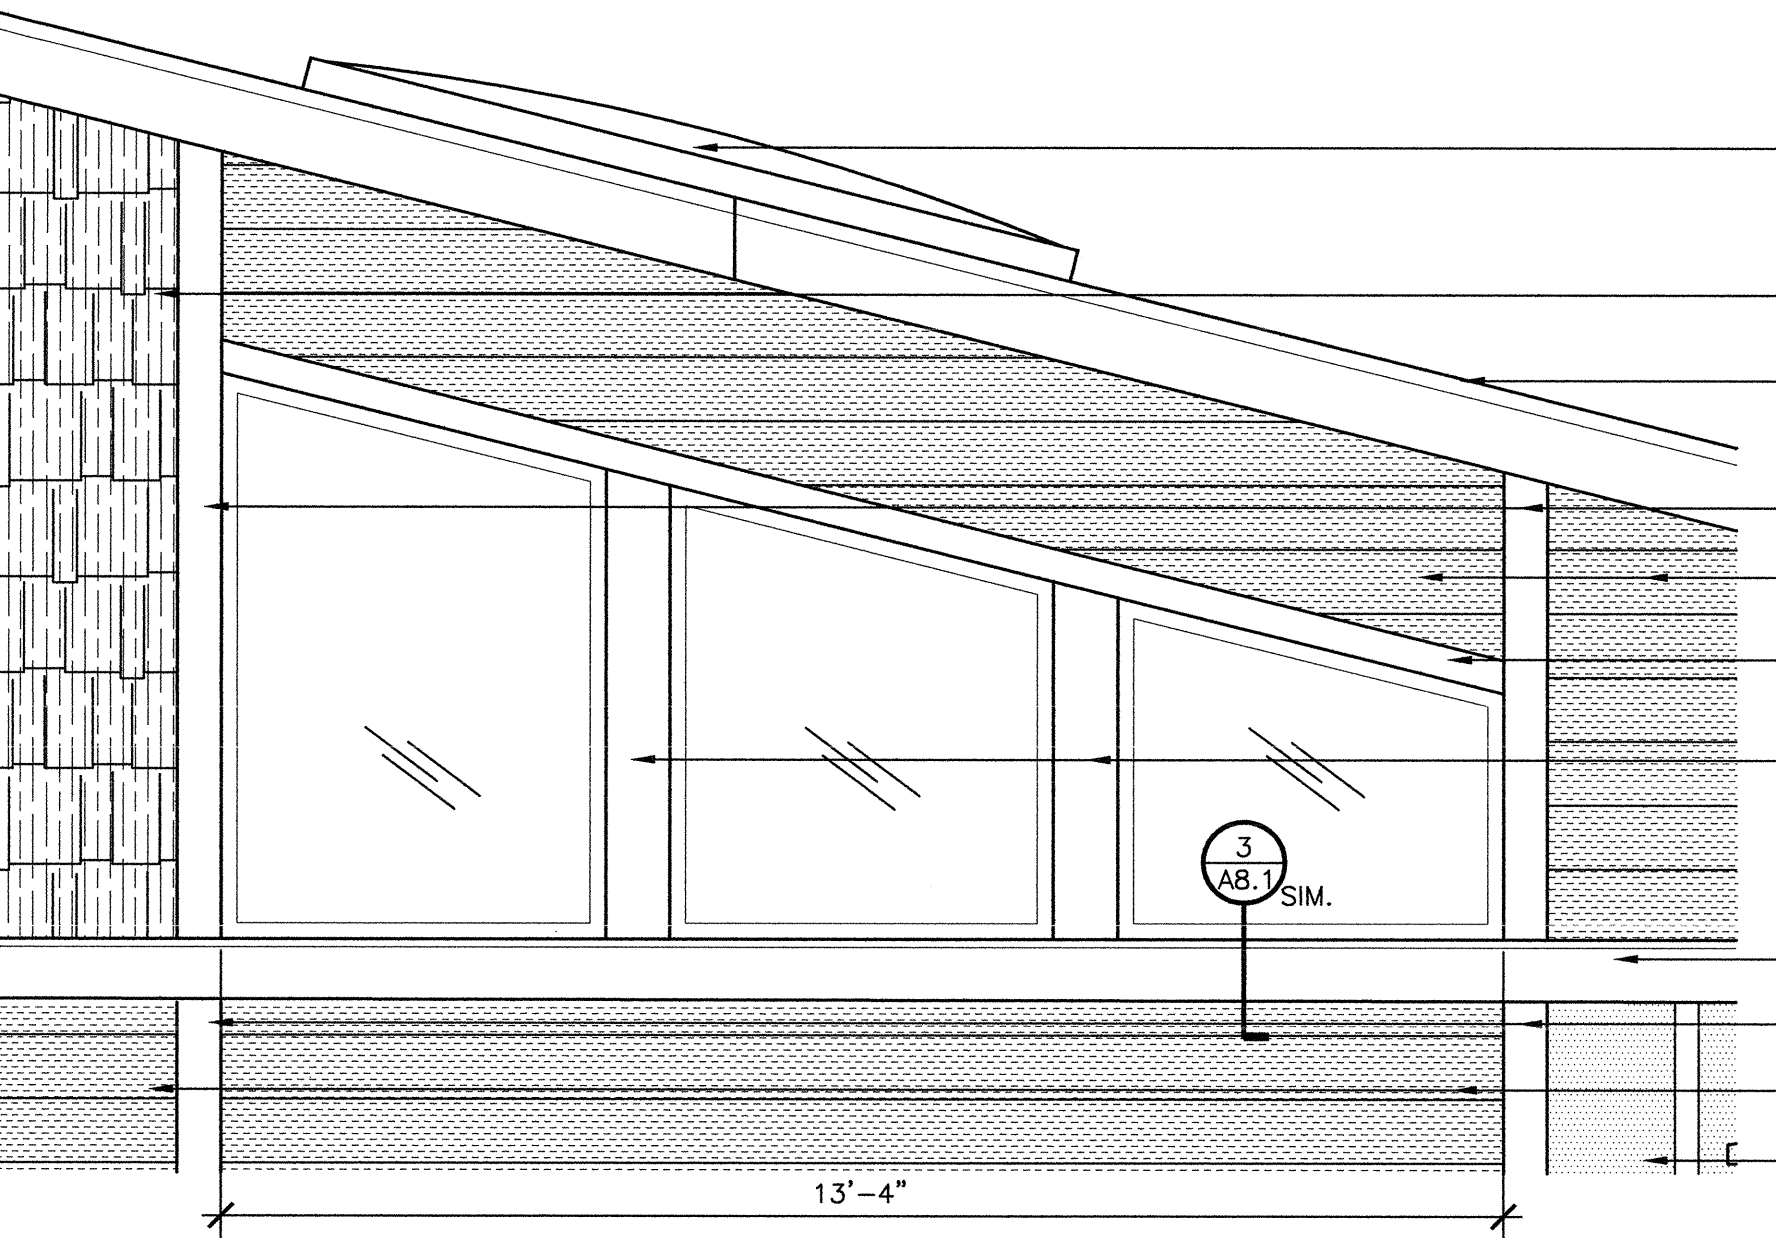


5 Partial Enlarged Elevation

SCALE: 1/2" = 1'-0"

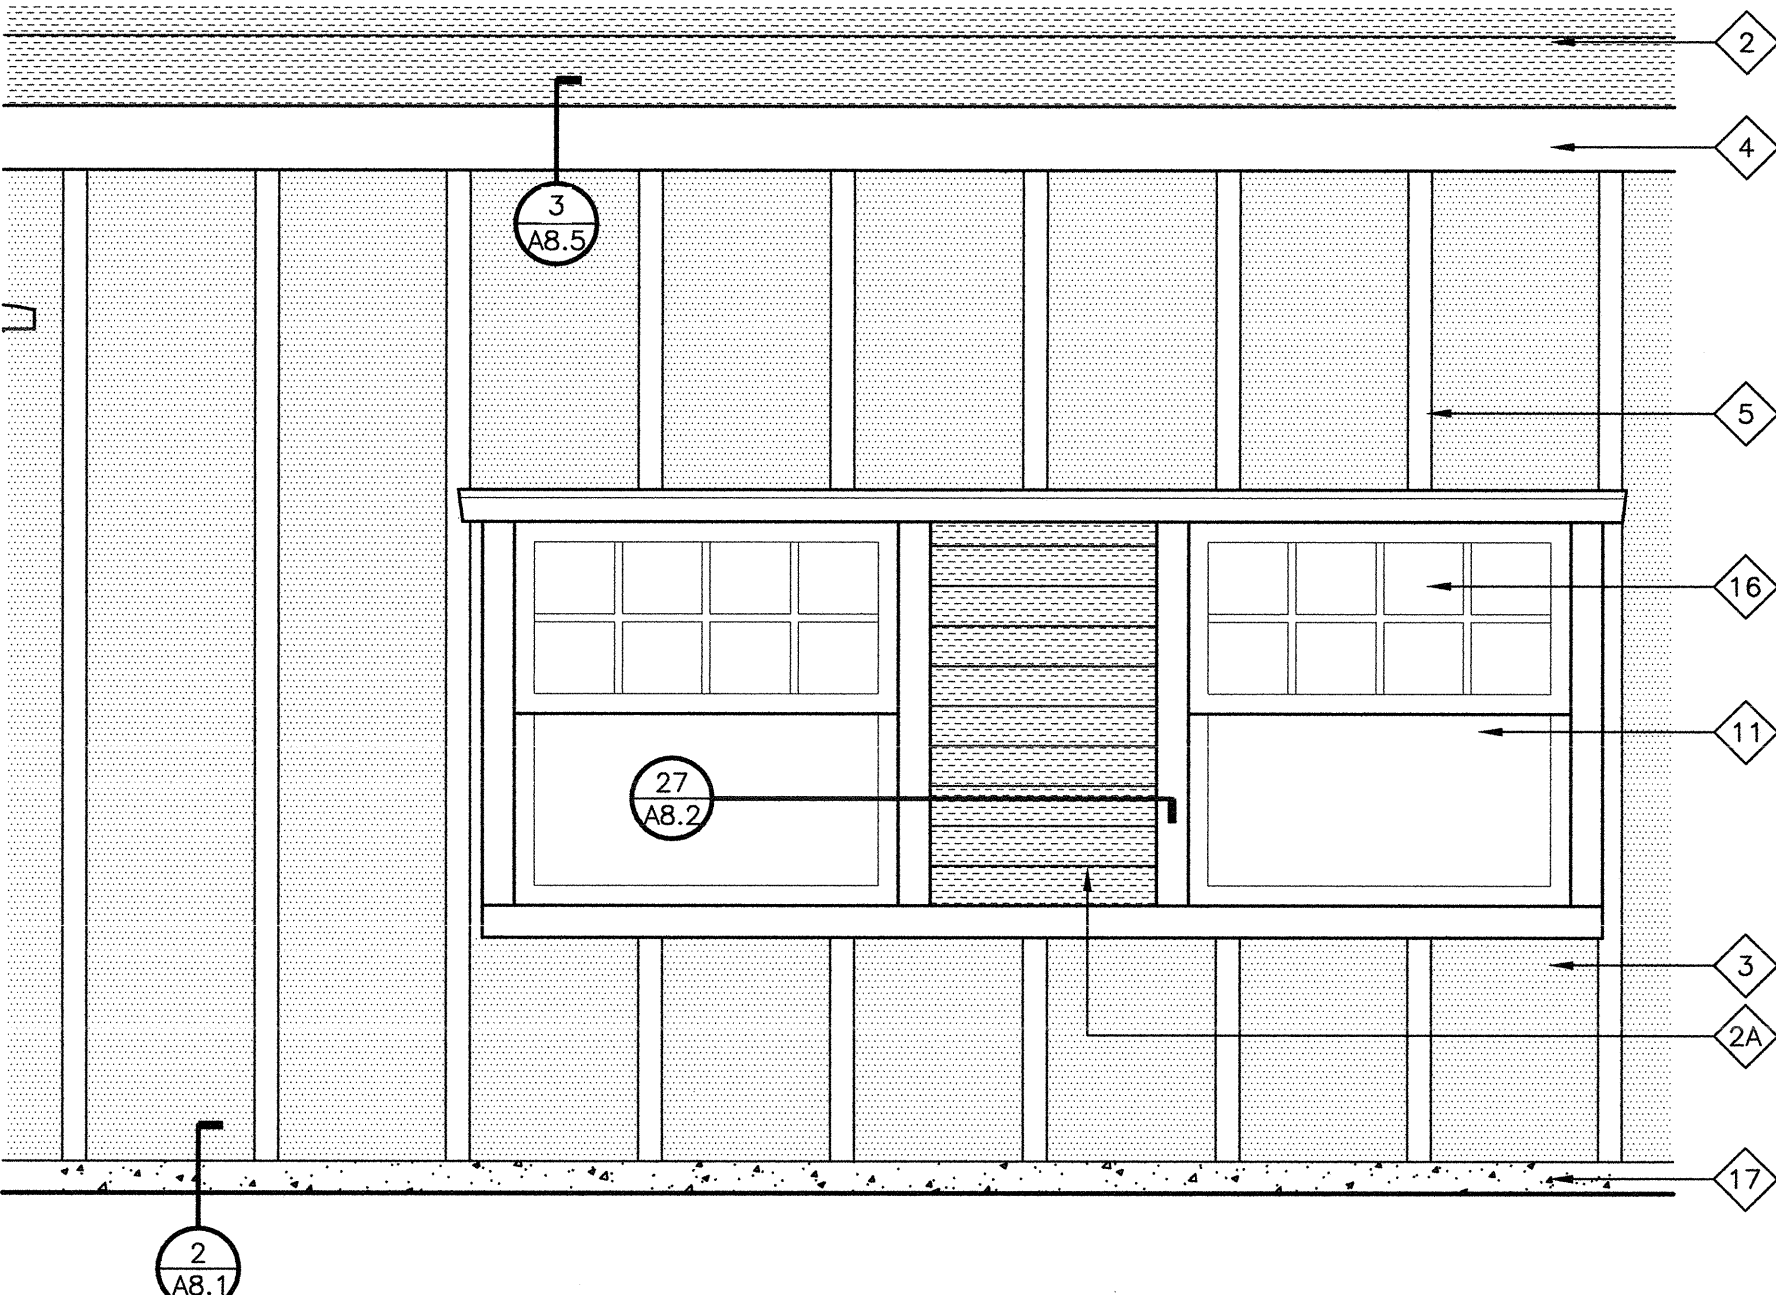

3 Partial Enlarged Elevation

SCALE: 1/2" = 1'-0"

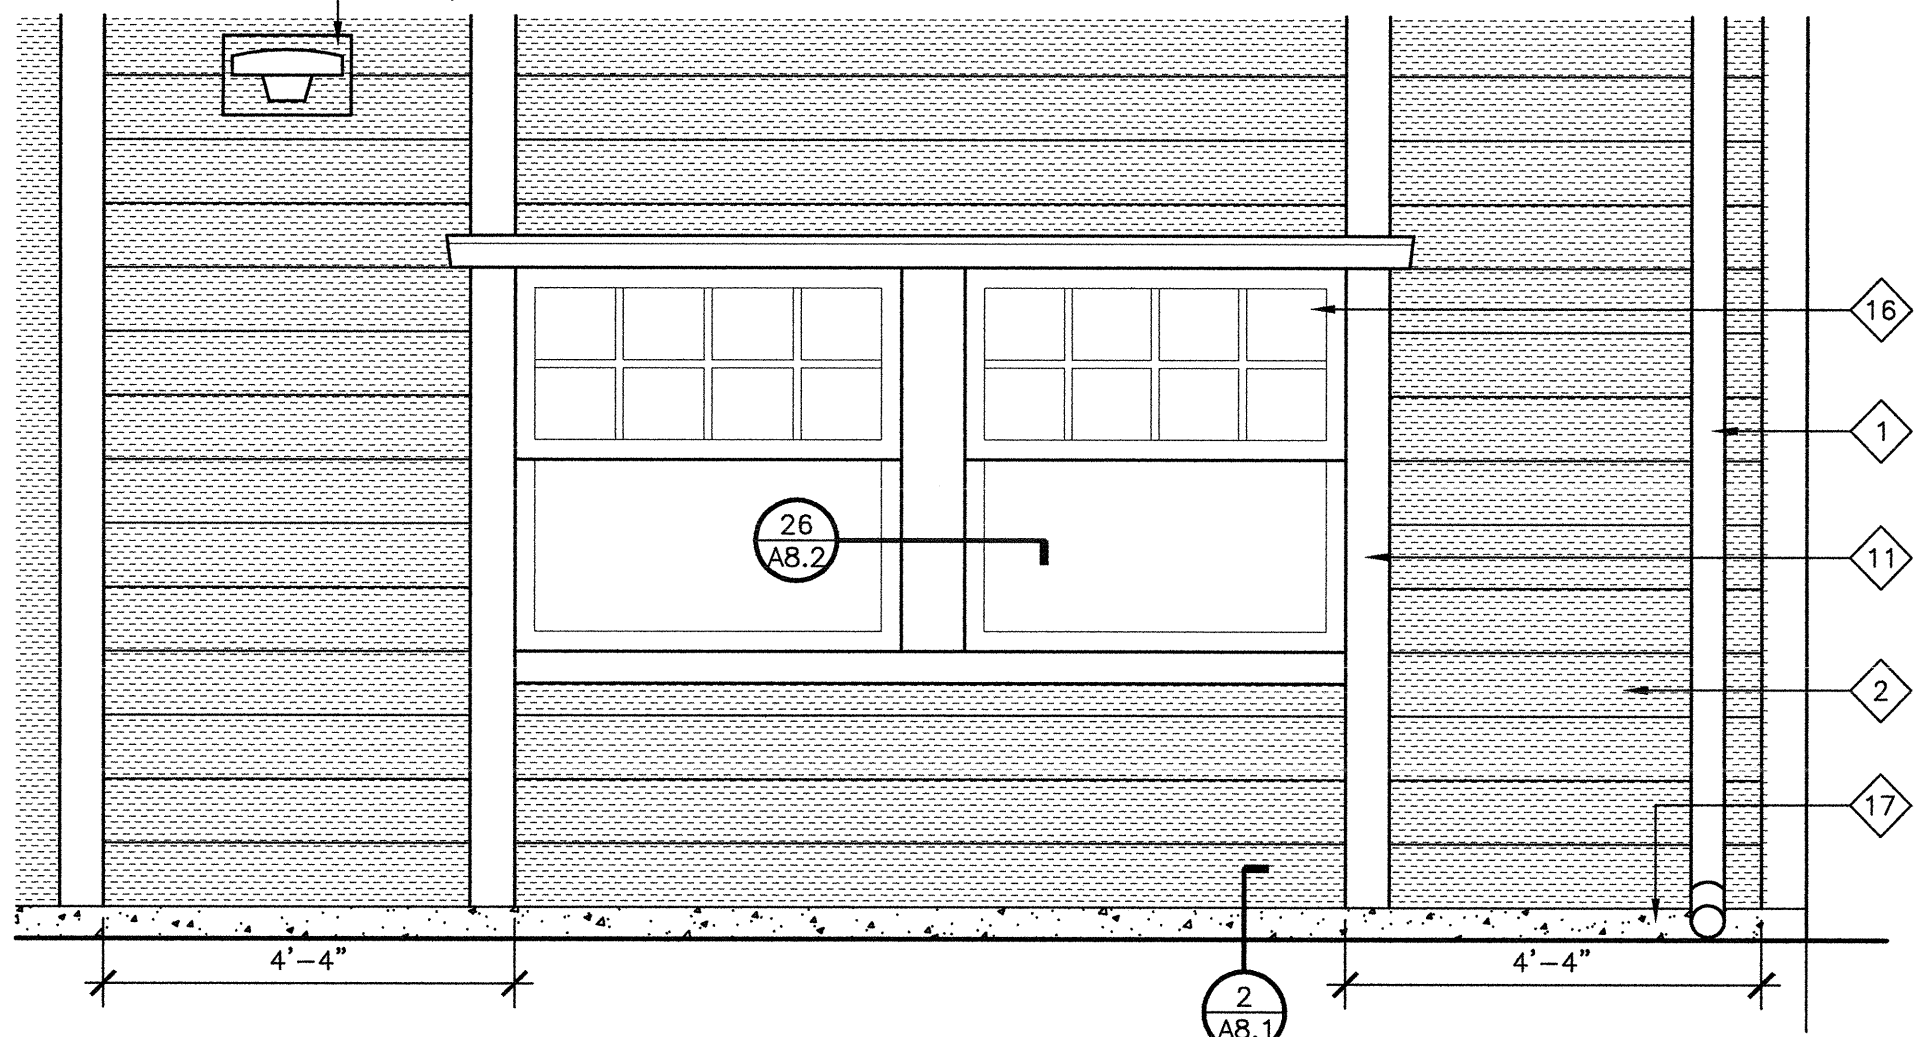

1 Partial Enlarged Elevation

SCALE: 1/2" = 1'-0"

Dry Creek Joint Elementary School District
District Education Center

8849 Cook Riolo Road, Roseville, CA 95747

Dry Creek Joint Elementary School District


FILE NO. 31-15
IDENTIFICATION STAMP DIV. OF THE
STATE ARCHITECT OFFICE OF
REGULATION SERVICES
APPLICATION NO. 02-115456
AC. TM FLS HMC AS. 62
DATE 2/23/17 CC BY

DIVISION OF THE STATE ARCHITECT
revision date: _____ by: _____

CONSULTANT

nacht&lewis

600 O Street, Suite 100
Sacramento, CA 95811
www.nachtandlewis.com
916.329.4000

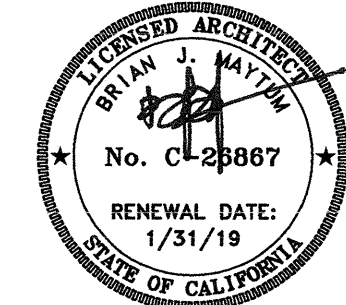

ARCHITECT

INITIAL BOX

NO.	DWG BY	DATE	REVIEWED

REVISIONS

NO.	DESCRIPTION	DATE	REV'D
	100% design development	7/6/16	
	75% construction documents	9/20/16	
	DSA submittal	12/31/16	
	DSA approval	02/23/17	

DATE February 23, 2017

JOB NO. Y1538.00

SHEET TITLE

Enlarged Exterior
Elevations

SHEET NO.

A3.1

SHEET ____ OF ____ TOTAL

Dry Creek Joint Elementary School District

revision date: _____ by: _____

SHEET ____ OF ____ TOTAL

1. ALL INTERIOR WALLS ARE COVERED WITH GYPSUM WALL BOARD AND SEPARATE WALL FINISH - SEE FINISH SCHEDULE ON SHEET A7.1.
2. SEE SHEET A7.1 FOR FLOOR FINISHES AND SHEET A7.1.1 FOR FLOORING PATTERNS.
3. SEE SHEET A7.2 FOR CASEWORK AND EQUIPMENT.
4. SEE SHEET A6.1 FOR DOOR AND WINDOW SCHEDULES.
5. SEE FLOOR PLAN SHEET A10 FOR WALL AND PARTITION FRAMING. ALL INTERIOR AND EXTERIOR WALLS SHALL BE INSULATED.
6. FOR ALL NON-BEARING INTERIOR WALLS, PROVIDE TOP OF WALL CONNECTION AND DIAGONAL BRACING PER DETAIL 3/54.5.



ONE INCH = TWENTY FEET
ONE-SIXTEENTH INCH = ONE FOOT
ONE-EIGHTH INCH = ONE FOOT
ONE-FOURTH INCH = ONE FOOT
ONE-HALF INCH = ONE FOOT
THREE-QUARTERS INCH = ONE FOOT
ONE INCH = ONE FOOT
ONE AND ONE-HALF INCH = ONE FOOT


KEYNOTES:

THESE KEYNOTES APPLY TO THIS SHEET ONLY.


- 1 ALL CEILINGS PER CEILING PLAN, SHEET A2.1 - SEE CEILING PLAN FOR HEIGHTS NOT NOTED.
- 1A SUSPENDED T-BAR CEILING.
- 1B GYPSUM WALL BOARD CEILING PER PLAN, ON 2x10 JOISTS @ 16" O.C. MAX.
- 2 BATT INSULATION.
- 3 WALL-MOUNTED T.V. - SEE ELECTRICAL DRAWINGS.
- 4 NOT USED
- 5 MECHANICAL UNIT - SEE MECHANICAL DRAWINGS (TYPICAL).
- 6 1/2" PLYWOOD WAINSCOT - 4'-0" HIGH AT MECHANICAL ATTIC, 8'-0" HIGH AT ALL OTHER LOCATIONS UNLESS OTHERWISE NOTED.
- 7 PENDANT LIGHT FIXTURE- SEE ELECTRICAL DRAWINGS.
- 8 CEILING-HUNG ACOUSTIC PANELS - SEE SPEC. SECTION 09 53 00.
- 9 CEILING FAN - SEE MECHANICAL DRAWINGS.

GENERAL SHEET NOTES:


1. ALL INTERIOR WALLS ARE COVERED WITH GYPSUM BOARD AND SEPARATE WALL FINISH - SEE FINISH SCHEDULE ON SHEET A7.1, AND FLOOR PATTERNS ON A7.1.1.
2. SEE SHEET A7.1 FOR FLOOR FINISHES.
3. SEE SHEET A7.2 FOR CASE WORK AND EQUIPMENT.
4. SEE SHEET A6.1 FOR DOOR AND WINDOW SCHEDULES.
5. SEE FLOOR PLAN SHEET A1.0 FOR WALL AND PARTITION FRAMING. ALL INTERIOR AND EXTERIOR WALLS SHALL BE INSULATED.

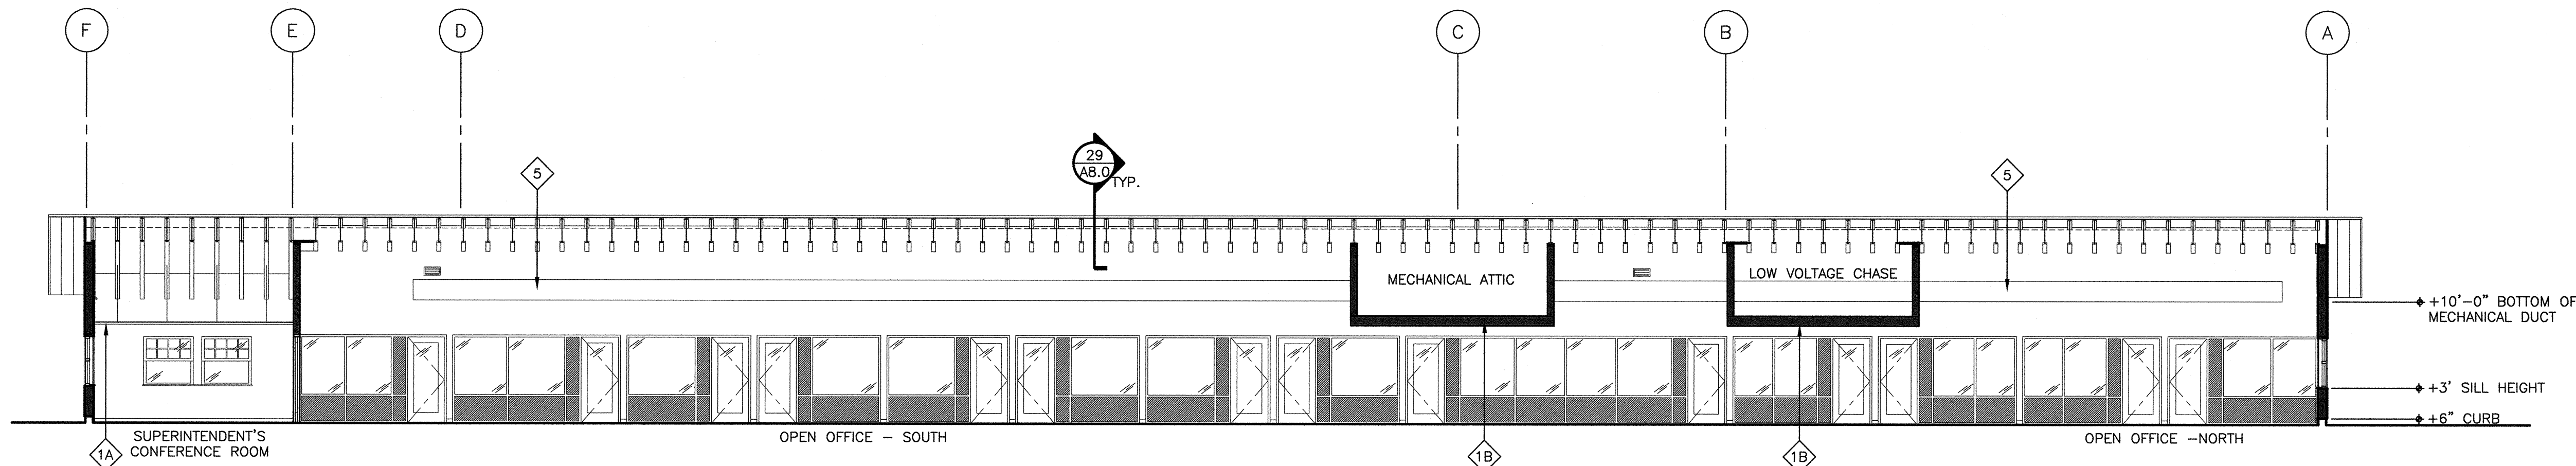

3 Section 3-3
SCALE: 1/8" = 1'-0"

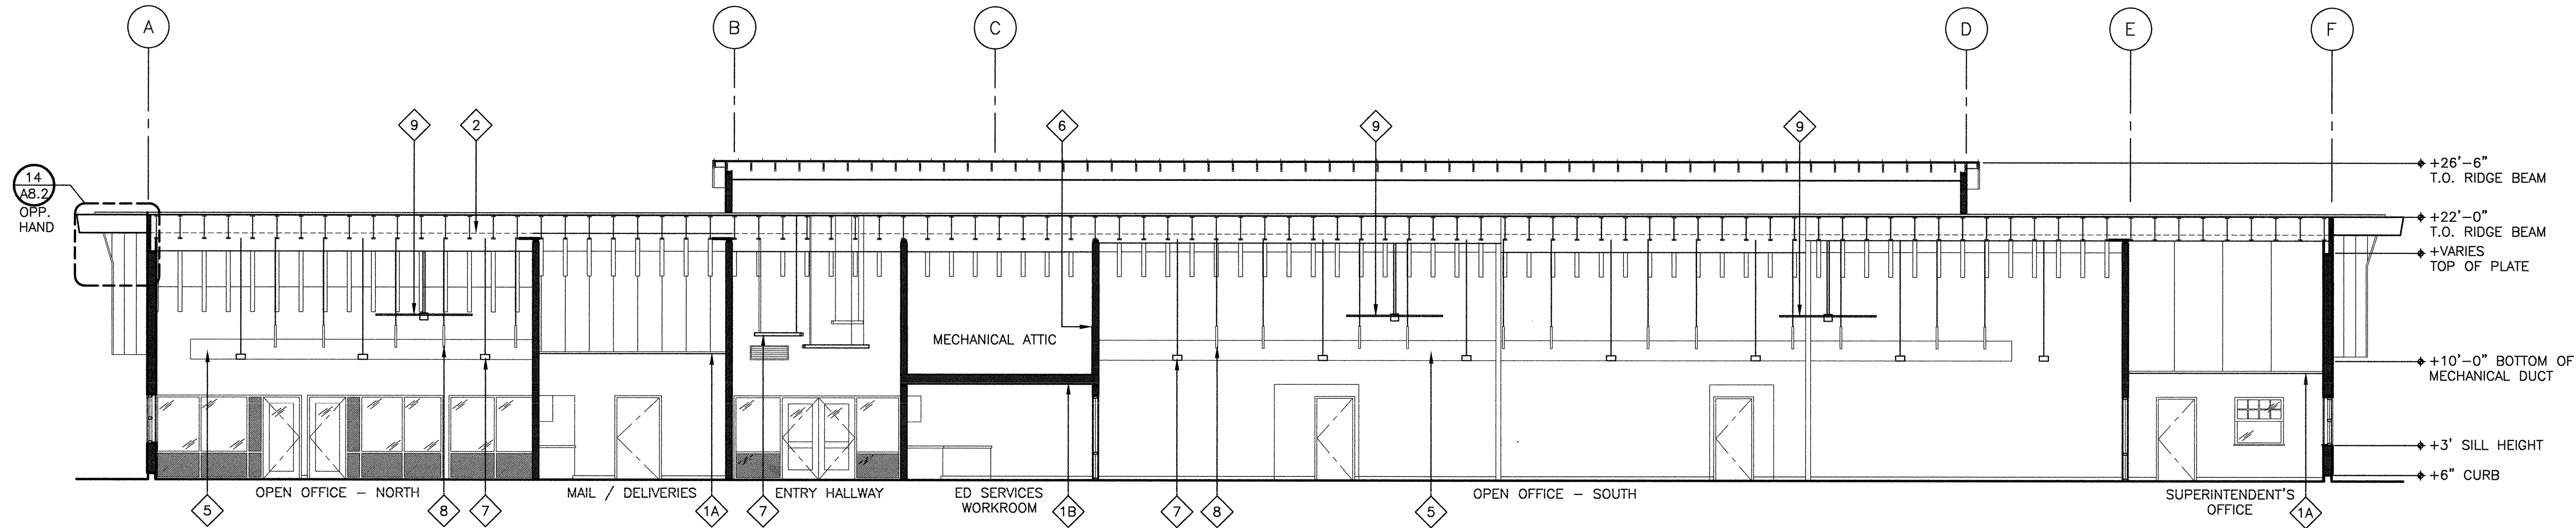

2 Section 2-2
SCALE: 1/8" = 1'-0"

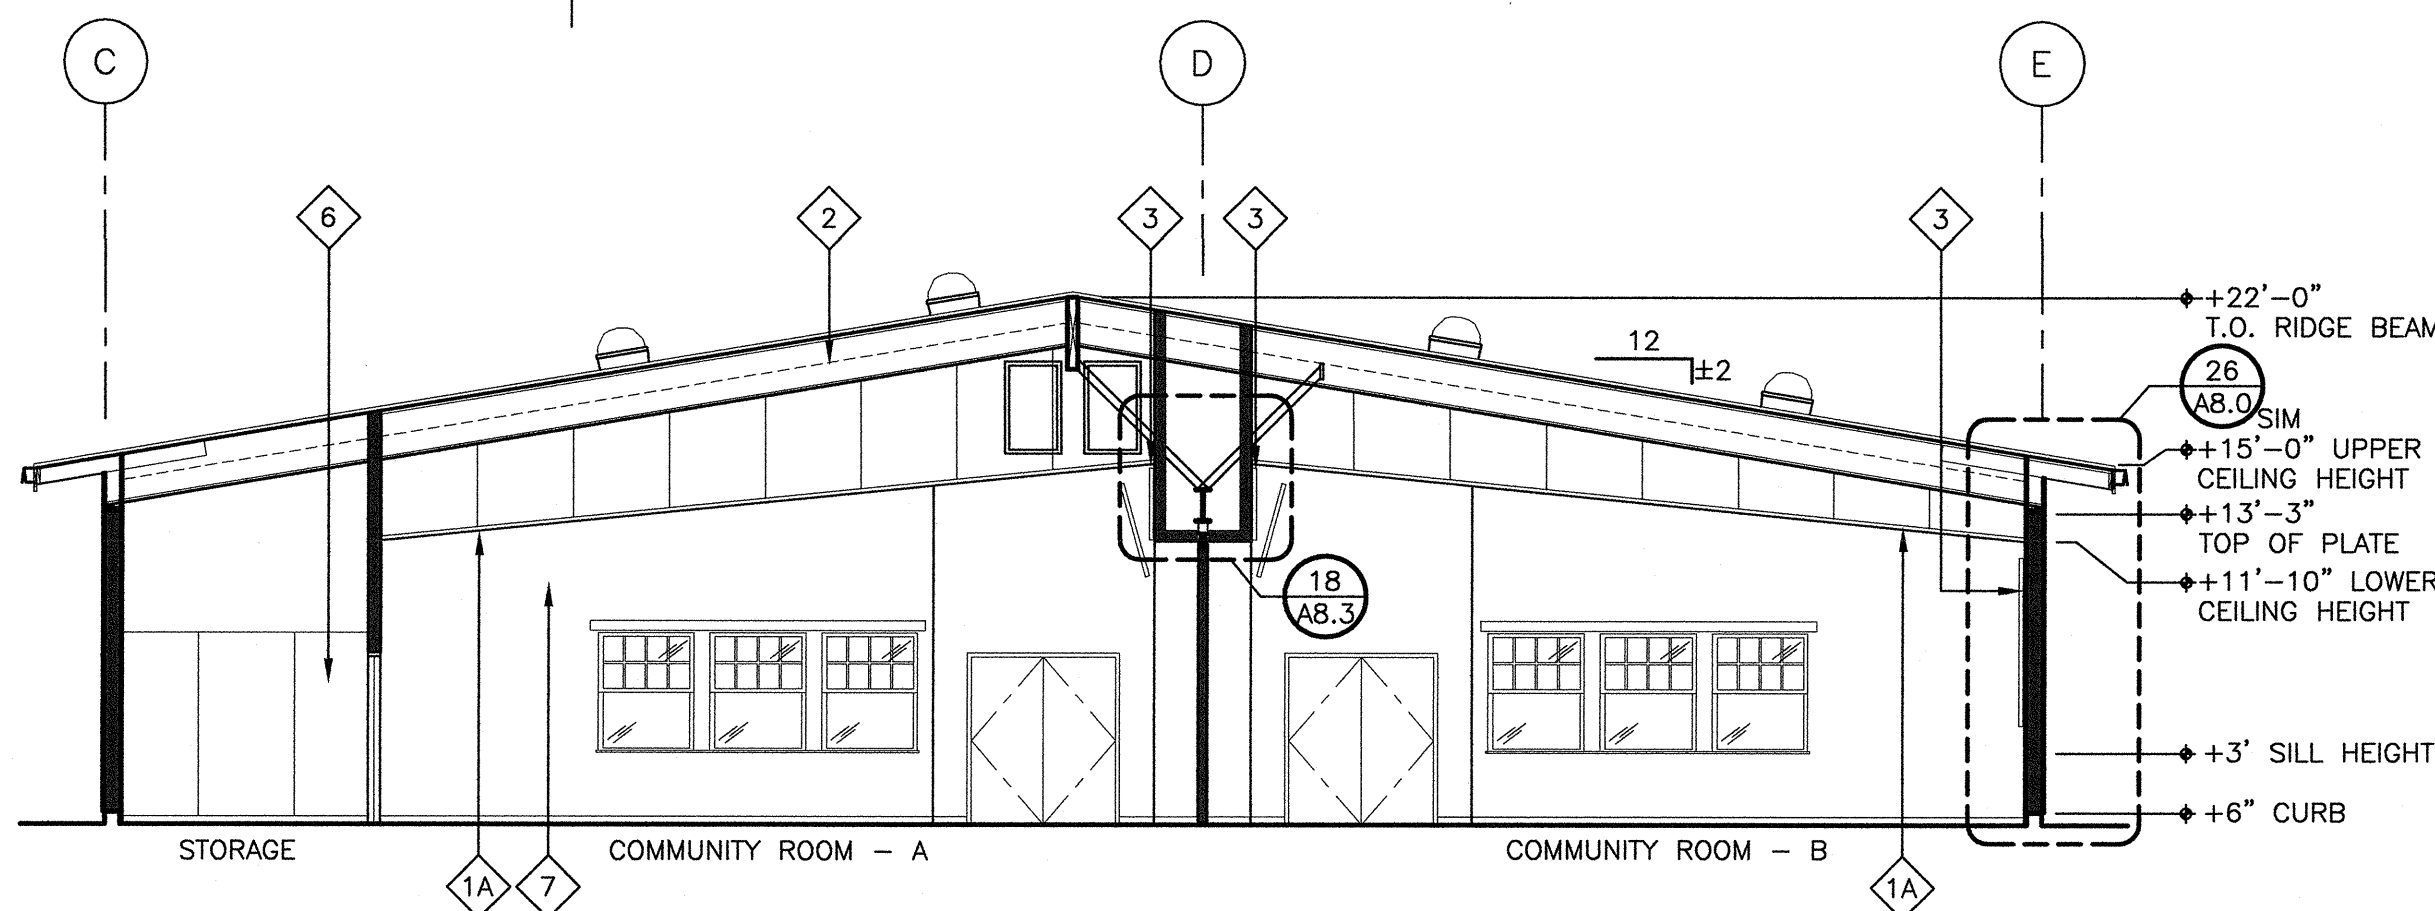

1 Section 1-1
SCALE: 1/8" = 1'-0"

Dry Creek Joint Elementary School District
District Education Center

8849 Cook Riolo Road, Roseville, CA 95747

Dry Creek Joint Elementary School District

FILE NO. 31-15

IDENTIFICATION STAMP DIV. OF THE
STATE ARCHITECT OFFICE OF
REGULATION SERVICES
APPLICATION NO.
02-115456
AC: TM FLS J. M. L. S. R. E. S.
DATE 2/23/17 CCA2


DIVISION OF THE STATE ARCHITECT

revision date: by:

CONSULTANT

nacht&lewis

600 O Street, Suite 100
Sacramento, CA 95811
www.nachtlewis.com
916.329.4000

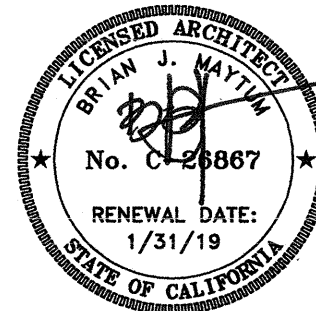

ARCHITECT

INITIAL BOX

NO.	DWG BY	DATE	REVIEWED

REVISIONS

NO.	DESCRIPTION	DATE	REV

DATE February 23, 2017

JOB NO. Y1538.00

SHEET TITLE


Building
Sections

SHEET NO.


A4.1

SHEET ____ OF ____ TOTAL


ONE INCH = ONE FOOT
ONE AND ONE-HALF INCH = ONE FOOT
THREE-QUARTERS INCH = ONE FOOT
ONE-QUARTER INCH = ONE FOOT
ONE-EIGHTH INCH = ONE FOOT
ONE-SIXTEENTH INCH = ONE FOOT
ONE-THIRTY-SECOND INCH = ONE FOOT
ONE INCH = TWENTY FEET

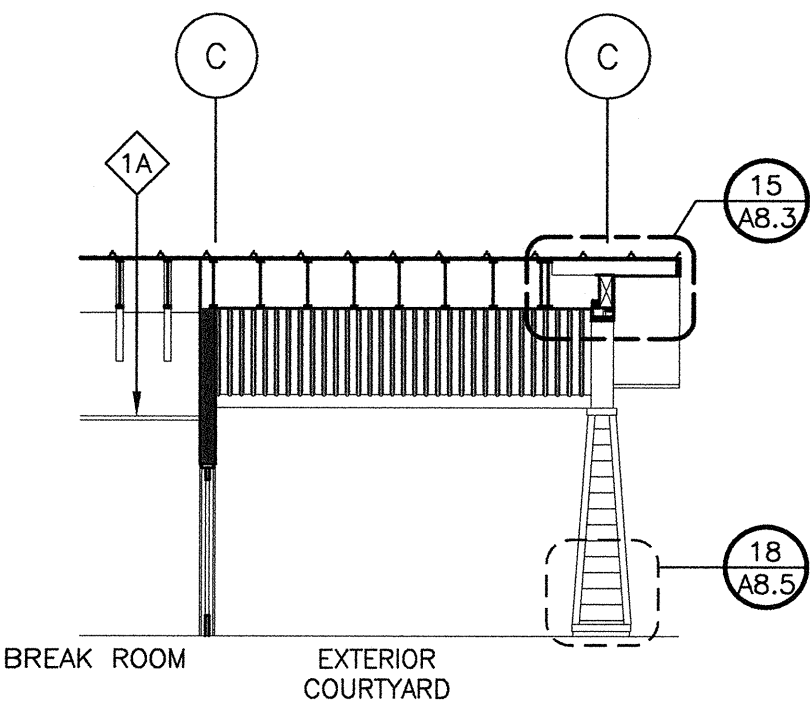


7 Section 7-7
SCALE: 1/8" = 1'-0"

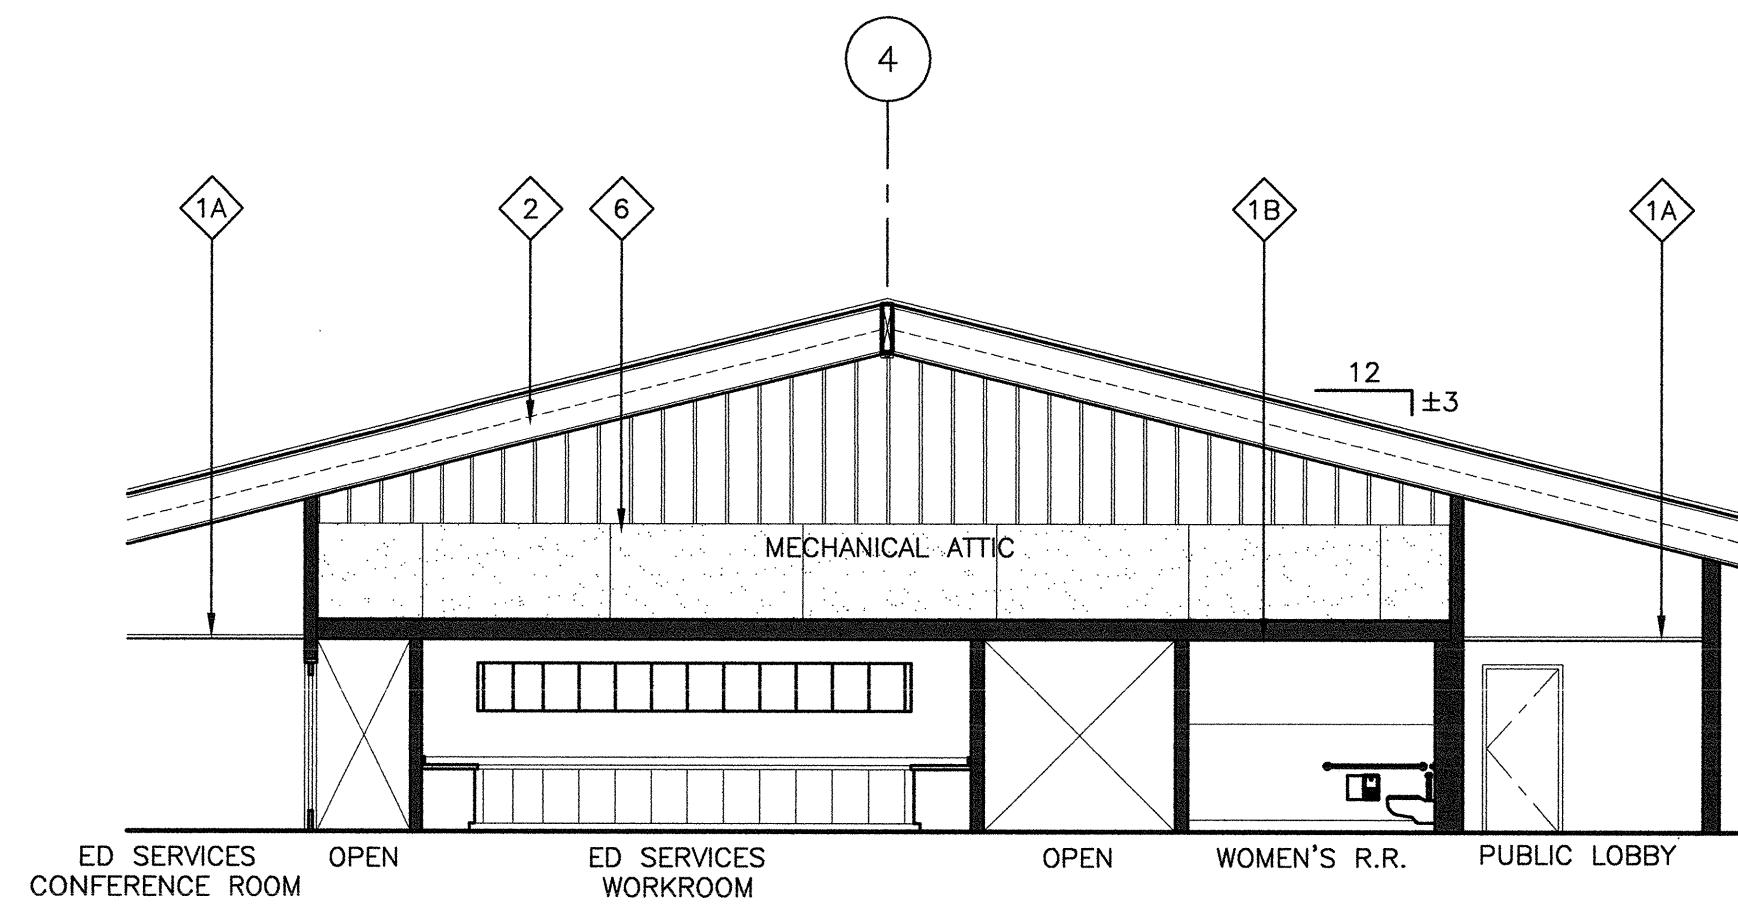


4 Section 4-4
SCALE: 1/8" = 1'-0"

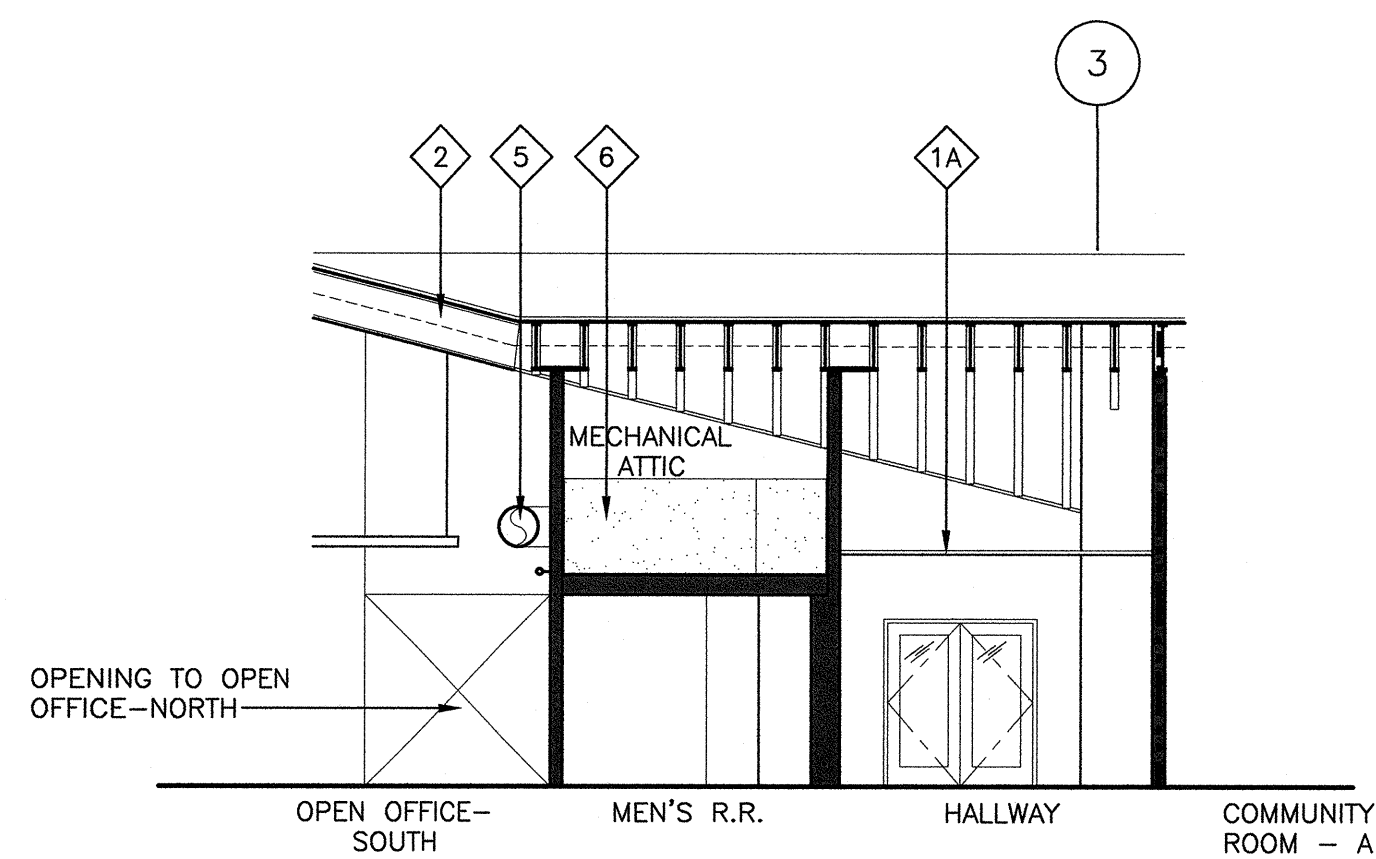


1 Section 1-1
SCALE: 1/8" = 1'-0"

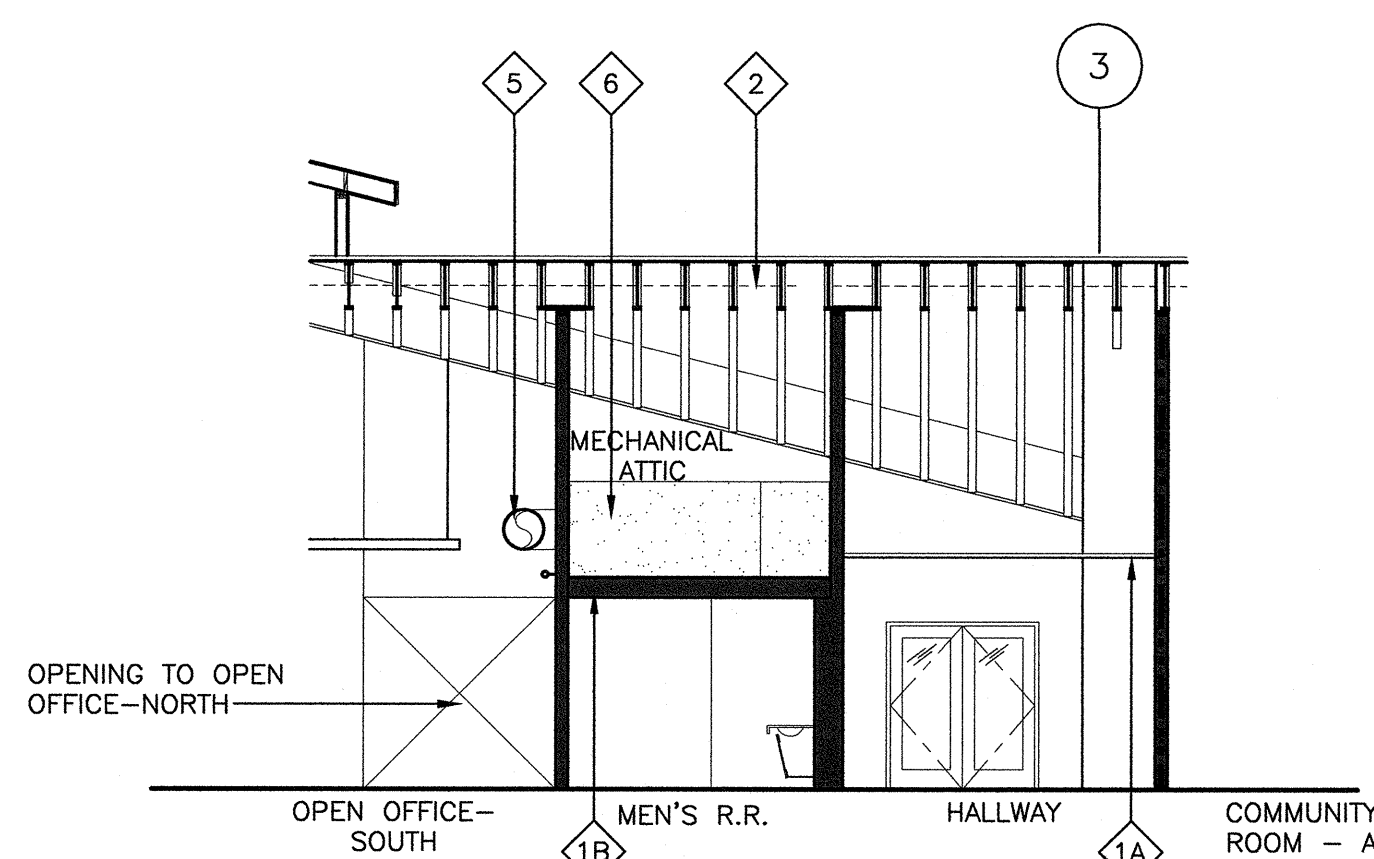


2 Section 2-2
SCALE: 1/8" = 1'-0"

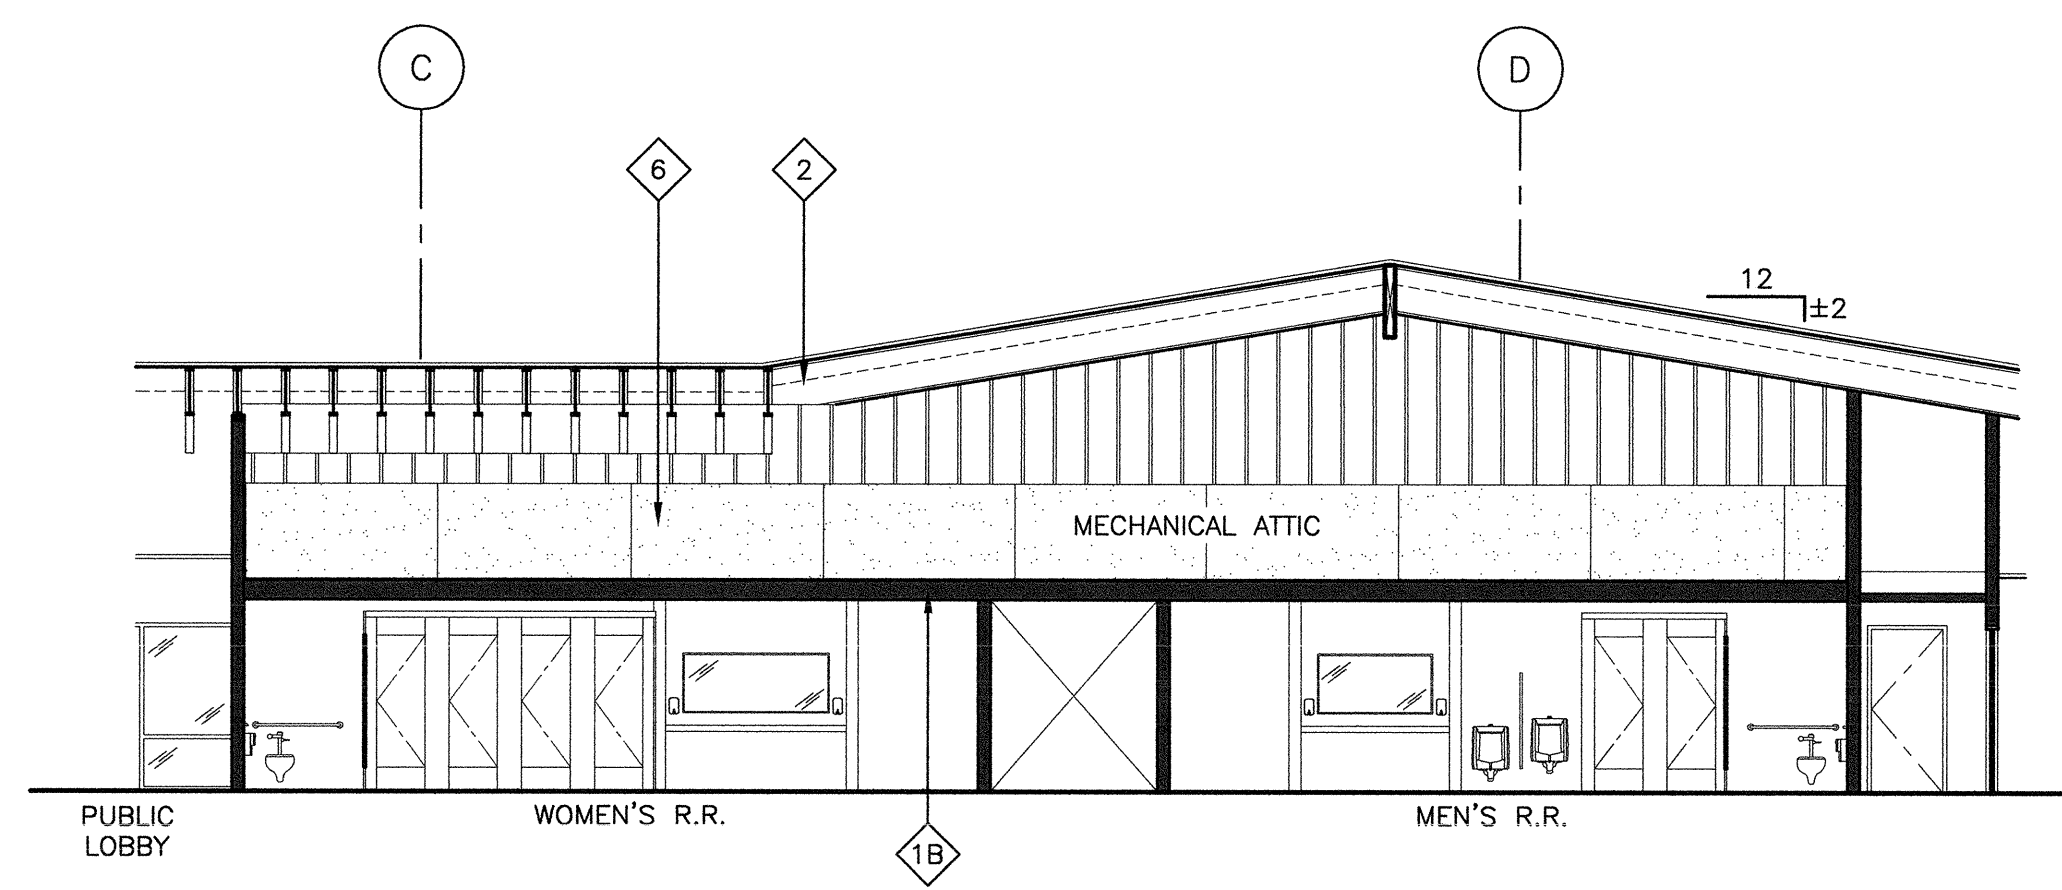

5 Section 5-5
SCALE: 1/8" = 1'-0"

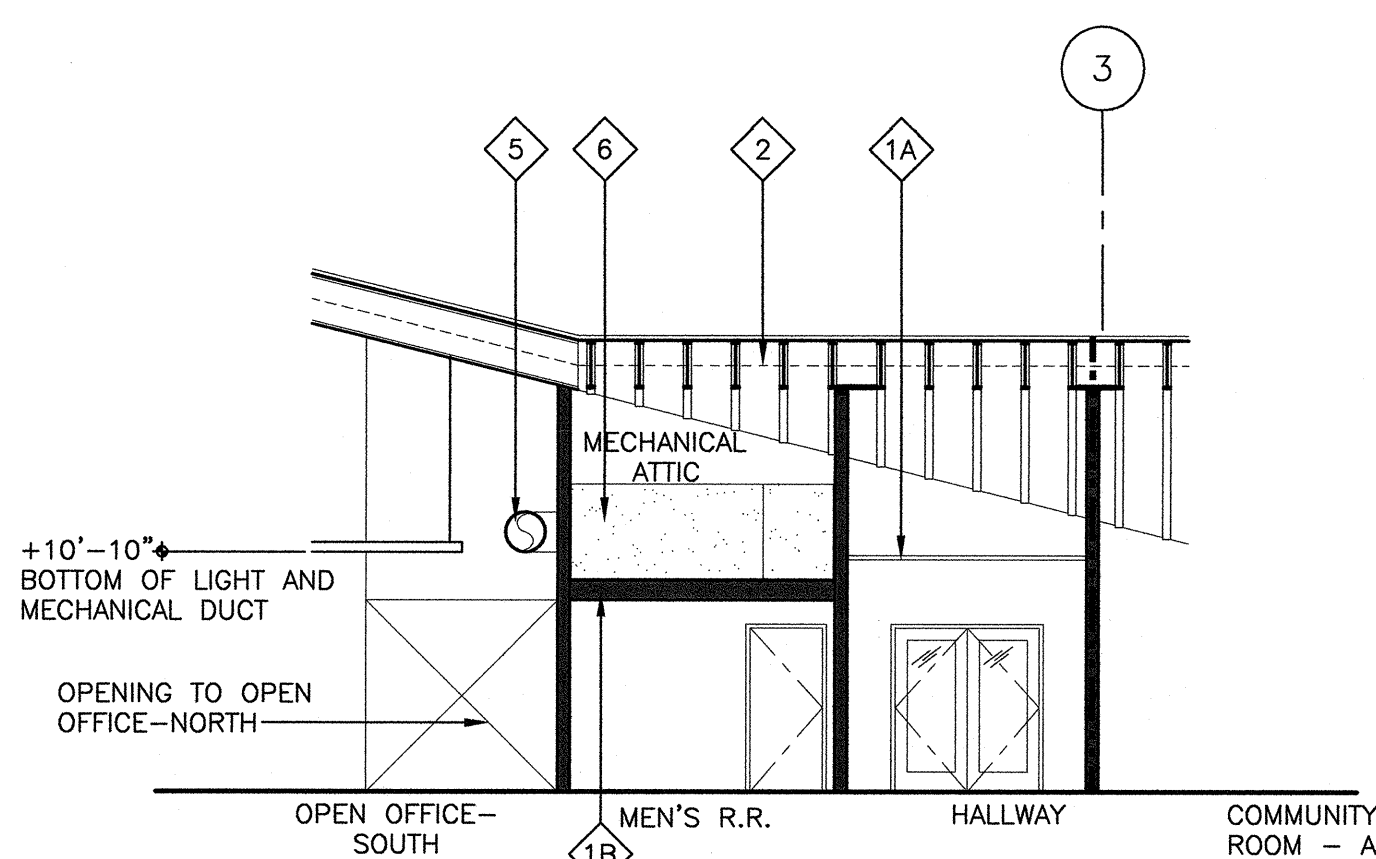

3 Section 3-3
SCALE: 1/8" = 1'-0"

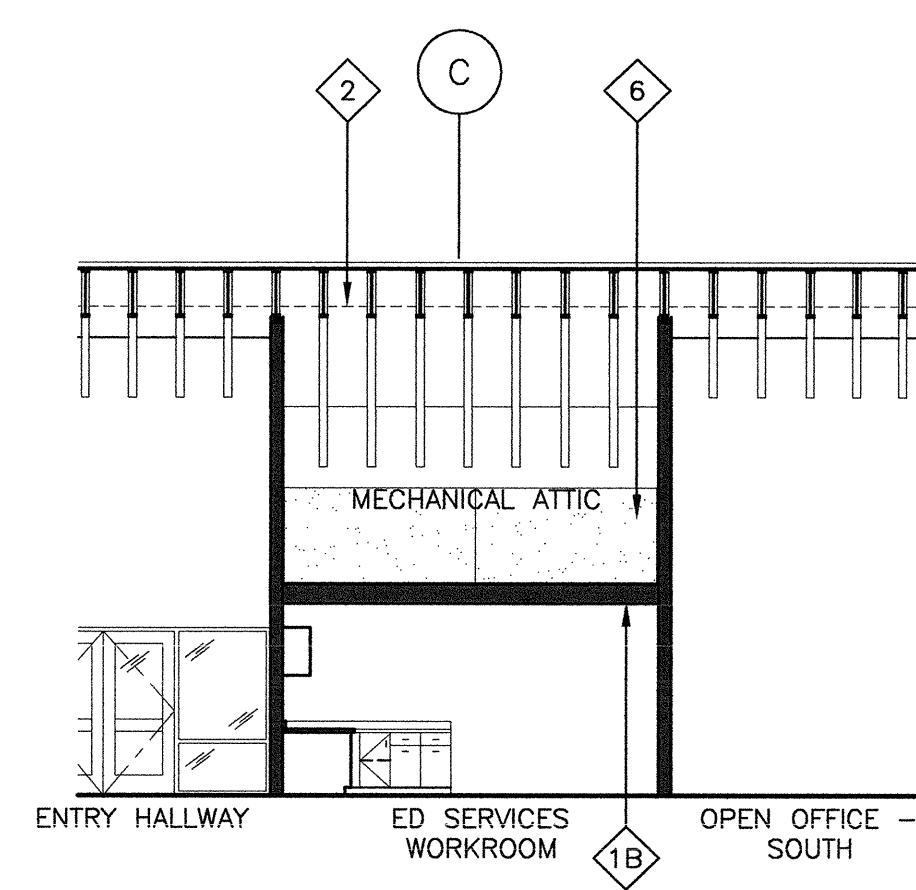

6 Section 6-6
SCALE: 1/8" = 1'-0"

KEYNOTES:

THESE KEYNOTES APPLY TO THIS SHEET ONLY.

- 1 ALL CEILINGS PER CEILING PLAN, SHEET A2.1 - SEE CEILING PLAN FOR HEIGHTS NOT NOTED.
- 1A SUSPENDED T-BAR CEILING.
- 1B GYPSUM WALL BOARD CEILING PER PLAN, ON 2x10 JOISTS @ 16" O.C. MAX.
- 2 BATT INSULATION.
- 3 WALL-MOUNTED T.V. - SEE ELECTRICAL DRAWINGS.
- 4 NOT USED
- 5 MECHANICAL UNIT - SEE MECHANICAL DRAWINGS (TYPICAL).
- 6 1/2" PLYWOOD WAINSCOT - 4'-0" HIGH AT MECHANICAL ATTIC, 8'-0" HIGH AT ALL OTHER LOCATIONS UNLESS OTHERWISE NOTED.
- 7 PENDANT LIGHT FIXTURE - SEE ELECTRICAL DRAWINGS.
- 8 CEILING-HUNG ACOUSTIC PANELS - SEE SPEC. SECTION 09 53 00.
- 9 CEILING FAN - SEE MECHANICAL DRAWINGS.

GENERAL SHEET NOTES:


- 1. ALL INTERIOR WALLS ARE COVERED WITH GYPSUM BOARD AND SEPARATE WALL FINISH. SEE FINISH SCHEDULE ON SHEET A7.1.
- 2. FOR FLOOR FINISHES - SEE SHEET A7.1. SEE SHEET A7.1.1 FOR FLOORING PATTERNS.
- 3. SEE SHEET A7.2 FOR CASEWORK AND EQUIPMENT.
- 4. SEE SHEET A6.1 FOR DOOR AND WINDOW SCHEDULES.
- 5. SEE FLOOR PLAN SHEET A1.0 FOR WEDALL AND PARTITION FRAMING. ALL INTERIOR AND EXTERIOR WALLS SHALL BE INSULATED.

Dry Creek Joint Elementary School District District Education Center

8849 Cook Riolo Road, Roseville, CA 95747

Dry Creek Joint Elementary School District

FILE NO. 31-15

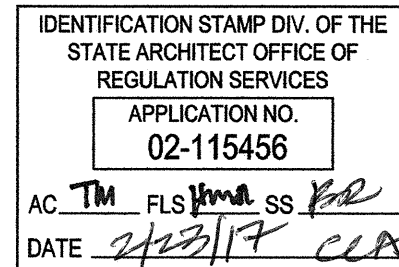


DIVISION OF THE STATE ARCHITECT
revision date: by:

CONSULTANT

nacht&lewis

600 O Street, Suite 100
Sacramento, CA 95811
www.nachtlewis.com
916.329.4000

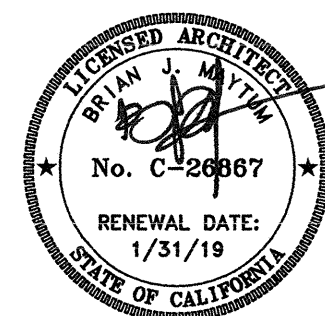

ARCHITECT

INITIAL BOX

NO.	DWG BY	DATE	REVIEWED

REVISIONS

NO.	DESCRIPTION	DATE	REV'D
	100% design development	7/8/16	
	75% construction documents	9/20/16	
	DSA submittal	12/31/16	
	DSA approval	02/23/17	

DATE February 23, 2017

JOB NO. Y1538.00

SHEET TITLE

Building
Sections

SHEET NO.

A4.2

SHEET ____ OF ____ TOTAL

ONE INCH = TWENTY FEET
ONE-SIXTEENTH INCH = ONE FOOT
ONE-EIGHTH INCH = ONE FOOT
ONE-FOURTH INCH = ONE FOOT
ONE-HALF INCH = ONE FOOT
THREE-QUARTERS INCH = ONE FOOT
ONE INCH = ONE FOOT
ONE AND ONE-HALF INCH = ONE FOOT

KEYNOTES:

THESE KEYNOTES APPLY TO THIS SHEET ONLY.



- 1 STANDING SEAM METAL ROOFING.
- 2 BOX GUTTER BY ROOFING MANUFACTURER.
- 3 RAIN WATER LEADER LOCATION, TYPICAL - SEE DETAIL 26/A8.0.
- 4A UNIT SKYLIGHT - 22"x22" - SEE DETAIL 27/A8.3.
- 4B UNIT SKYLIGHT - 22"x96" - SEE DETAIL 27/A8.3.
- 4C TUBULAR SKYLIGHT - 24" DIA. - SEE DETAILS 3/A5.0 & 17/A8.3.
- 5 LOCATION OF FUTURE PHOTO VOLTAIC PANELS - 2.832 SF MINIMUM REQUIRED, 2,920 SF PROVIDED AS SHOWN.
- 6 METAL CRICKET AT TOP OF SKYLIGHT - SEE DETAIL 27/A8.3.
- 7 VENT THRU ROOF - SEE PLUMBING DRAWINGS. PROVIDE PIPE PENETRATION FLASHING AS SHOWN IN DETAIL 2/A5.0.

GENERAL SHEET NOTES:


- ALL ROOF PIPE PENETRATIONS SHALL BE FLASHED PER DECK-TIGHT INSTALLATION DETAIL SHOWN BELOW AND AS DESCRIBED BY MBCL.
- SEE SPEC SECTION 07 41 13-3.02-A-1 FOR SPECIFIC LOCATIONS WHERE SAMS TYPE MATERIAL IS REQUIRED TO BE INSTALLED IN ADDITION TO LOCATIONS REQUIRED FOR STANDARD INSTALLATION OR TO OBTAIN WARRANTY.

7- INDICATES WALL TYPES, SEE SHEET A8.0

STANDING SEAM ROOF CLIP SPACING:

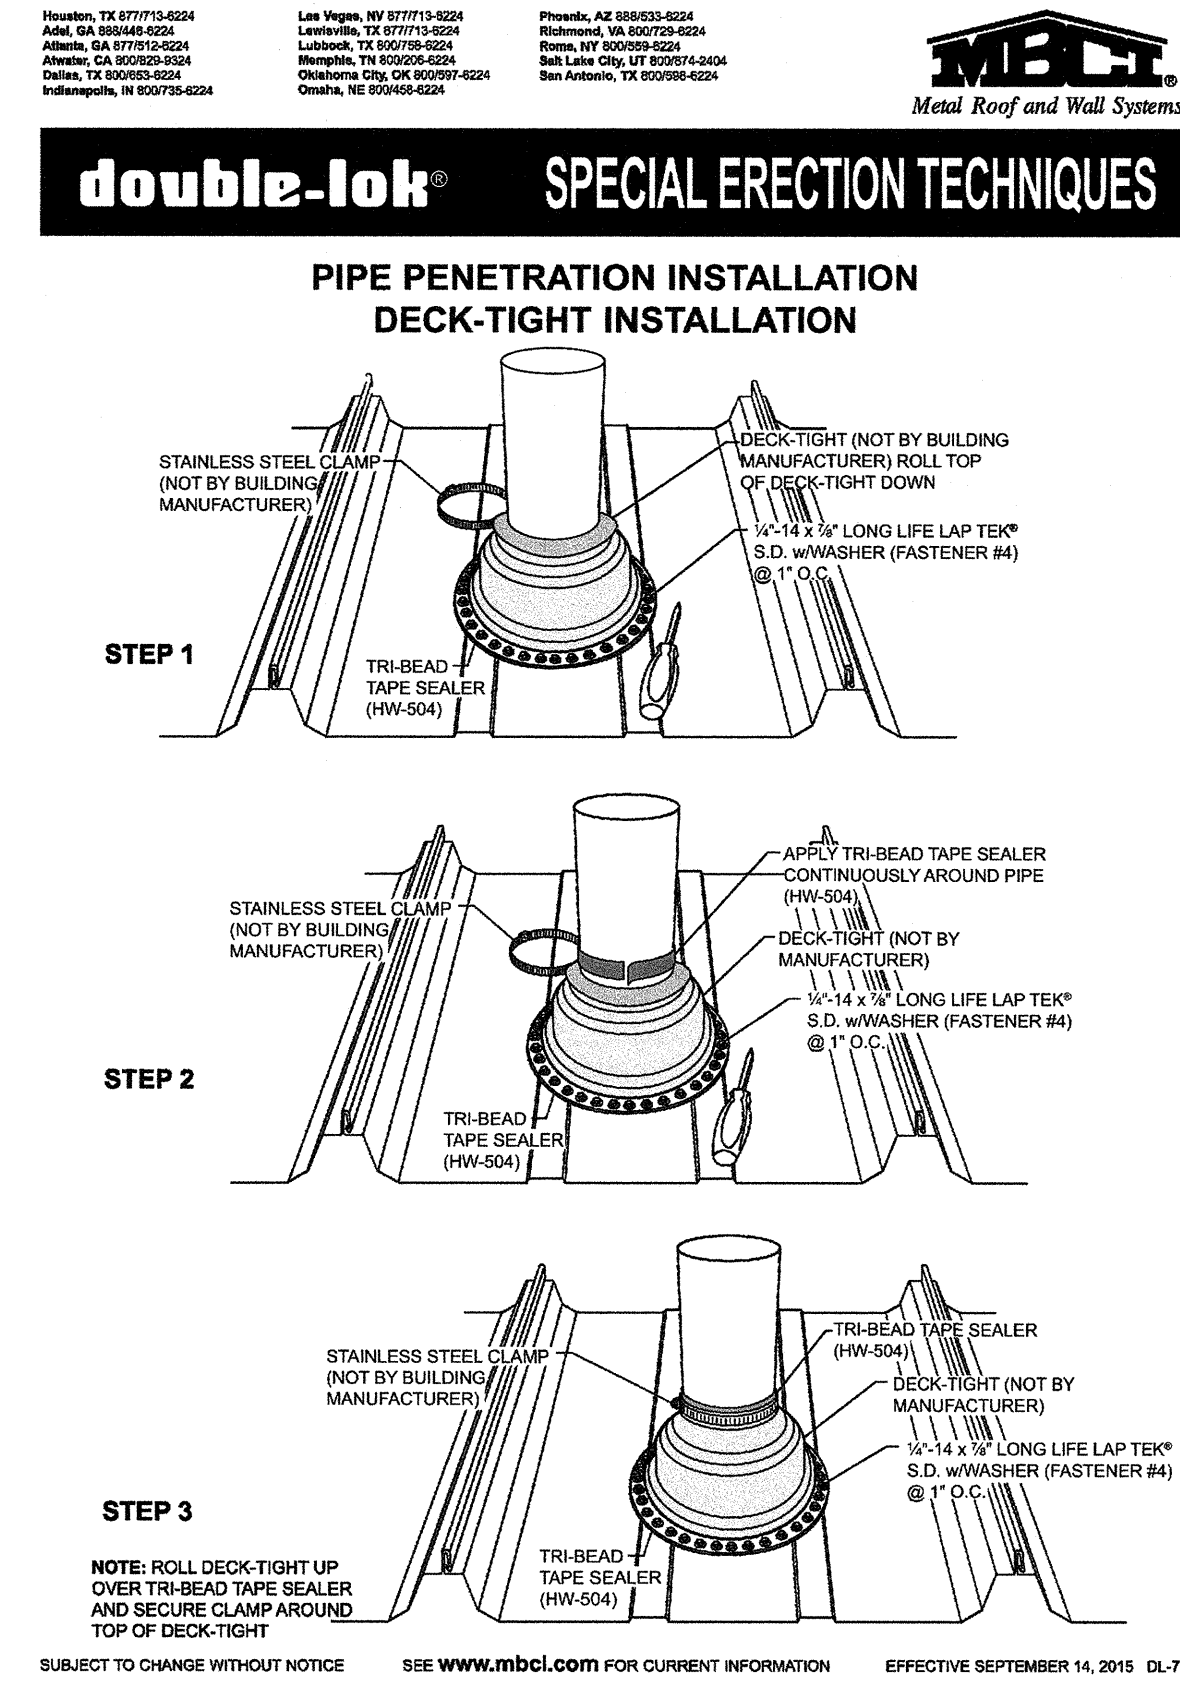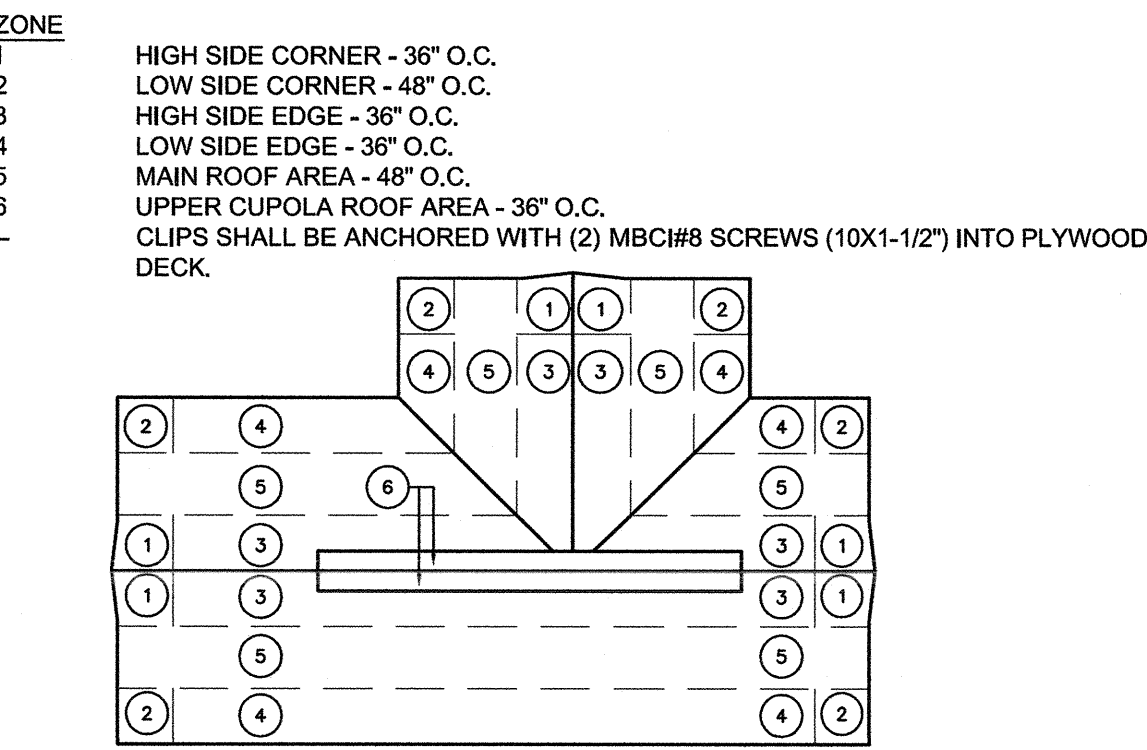


2 Pipe Flashing Thru Roof
SCALE: N.T.S.

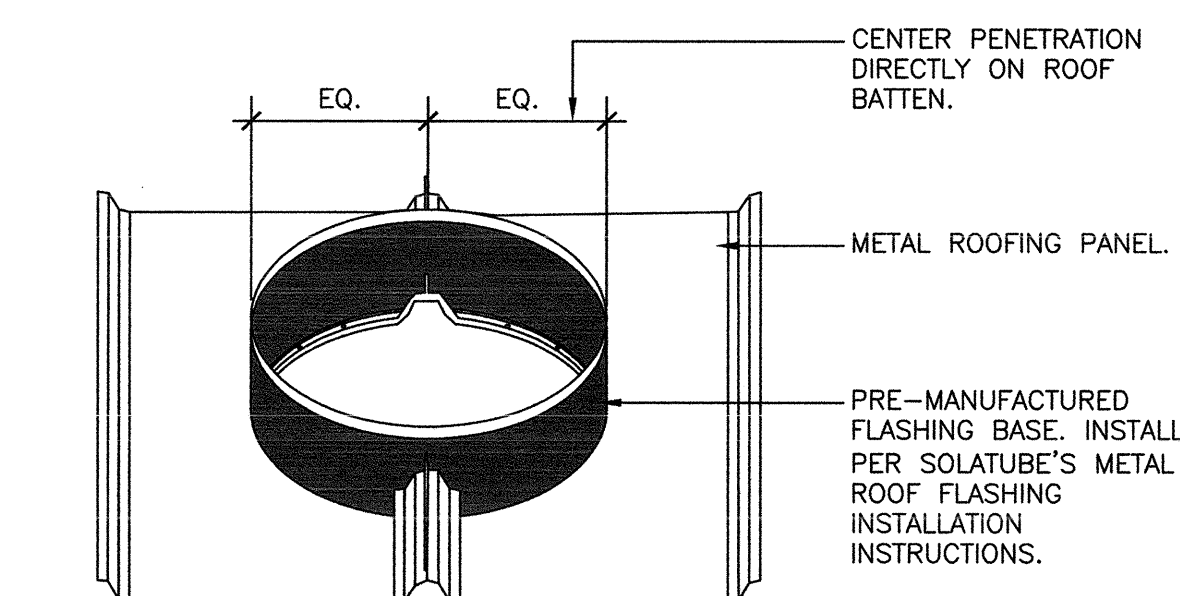

3 Solatube Roof Penetration
SCALE: N.T.S.

1 Roof Plan
SCALE: 1/8" = 1'-0"

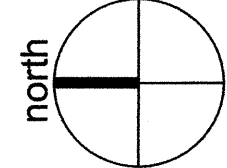

Dry Creek Joint Elementary School District
District Education Center

8849 Cook Riolo Road, Roseville, CA 95747

Dry Creek Joint Elementary School District


FILE NO. 31-15
IDENTIFICATION STAMP DIV. OF THE
STATE ARCHITECT OFFICE OF
REGULATION SERVICES
APPLICATION NO.
02-115456
AC. TM FLS SS SS
DATE 2/23/17 CLP

DIVISION OF THE STATE ARCHITECT
revision date: by:

CONSULTANT

nacht&lewis

600 Q Street, Suite 100
Sacramento, CA 95811
www.nachtandlewis.com
916.329.4000

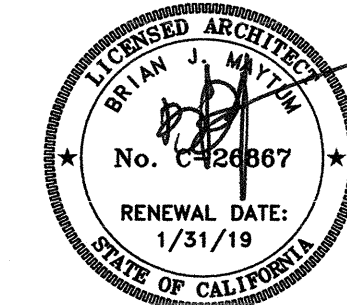

ARCHITECT

INITIAL BOX

NO.	DWG BY	DATE	REVIEWED

REVISIONS

NO.	DESCRIPTION	DATE	REV'D
	100% design development	7/6/16	
	75% construction documents	9/20/16	
	DSA submittal	12/31/16	
	DSA approval	02/23/17	

DATE February 23, 2017

JOB NO. Y1538.00

SHEET TITLE


Roof Plan

SHEET NO.


A5.0

SHEET ___ OF ___ TOTAL

ONE AND ONE-HALF INCH = ONE FOOT
THREE-QUARTERS INCH = ONE FOOT
ONE INCH = ONE FOOT
ONE-QUARTER INCH = ONE FOOT
ONE-EIGHTH INCH = ONE FOOT
ONE-SIXTEENTH INCH = ONE FOOT
ONE INCH = TWENTY FEET

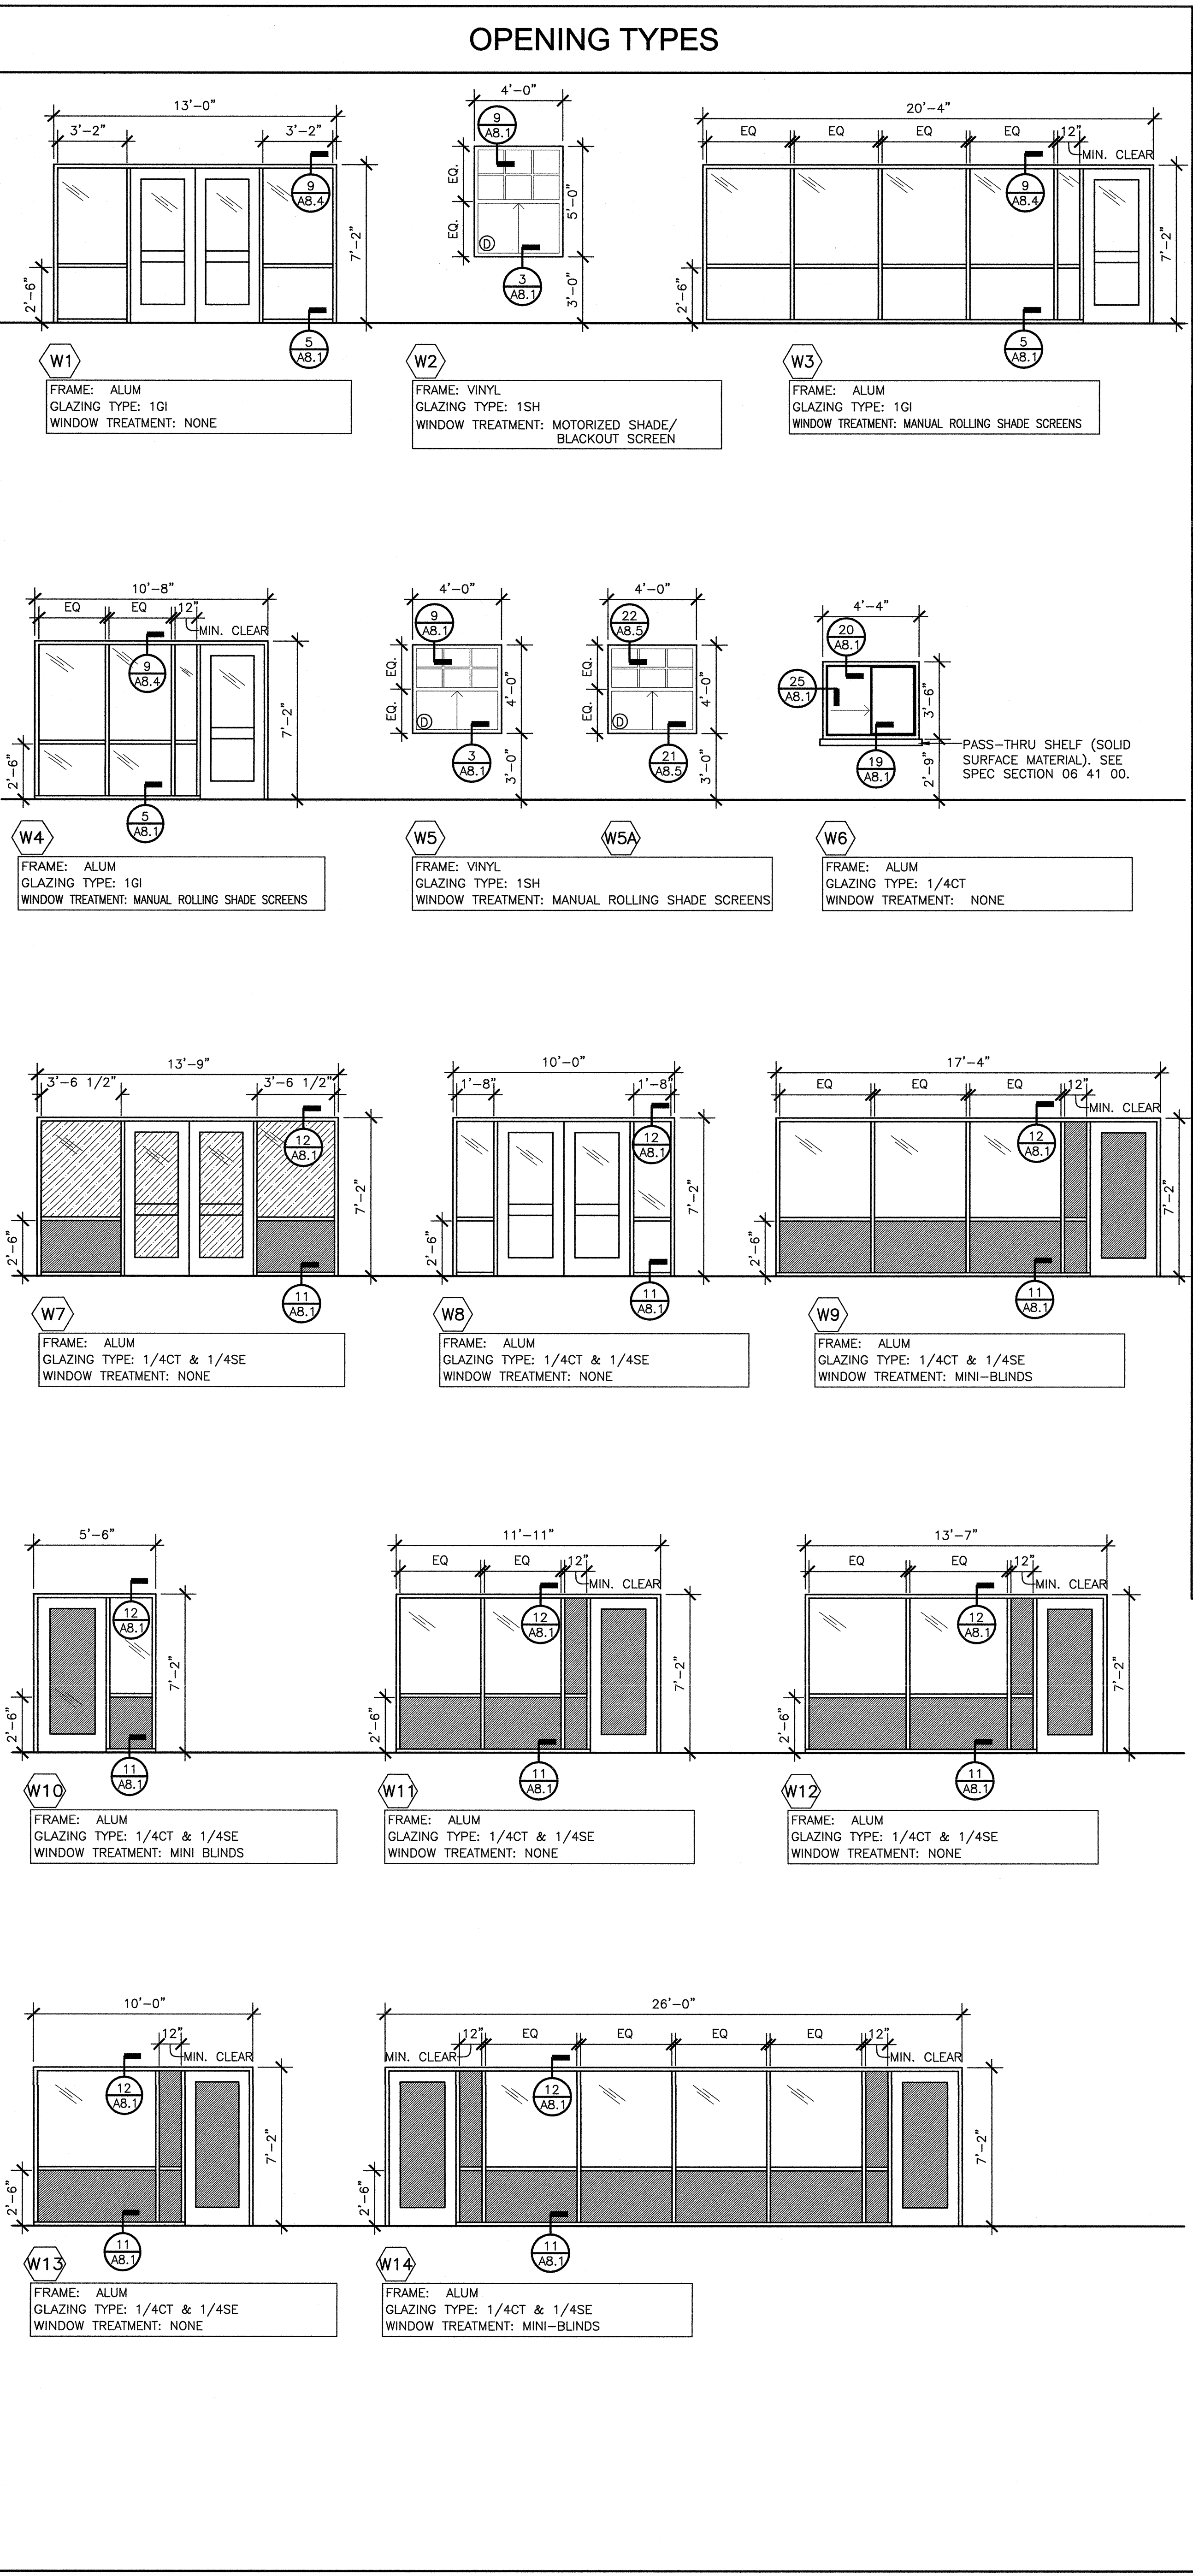




DOOR SCHEDULE													
DOOR NO.	DOOR					HWR. GROUP	FRAME		DETAILS				REMARKS
	NOMINAL DOOR SIZE	TYPE	MAT	FIN	GLASS		MAT	FIN	HEAD	JAMB	JAMB	SILL	
100A	PR. 3'-0" X 7'-0"	B	D	3	1GI	E01	D	3	10/A8.1	7/A8.1	10/A8.4	27/A8.5	V-3, S-2
100B	PR. 3'-0" X 7'-0"	B	D	3	1/4SE	I10	D	3	30/A8.1	4/A8.4	4/A8.4	26/A8.5	V-2, S-3
101	3'-0" X 7'-0"	A	A	1	-	I04	B	2	18/A8.1	17/A8.1	17/A8.1	28/A8.5	S-6
102	PR. 3'-0" X 7'-0"	B	D	3	1/4CT	I10	D	3	30/A8.1	12/A8.1	12/A8.1	26/A8.5	V-3, S-3
103A	PR. 3'-0" X 7'-0"	B	A	1	1/4CT	I06	B	2	16/A8.1	17/A8.1	17/A8.1	26/A8.5	20 MIN., V-4, S-1, S-3
103B	PR. 3'-0" X 7'-0"	B	B	2	-	E01	B	2	15/A8.1	14/A8.1	14/A8.1	27/A8.5	S-1, S-2
104A	PR. 3'-0" X 7'-0"	B	A	1	1/4CT	I06	B	2	16/A8.1	17/A8.1	17/A8.1	26/A8.5	20 MIN., V-4, S-1, S-3
104B	PR. 3'-0" X 7'-0"	B	B	2	-	E01	B	2	15/A8.1	14/A8.1	14/A8.1	27/A8.5	S-1, S-2
104C	3'-0" X 7'-0"	A	B	2	-	E03	B	2	15/A8.1	14/A8.1	14/A8.1	27/A8.5	S-1, S-2
105	PR. 3'-6" X 7'-0"	B	A	1	-	I07	B	2	18/A8.1	18/A8.1	18/A8.1	26/A8.5	S-1, L-1x2
106A	3'-6" X 7'-0"	A	A	1	1/4CT	I09	B	2	18/A8.1	17/A8.1	17/A8.1	26/A8.5	V-4, S-1
106B	3'-6" X 7'-0"	A	A	1	1/4CT	I08	B	2	18/A8.1	18/A8.1	18/A8.1	26/A8.5	V-4, S-1
106C	3'-0" X 7'-0"	A	D	3	1GI	E02	D	3	10/A8.1	7/A8.1	29/A8.4	27/A8.5	V-3, S-1, S-2
107	3'-4" X 7'-0"	A	A	1	-	I08	B	2	18/A8.1	18/A8.1	18/A8.1	26/A8.5	L-1, S-1
108	3'-0" X 7'-0"	A	A	1	-	I03	B	2	18/A8.1	17/A8.1	17/A8.1	28/A8.5	S-4, L-1
109	3'-0" X 7'-0"	A	A	1	-	I03	B	2	18/A8.1	17/A8.1	17/A8.1	28/A8.5	S-5, L-1
110A	3'-0" X 7'-0"	A	A	1	1/4CT	I09	B	2	18/A8.1	17/A8.1	17/A8.1	26/A8.5	V-4, S-3
110B	3'-0" X 7'-0"	A	A	1	1/4CT	I09	B	2	18/A8.1	17/A8.1	17/A8.1	26/A8.5	V-4, S-3
110C	3'-0" X 7'-0"	A	D	3	1GI	E02	D	3	10/A8.1	29/A8.4	19/A8.4	26/A8.5	V-3, S-2, R-1
111A	3'-0" X 7'-0"	A	A	1	1/4SE	I01	D	3	30/A8.1	30/A8.1	19/A8.4	27/A8.5	V-1, S-1
111B	3'-0" X 7'-0"	A	B	2	-	E03	B	2	15/A8.1	19/A8.4	14/A8.1	26/A8.5	
112	3'-0" X 7'-0"	A	A	1	1/4SE	I01	D	3	30/A8.1	30/A8.1	12/A8.1	27/A8.5	V-1, S-1
113	3'-0" X 7'-0"	A	A	1	1/4SE	I01	D	3	30/A8.1	30/A8.1	12/A8.1	26/A8.5	V-1, S-1
114	3'-0" X 7'-0"	A	A	1	1/4SE	I01	D	3	30/A8.1	30/A8.1	12/A8.1	26/A8.5	V-1, S-1
115	3'-0" X 7'-0"	A	A	1	1/4SE	I01	D	3	30/A8.1	30/A8.1	12/A8.1	26/A8.5	V-1, S-1
116	3'-0" X 7'-0"	A	A	1	1/4SE	I01	D	3	30/A8.1	30/A8.1	12/A8.1	26/A8.5	V-1, S-1
117	3'-0" X 7'-0"	A	A	1	1/4SE	I01	D	3	30/A8.1	30/A8.1	12/A8.1	26/A8.5	V-1, S-1
118	3'-0" X 7'-0"	A	A	1	1/4SE	I01	D	3	30/A8.1	30/A8.1	12/A8.1	26/A8.5	V-1, S-1
119	3'-0" X 7'-0"	A	A	1	1/4SE	I01	D	3	30/A8.1	30/A8.1	12/A8.1	26/A8.5	V-1, S-1
120	3'-0" X 7'-0"	A	A	1	1/4SE	I01	D	3	30/A8.1	30/A8.1	12/A8.1	26/A8.5	V-1, S-1
121A	3'-0" X 7'-0"	A	A	1	1/4SE	I01	D	3	30/A8.1	30/A8.1	12/A8.1	26/A8.5	V-1, S-1
121B	3'-0" X 7'-0"	A	A	1	1/4SE	I01	D	3	30/A8.1	30/A8.1	12/A8.1	26/A8.5	V-1, S-1
122	3'-0" X 7'-0"	A	A	1	1/4SE	I01	D	3	30/A8.1	30/A8.1	12/A8.1	26/A8.5	V-1, S-1
123	3'-0" X 7'-0"	A	A	1	1/4SE	I01	D	3	30/A8.1	30/A8.1	12/A8.1	26/A8.5	V-1, S-1
124	3'-0" X 7'-0"	A	A	1	1/4SE	I01	D	3	30/A8.1	30/A8.1	12/A8.1	26/A8.5	V-1, S-1
125	3'-0" X 7'-0"	A	A	1	1/4SE	I01	D	3	30/A8.1	30/A8.1	12/A8.1	27/A8.5	V-1, S-1
126	3'-0" X 7'-0"	A	B	2	1GI	E02	B	2	25/A8.1	14/A8.1	14/A8.1	26/A8.5	V-2, S-1, S-2
127	3'-6" X 7'-0"	A	A	1	1/4CT	I02	D	3	30/A8.1	12/A8.1	12/A8.1	26/A8.5	V-1, S-1
128A	PR. 2'-11" X 7'-0"	B	A	1	-	I07	B	2	18/A8.1	18/A8.1	18/A8.1	26/A8.5	S-1
128B	PR. 2'-11" X 7'-0"	B	A	1	-	I07	B	2	18/A8.1	18/A8.1	18/A8.1	26/A8.5	
129	3'-6" X 7'-0"	A	A	1	1/4CT	I02	B	2	18/A8.1	18/A8.1	18/A8.1	26/A8.5	V-2, S-1
131	3'-0" X 7'-0"	A	A	1	1/4SE	I01	D	3	30/A8.1	12/A8.1	12/A8.1	26/A8.5	V-1, S-1
132	3'-0" X 7'-0"	A	A	1	1/4SE	I01	D	3	30/A8.1	30/A8.1	12/A8.1	26/A8.5	V-1, S-1
133	3'-0" X 7'-0"	A	A	1	1/4SE	I01	D	3	30/A8.1	30/A8.1	30/A8.1	26/A8.5	V-1, S-1
134	3'-0" X 7'-0"	A	B	2	-	E04	B	2	15/A8.1	14/A8.1	14/A8.1	27/A8.5	S-7
G1	4'-0" X 6'-0"	-	-	-	-	G01	-	-					SEE DETAIL 7 / A0.6
G2	4'-0" X 6'-0"	-	-	-	-	G02	-	-					SEE SHT. A0.3 AND DTL. 12 / A0.6
G3	4'-0" X 6'-0"	-	-	-	-	G02	-	-					SEE SHT. A0.3 AND DTL. 12 / A0.6
G4	(E) SITE TRAFFIC SWING GATE	-	-	-	-	-	-	-					RELOCATE AND MODIFY PER SITE PLAN
G5	(E) SITE TRAFFIC CANTILEVER GATE	-	-	-	-	-	-	-					RELOCATE AND MODIFY PER SITE PLAN

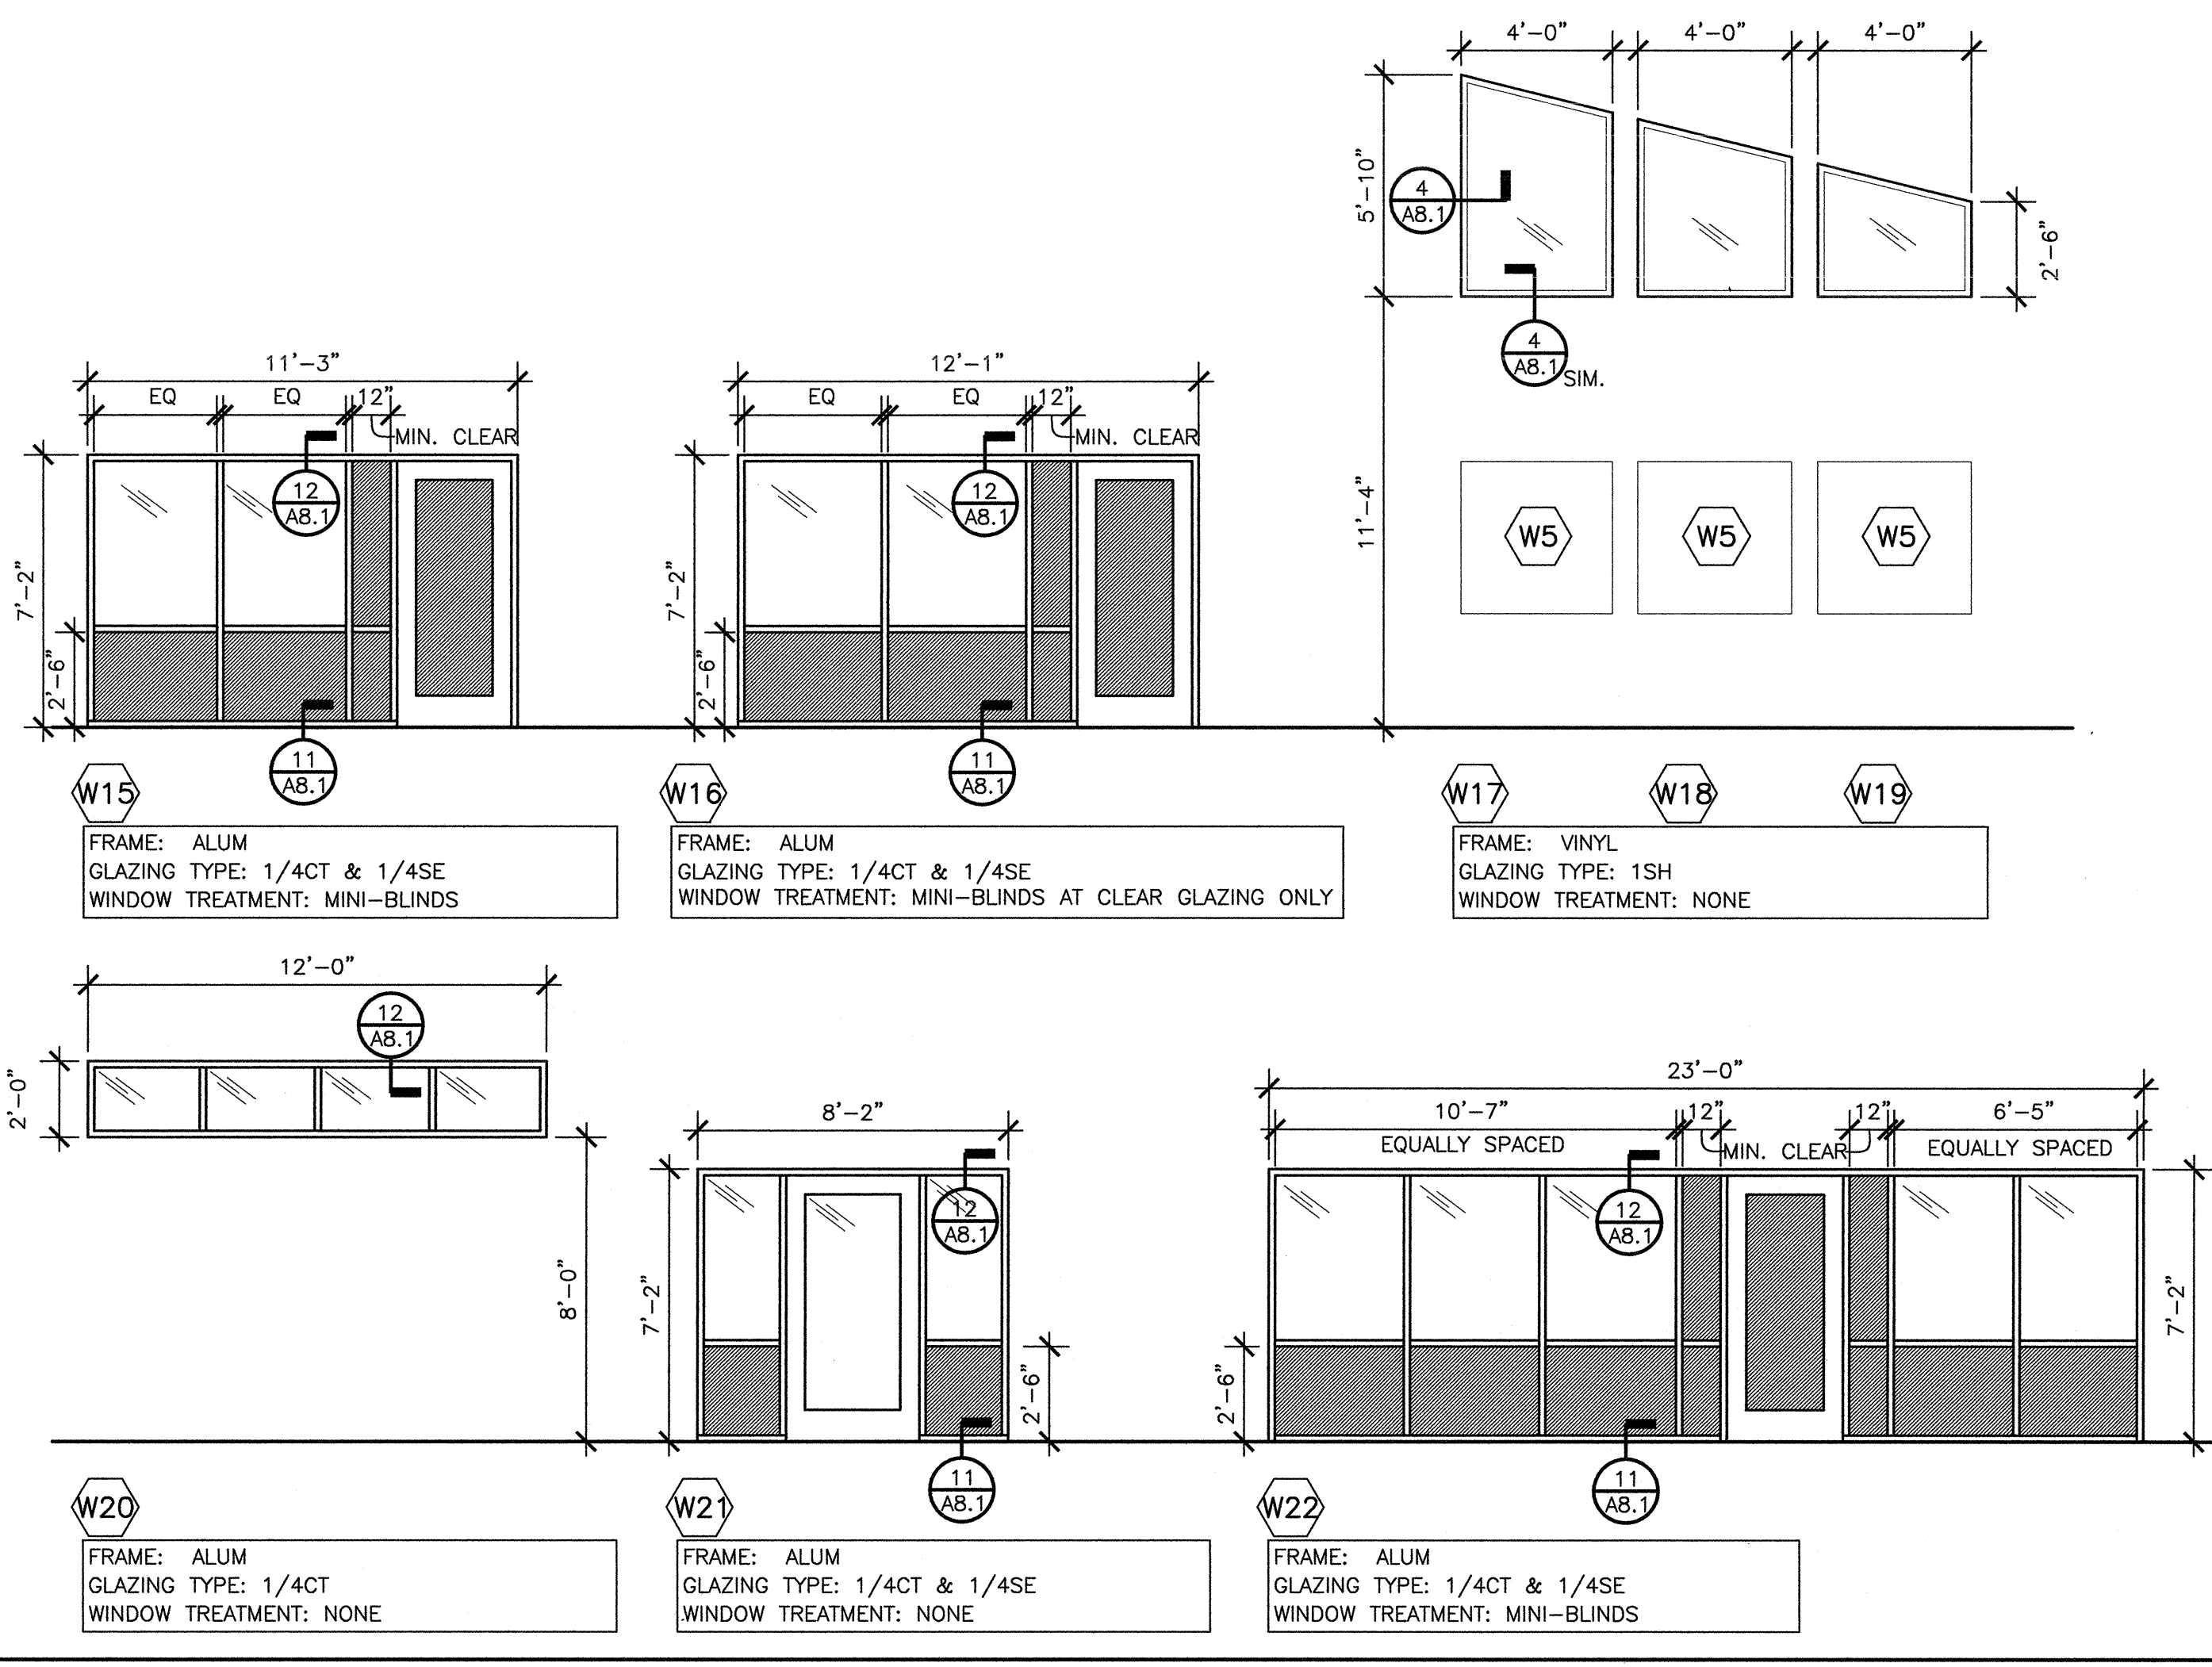

DOOR SCHEDULE LEGEND		
MATERIAL TYPE	FINISH TYPE	GLAZING TYPE
A. WOOD B. HOLLOW METAL C. NOT USED D. ALUMINUM E. CHAIN LINK	1. STAIN AND SEALER 2. PAINT 3. FACTORY FINISH	1. SEE SPEC SECTION 08 43 13 FOR ALL GLAZING TYPES.

DOOR TYPES

NOT TO SCALE

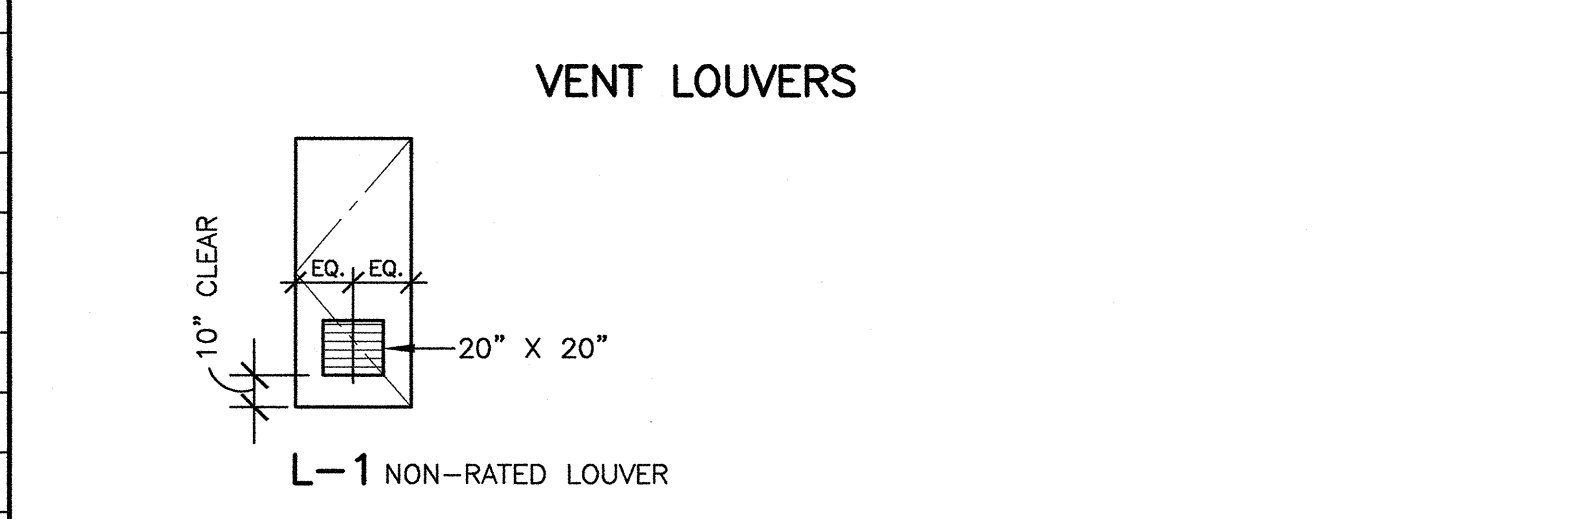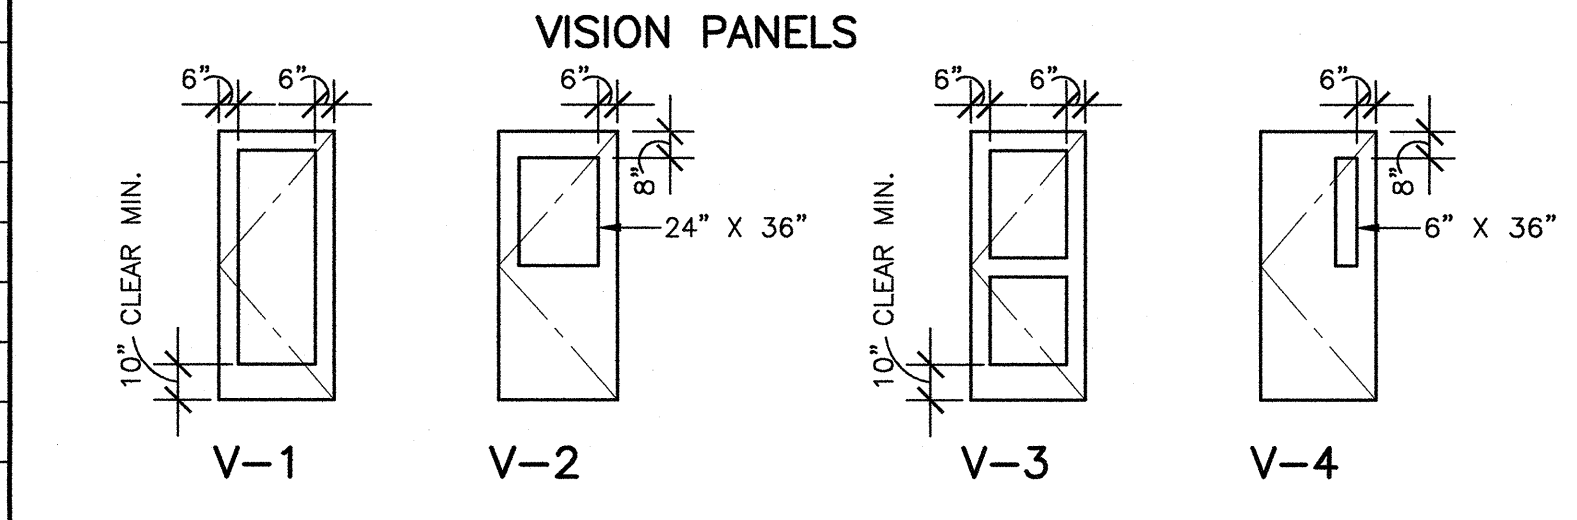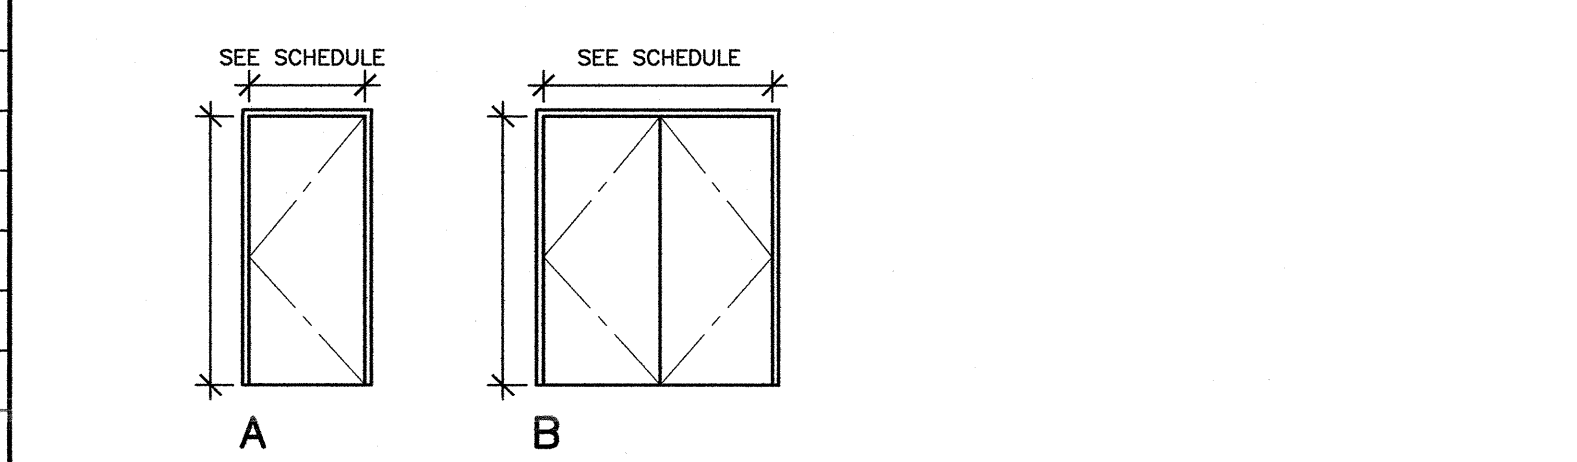

DOOR SIGNAGE & REMARK NOTES

- REMARK NOTES
- FOR SIGN TYPES SEE DETAILS ON SHEET A8.1 AND SPEC SECTION 10 14 00. FOR ADDITIONAL SIGNS NOT SCHEDULED IN THIS DOOR SCHEDULE, SEE KEYNOTES ON FLOOR PLANS, EQUIPMENT PLANS AND SITE PLANS.
 - SIGN SIZES SHOWN IN DETAILS ARE MINIMUM. CONTRACTOR TO VERIFY ACTUAL SIGN SIZE DURING SUBMITTAL.
- SIGN TYPE:
- S-1 PROVIDE ROOM IDENTIFICATION SIGN - SEE DETAIL 28/A8.1.
 - S-2 PROVIDE EXIT SIGN - SEE DETAIL 28/A8.1 SIMILAR.
 - S-3 PROVIDE EXIT ROUTE SIGN - SEE DETAIL 28/A8.1 SIMILAR.
 - S-4 PROVIDE ACCESSIBLE "MEN'S" TOILET ROOM SIGN - SEE DETAIL 26/A8.1.
 - S-5 PROVIDE ACCESSIBLE "WOMEN'S" TOILET ROOM SIGN - SEE DETAIL 26/A8.1.
 - S-6 PROVIDE ACCESSIBLE "ALL GENDER RESTROOM" TOILET ROOM SIGN - SEE DETAIL 26/A8.1.
 - S-7 PROVIDE 3" VINYL TRANSFER LETTERS "FIRE RISER ROOM".
 - S-8 PROVIDE ASSISTIVE LISTENING SYSTEM SIGN.
 - S-9 PROVIDE OCCUPANCY LIMIT POSTING SIGN.
 - S-10 PROVIDE INTERIOR LOBBY GRAPHIC WALL SIGN AND LETTERS.
 - S-11 PROVIDE EXTERIOR BUILDING GRAPHIC WALL SIGN.
- R-1 PROVIDE FIXED SHADE SCREEN PANEL AT DOOR LITE.
- 20 MIN. INDICATES LABELED DOOR AND FRAME ASSEMBLY IN 1-HR FIRE RATED OCCUPANCY SEPARATION.
- DOOR GENERAL NOTES:
- NEW DOORS SHALL HAVE 1/4" MAXIMUM UNDERCUT ABOVE SILL SURFACE MATERIAL EXCEPT AS REQUIRED BY MECHANICAL DRAWINGS. AT EXTERIOR DOORS, THIS IS TO BE MEASURED FROM THE EXTERIOR FINISH SURFACE.
 - ALL DOORS IN THE ACCESSIBLE PATH OF TRAVEL SHALL:
 - PROVIDE 32" OF CLEAR ACCESS
 - BE PROVIDED WITH LEVER TYPE OR PANIC BAR LOCKS & LATCHES
 - BE OPERATED WITH A MAX. FORCE OF 5# INTERIOR, 5# EXTERIOR
 - HAVE MAX. THRESHOLD HEIGHT OF 1/2" WITH 1/4" MAX. VERTICAL RISE WITH REMAINDER BEVELED AT 2:1.
 - AT ALL SIGNS MOUNTED TO GLAZING PANEL ADJACENT TO DOOR, PROVIDE ADHESIVE BACKED VINYL STICKER DETAIL MATCHING SIGNAGE SIZE AND COLOR.
 - G# INDICATES SITE GATES. SEE SITE PLANS FOR ADDITIONAL WORK.
 - ALL DOOR VISION LITE FRAMES SHALL BE FIELD PAINTED.

WINDOW NOTES

- GLAZING LEGEND:
- SEE SPEC SECTION 08 80 00 FOR GLAZING TYPES AND FILM COATINGS.
- CLEAR GLASS
 - CLEAR GLASS WITH FROSTED FILM
 - CLEAR GLASS WITH CUSTOM PATTERN FILM
- ⑩ WINDOW SHALL BE FIXED IN CLOSED POSITION AND NON-OPERABLE.
- FOR TYPICAL INTERIOR STOREFRONT SYSTEM DETAILS, SEE 11 & 12/A8.1.
 - FOR TYPICAL EXTERIOR STOREFRONT SYSTEM DETAILS, SEE 5, 6, & 10/A8.1.
 - DIMENSIONS SHOWN ARE TO ROUGH OPENING FACE OF STUD- FIELD VERIFY ALL OVERALL ROUGH OPENING DIMENSIONS AFTER ROUGH FRAMING.
 - ALL INTERMEDIATE VERTICAL AND HORIZONTAL MULLIONS AT ALUMINUM STOREFRONT ARE PER MANUFACTURER STANDARDS- SEE SPEC. SECTION 08 43 13.
 - FOR VINYL WINDOW SYSTEM- SEE SPEC. SECTION 08 53 13.

Dry Creek Joint Elementary School District
District Education Center

8849 Cook Riolo Road, Roseville, CA 95747

Dry Creek Joint Elementary School District

FILE NO. 31-15
IDENTIFICATION STAMP DIV. OF THE
STATE ARCHITECT OFFICE OF
REGULATION SERVICES
APPLICATION NO.
02-115456
AC. TIM FLS ss
DATE 2/23/17

DIVISION OF THE STATE ARCHITECT
revision date: by:

CONSULTANT

nacht&lewis
600 Q Street, Suite 100
Sacramento, CA 95811
www.nachtandlewis.com
916.329.4000

ARCHITECT
INITIAL BOX
NO. DWG BY DATE REVIEWED
REVISIONS
NO. DESCRIPTION DATE REV
100% design development 7/6/16
75% construction documents 9/23/16
DSA submittal 12/31/16
DSA approval 02/23/17
DATE February 23, 2017
JOB NO. Y1538.00
SHEET TITLE
Opening Schedule
SHEET NO.
A6.1
SHEET OF TOTAL