

NOTE: COLORS NOT SPECIFIED HERE SHALL BE SELECTED BY ARCHITECT DURING SUBMITTAL PHASE.

LEGEND:





SW SHERWIN WILLIAMS

SW SHERWIN WILLIAMS

1. SEE SHEET A7.1.1 FOR FLOOR FINISH PATTERNS.
2. SEE DIVISION 09 SPECIFICATIONS FOR FINISH MATERIALS IDENTIFIED HEREIN.

GENERAL SHEET NOTES:

1. SEE SPEC SECTION 09 08 00 FOR CONCRETE MOISTURE MITIGATION REQUIREMENTS.
2. ALL CEILING HEIGHT DIMENSIONS NOTED ARE TAKEN FROM FINISH FLOOR UNLESS OTHERWISE NOTED. IF HEIGHT INDICATION IS "VARIES" REFER TO REFLECTED CEILING PLANS & SECTIONS.
3. ALL WAINSCOT HEIGHT DIMENSIONS ARE TAKEN FROM TOP OF BASE UNLESS OTHERWISE NOTED.
4. SEE BUILDING SECTIONS AND CASEWORK ELEVATIONS FOR MORE DETAILED INFORMATION ON LOCATIONS AND EXTENT OF PAINT, ACCENT COLORS, PLASTIC LAMINATE WALL PANELS, CERAMIC TILE, ACOUSTICAL WALL PANELS, AND OTHER FINISHES THAT MAY NOT BE SCHEDULED HEREIN.
5. UNLESS OTHERWISE NOTED, PAINT ALL EXPOSED CONDUIT, PIPING, AND NON-FACTORY FINISHED ITEMS TO MATCH ADJACENT WALL OR CEILING COLOR.
6. UNLESS OTHERWISE NOTED, PAINT ALL EXPOSED DUCTWORK GALLERY GRAY - KM4907.
7. SEE SHEET A7.1.1 FOR FLOOR FINISH PATTERNS.

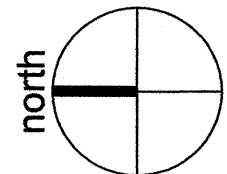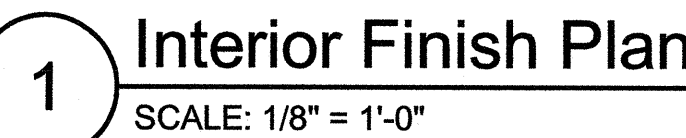


8849 Cook Riolo Road, Roseville, CA 95747

Dry Creek Joint Elementary School District

revision date: _____ by: _____

CONSULTANT

600 Q Street, Suite 100
Sacramento, CA 95811
www.nachtlewis.com
916.329.4000

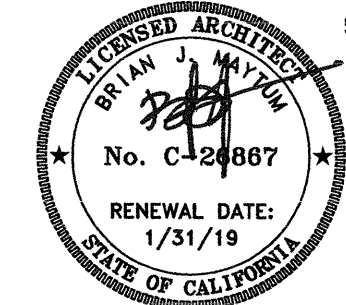

ARCHITECT

INITIAL BOX

REVISIONS

DATE February 23, 2017

JOB NO. Y1538.00

SHEET TITLE


Interior Finish Plan

SHEET NO.


A7.1

SHEET ____ OF ____ TOTAL



ONE INCH = TWENTY FEET
0 5 10 20 40 60 80
ONE-SIXTEENTH INCH = ONE FOOT
0 4 8 12 16 20 24 28 32 36 40 44 48 52 56 60 64 68 72 76 80 84 88 92 96 100
ONE-EIGHTH INCH = ONE FOOT
0 4 8 12 16 20 24 28 32 36 40 44 48 52 56 60 64 68 72 76 80 84 88 92 96 100
ONE-FOURTH INCH = ONE FOOT
0 4 8 12 16 20 24 28 32 36 40 44 48 52 56 60 64 68 72 76 80 84 88 92 96 100
ONE-HALF INCH = ONE FOOT
0 4 8 12 16 20 24 28 32 36 40 44 48 52 56 60 64 68 72 76 80 84 88 92 96 100
THREE-QUARTERS INCH = ONE FOOT
0 6 12 18 24 30 36 42 48 54 60 66 72 78 84 90 96 100
ONE AND ONE-HALF INCH = ONE FOOT
0 6 12 18 24 30 36 42 48 54 60 66 72 78 84 90 96 100

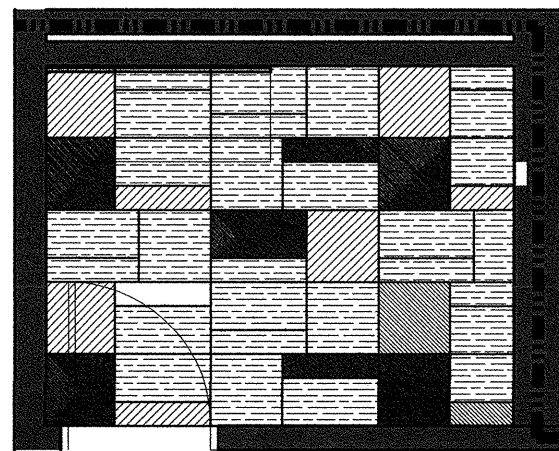


1 Restroom Floor Pattern Plan
SCALE: 1/4" = 1'-0"

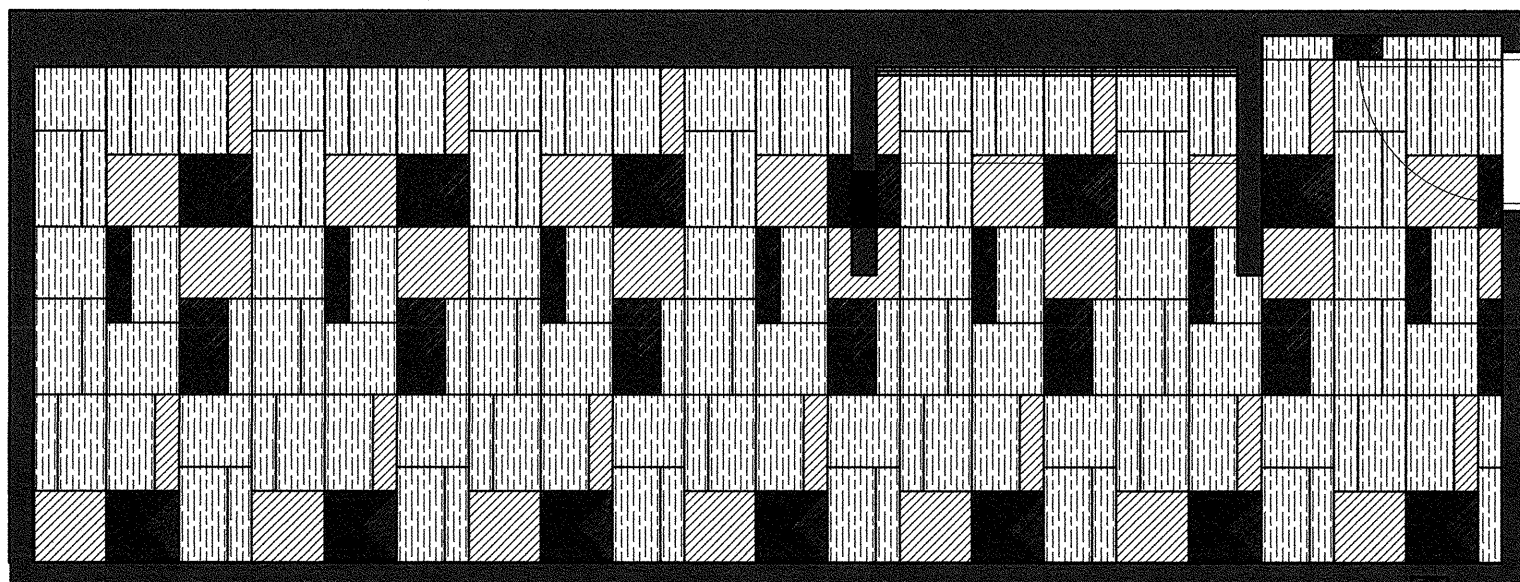

2 Restroom Floor Pattern Plan
SCALE: 1/4" = 1'-0"

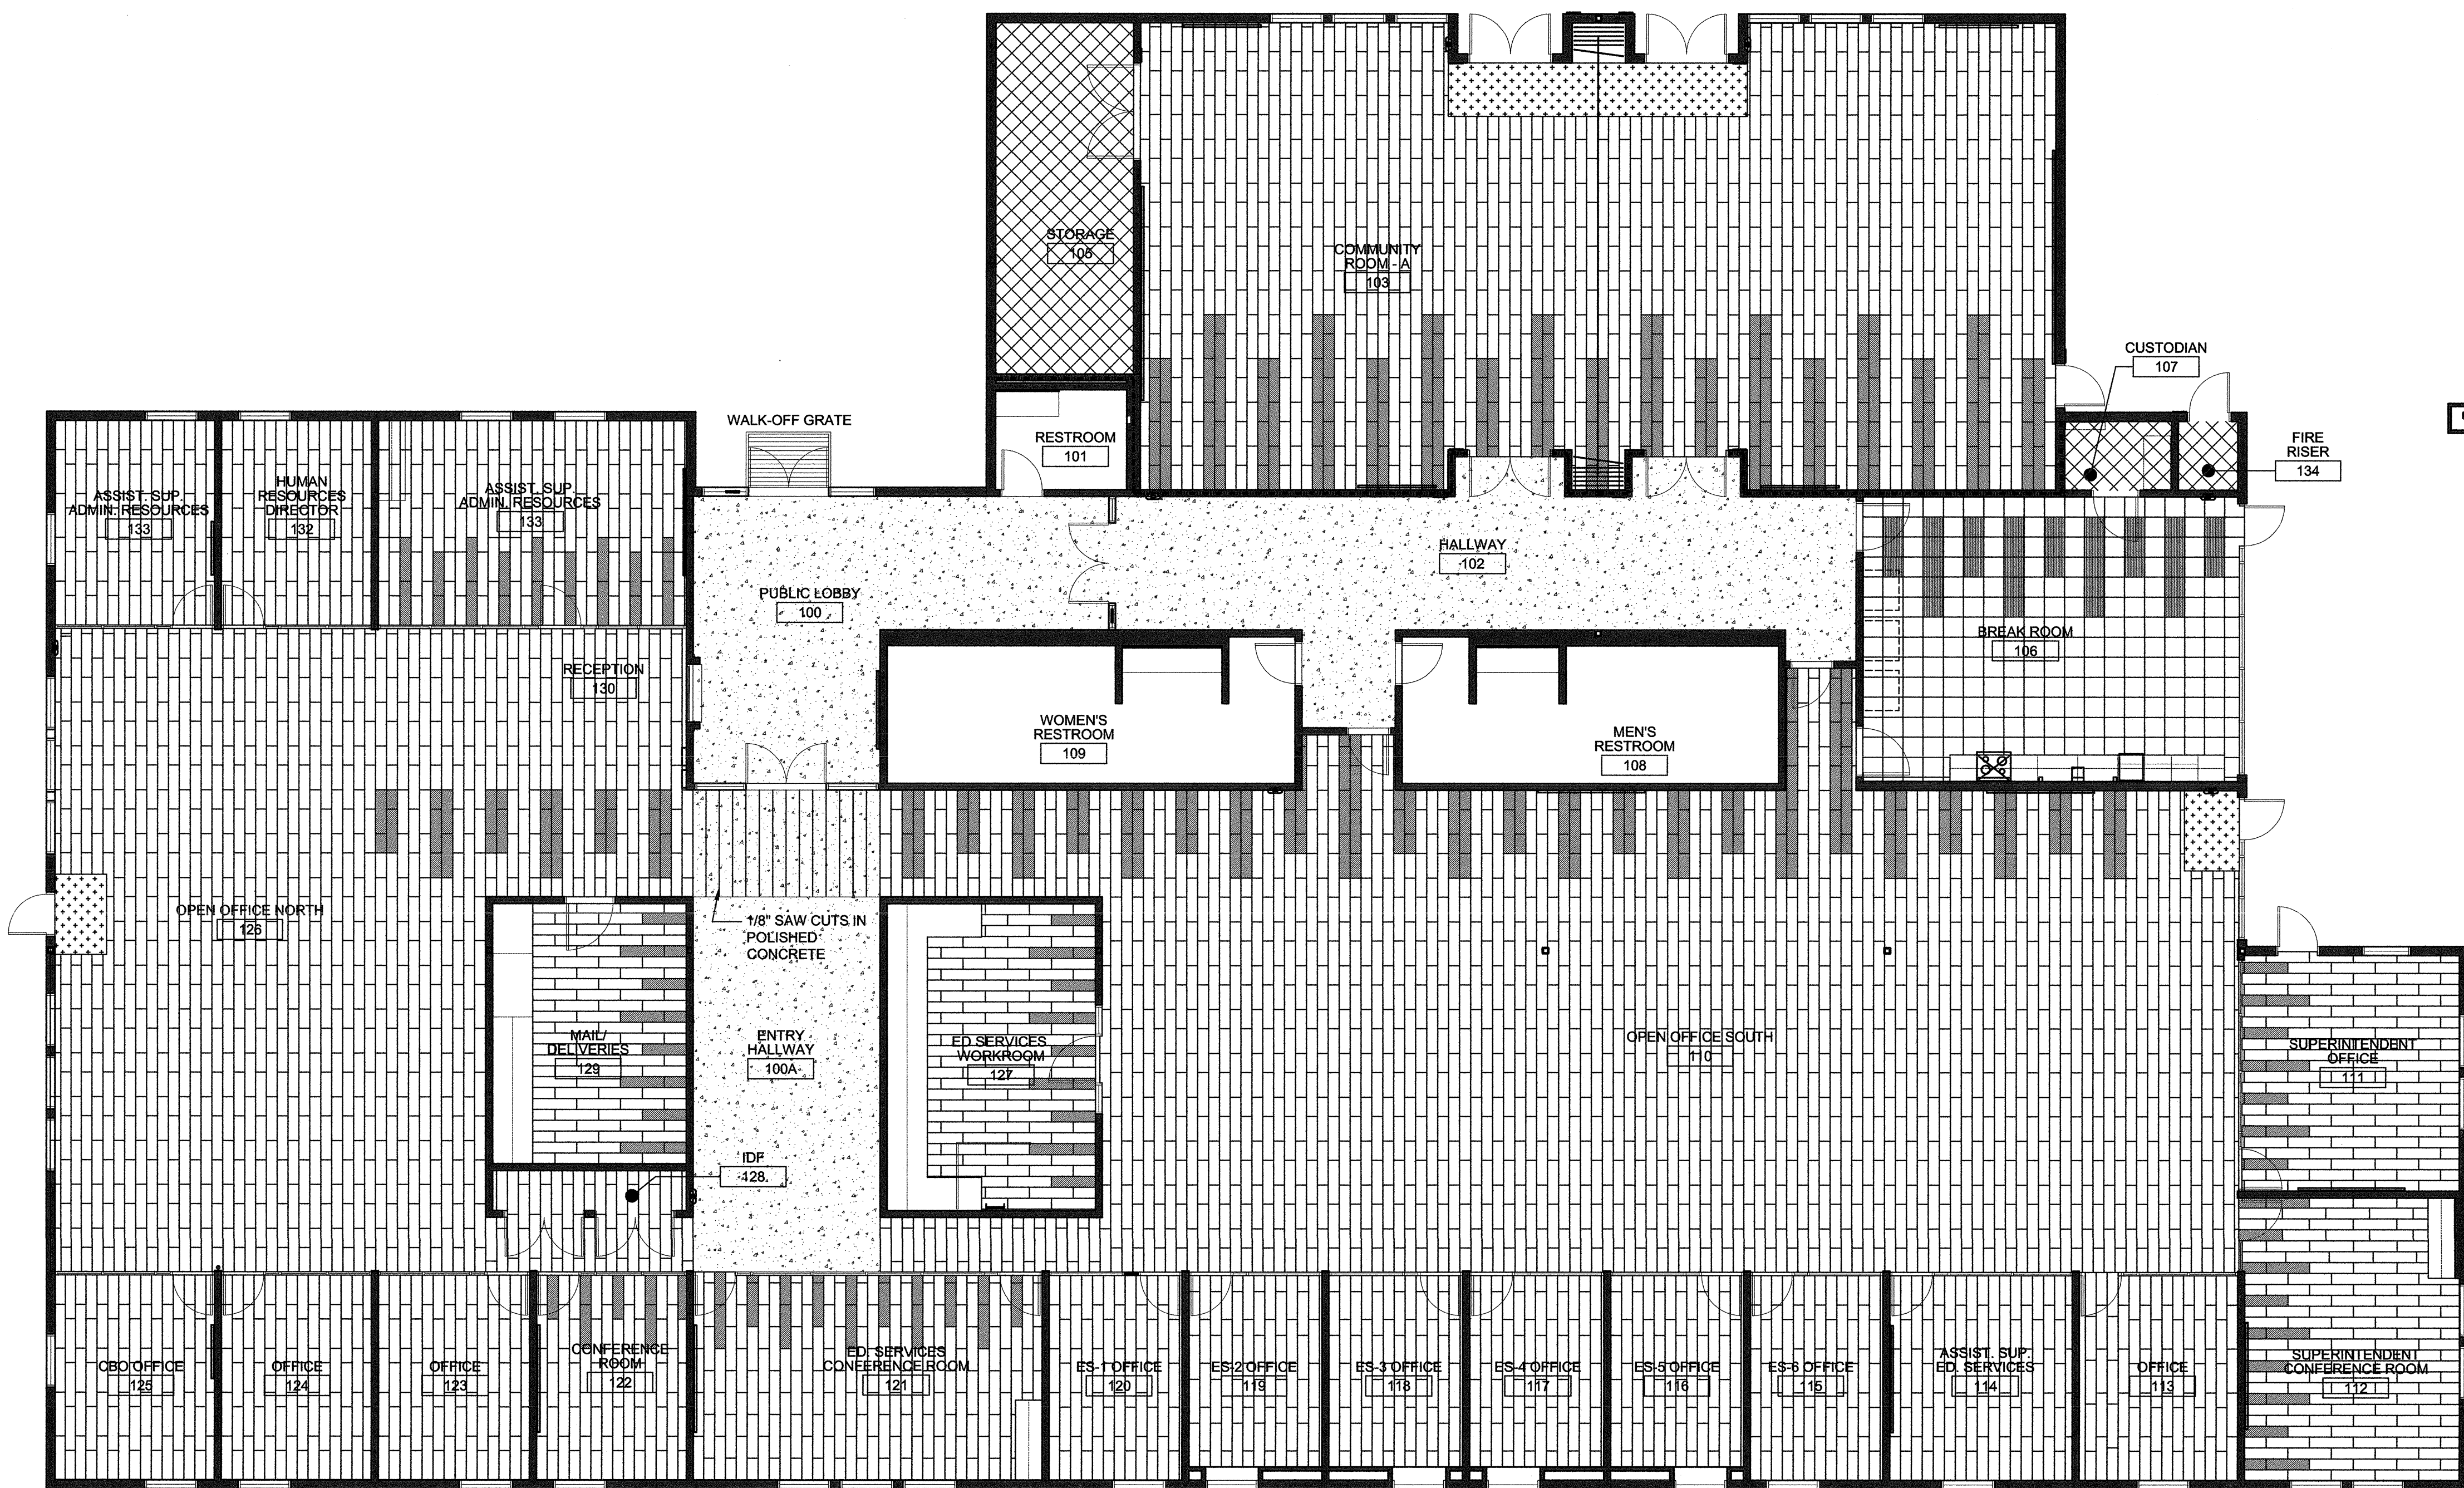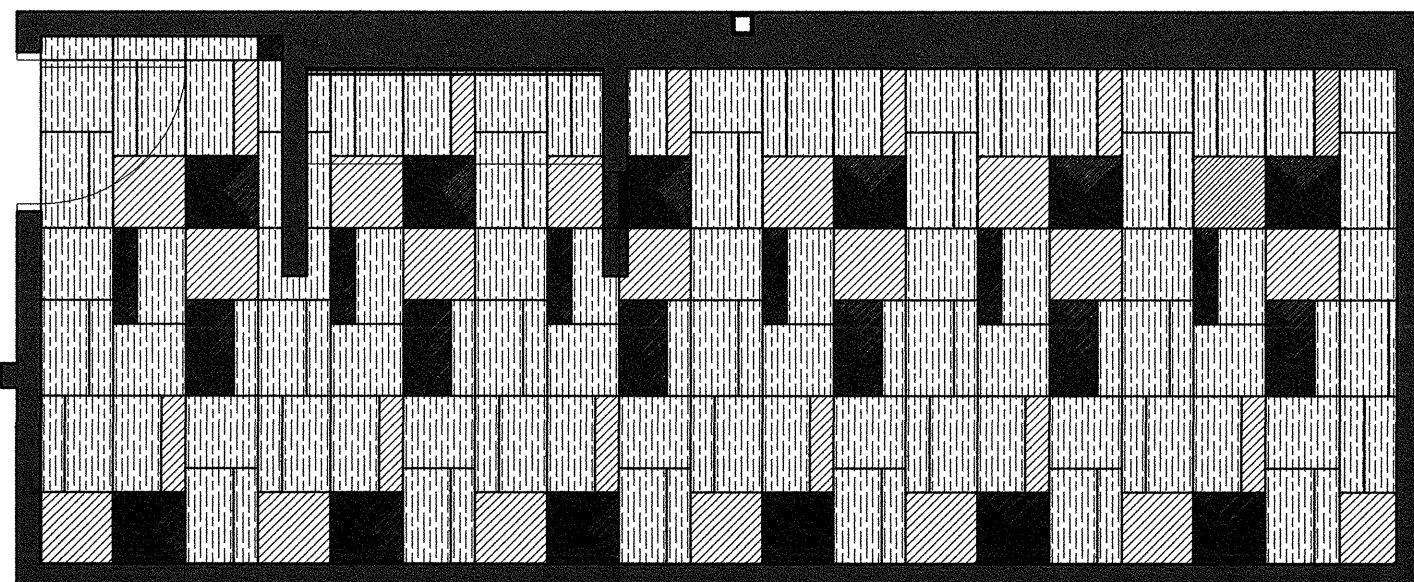

3 Finish Plan
SCALE: 1/8" = 1'-0"

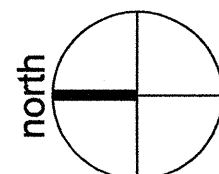

- GENERAL SHEET NOTES:
- SEE SPEC SECTION 09 68 00 FOR CONCRETE MOISTURE MITIGATION REQUIREMENTS.
 - ALL CEILING HEIGHT DIMENSIONS NOTED ARE TAKEN FROM FINISH FLOOR UNLESS OTHERWISE NOTED. IF HEIGHT INDICATION IS "VARIES" REFER TO REFLECTED CEILING PLANS & SECTIONS.
 - ALL WAINSCOT HEIGHT DIMENSIONS ARE TAKEN FROM TOP OF BASE UNLESS OTHERWISE NOTED.
 - SEE BUILDING SECTIONS AND CASEWORK ELEVATIONS FOR MORE DETAILED INFORMATION ON LOCATIONS AND EXTENT OF PAINT, ACCENT COLORS, PLASTIC LAMINATE WALL PANELS, ACOUSTICAL WALL PANELS, ETC. THAT MAY NOT BE SCHEDULED HEREIN.
 - UNLESS OTHERWISE NOTED, PAINT ALL EXPOSED CONDUIT, PIPING, AND NON-FACTORY FINISHED ITEMS TO MATCH ADJACENT WALL OR CEILING COLOR.
 - UNLESS OTHERWISE NOTED, PAINT ALL EXPOSED DUCTWORK TO MATCH ADJACENT WALL OR CEILING COLOR.
 - SEE SHEET A7.1 FOR ADDITIONAL FINISH INFORMATION.
 - SEE DIVISION 09 SPECIFICATIONS FOR FINISH MATERIALS IDENTIFIED HEREIN.

FLOOR FINISHES

	INTERFACE CARPET - VERTICALS - MERIDIAN 104010
	INTERFACE ACCENT CARPET - ON LINE - OCEAN
	INTERFACE WALK OFF MAT - SUPERFLOR - OCEANUS
	POLISHED CONCRETE - SEE SPEC SECTION 03 35 43.
	HARD TROWELED CONCRETE
	SHEET LINOLEUM - ARMSTRONG FORBO - ROSATO 3120
	SHEET LINOLEUM - ARMSTRONG FORBO - RUST 2767
	PORCELAIN TILE - SANTINI - GRIGIO SN08
	PORCELAIN TILE - INVOKE - MYSTIC WAY ID02
	PORCELAIN TILE - INVOKE - COPPER HAZE ID03


Dry Creek Joint Elementary School District
District Education Center
8849 Cook Riolo Road, Roseville, CA 95747
Dry Creek Joint Elementary School District

FILE NO. 31-15
IDENTIFICATION STAMP DIV. OF THE
STATE ARCHITECT OFFICE OF
REGULATION SERVICES
APPLICATION NO.
02-115456
AC. TM. FLS. R. SS. *SS*
DATE *1/31/19* *CE*

DIVISION OF THE STATE ARCHITECT
revision date: _____ by: _____

CONSULTANT

nacht&lewis
600 Q Street, Suite 100
Sacramento, CA 95811
www.nachtandlewis.com
916.329.4000

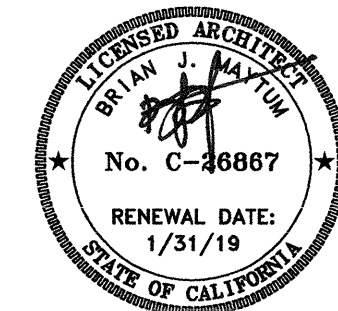

ARCHITECT

INITIAL BOX

NO.	DWG BY	DATE	REVIEWED

REVISIONS

NO.	DESCRIPTION	DATE	REV
1	100% design development	7/6/16	
2	75% construction documents	9/20/16	
3	DSA submittal	12/31/16	
4	DSA approval	02/23/17	

DATE February 23, 2017
JOB NO. Y1538.00
SHEET TITLE























Floor Pattern
Finish Plan

SHEET NO.

A7.1.1

SHEET ____ OF ____ TOTAL

ONE AND ONE-HALF INCH = ONE FOOT
ONE INCH = ONE FOOT
THREE-QUARTERS INCH = ONE FOOT
ONE-HALF INCH = ONE FOOT
ONE-QUARTER INCH = ONE FOOT
ONE-EIGHTH INCH = ONE FOOT
ONE-SIXTEENTH INCH = ONE FOOT
ONE INCH = TWENTY FEET

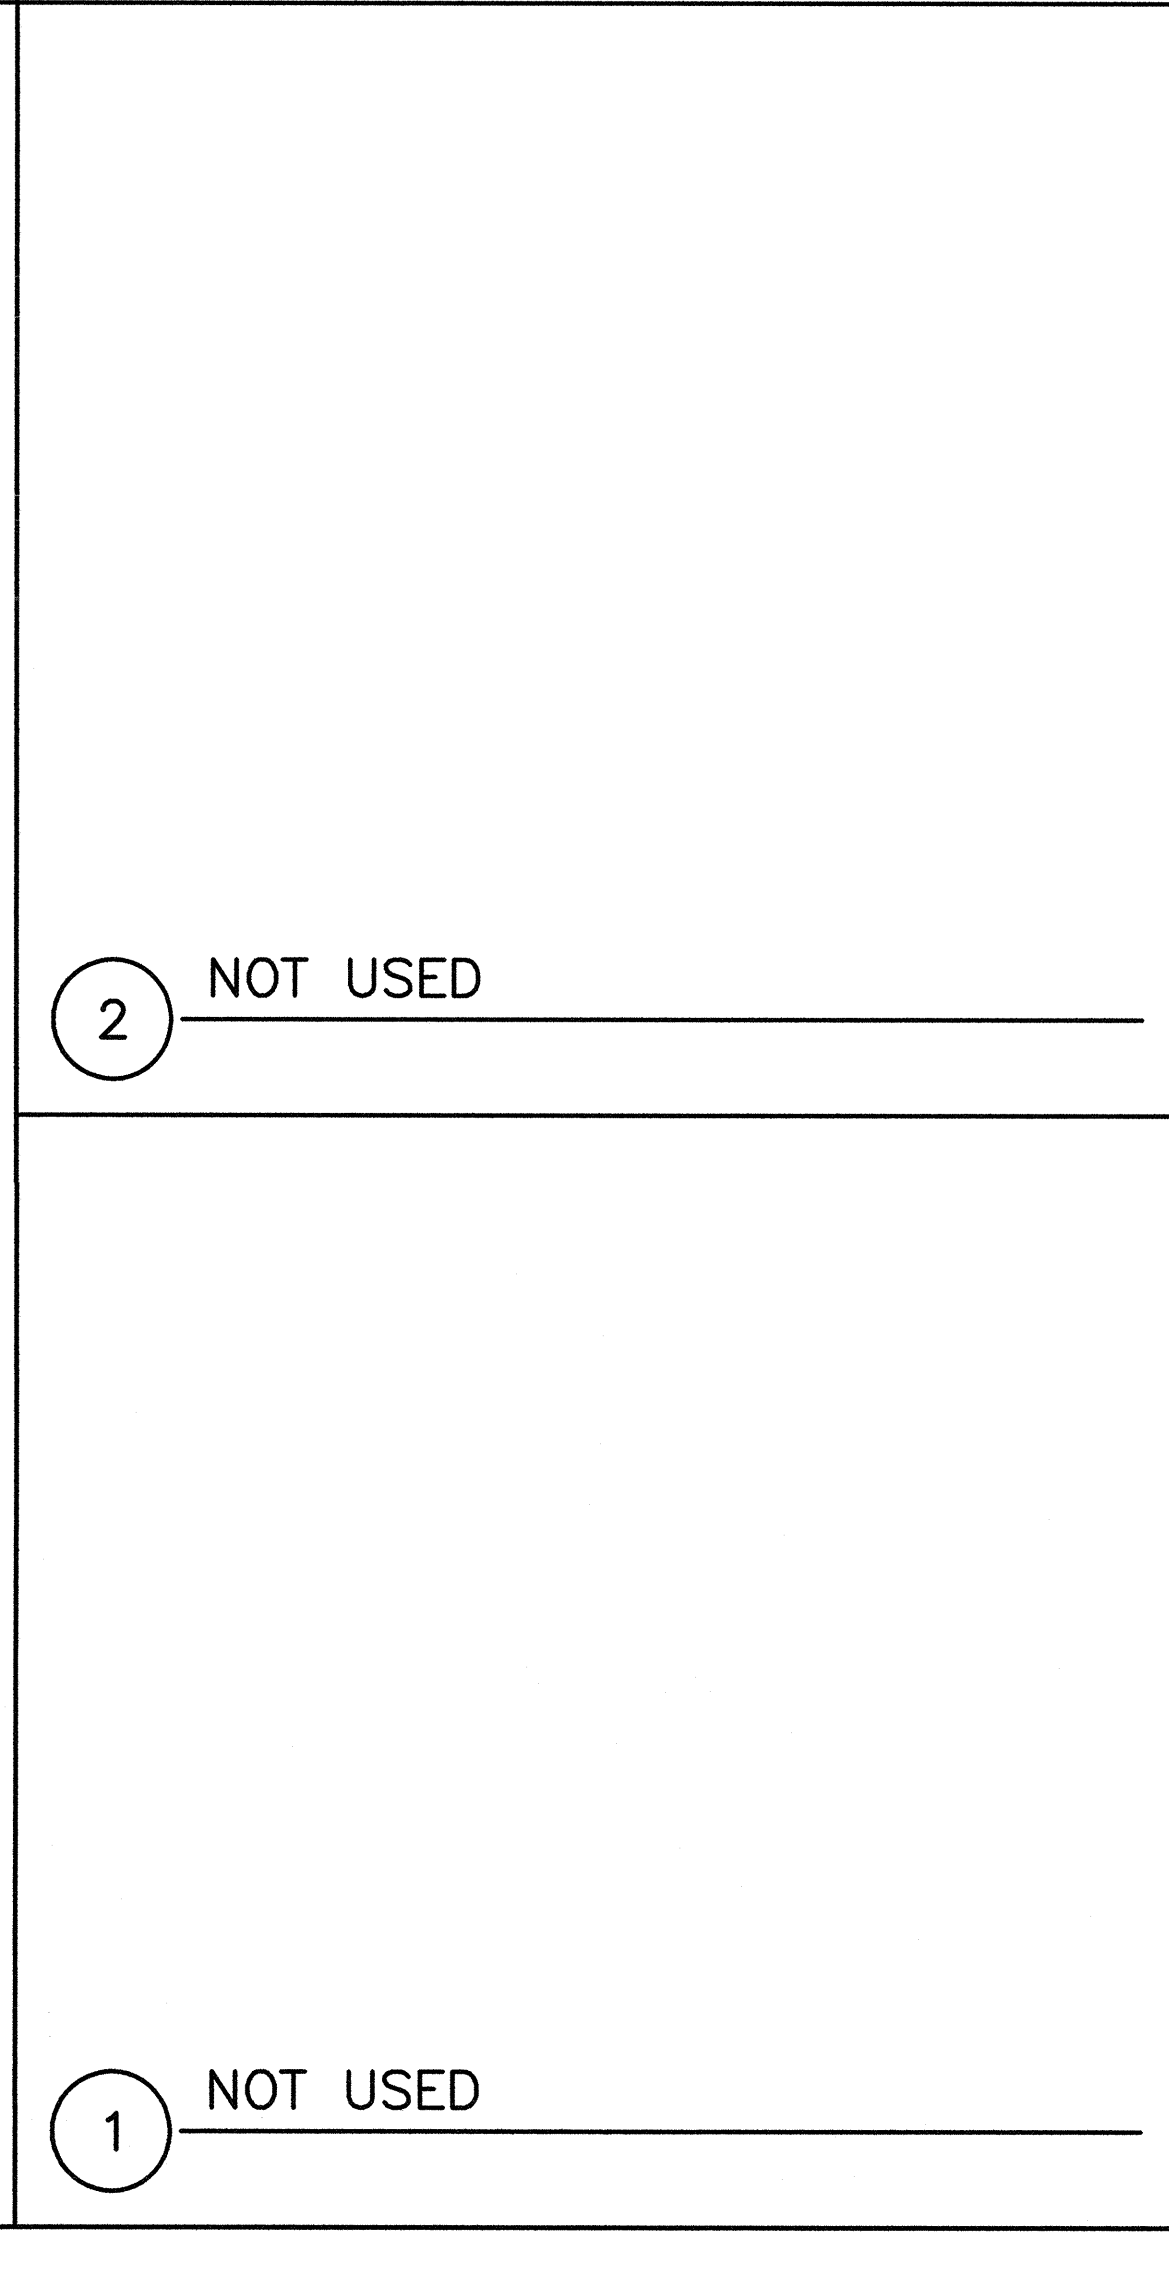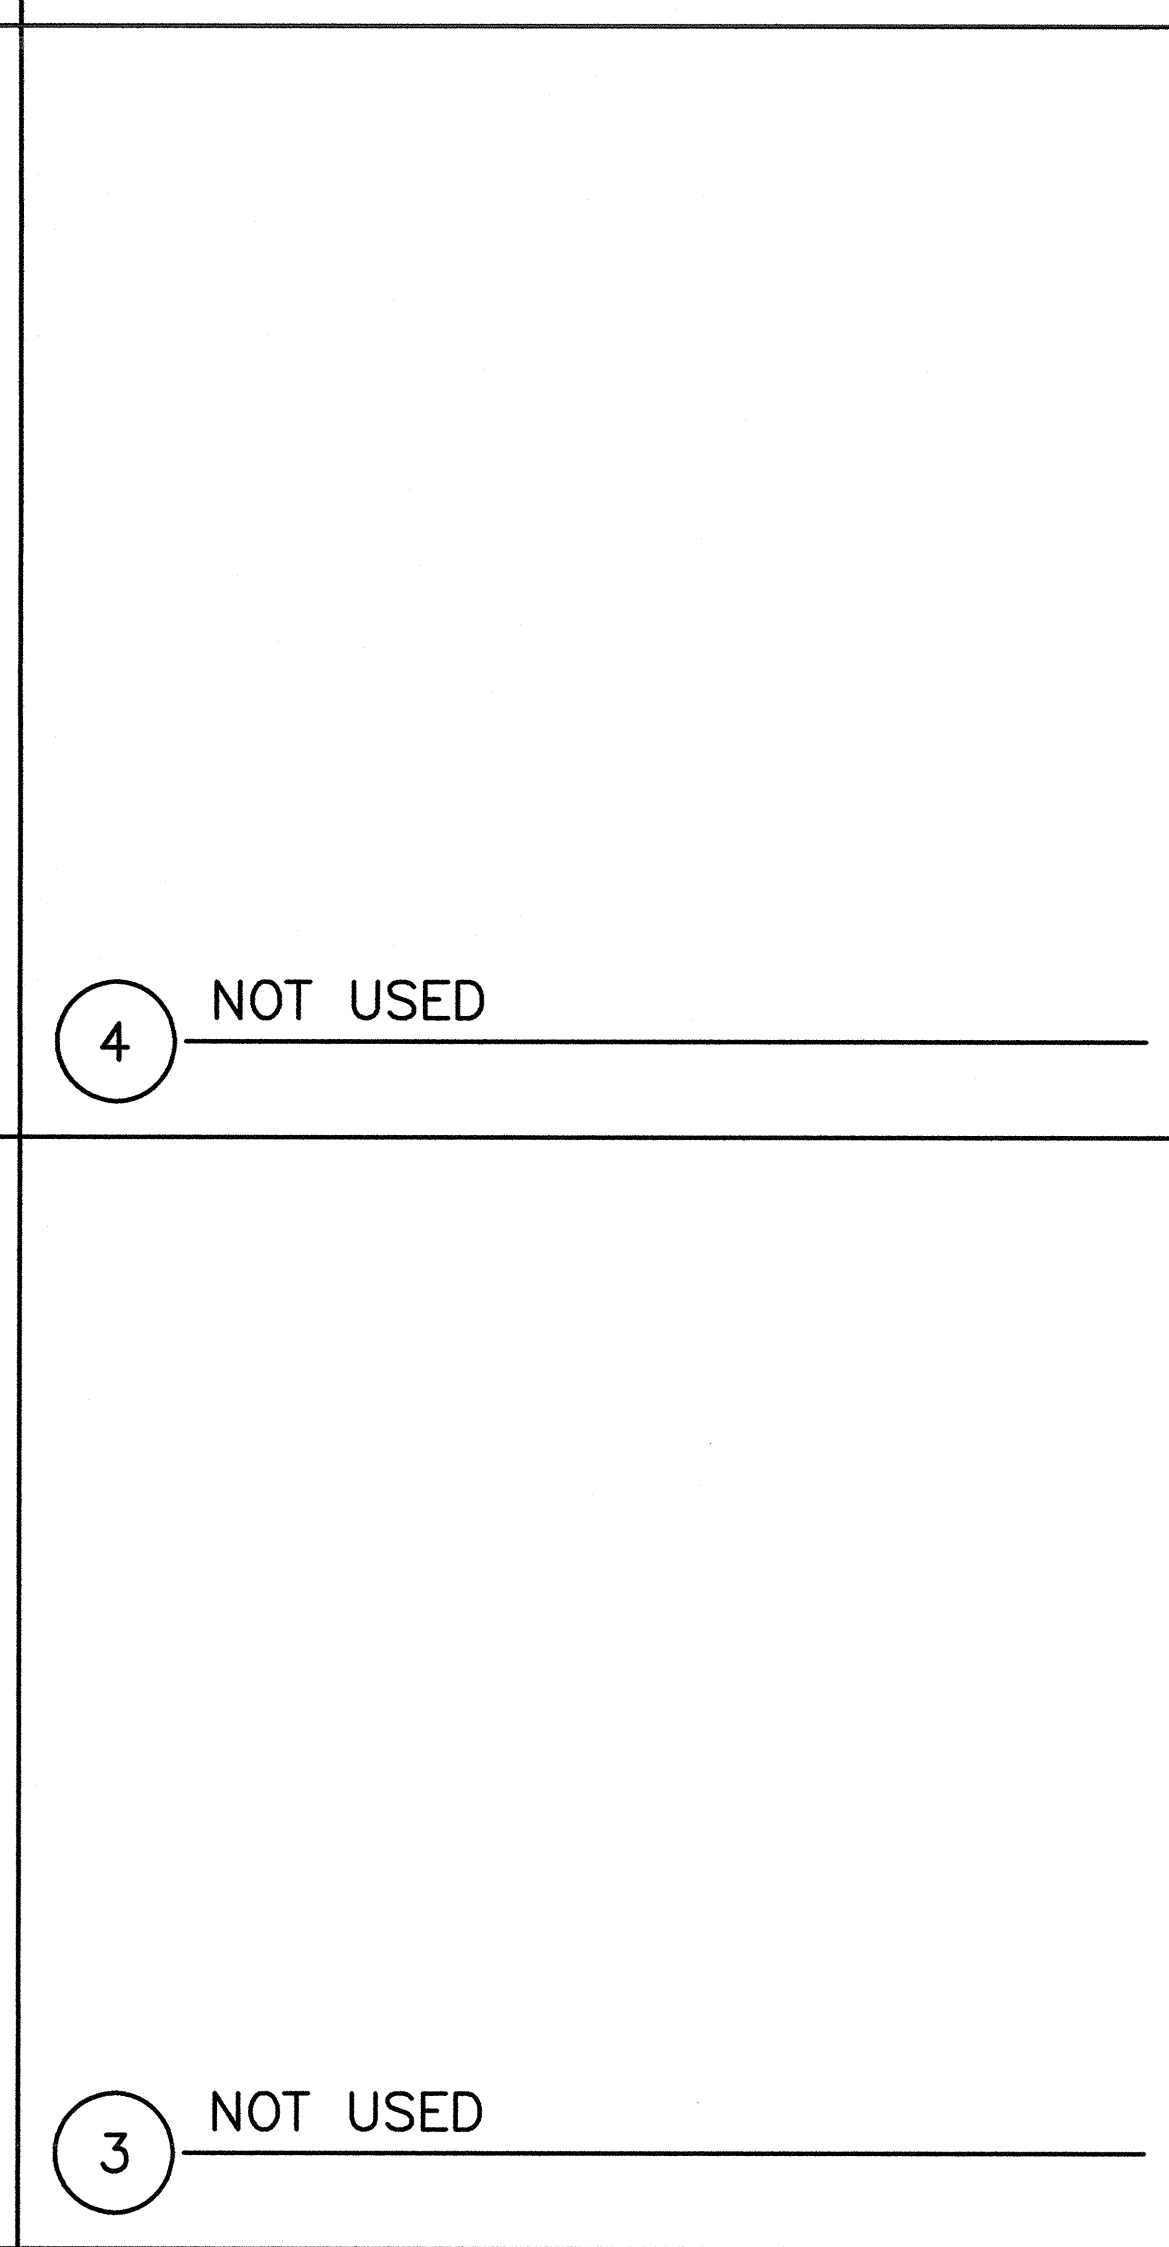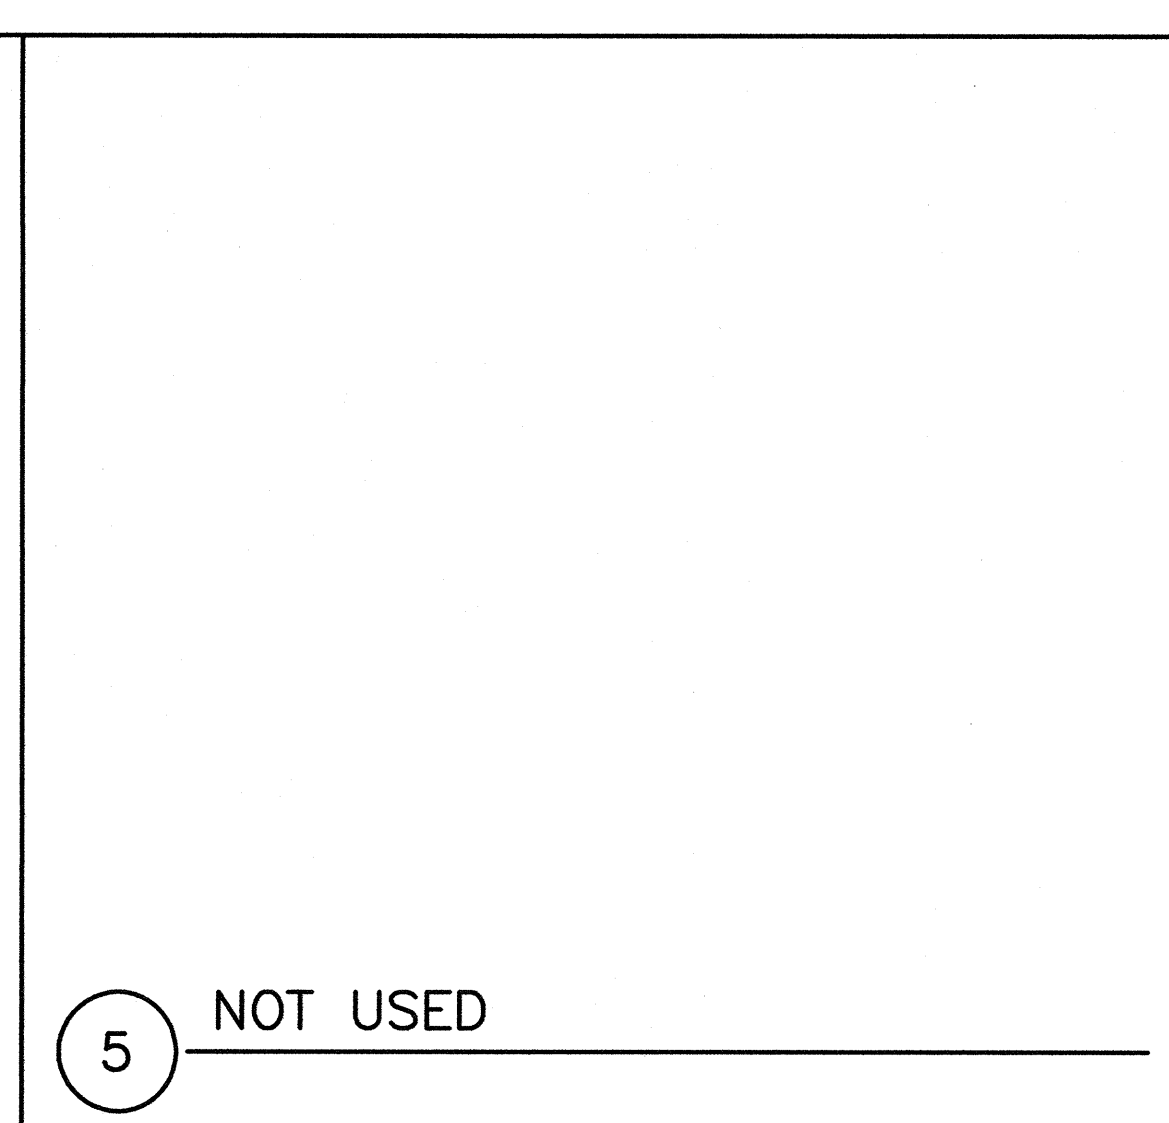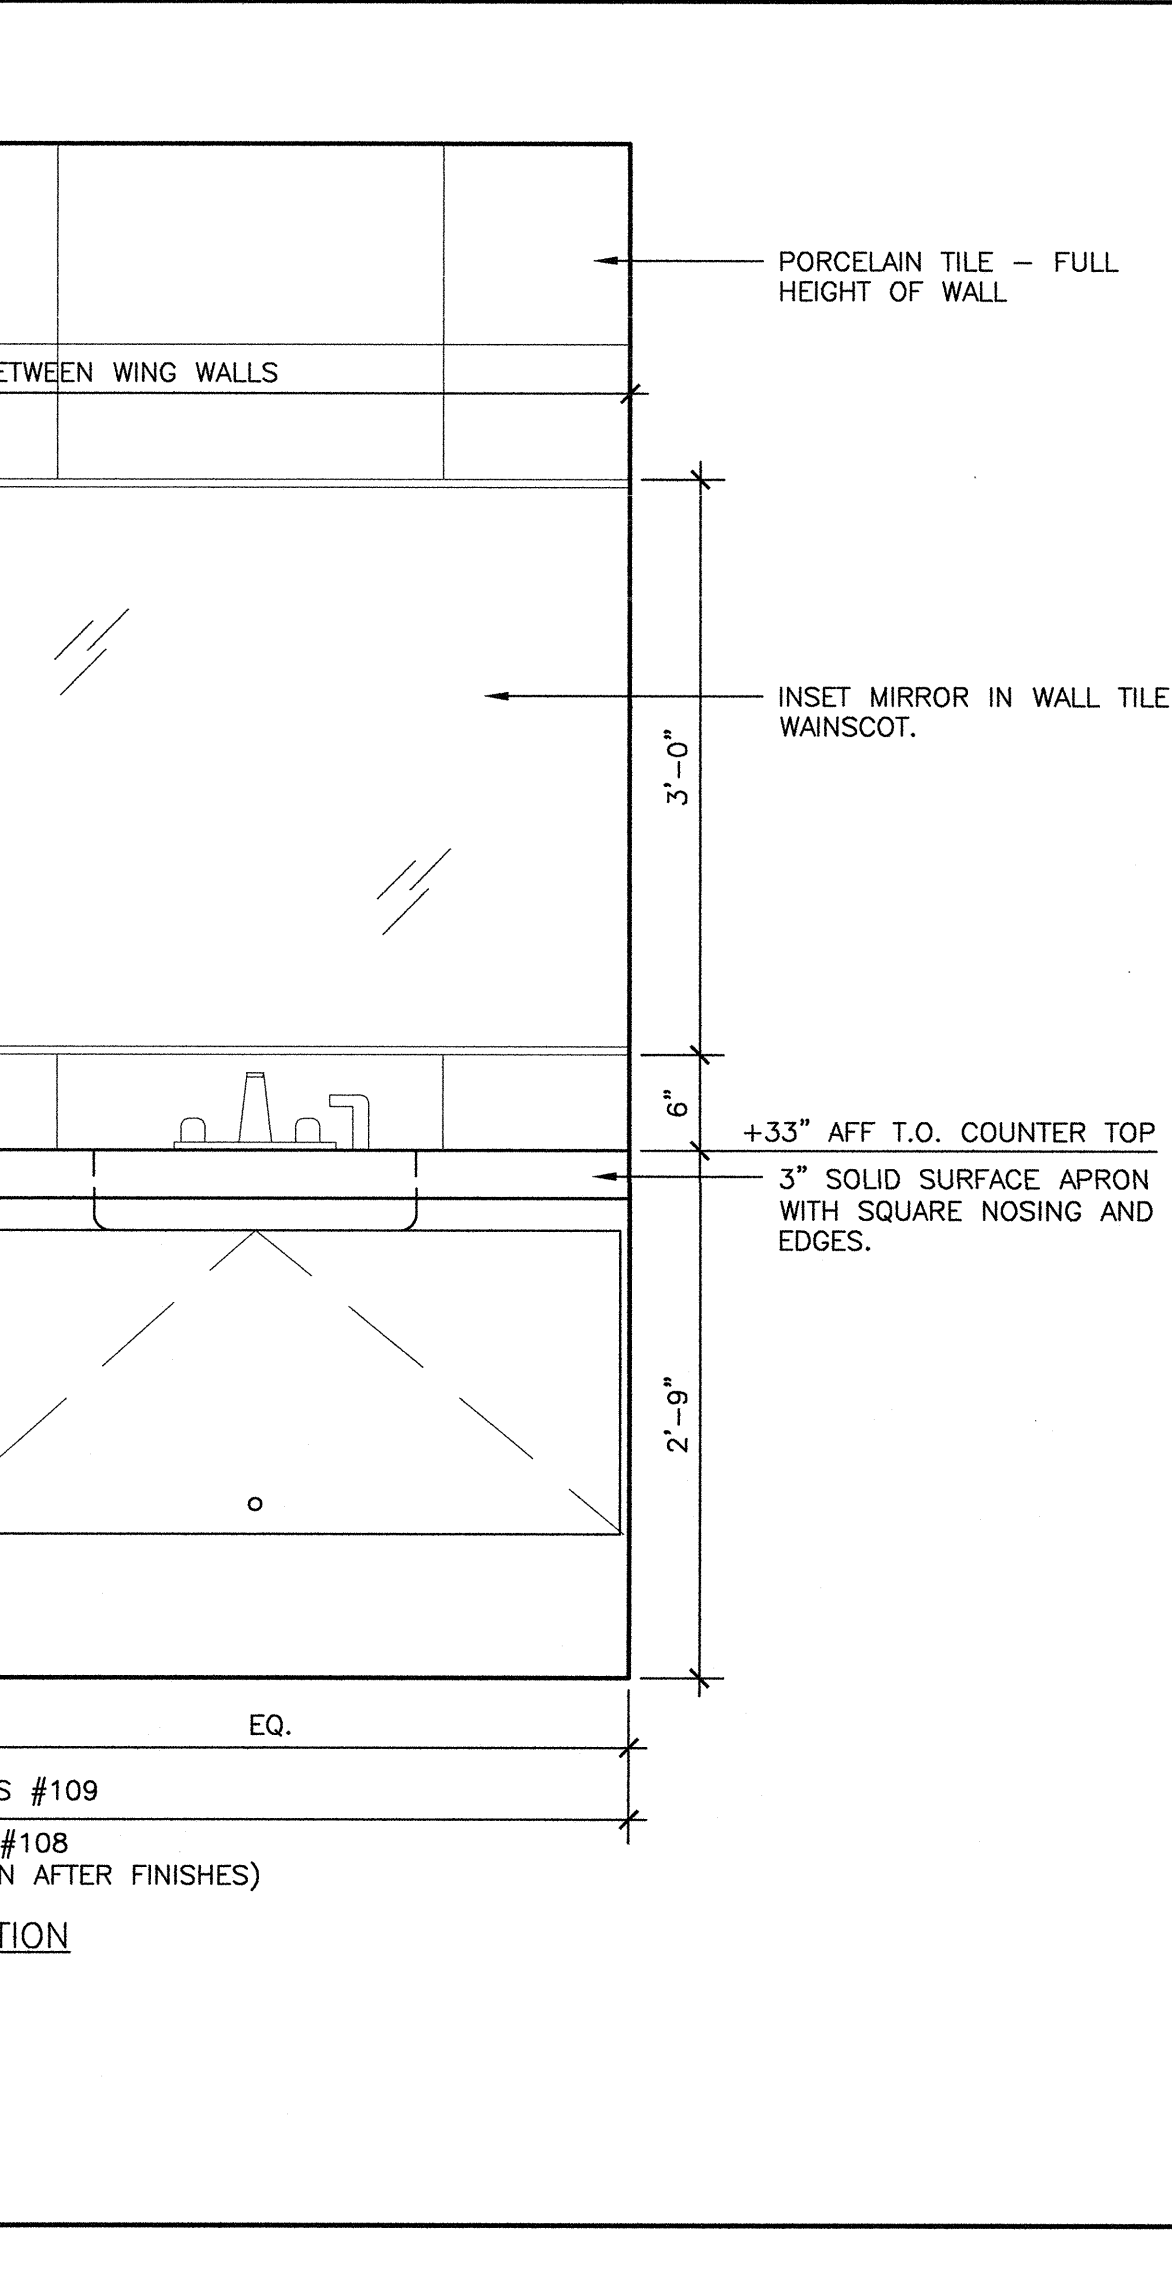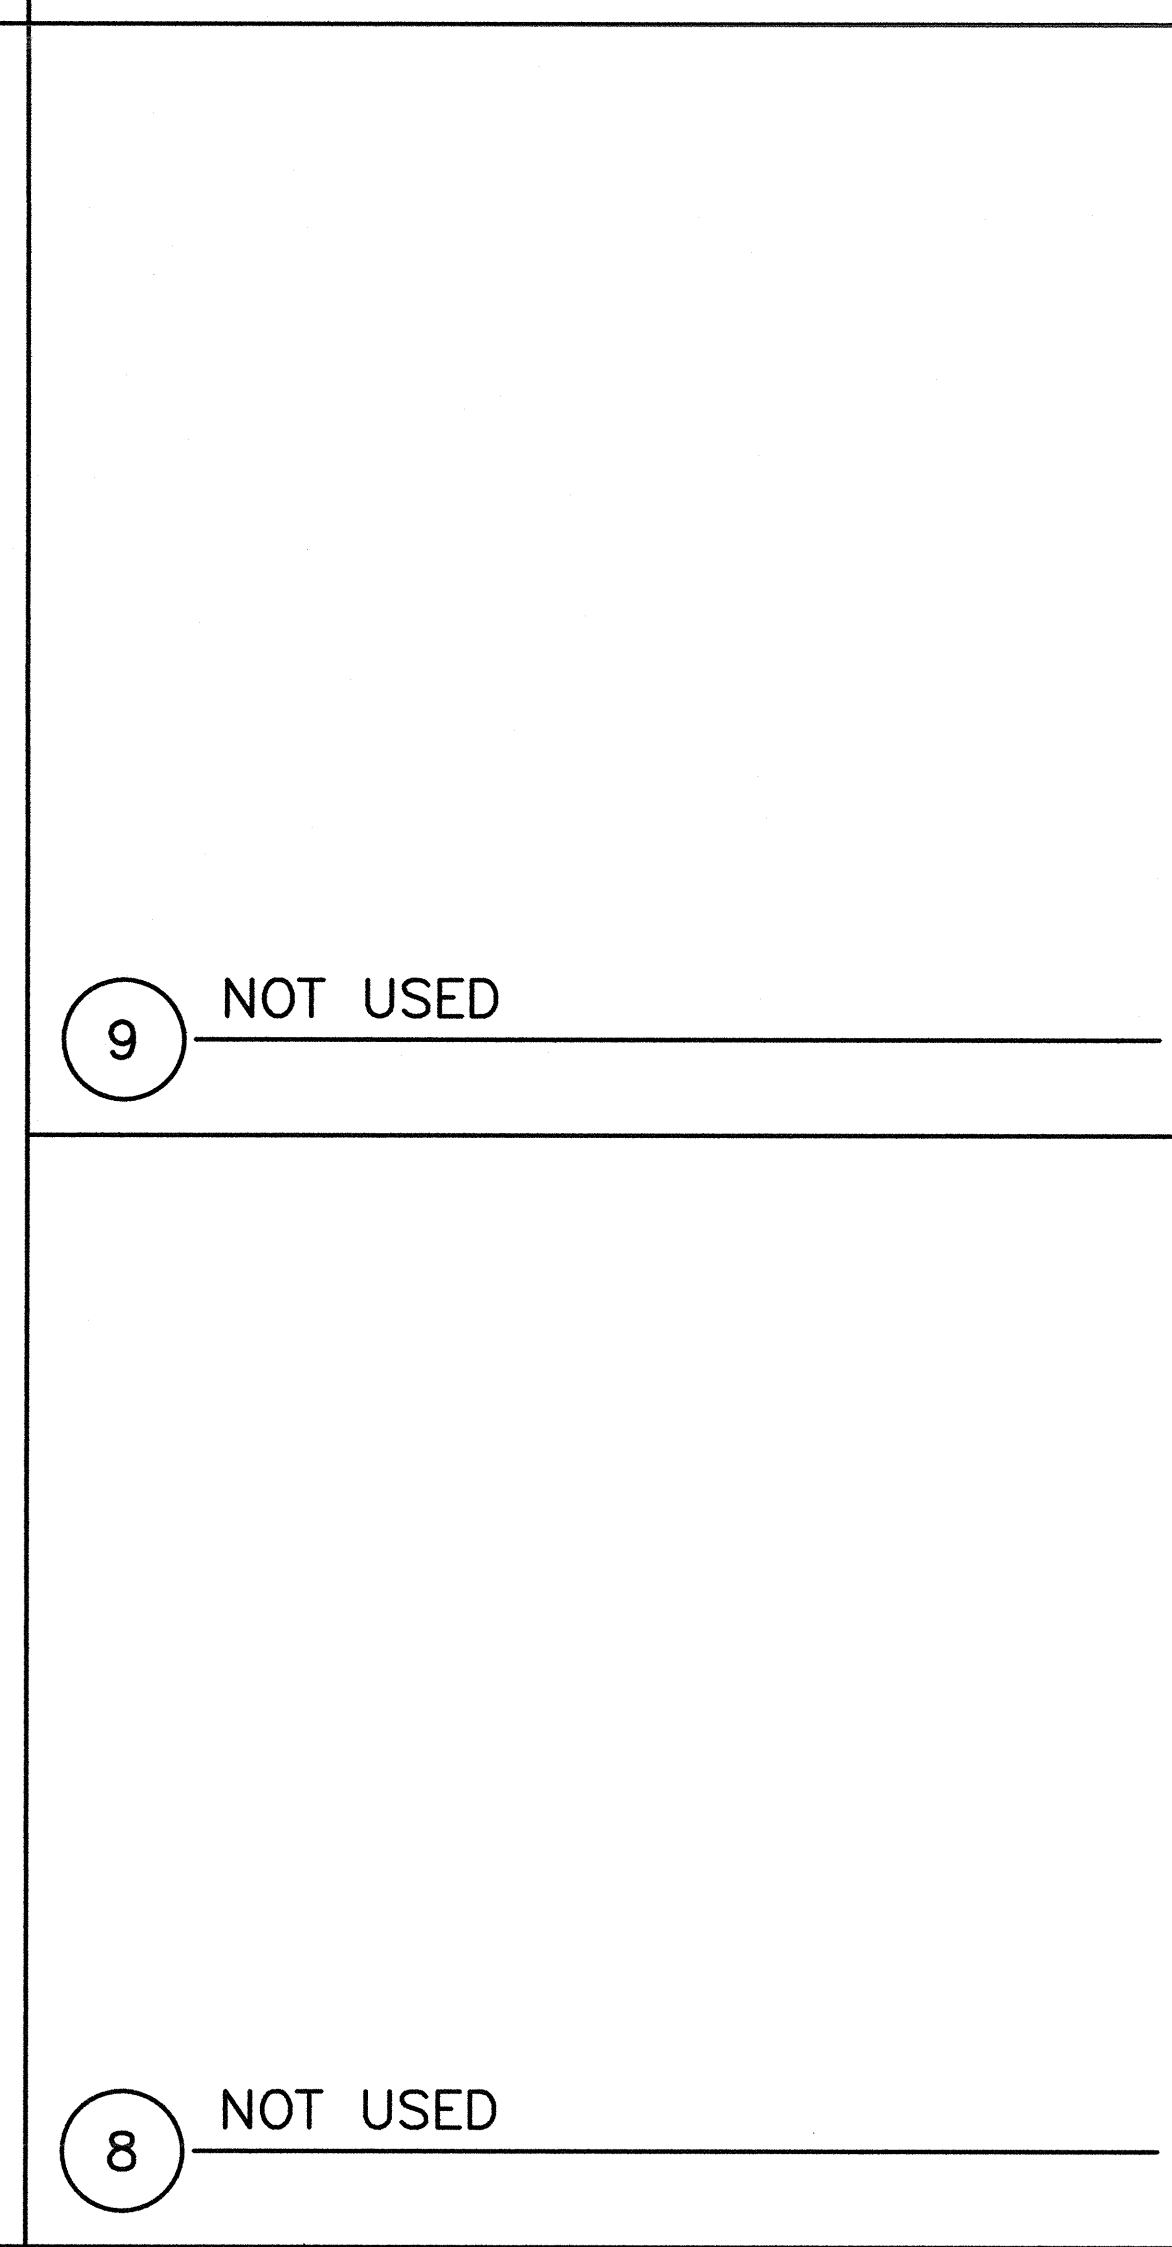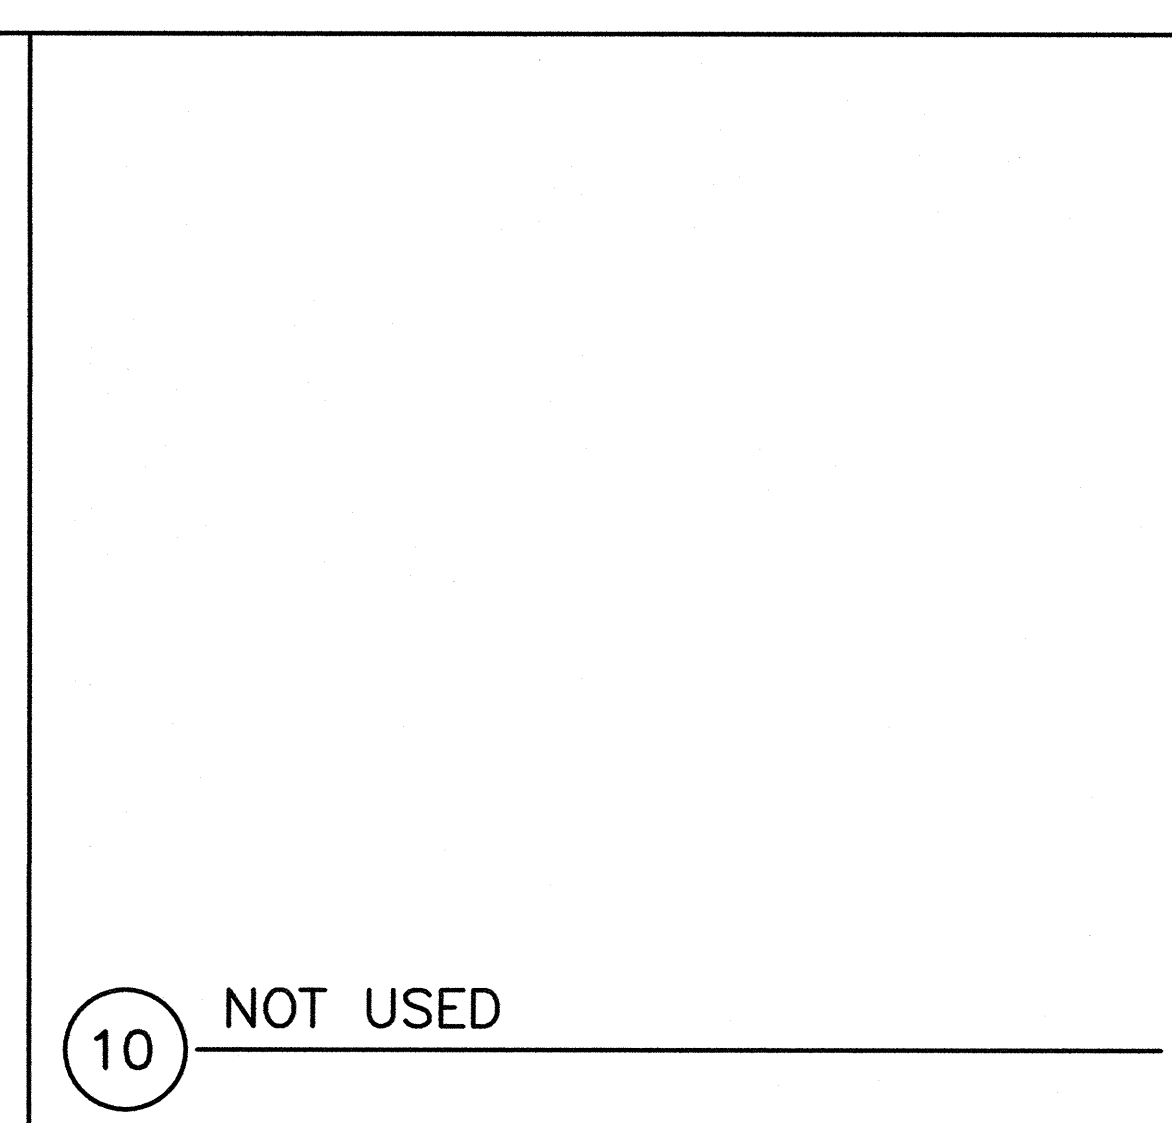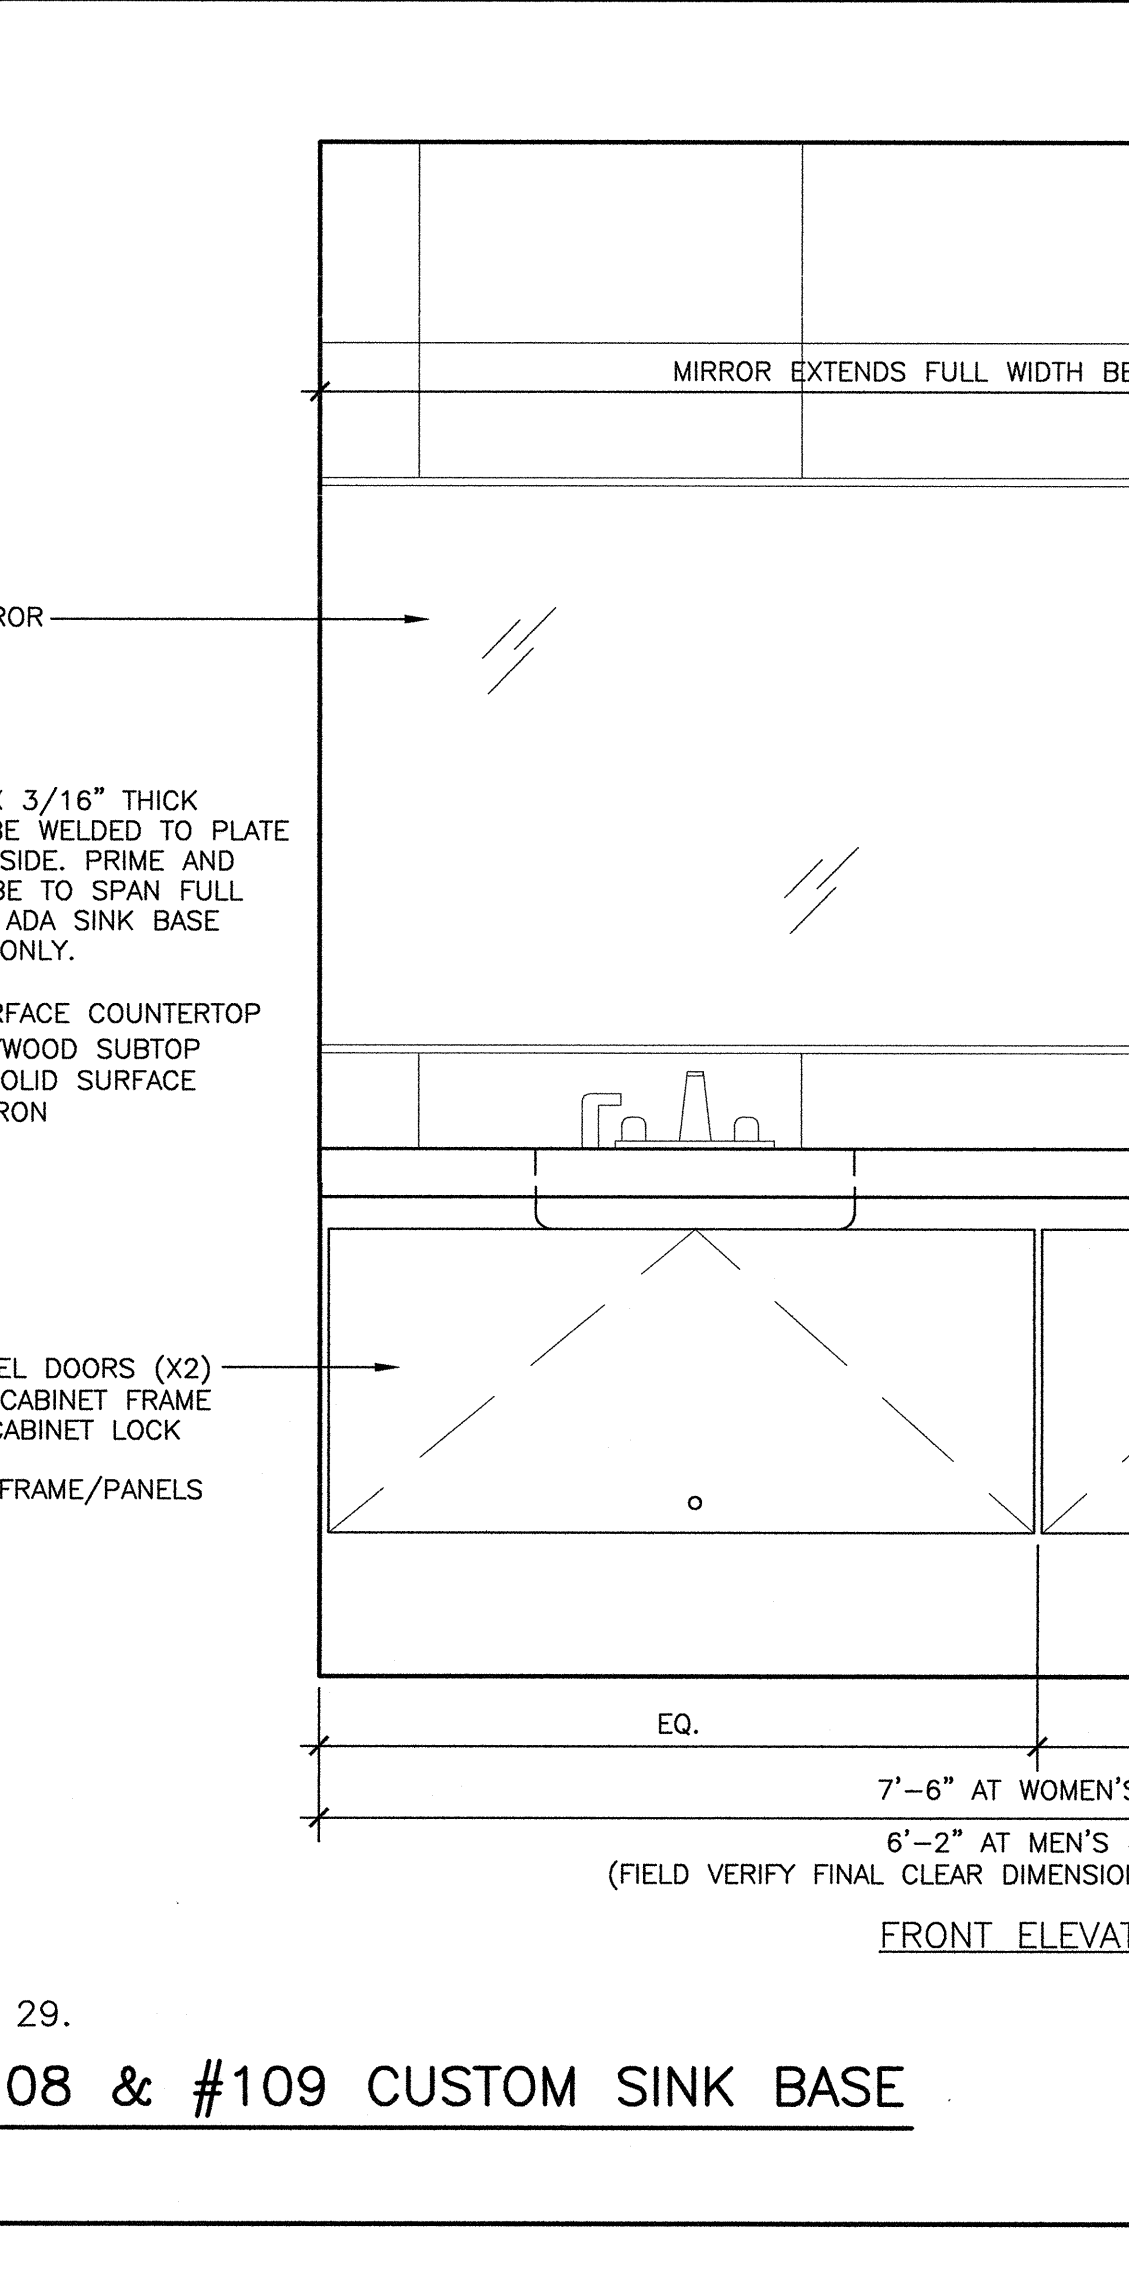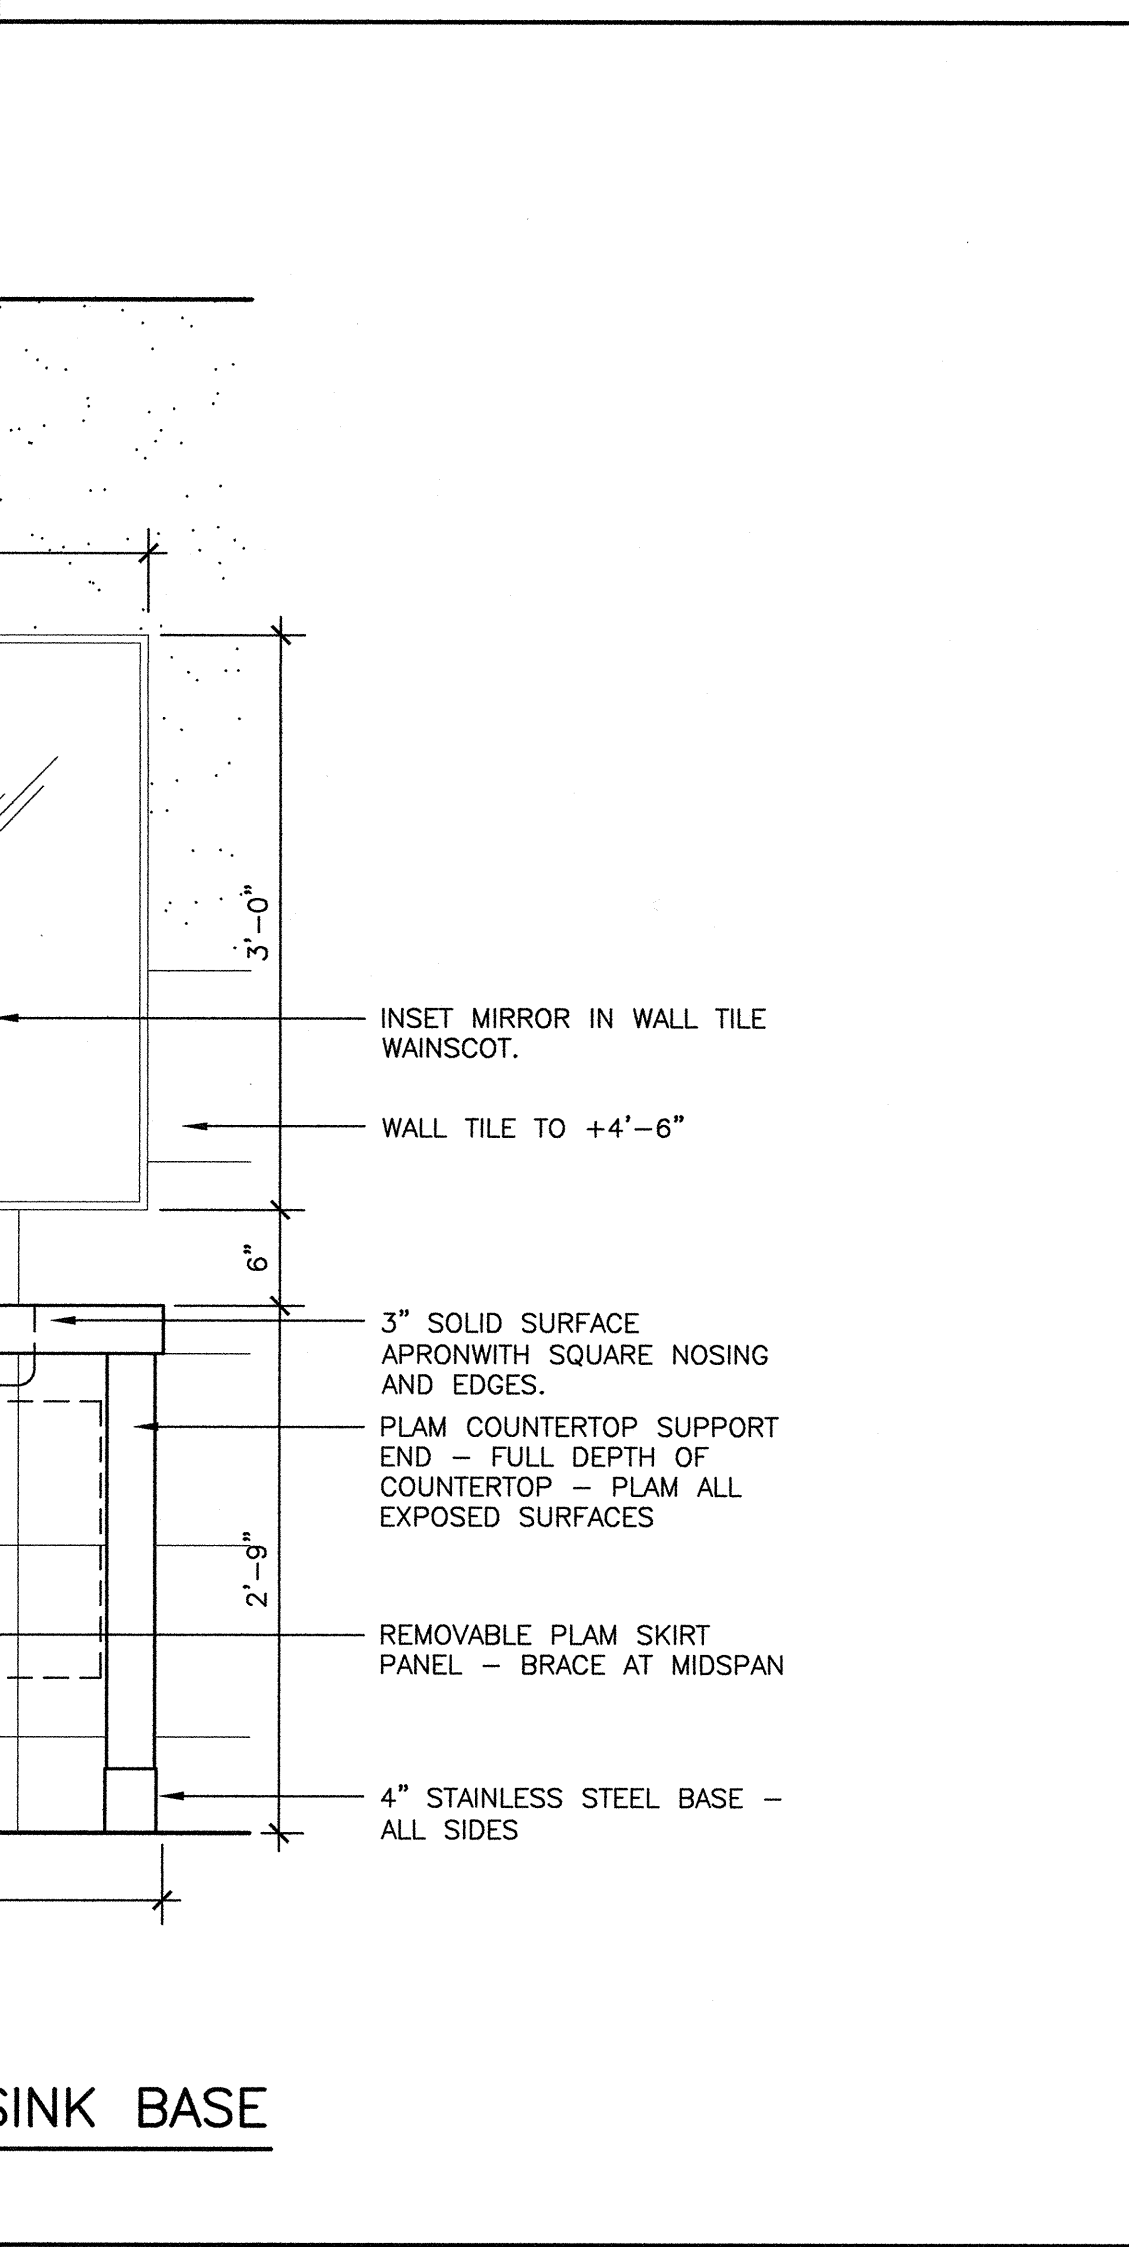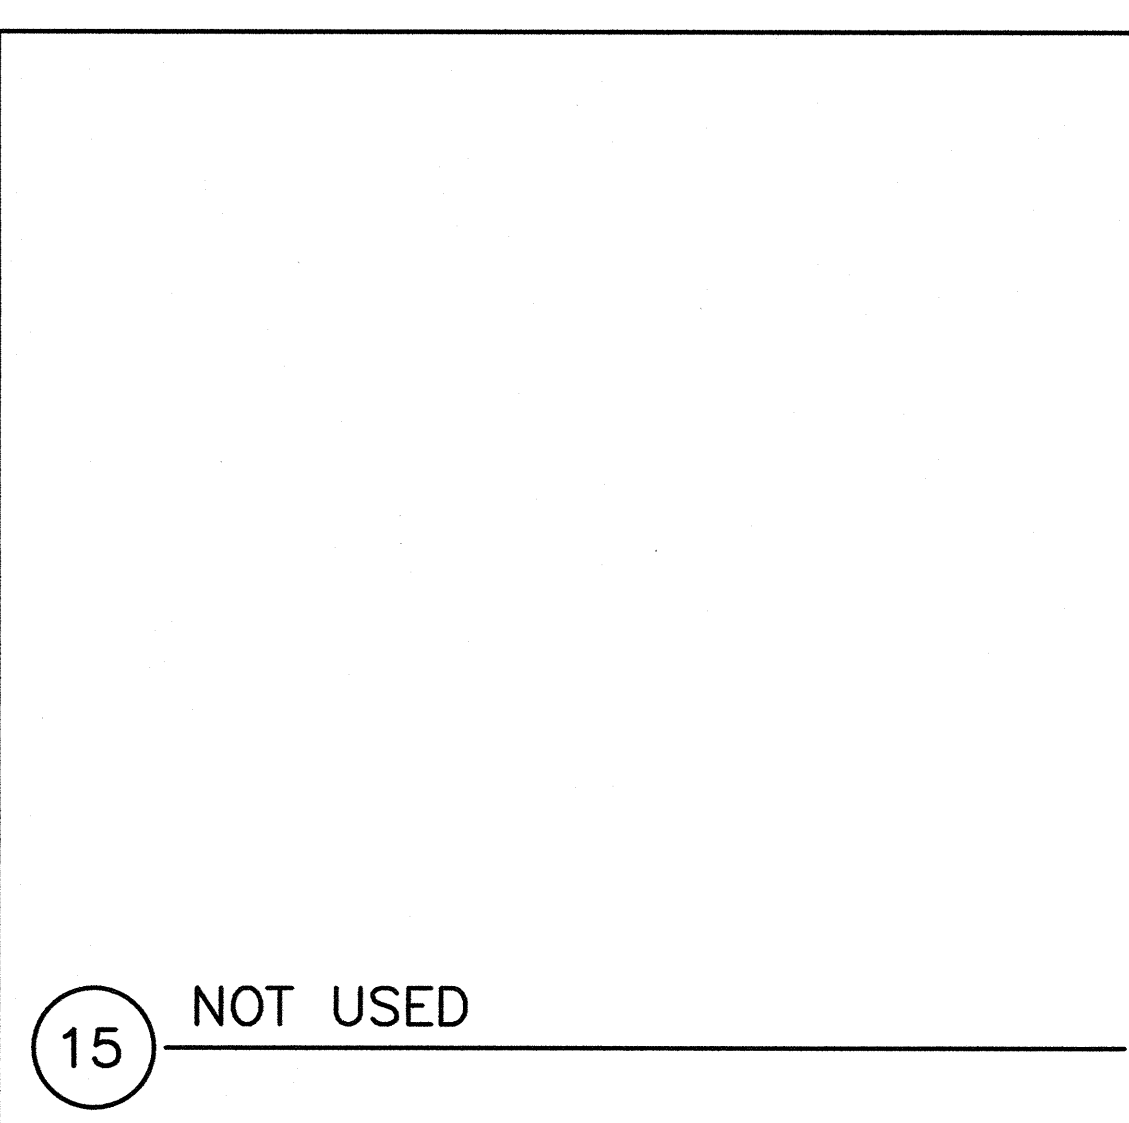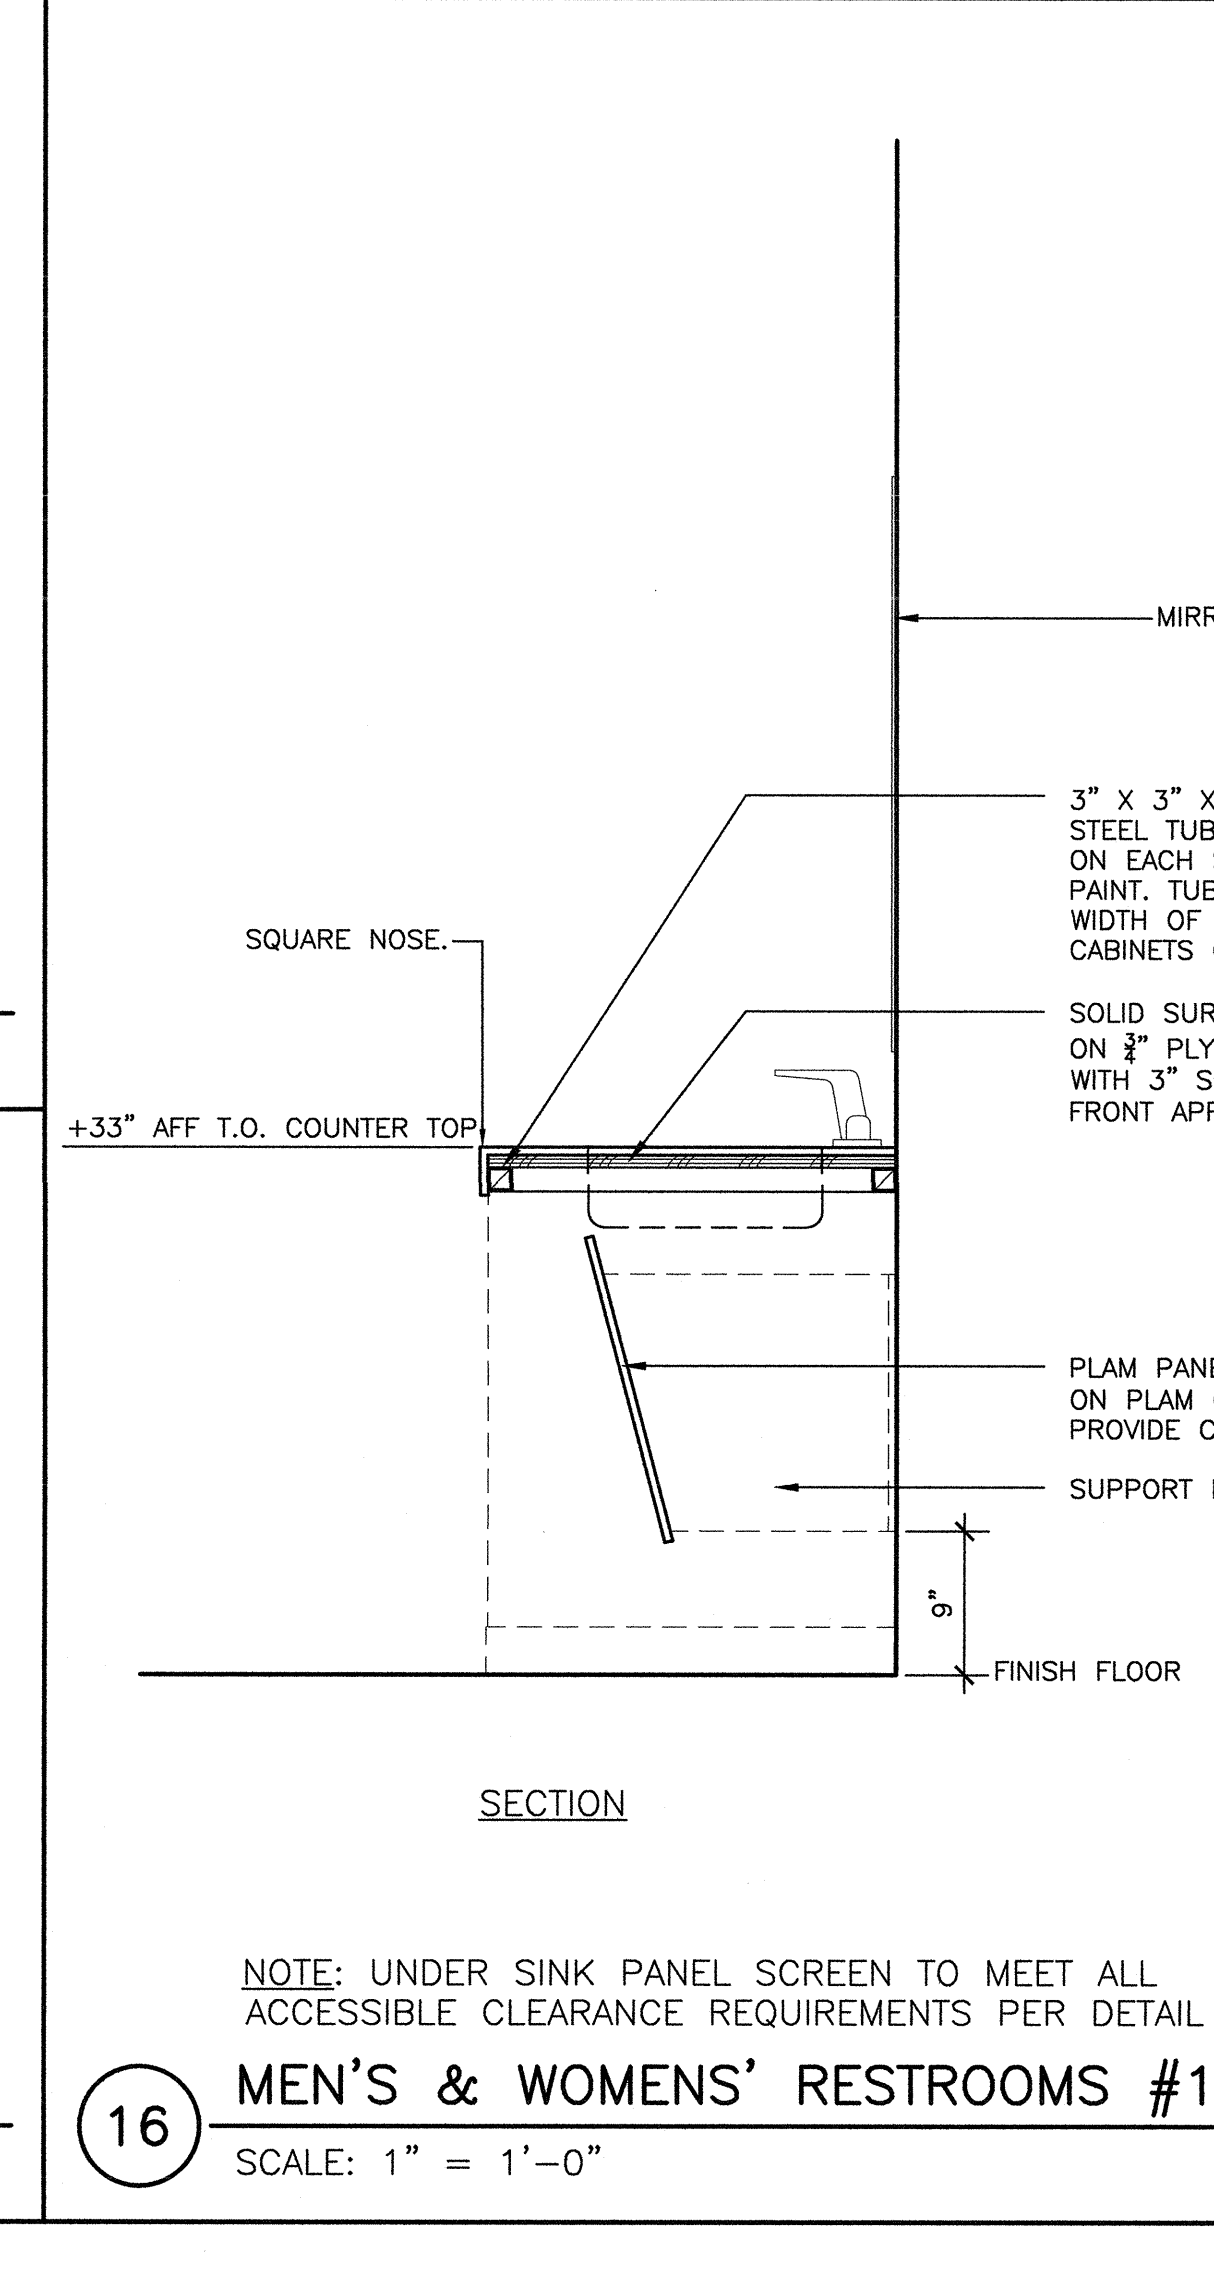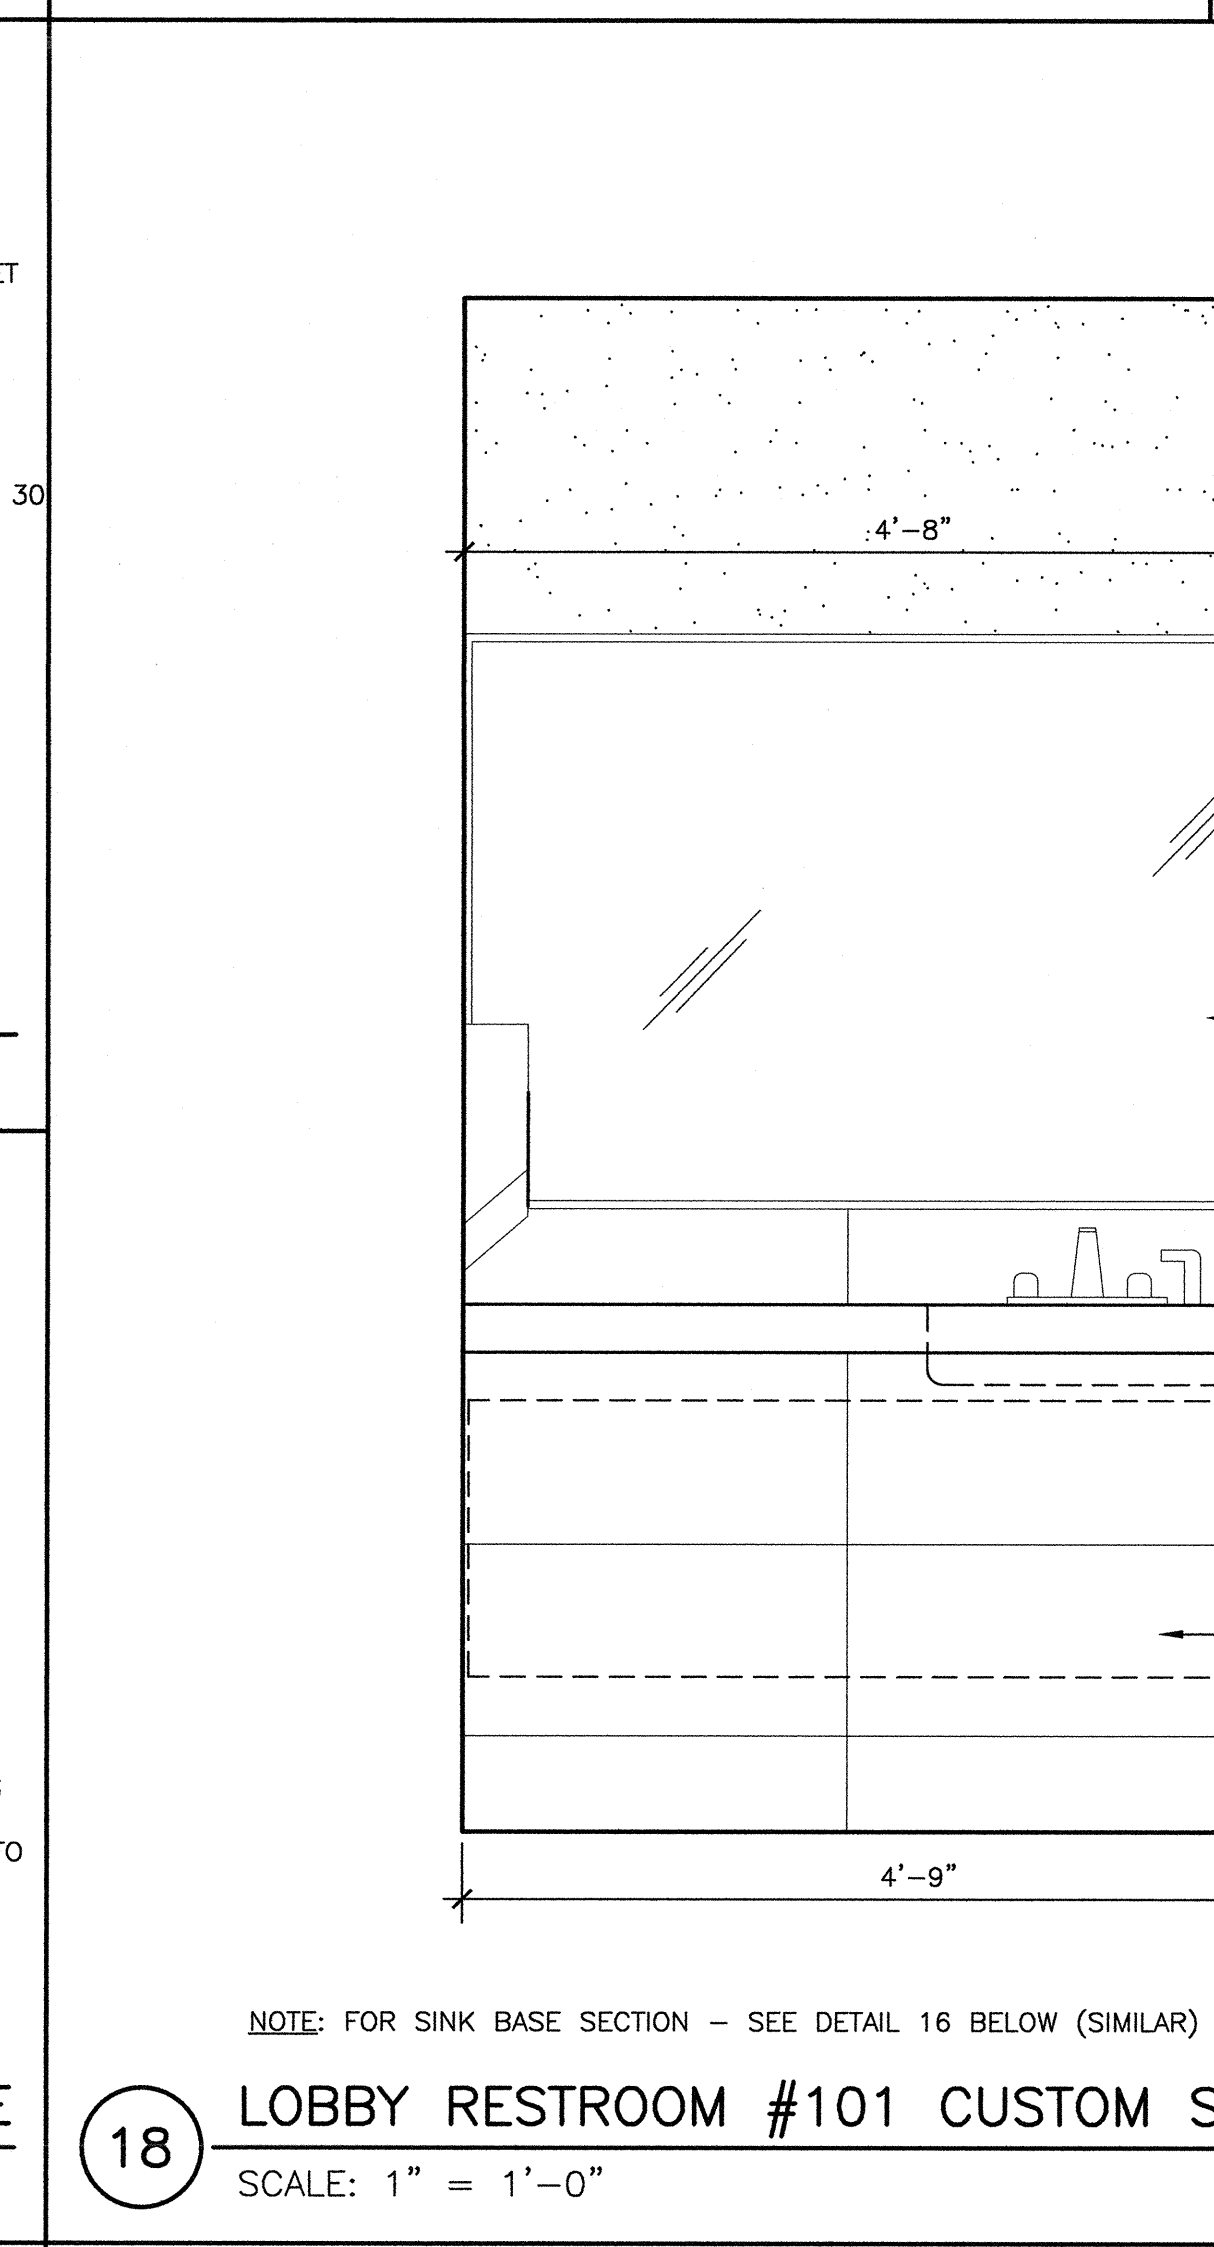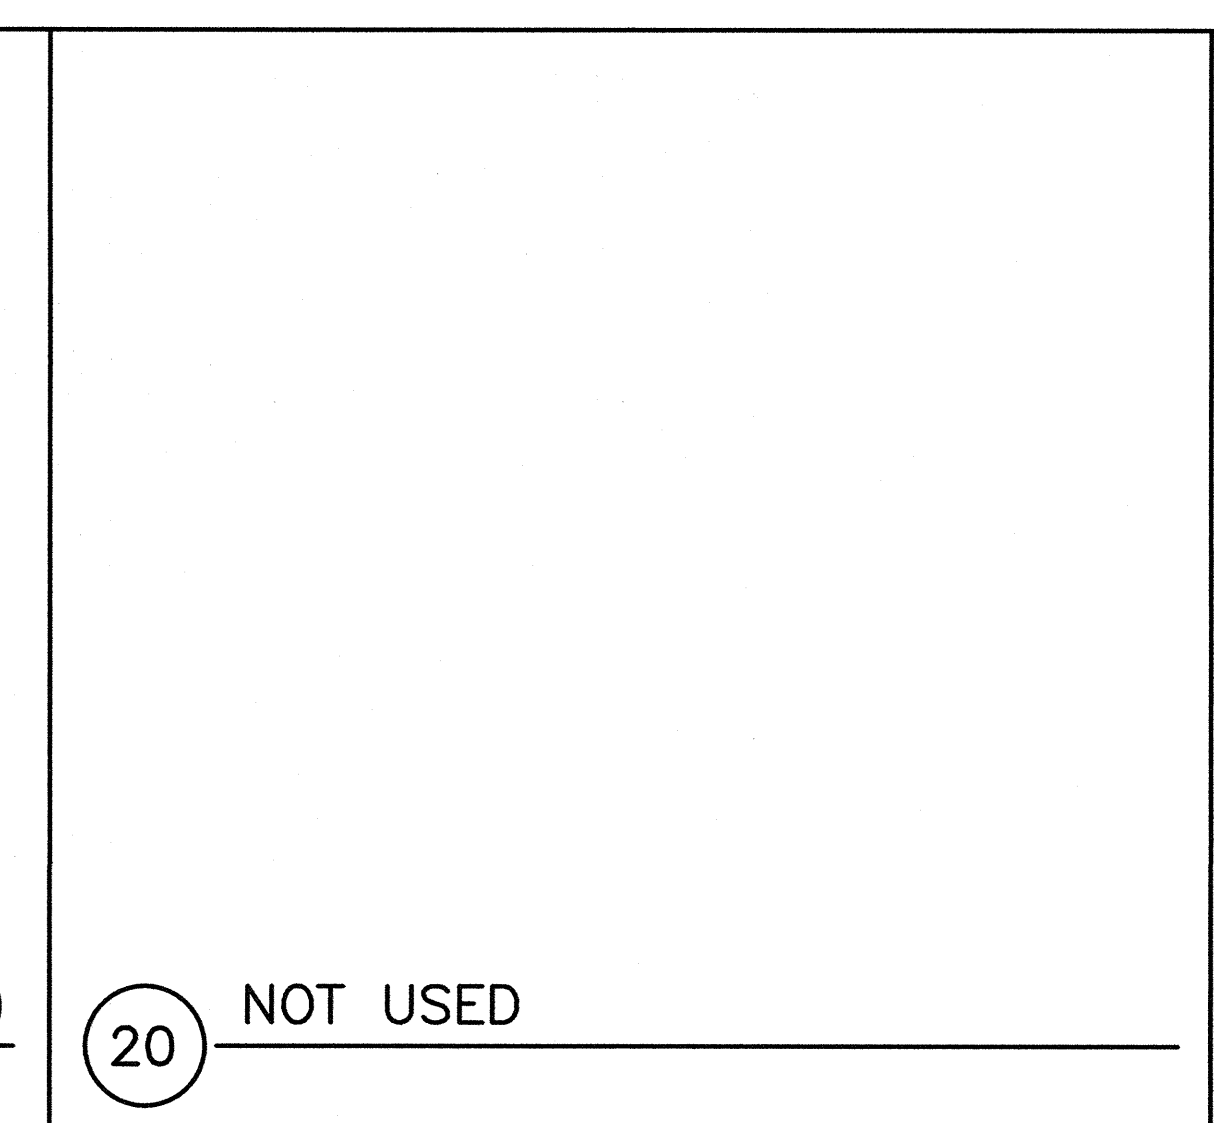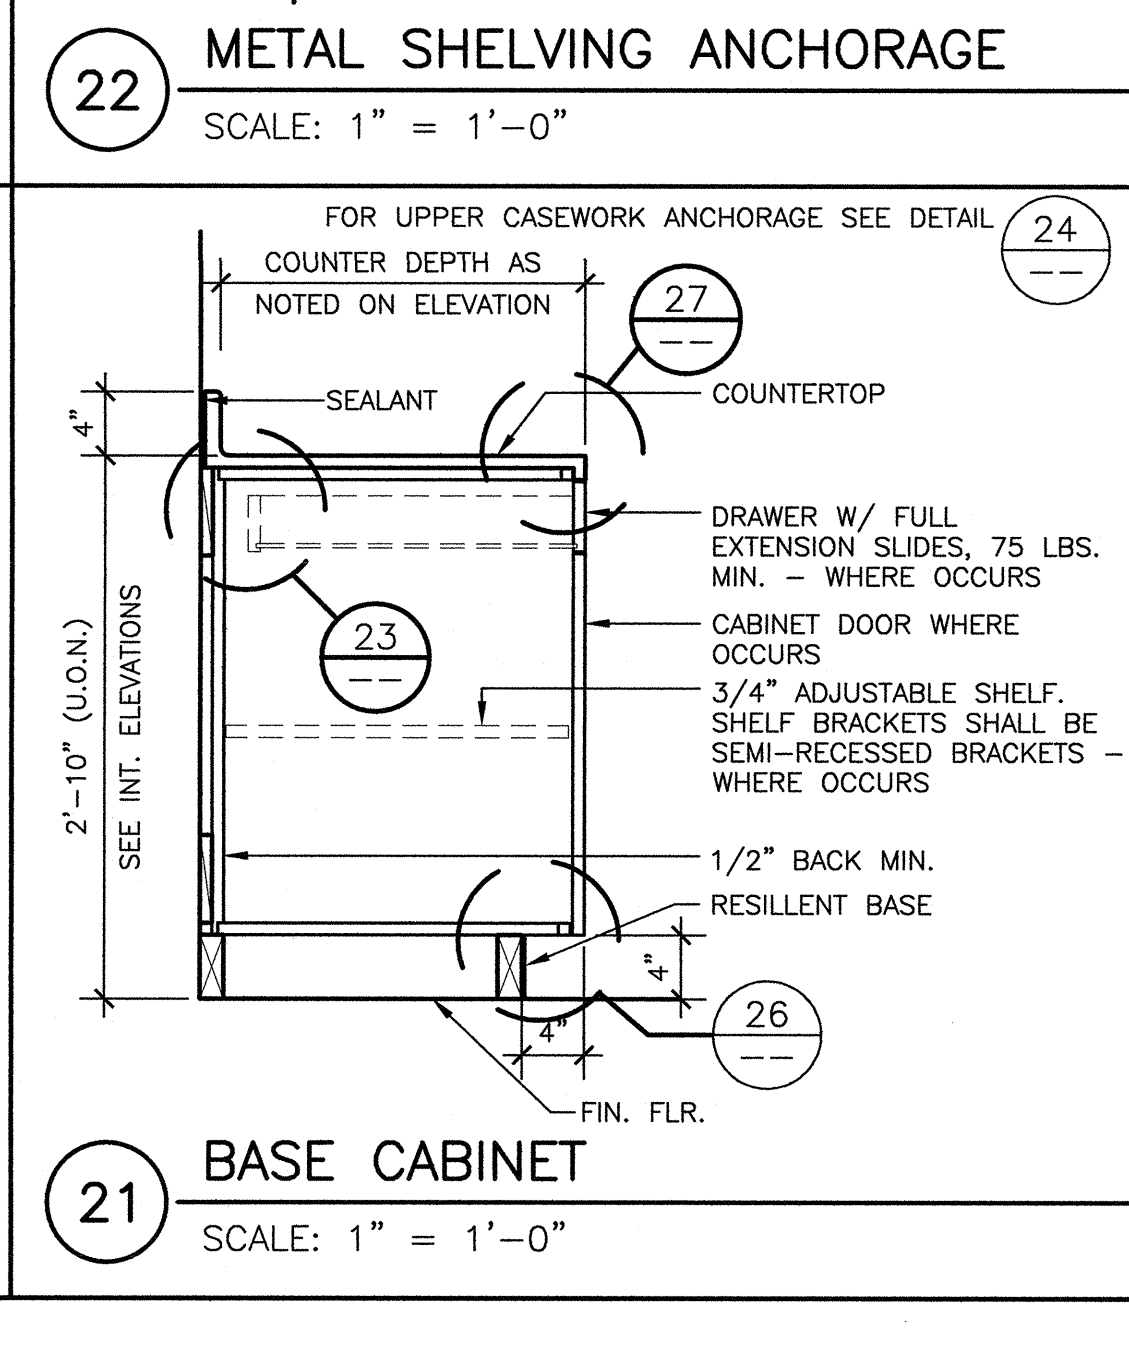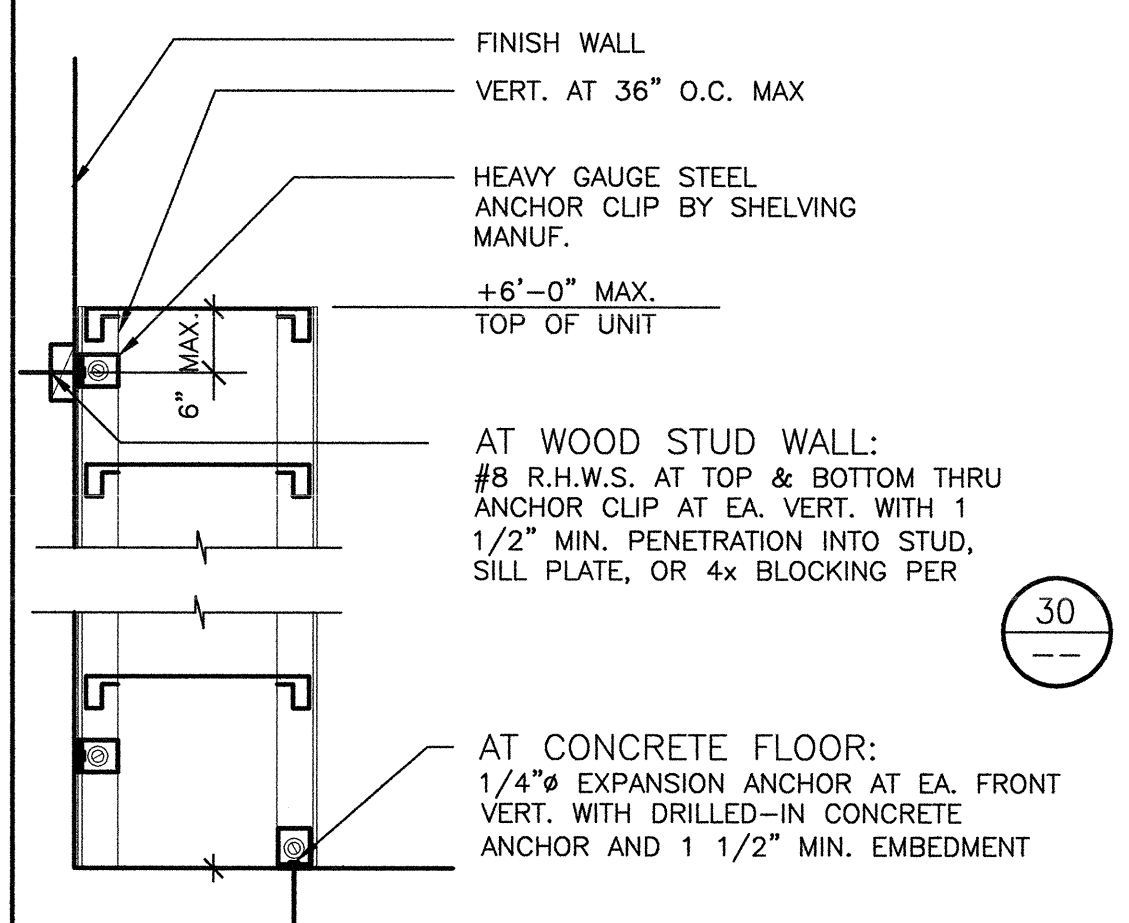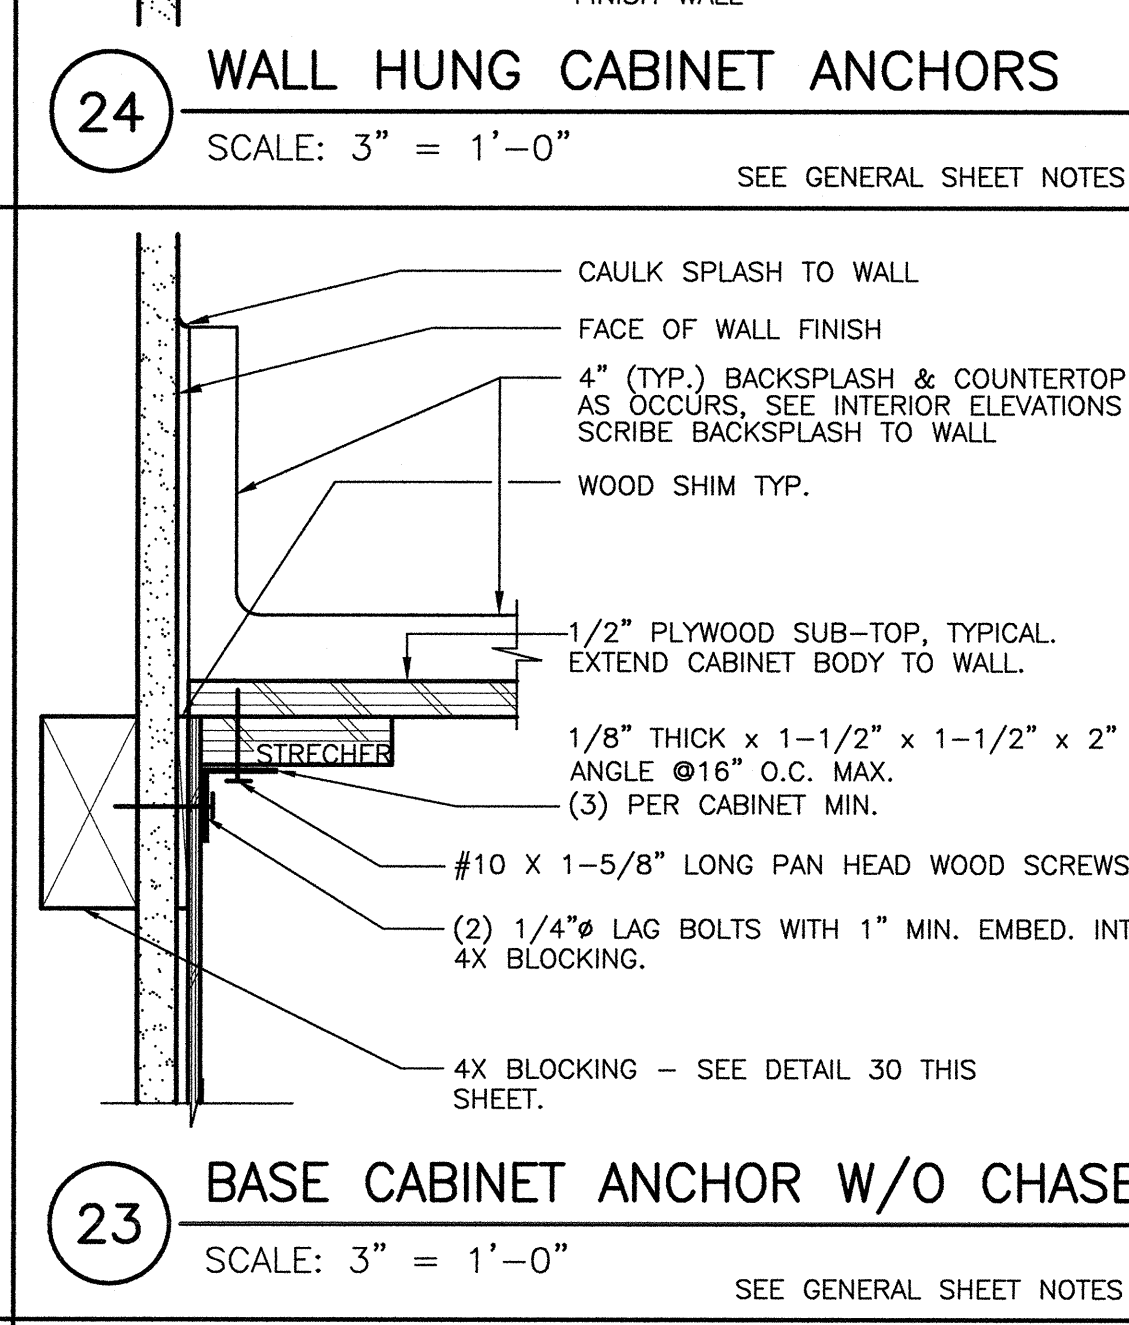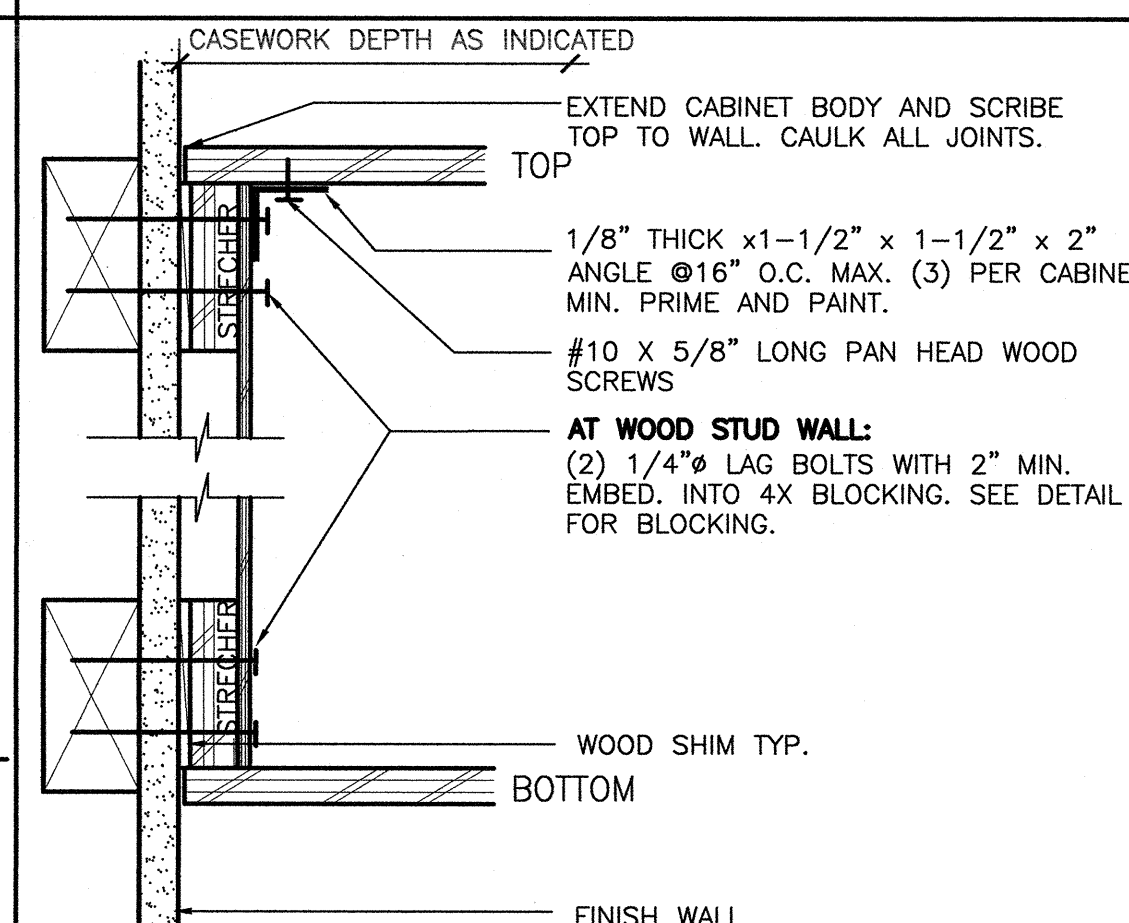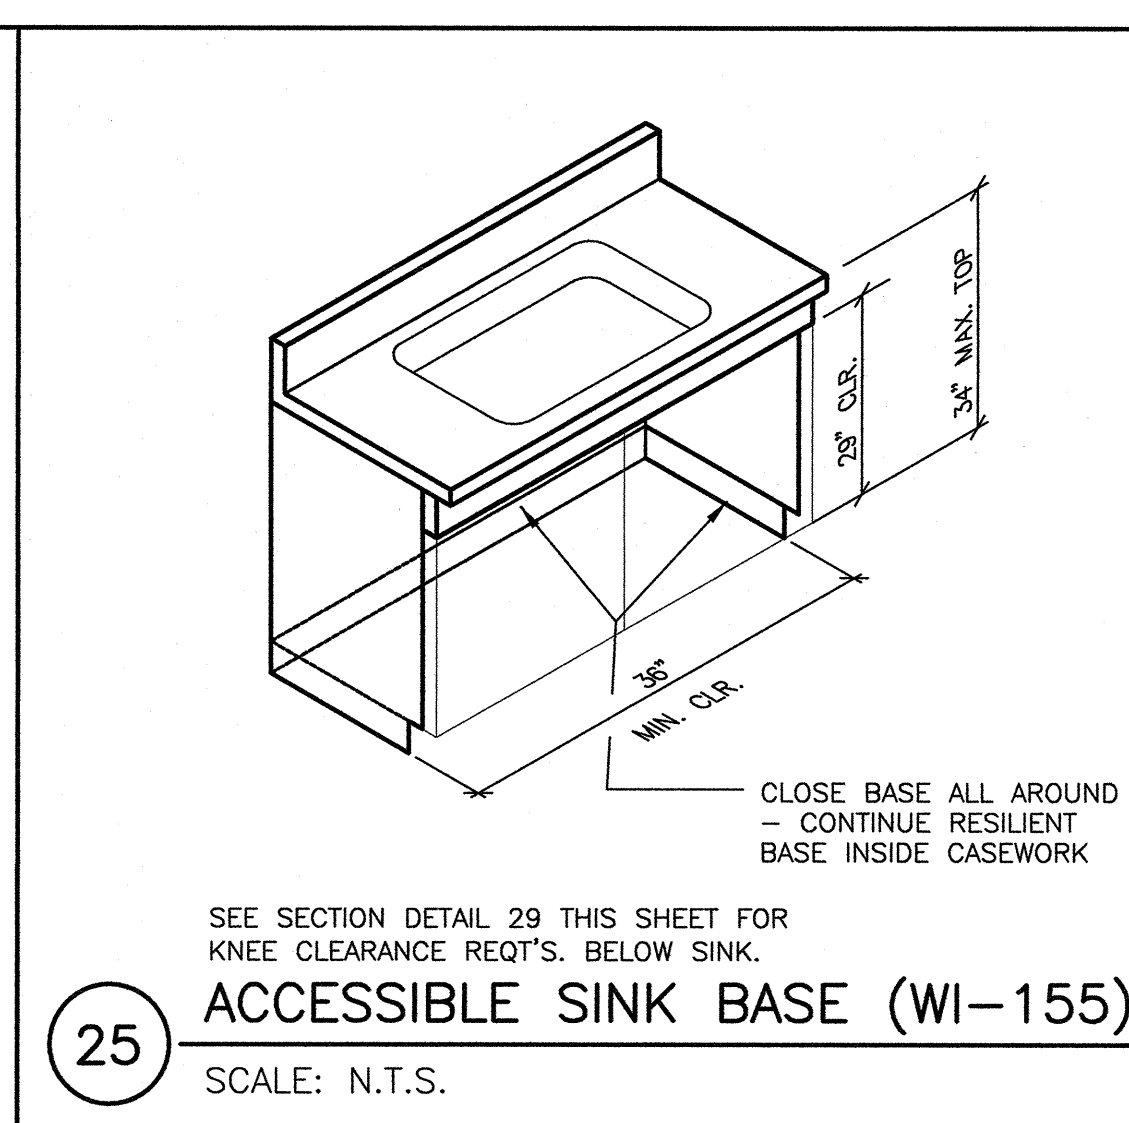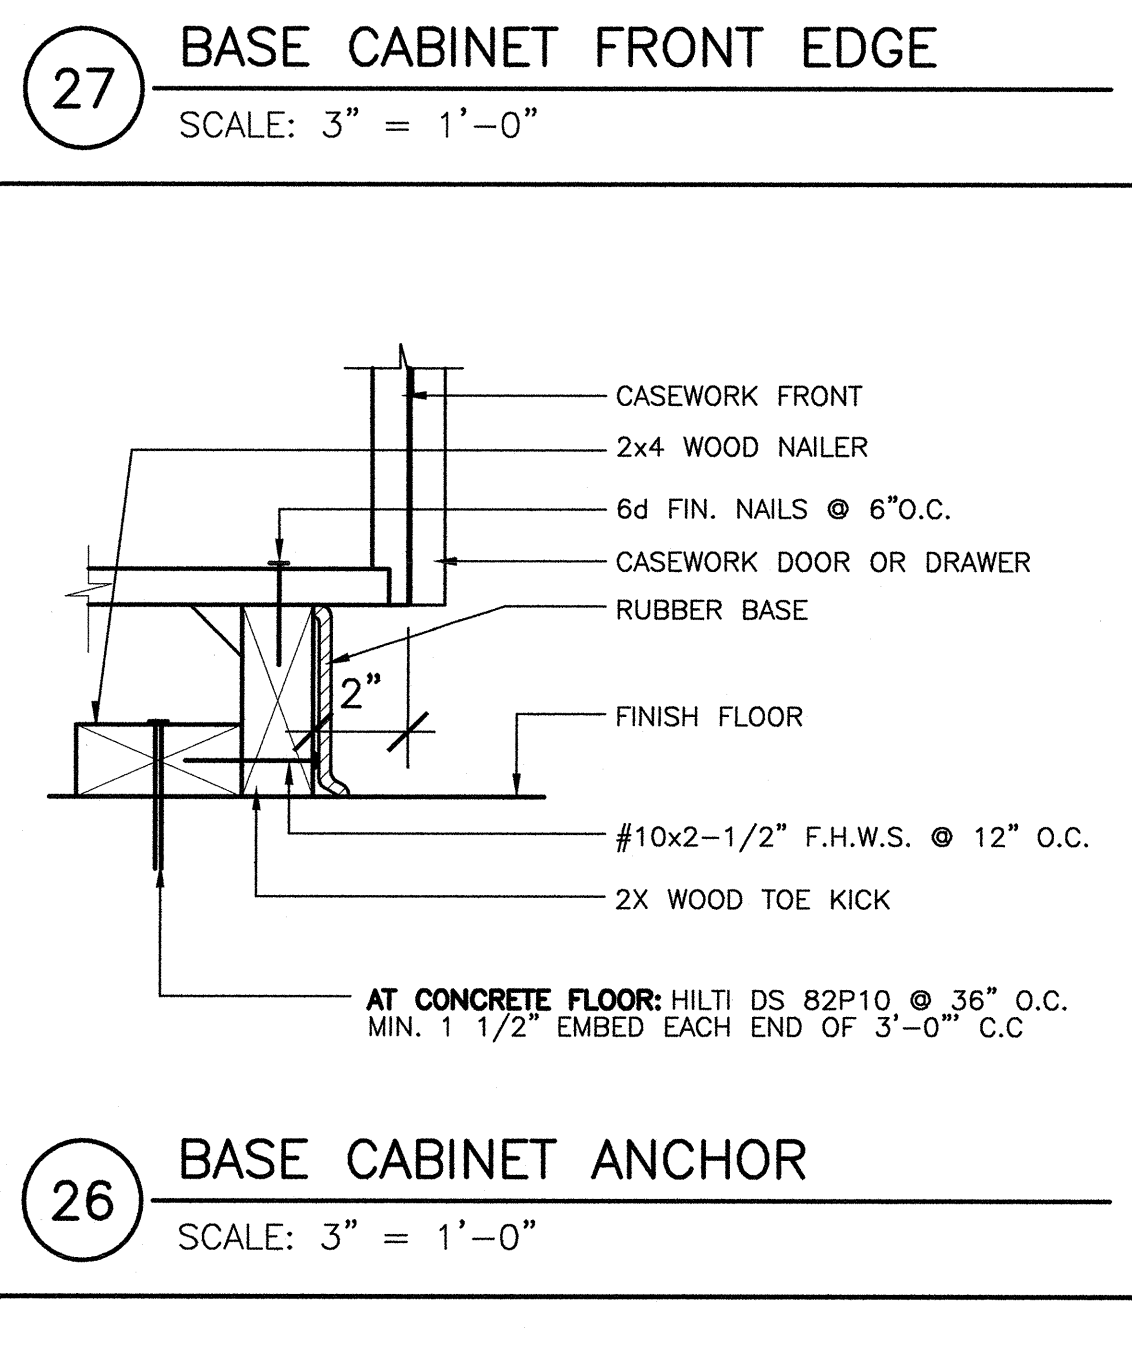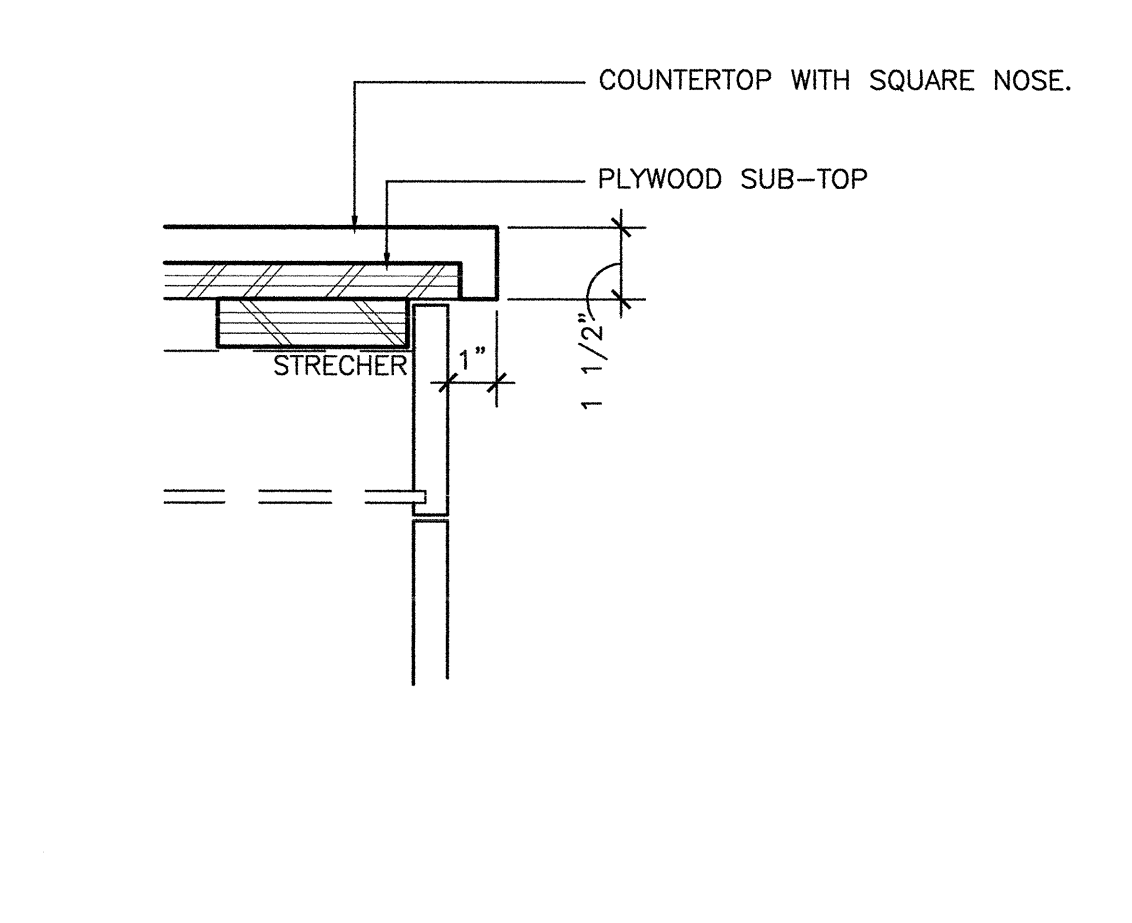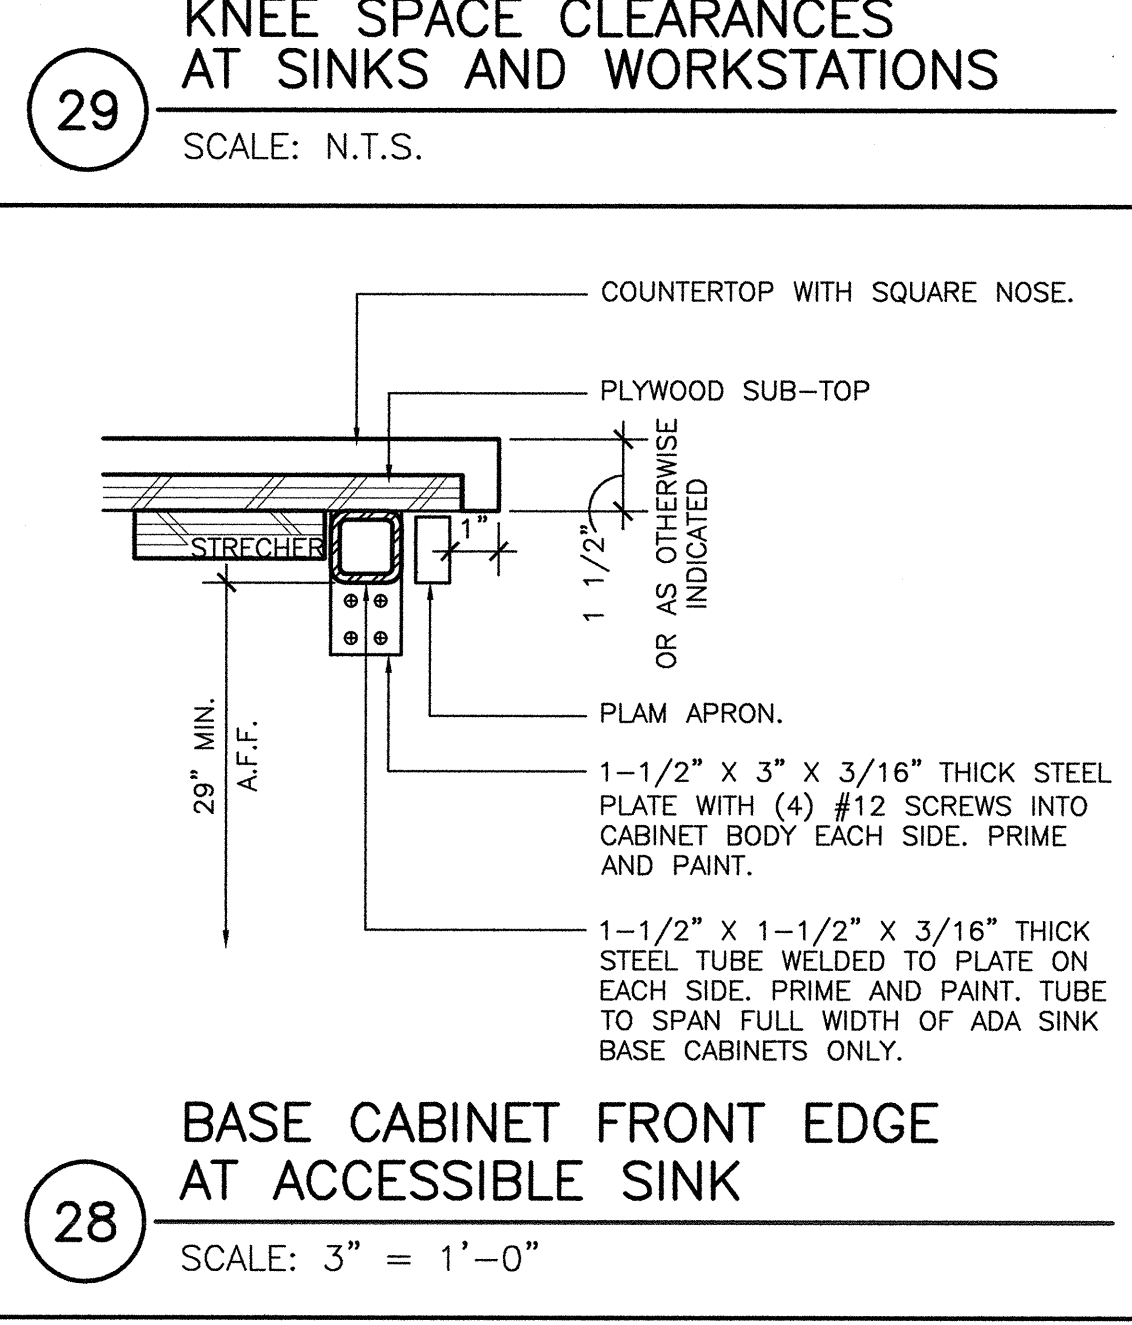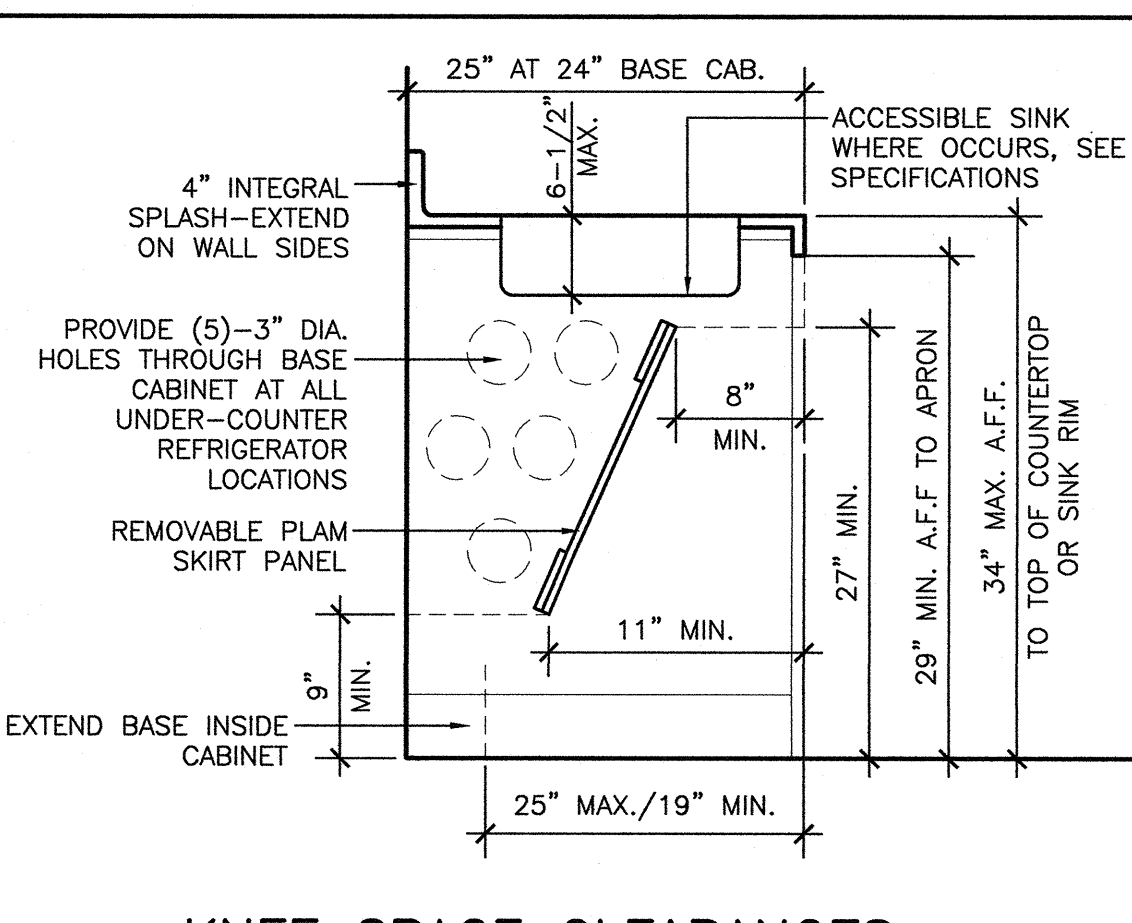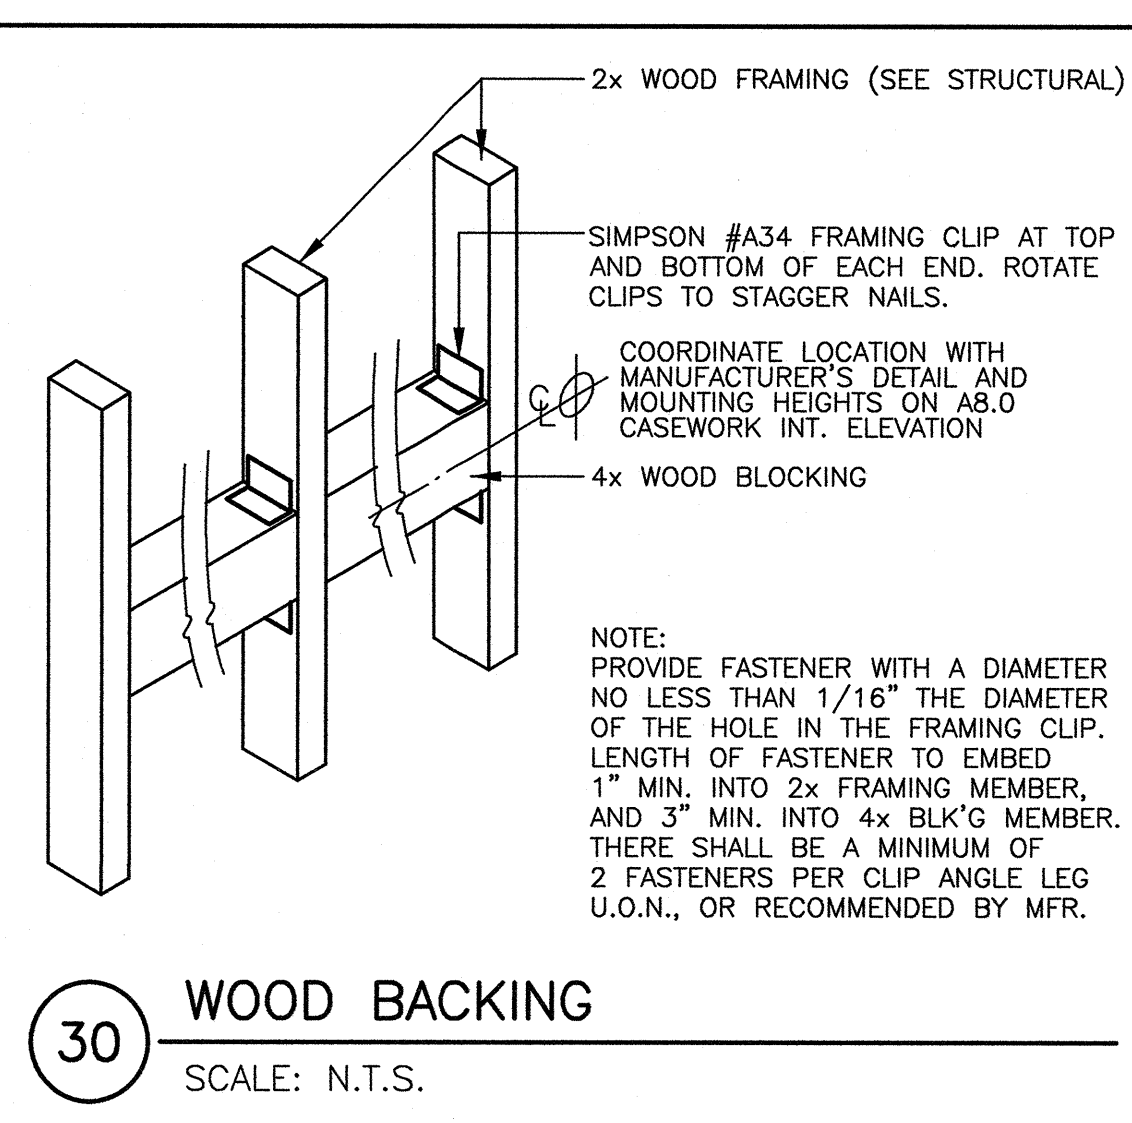

Dry Creek Joint Elementary School District
District Education Center

8849 Cook Riolo Road, Roseville, CA 95747

Dry Creek Joint Elementary School District

FILE NO. 31-15

IDENTIFICATION STAMP DIV. OF THE
STATE ARCHITECT OFFICE OF
REGULATION SERVICES

APPLICATION NO.
02-115456

AC. *FLS* *SS* *SS*

DATE *1/31/19* *CS*

DIVISION OF THE STATE ARCHITECT

revision date: _____ by: _____

CONSULTANT

nacht&lewis

600 O Street, Suite 100
Sacramento, CA 95811
www.nachtlewis.com
916.329.4000

REGISTERED ARCHITECT
No. C-50867
RENEWAL DATE:
1/31/19
STATE OF CALIFORNIA

ARCHITECT

INITIAL BOX

NO.	DWG BY	DATE	REVIEWED

REVISIONS

NO.	DESCRIPTION	DATE	REV'D
	100% design development	7/2016	
	75% construction documents	9/2016	
	DSA submittal	12/31/16	
	DSA approval	02/23/17	

DATE February 23, 2017

JOB NO. Y1538.00

SHEET TITLE













Casework
Elevations
& Details

SHEET NO.

A7.3

SHEET ____ OF ____ TOTAL

ONE AND ONE-HALF INCH = ONE FOOT
ONE INCH = ONE FOOT
THREE-QUARTERS INCH = ONE FOOT
ONE-HALF INCH = ONE FOOT
ONE-QUARTER INCH = ONE FOOT
ONE-EIGHTH INCH = ONE FOOT
ONE-SIXTEENTH INCH = ONE FOOT
ONE INCH = TWENTY FEET

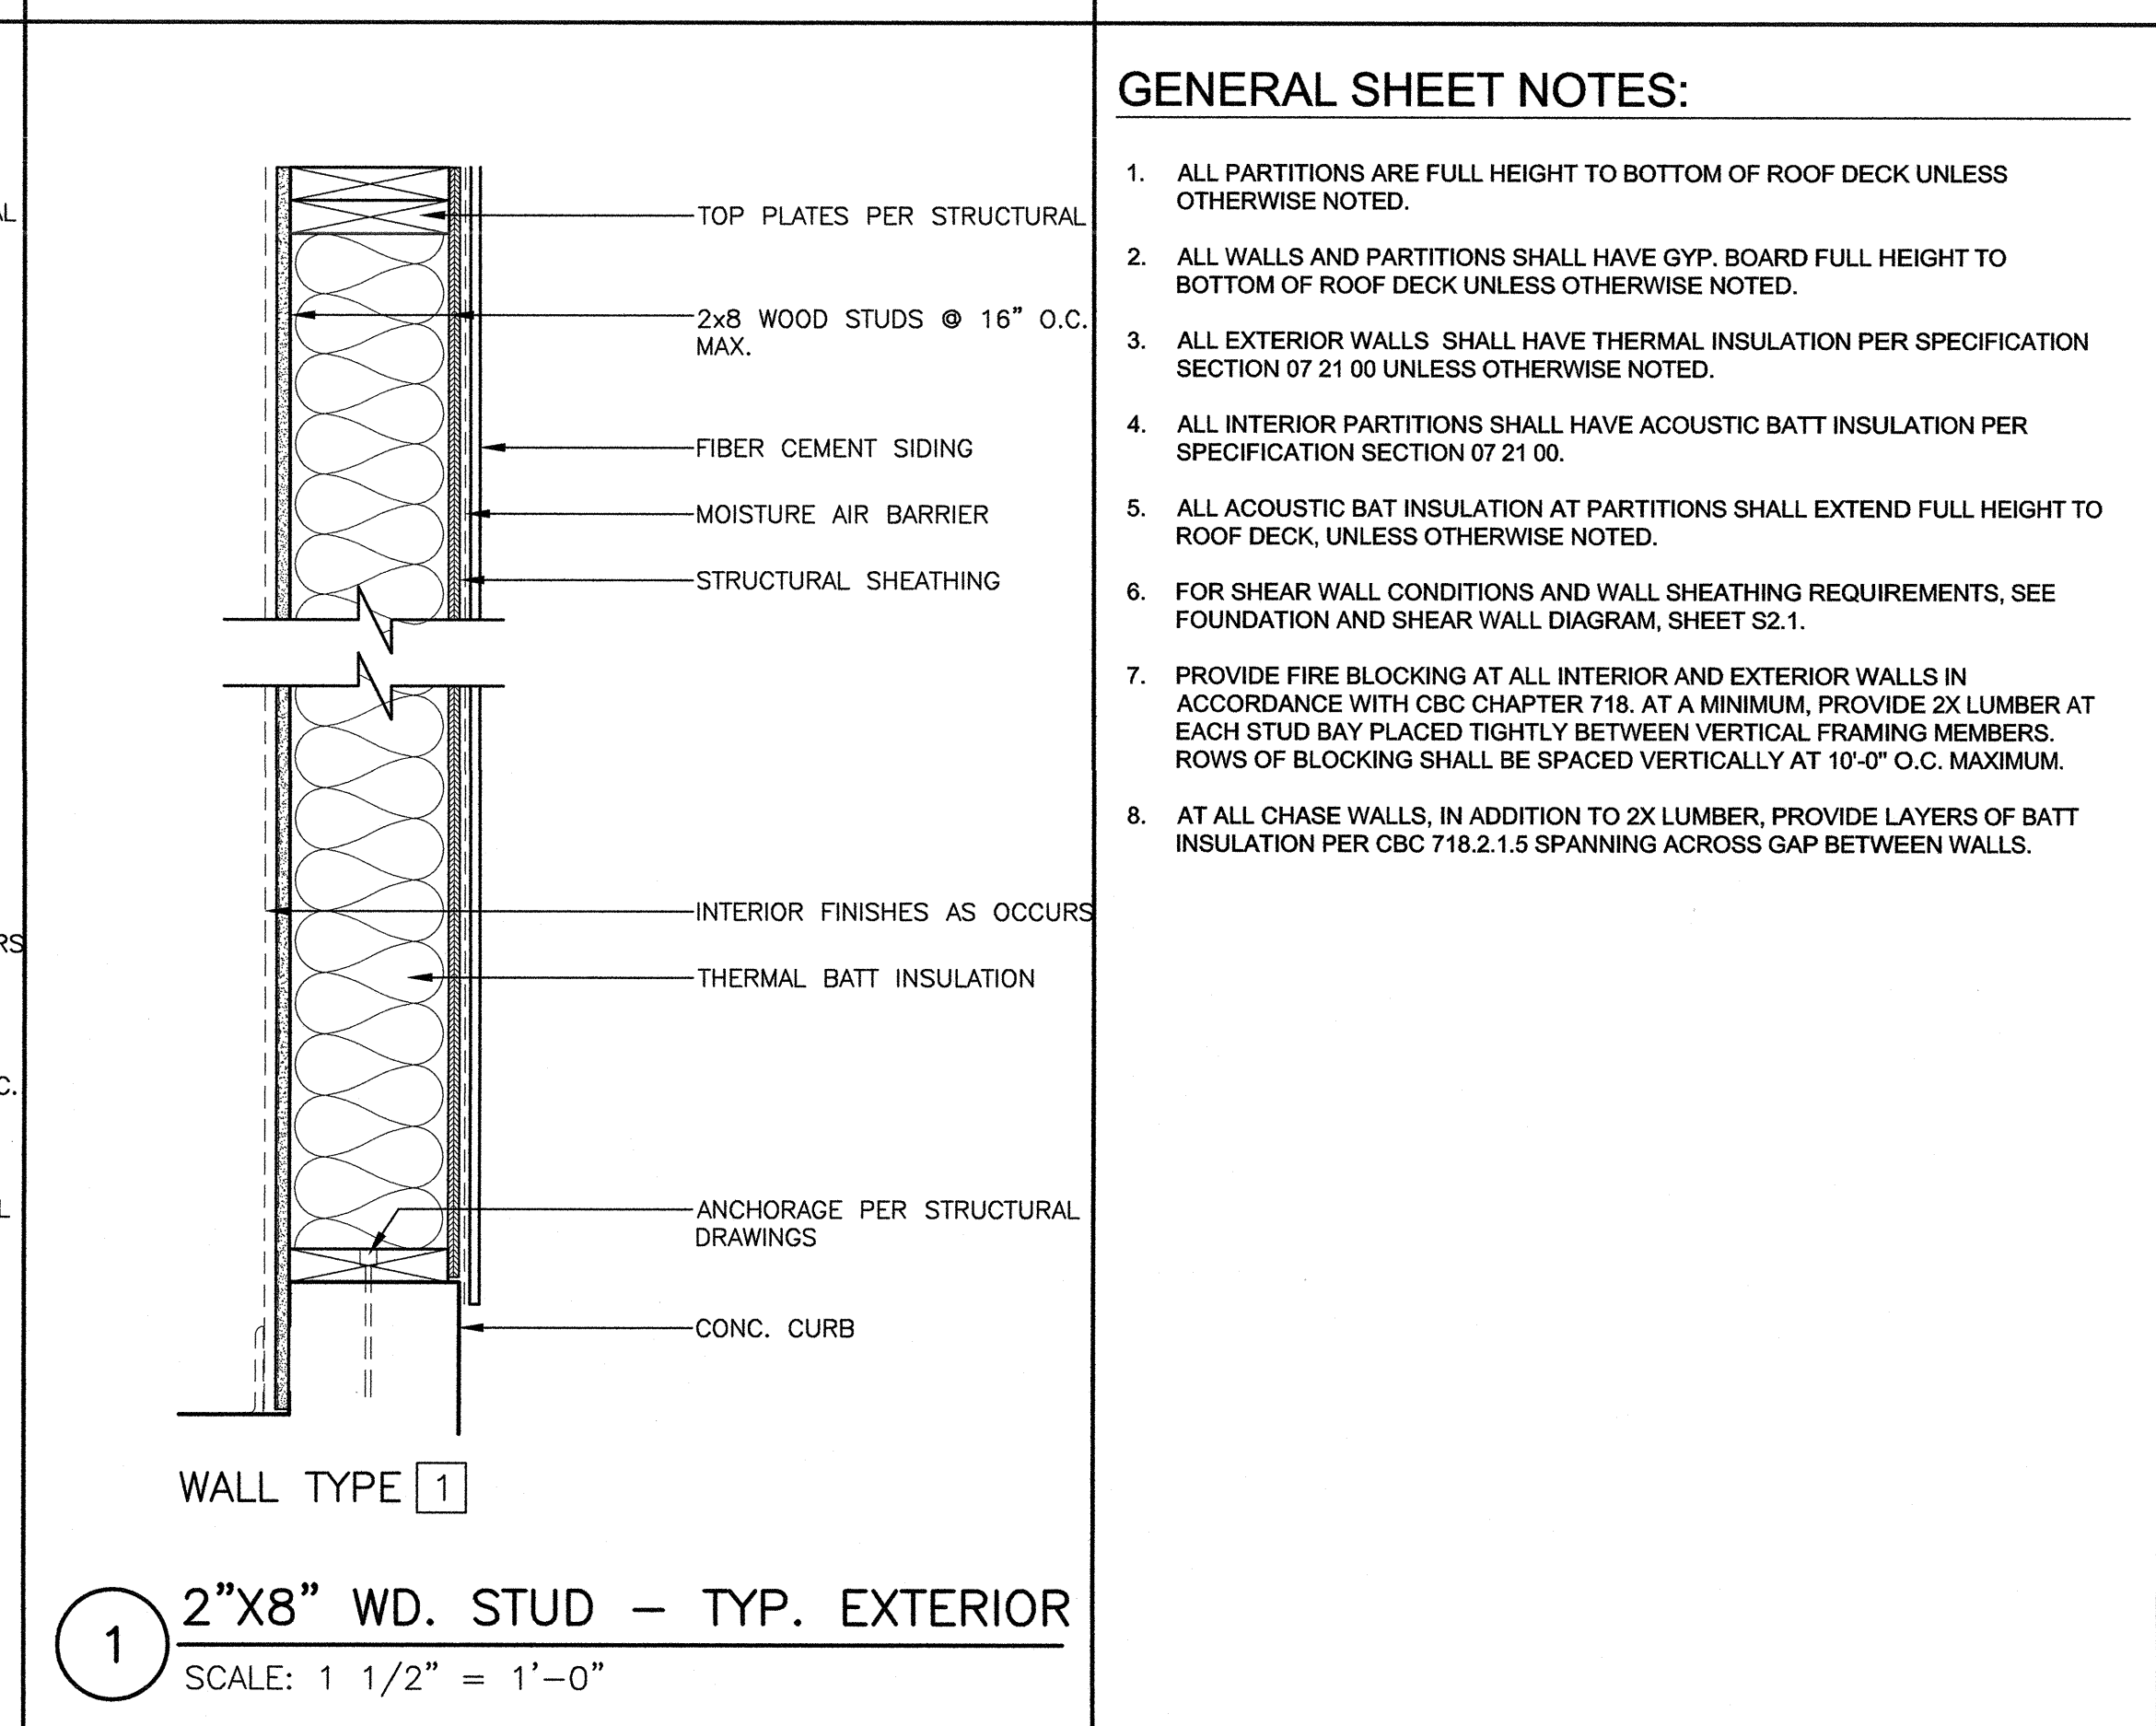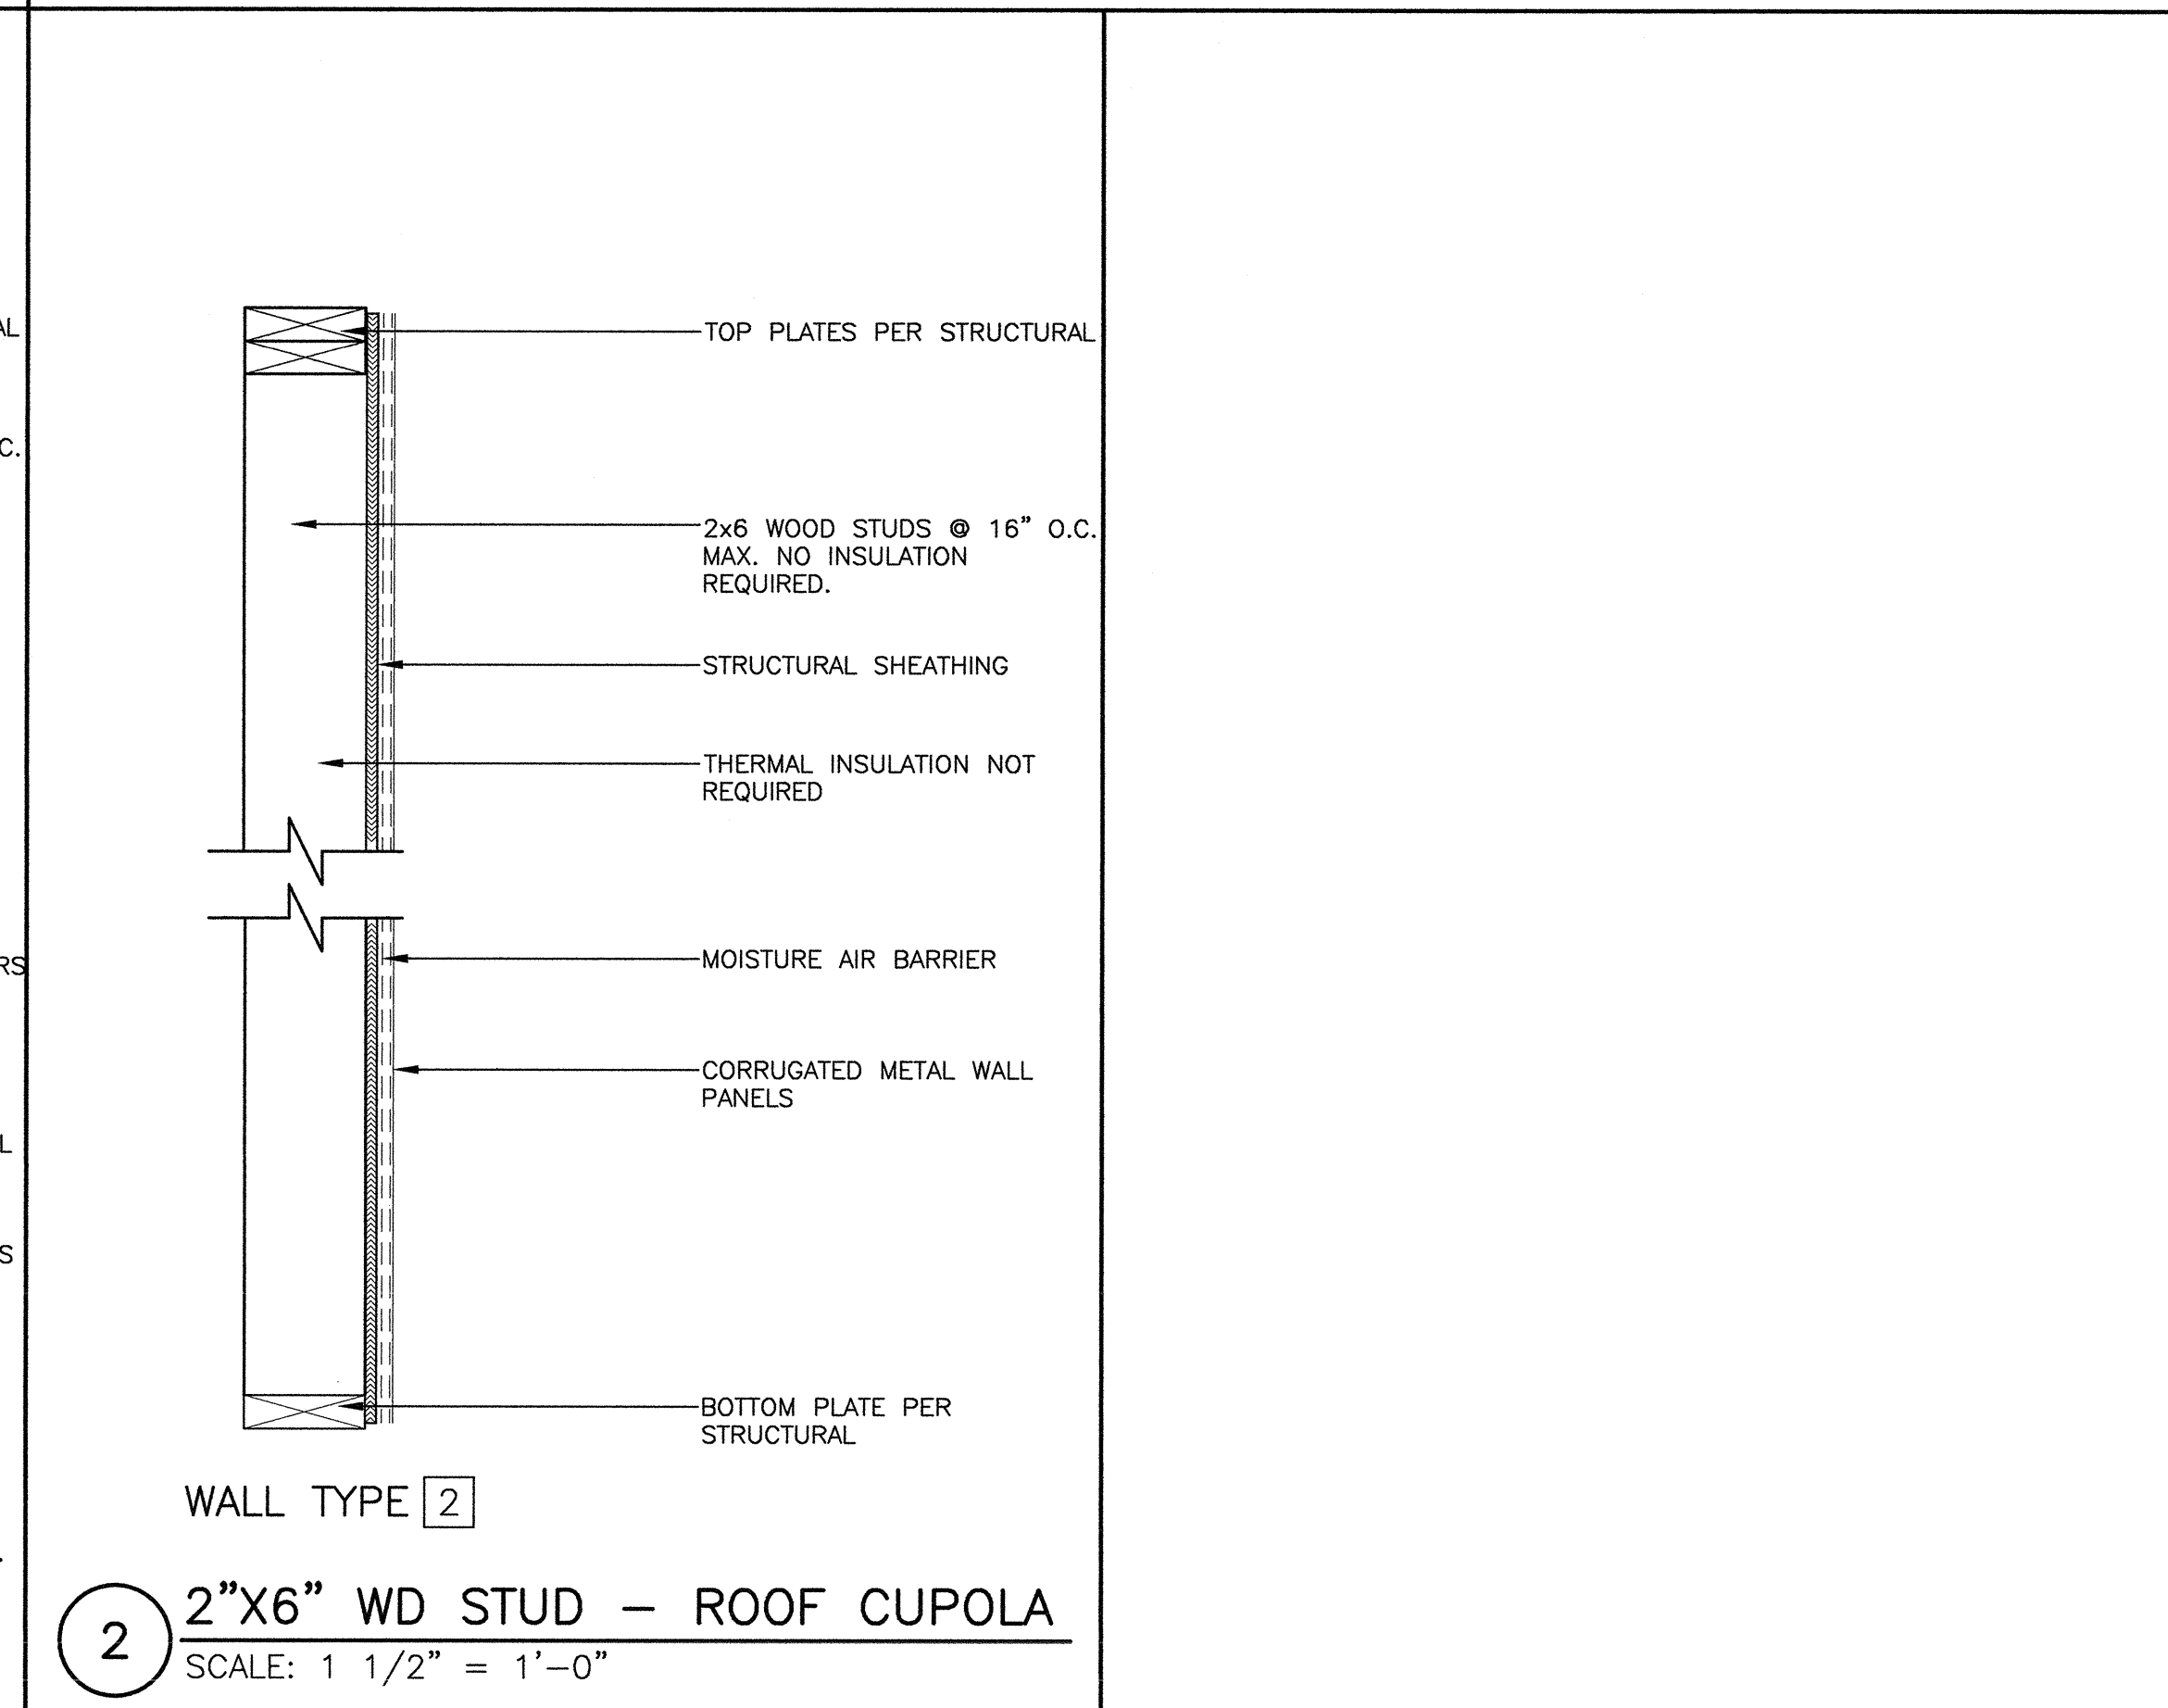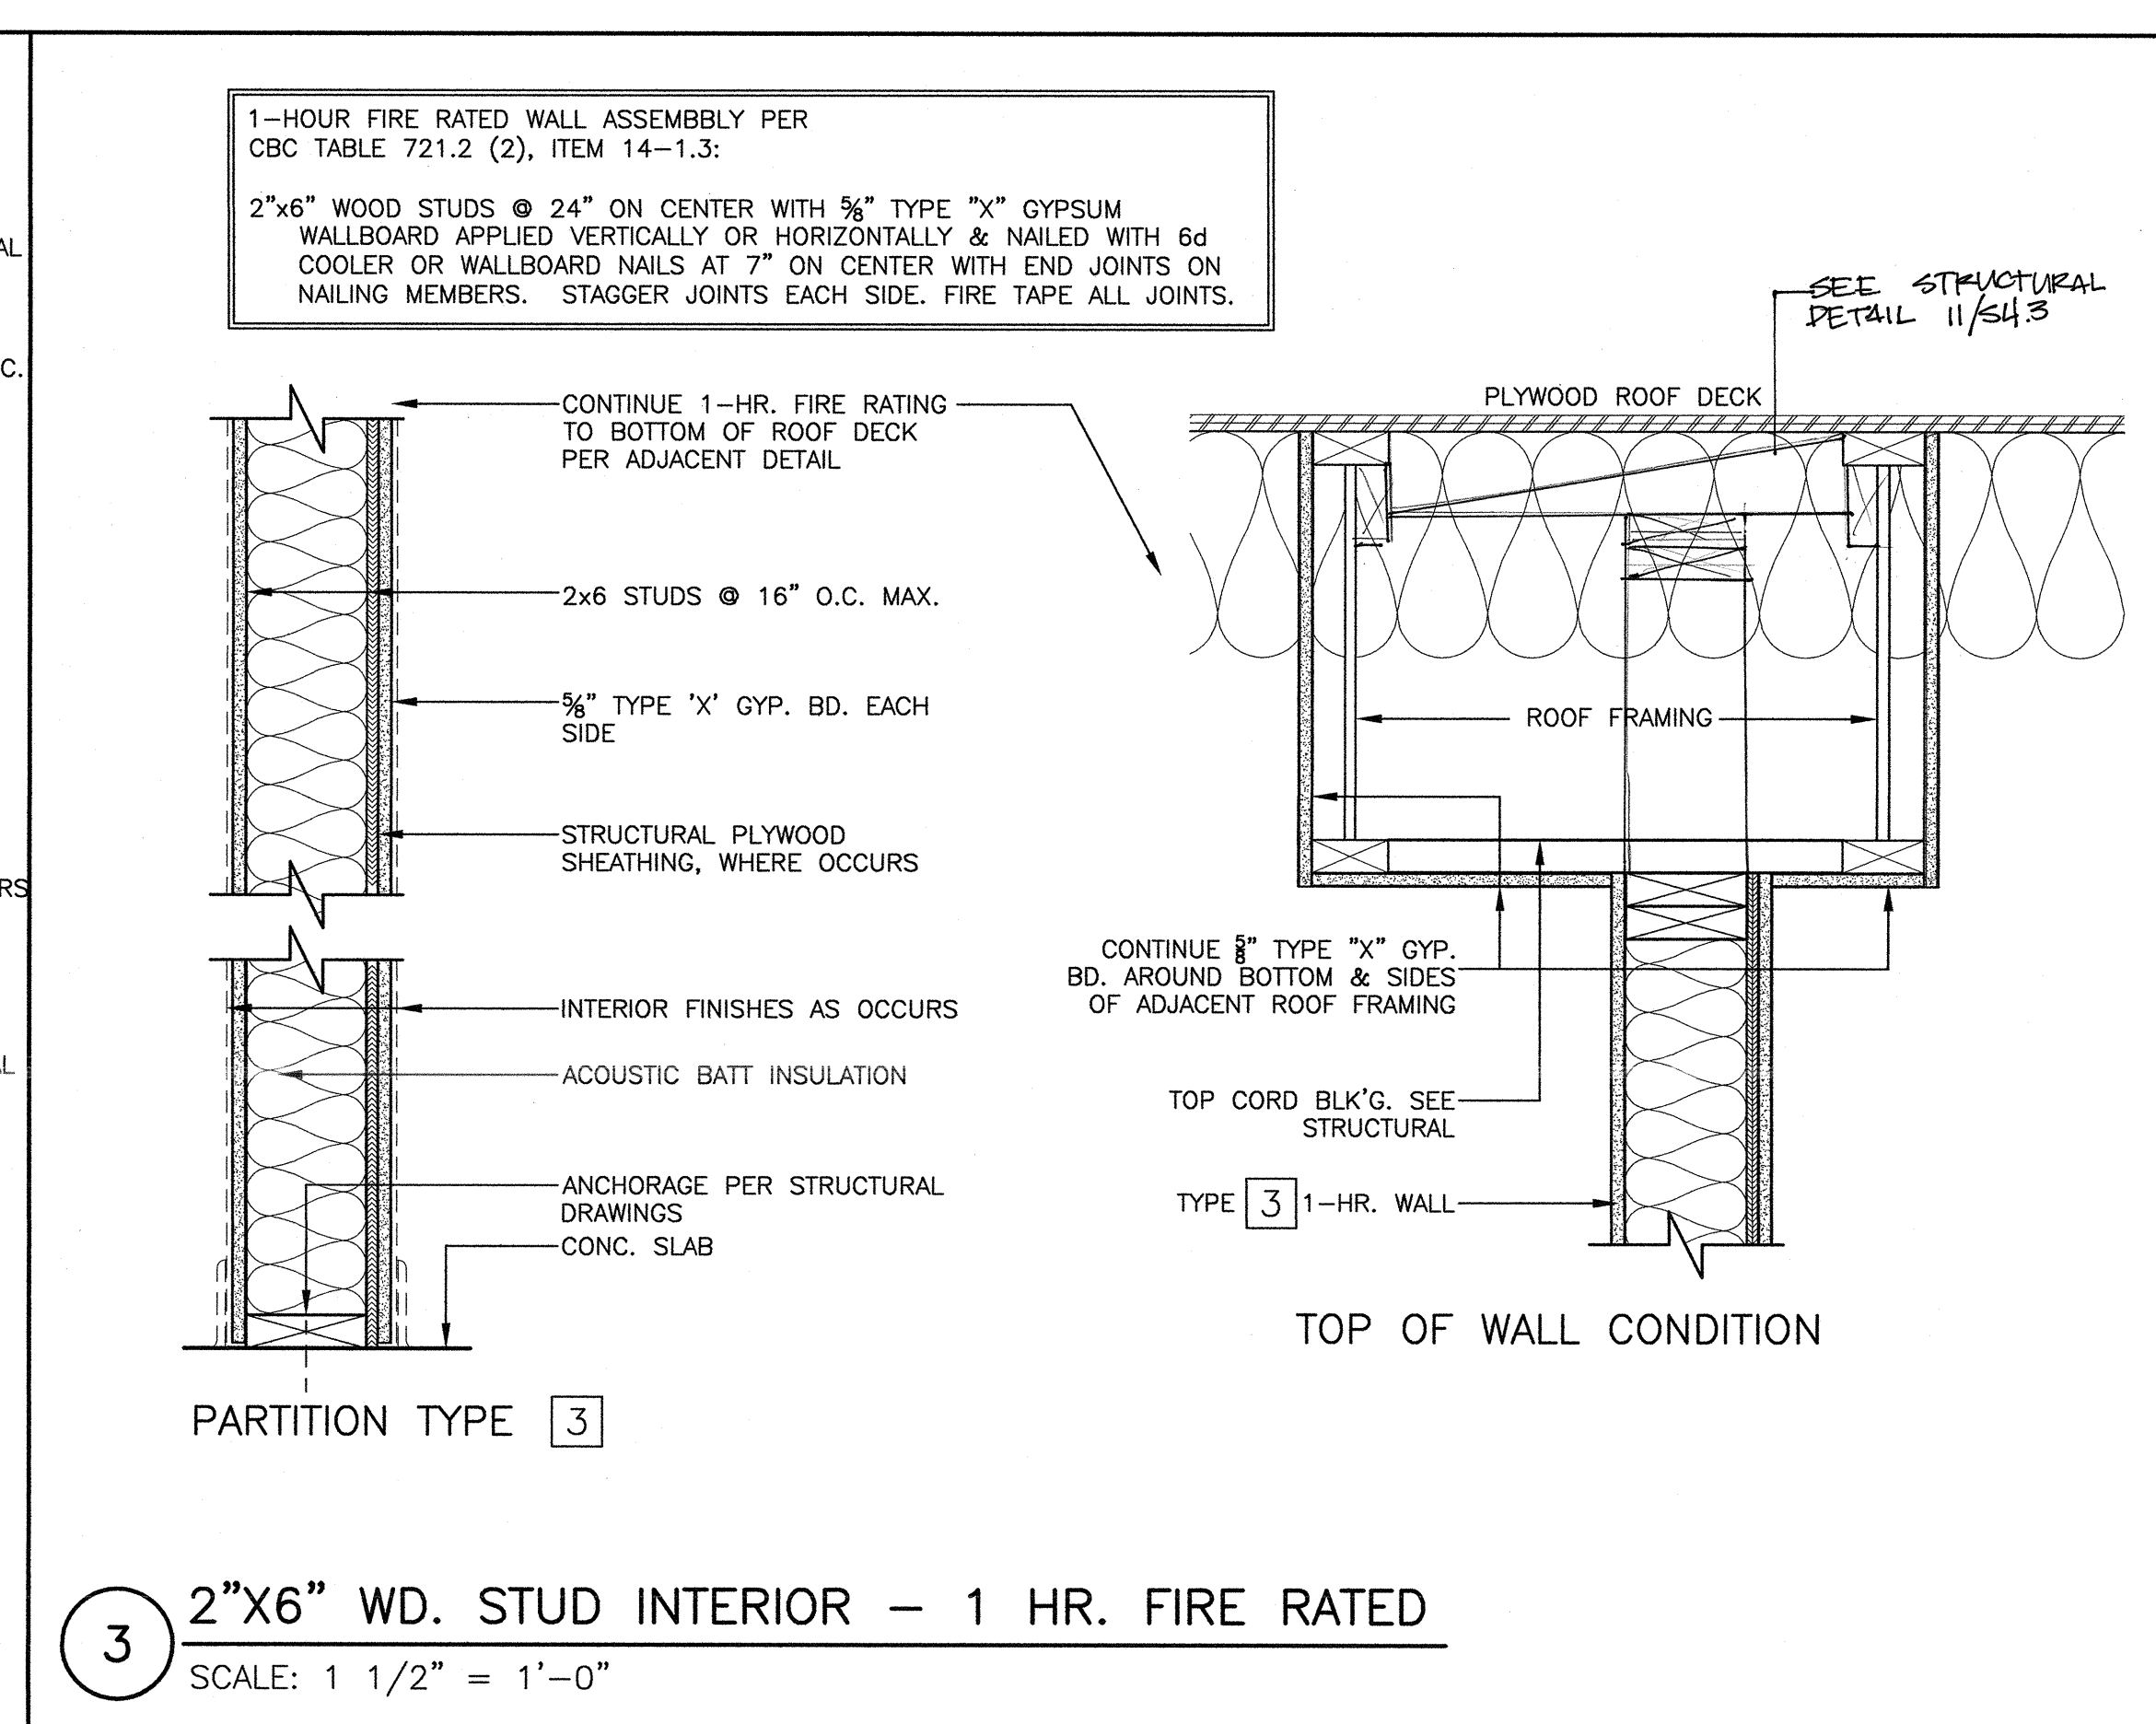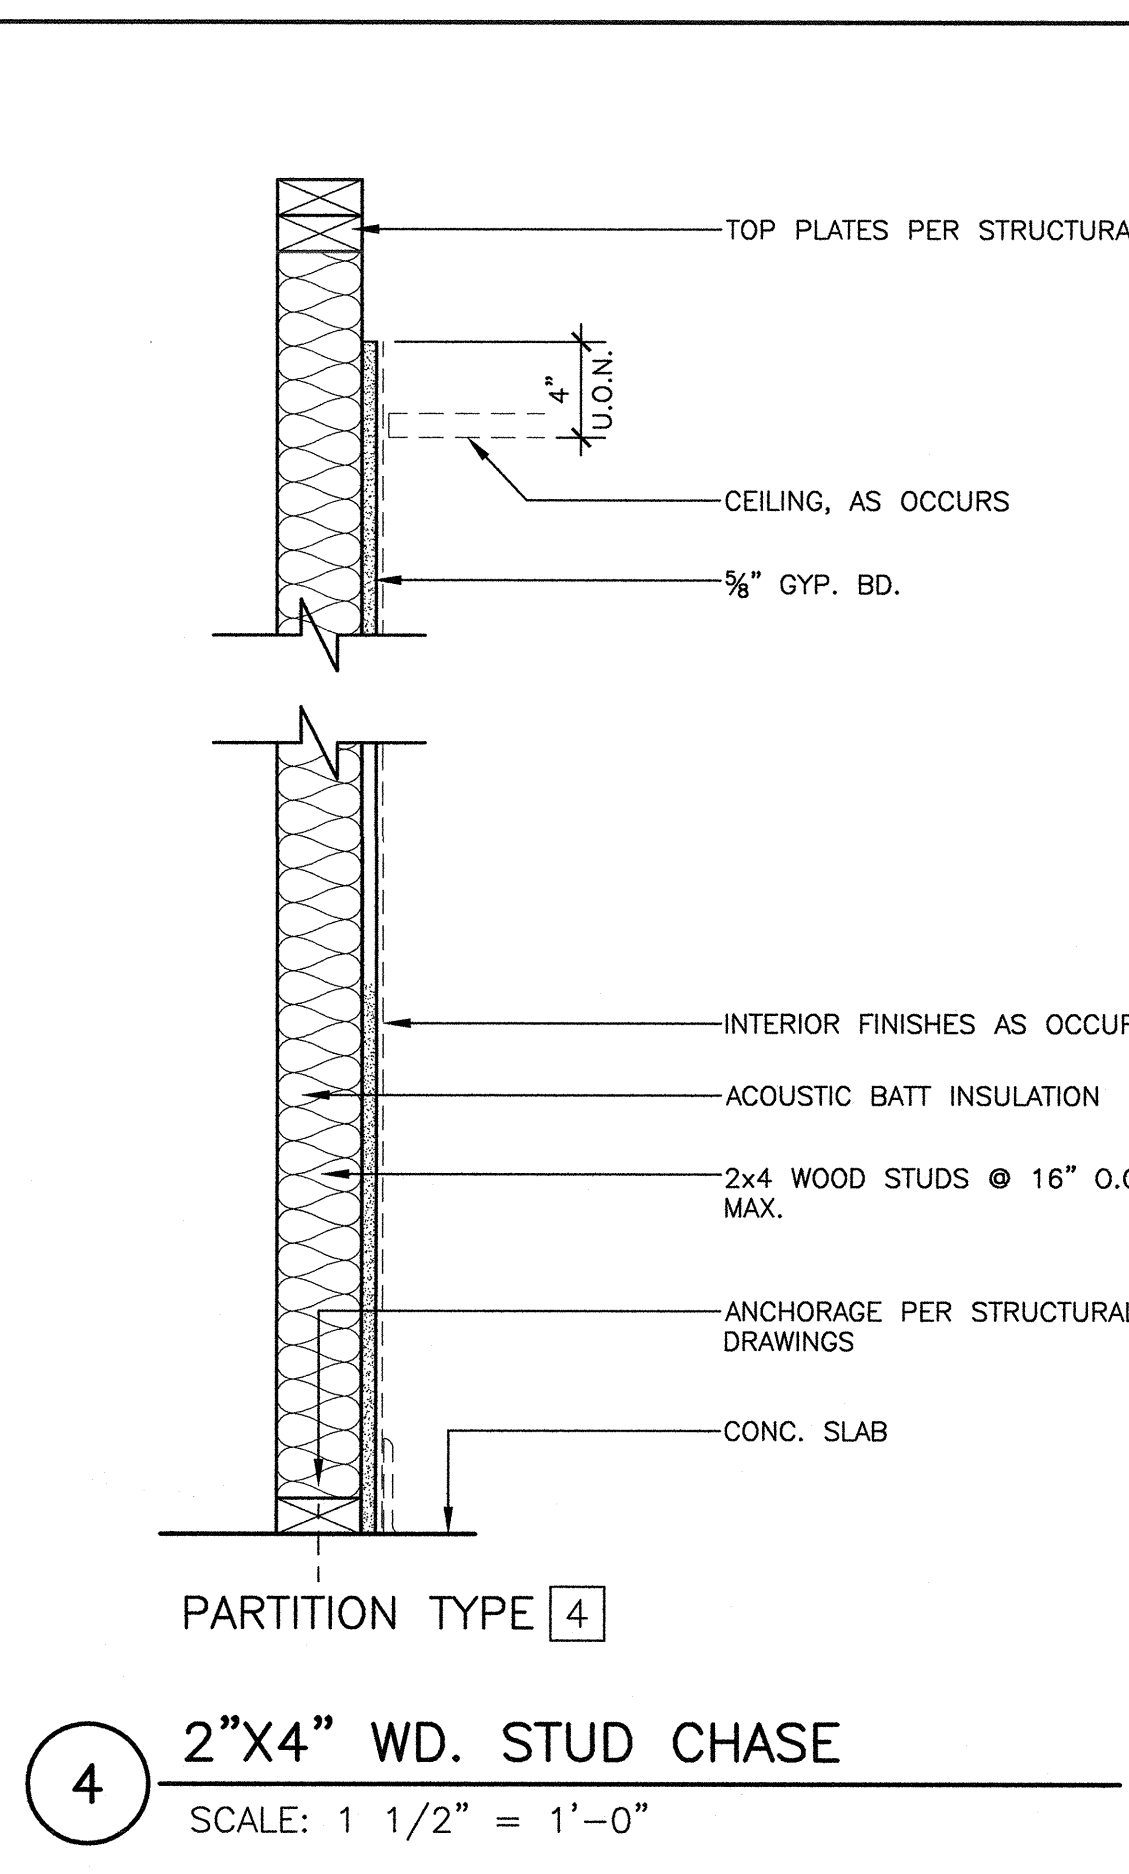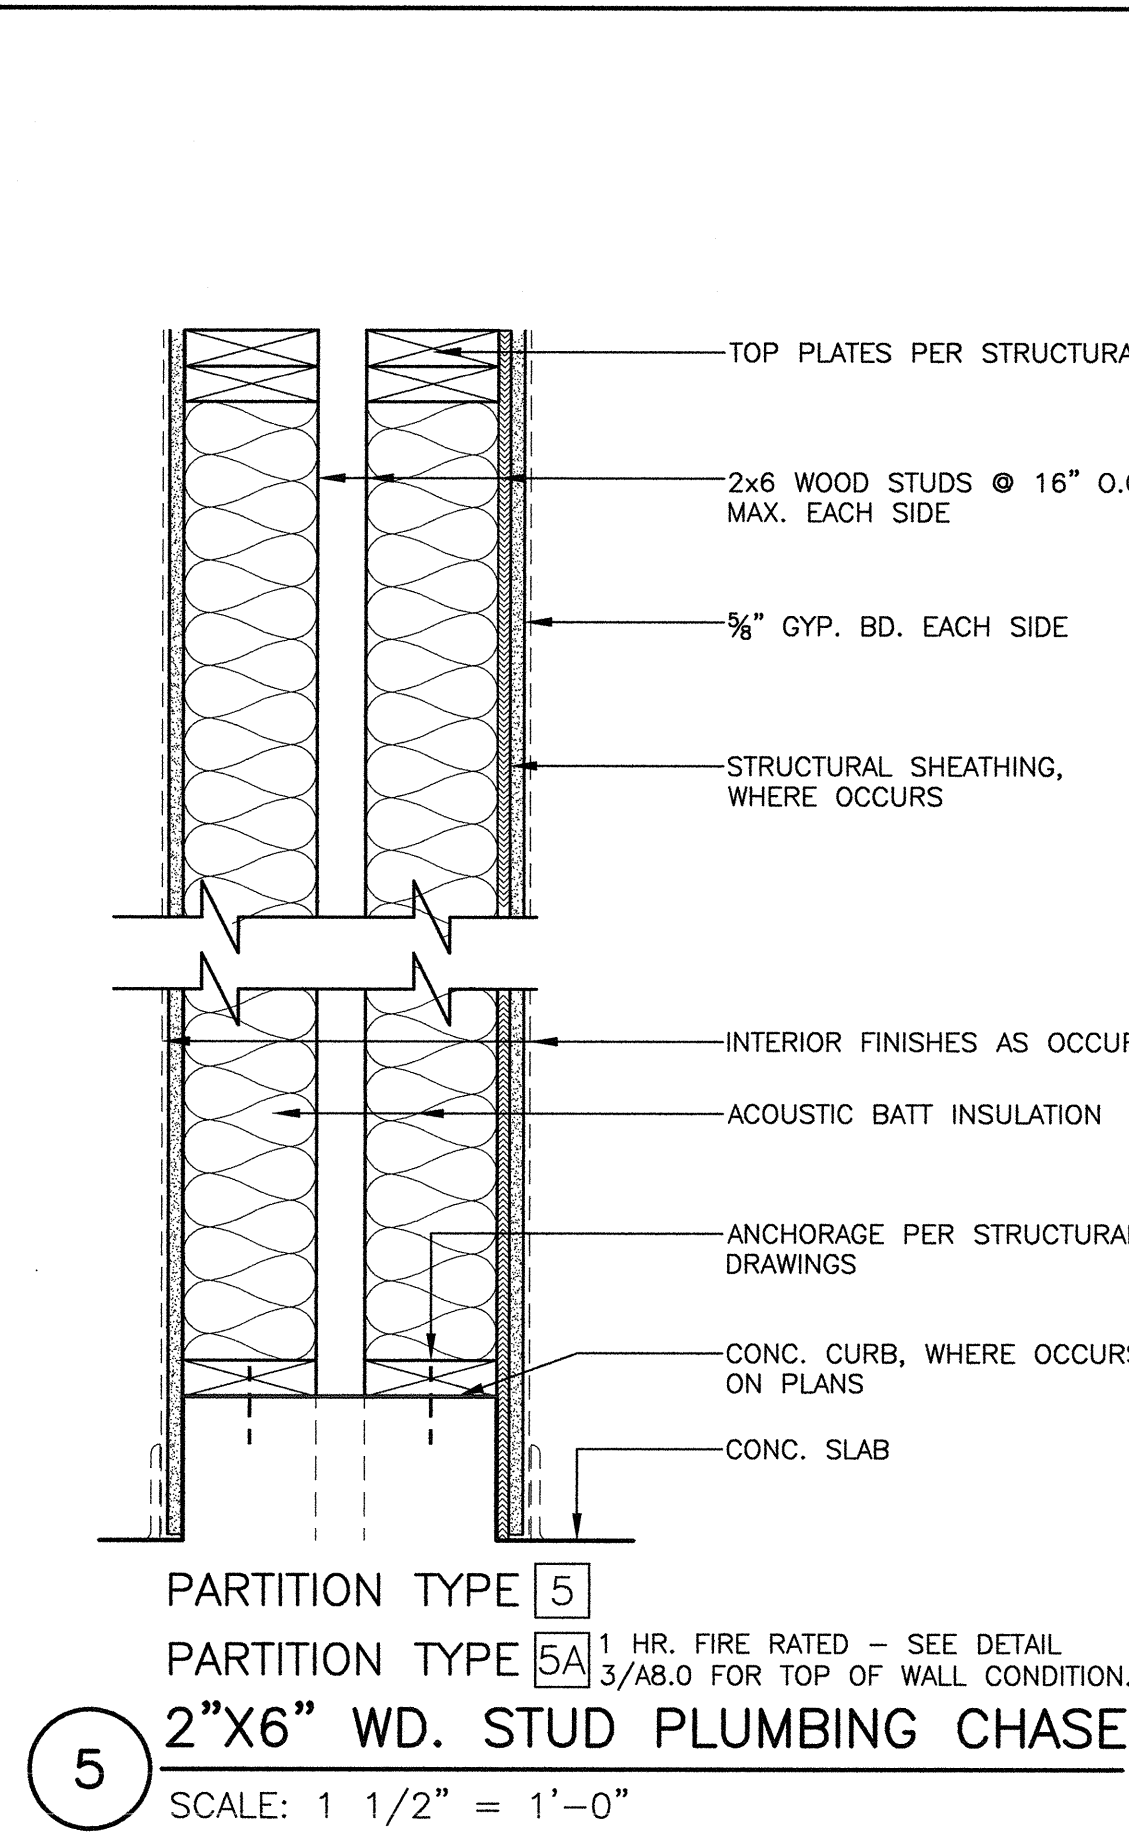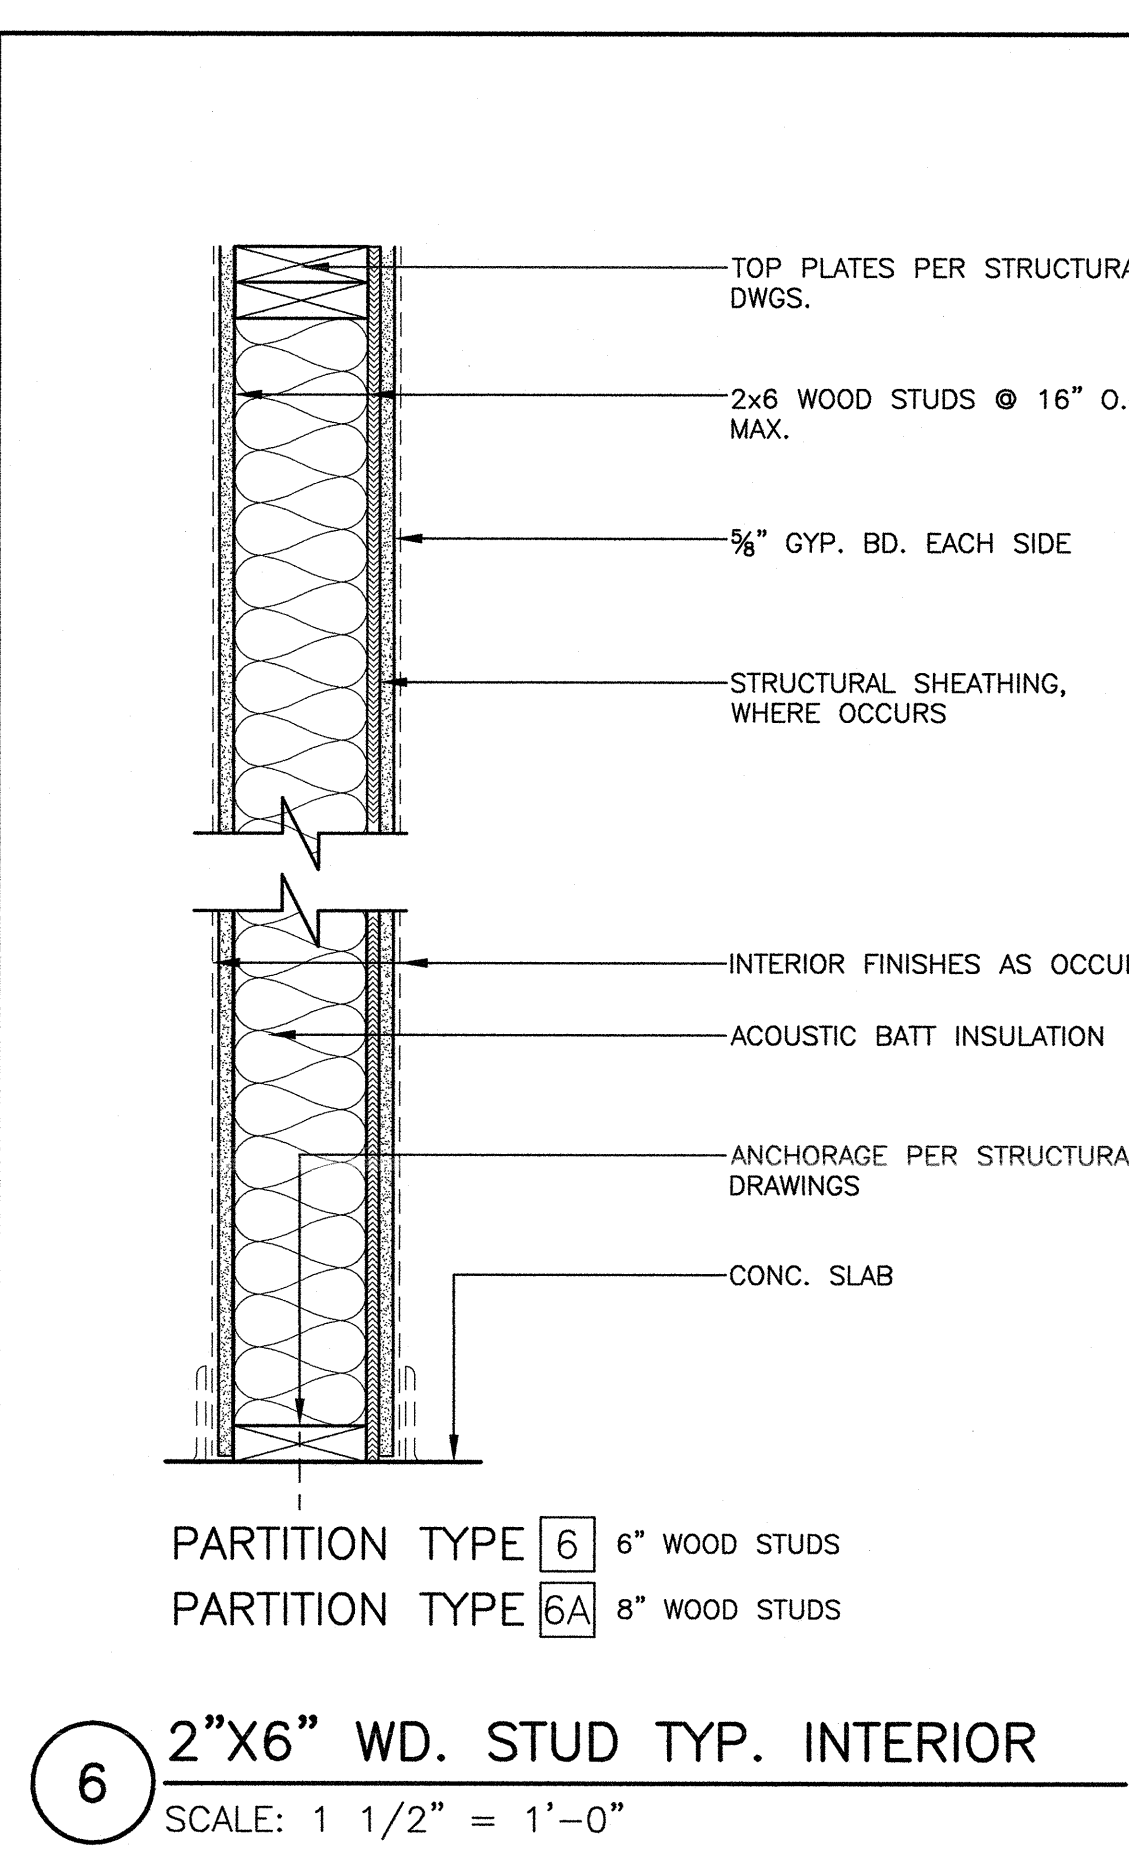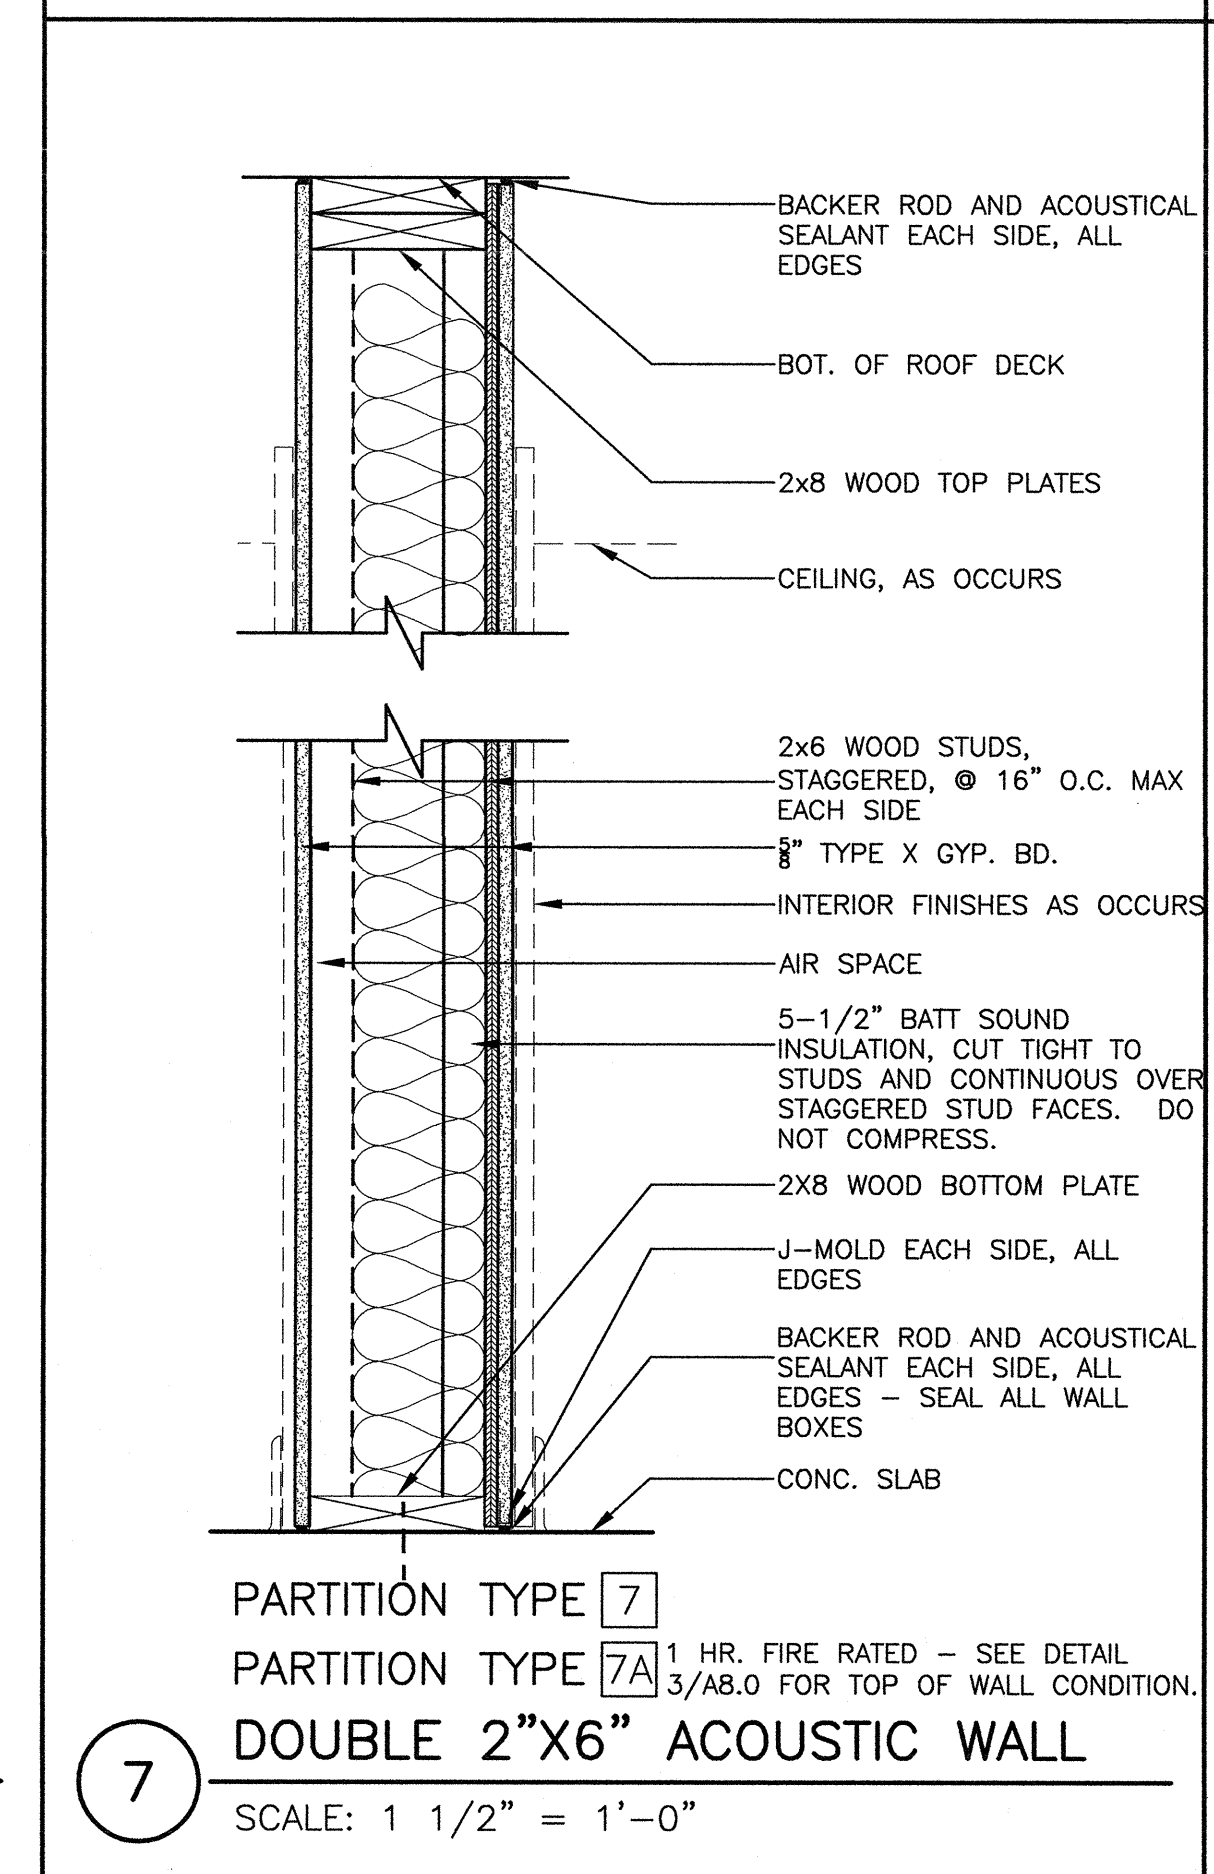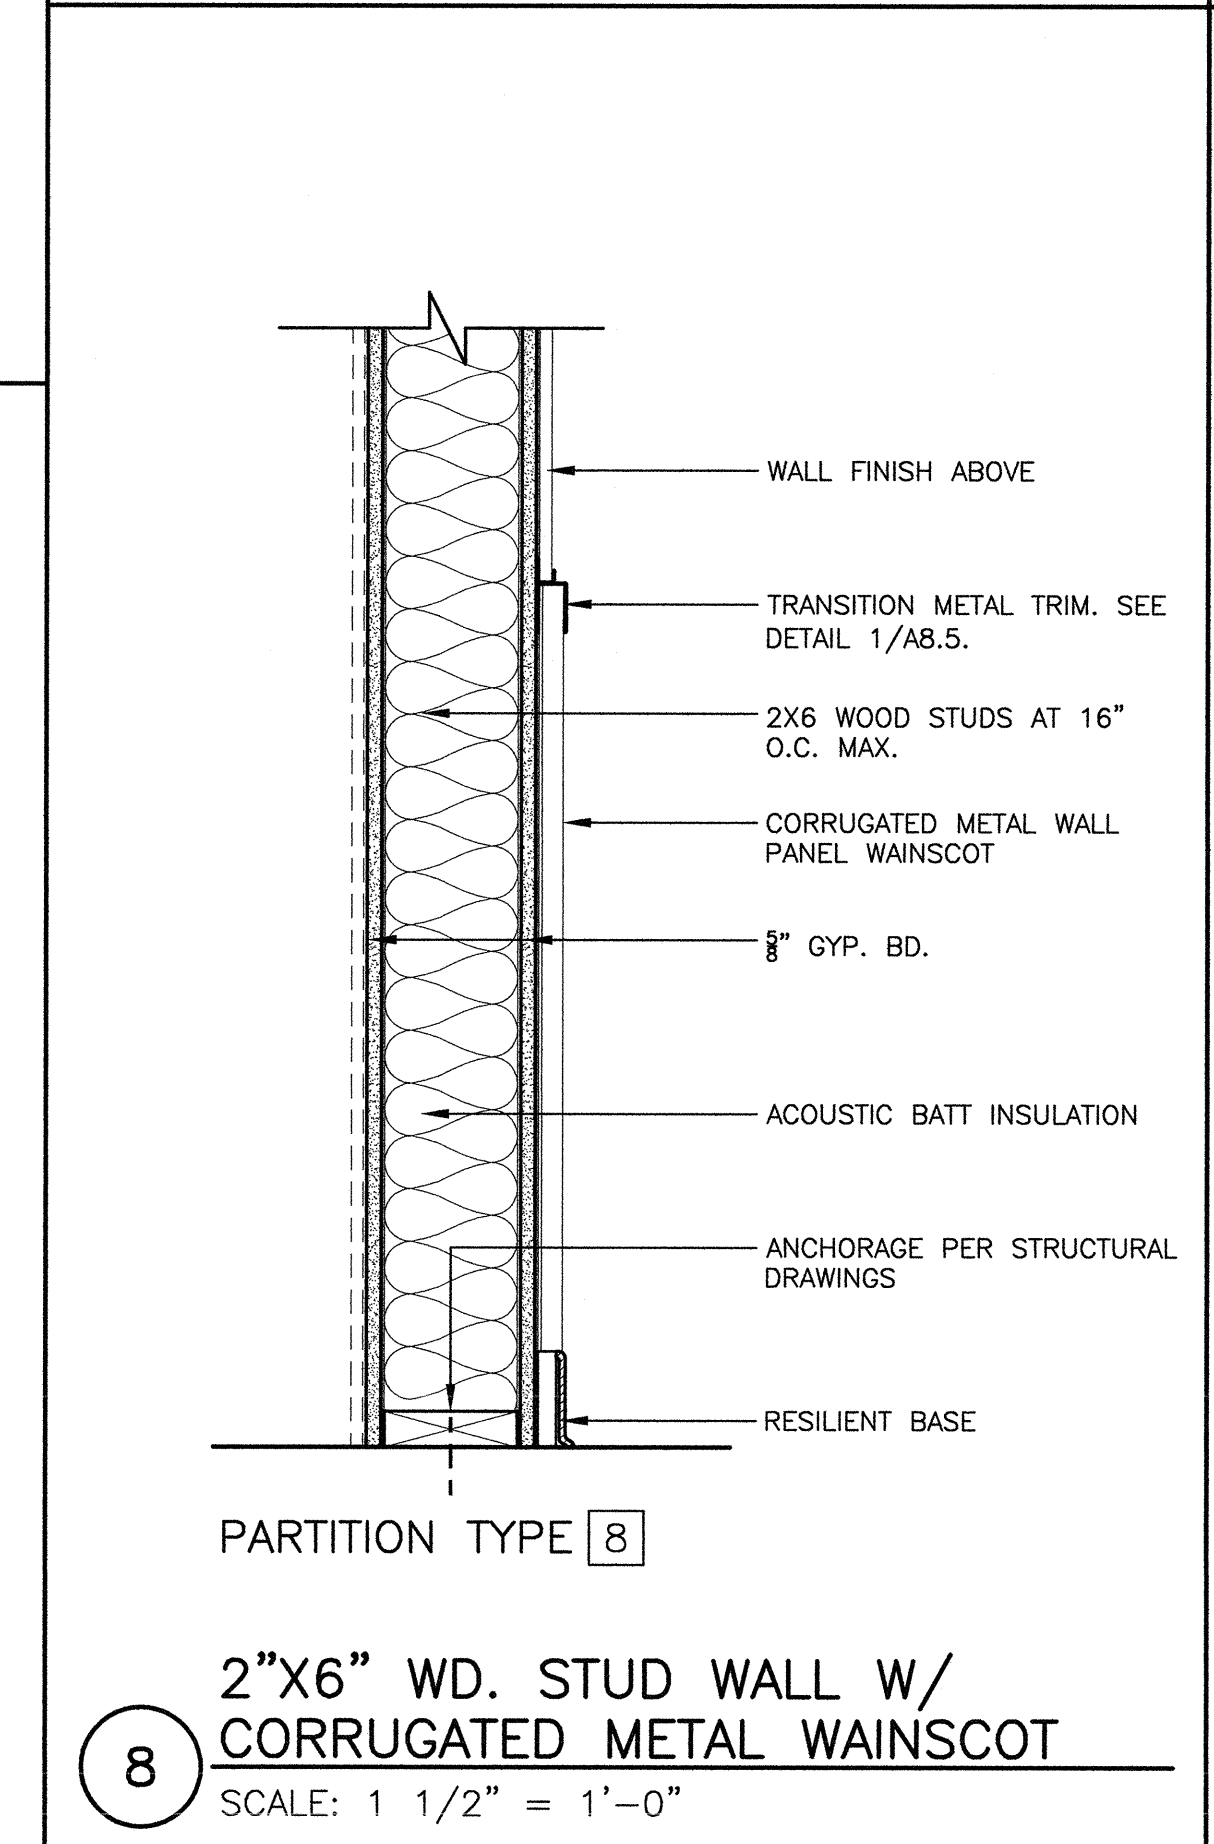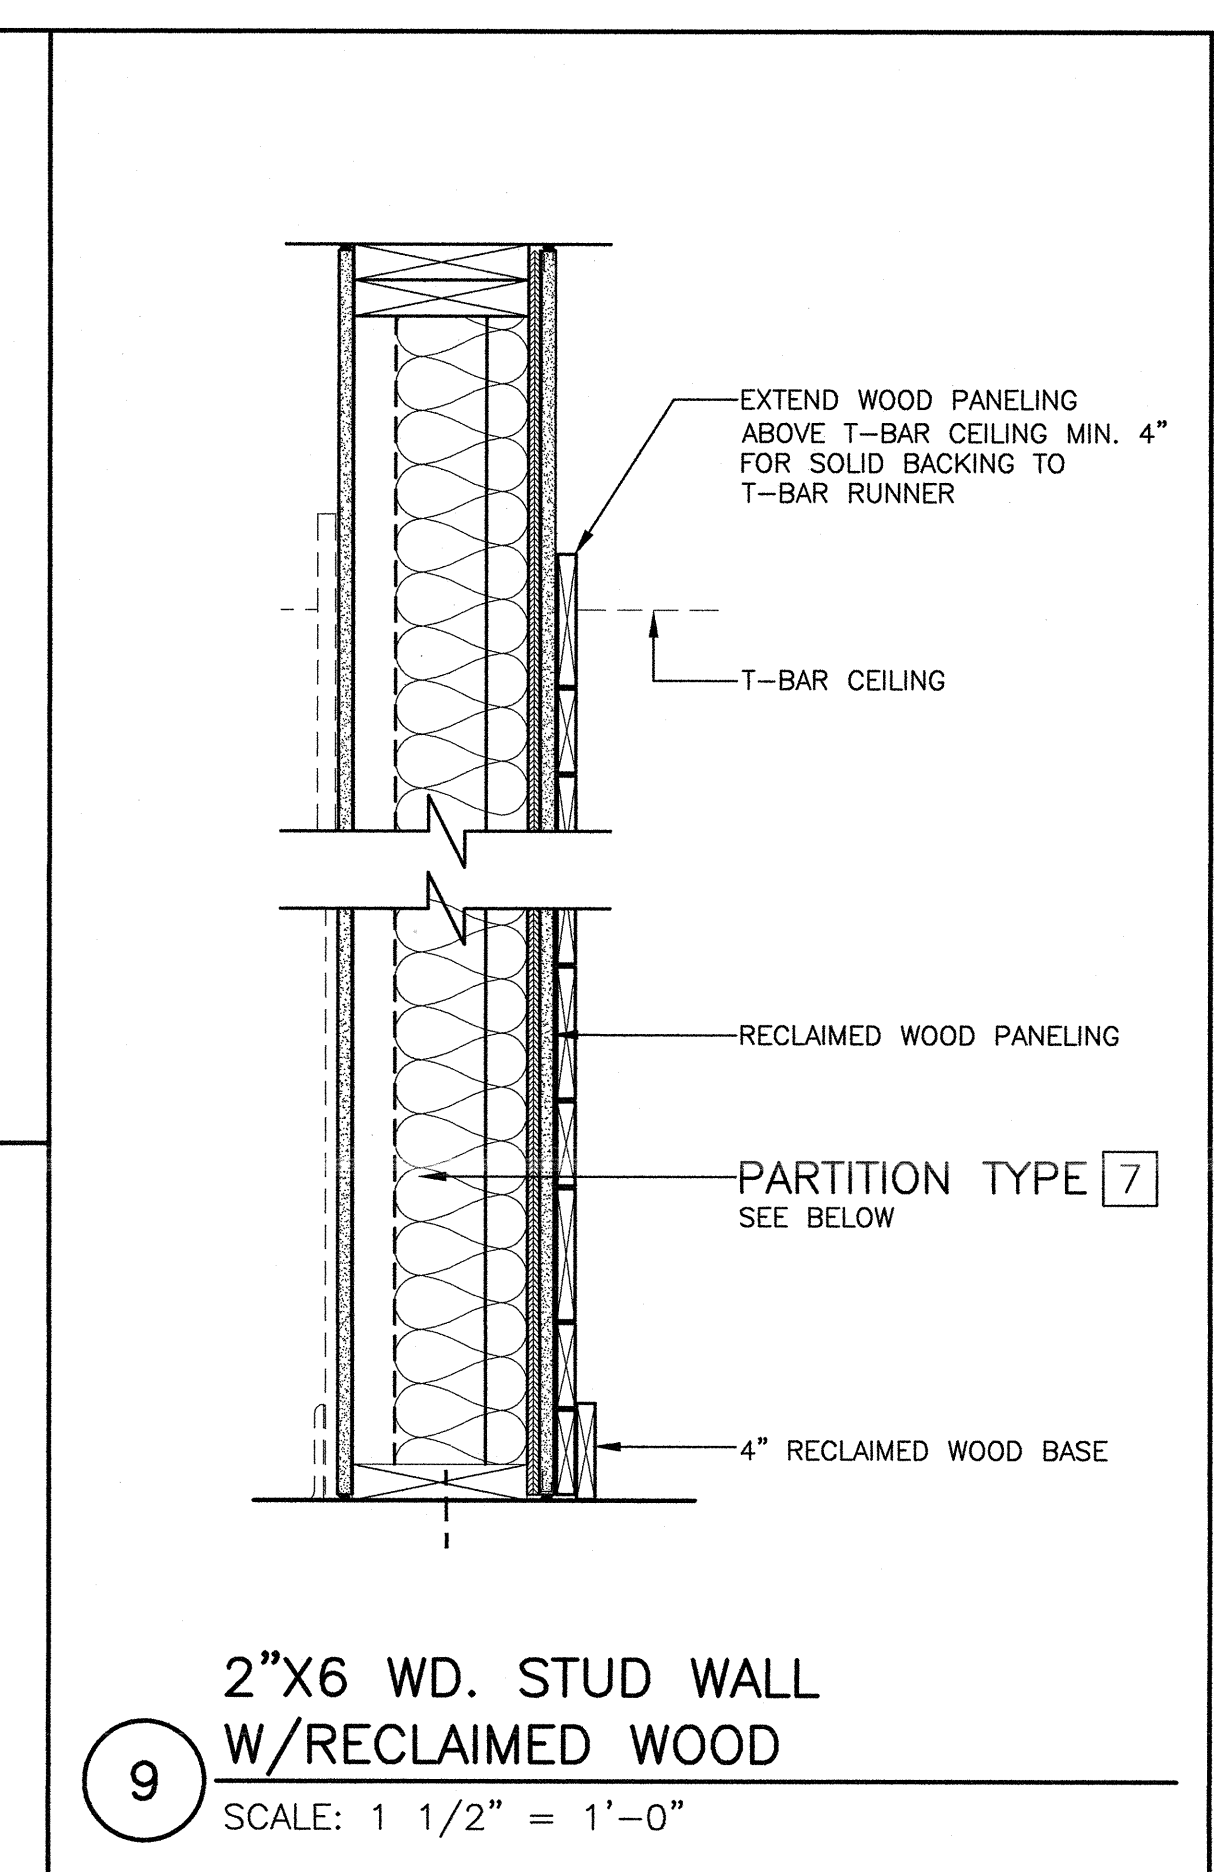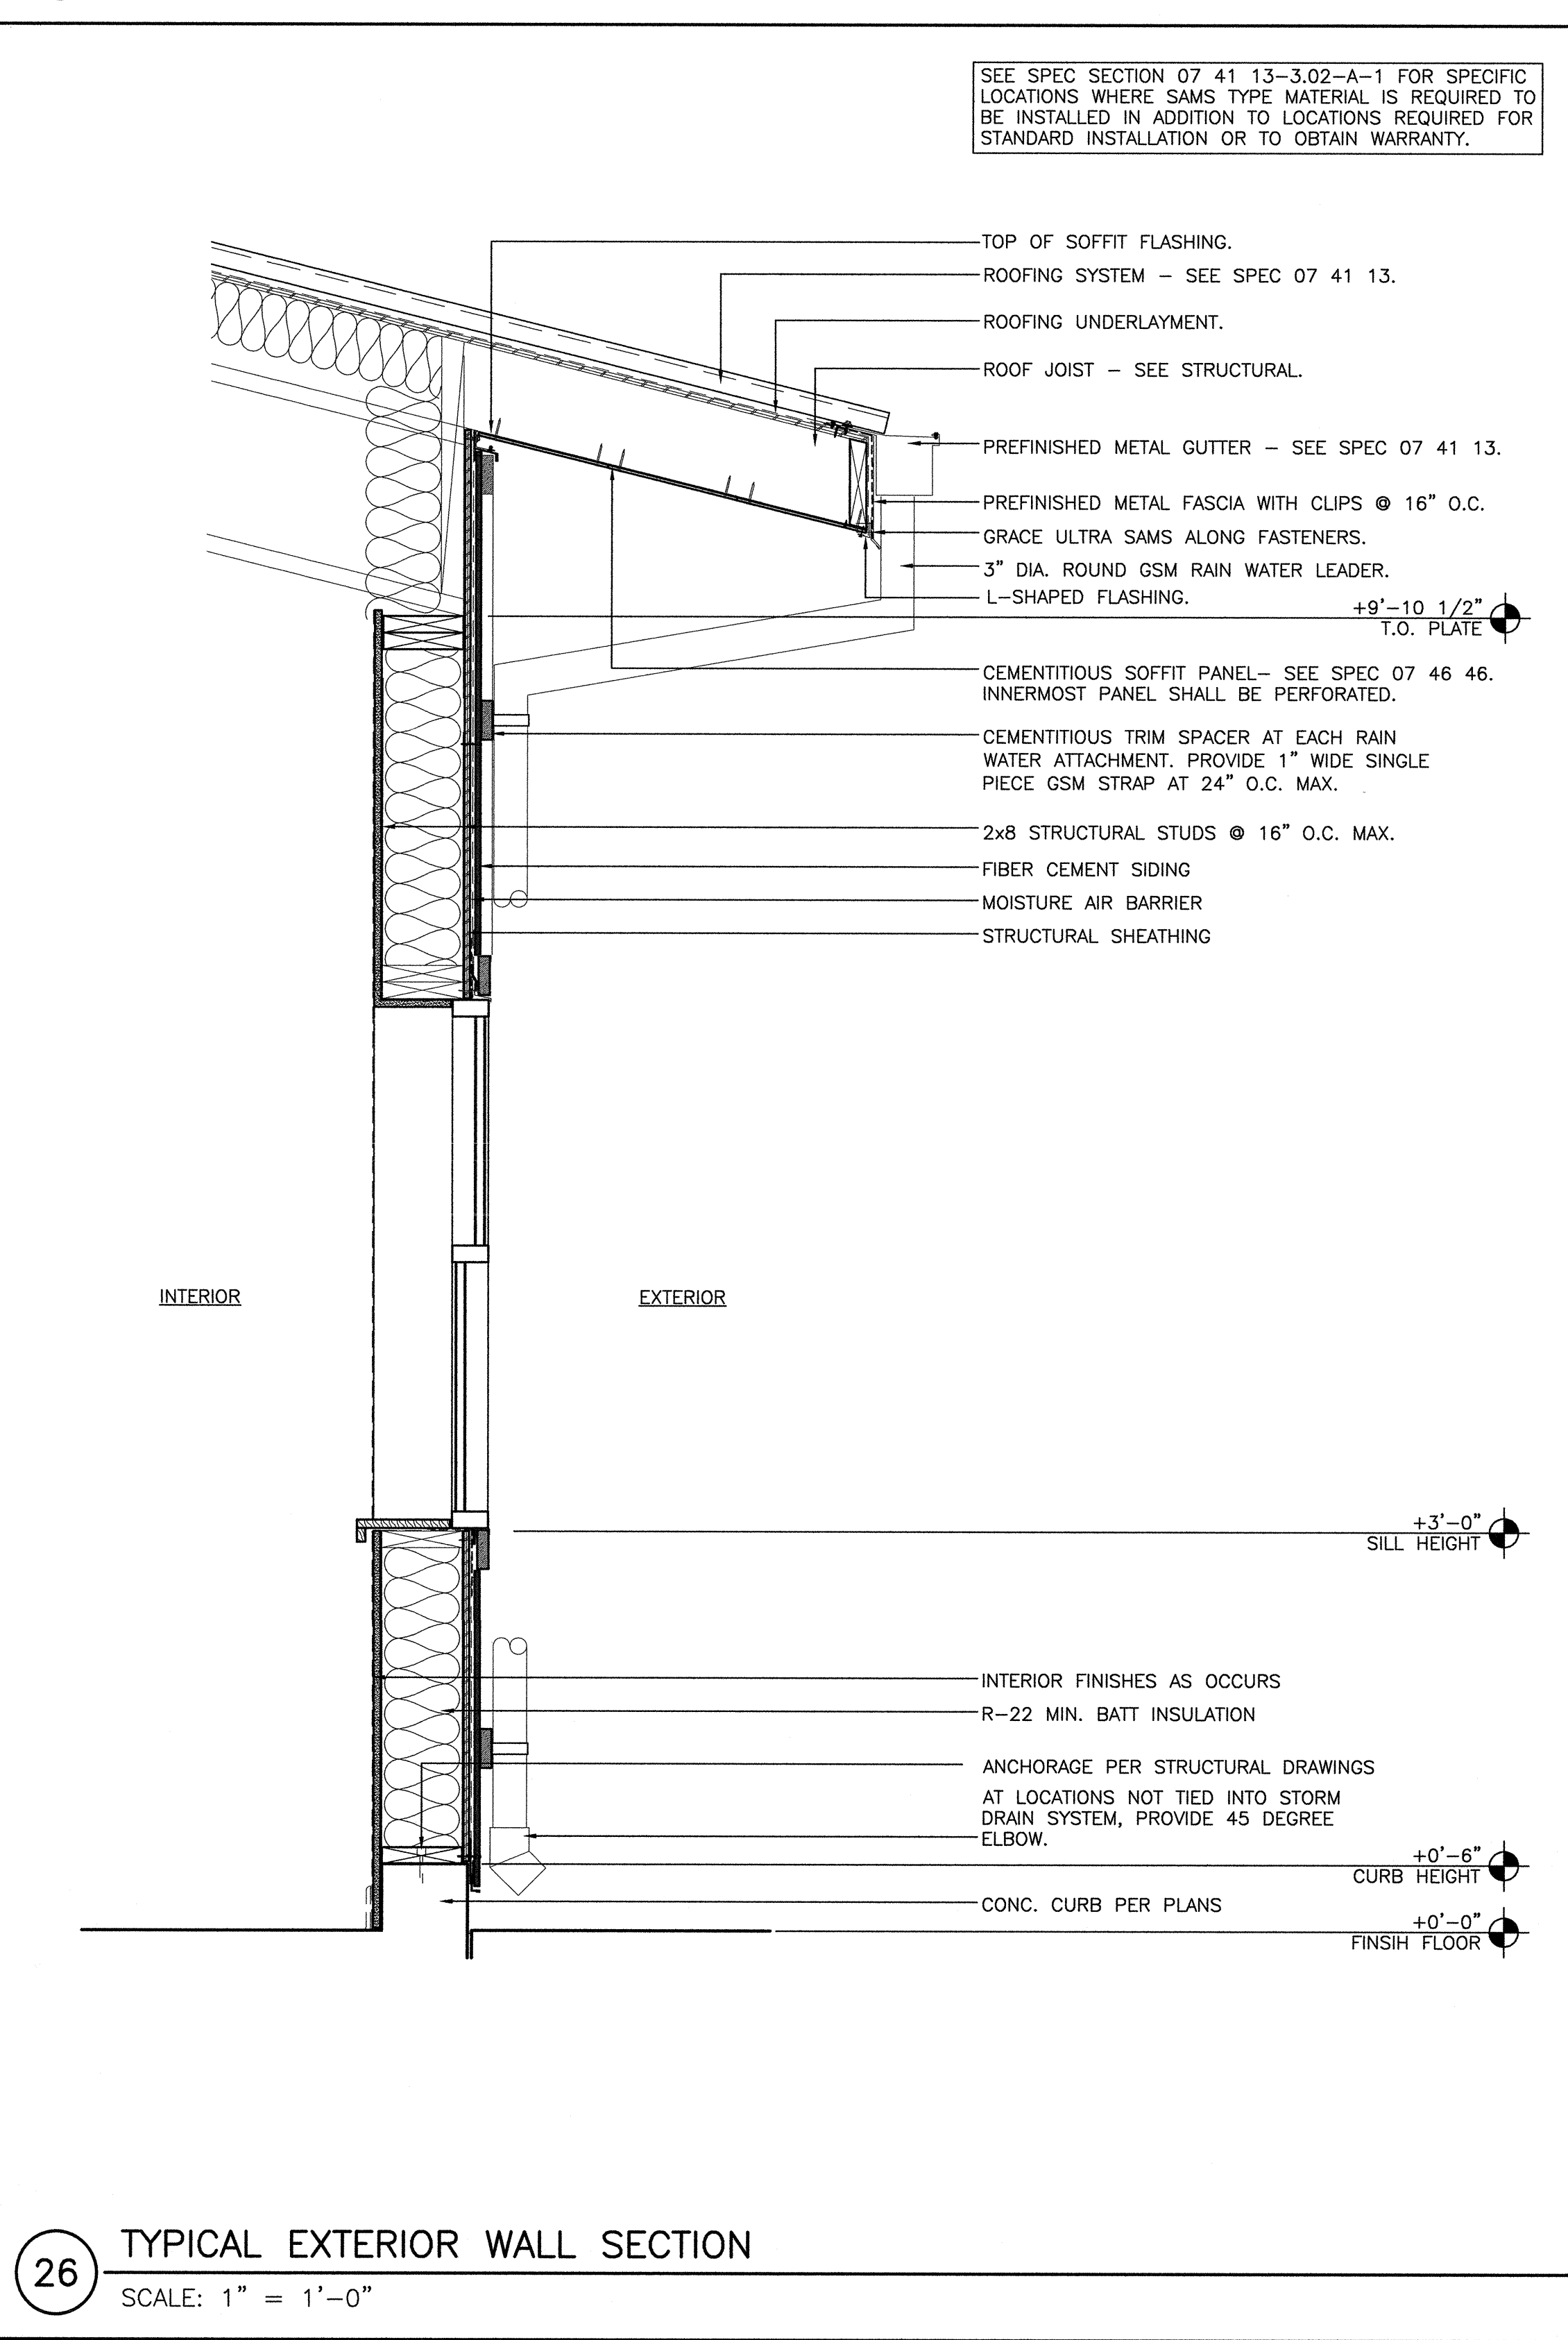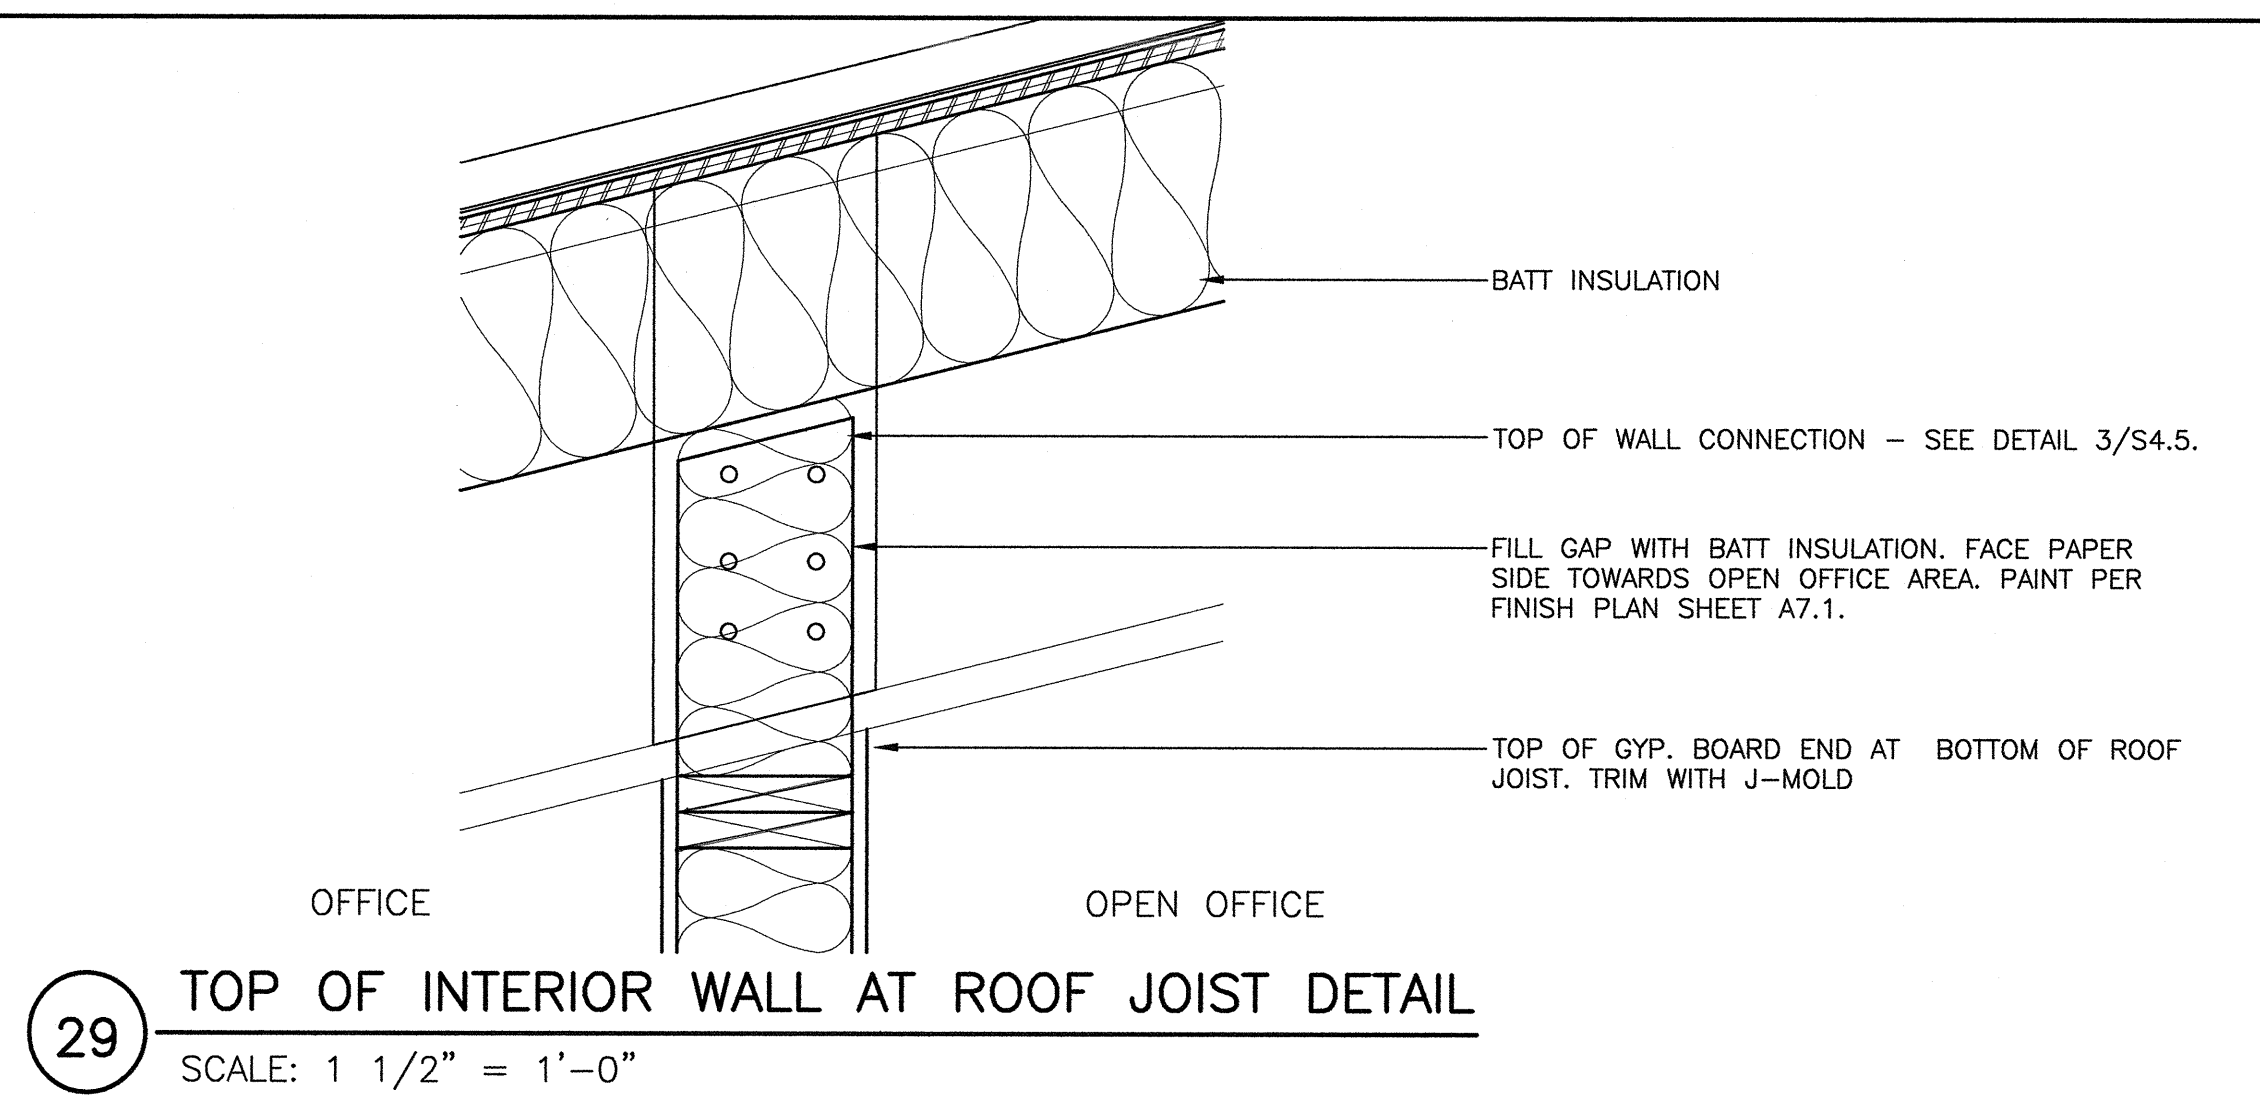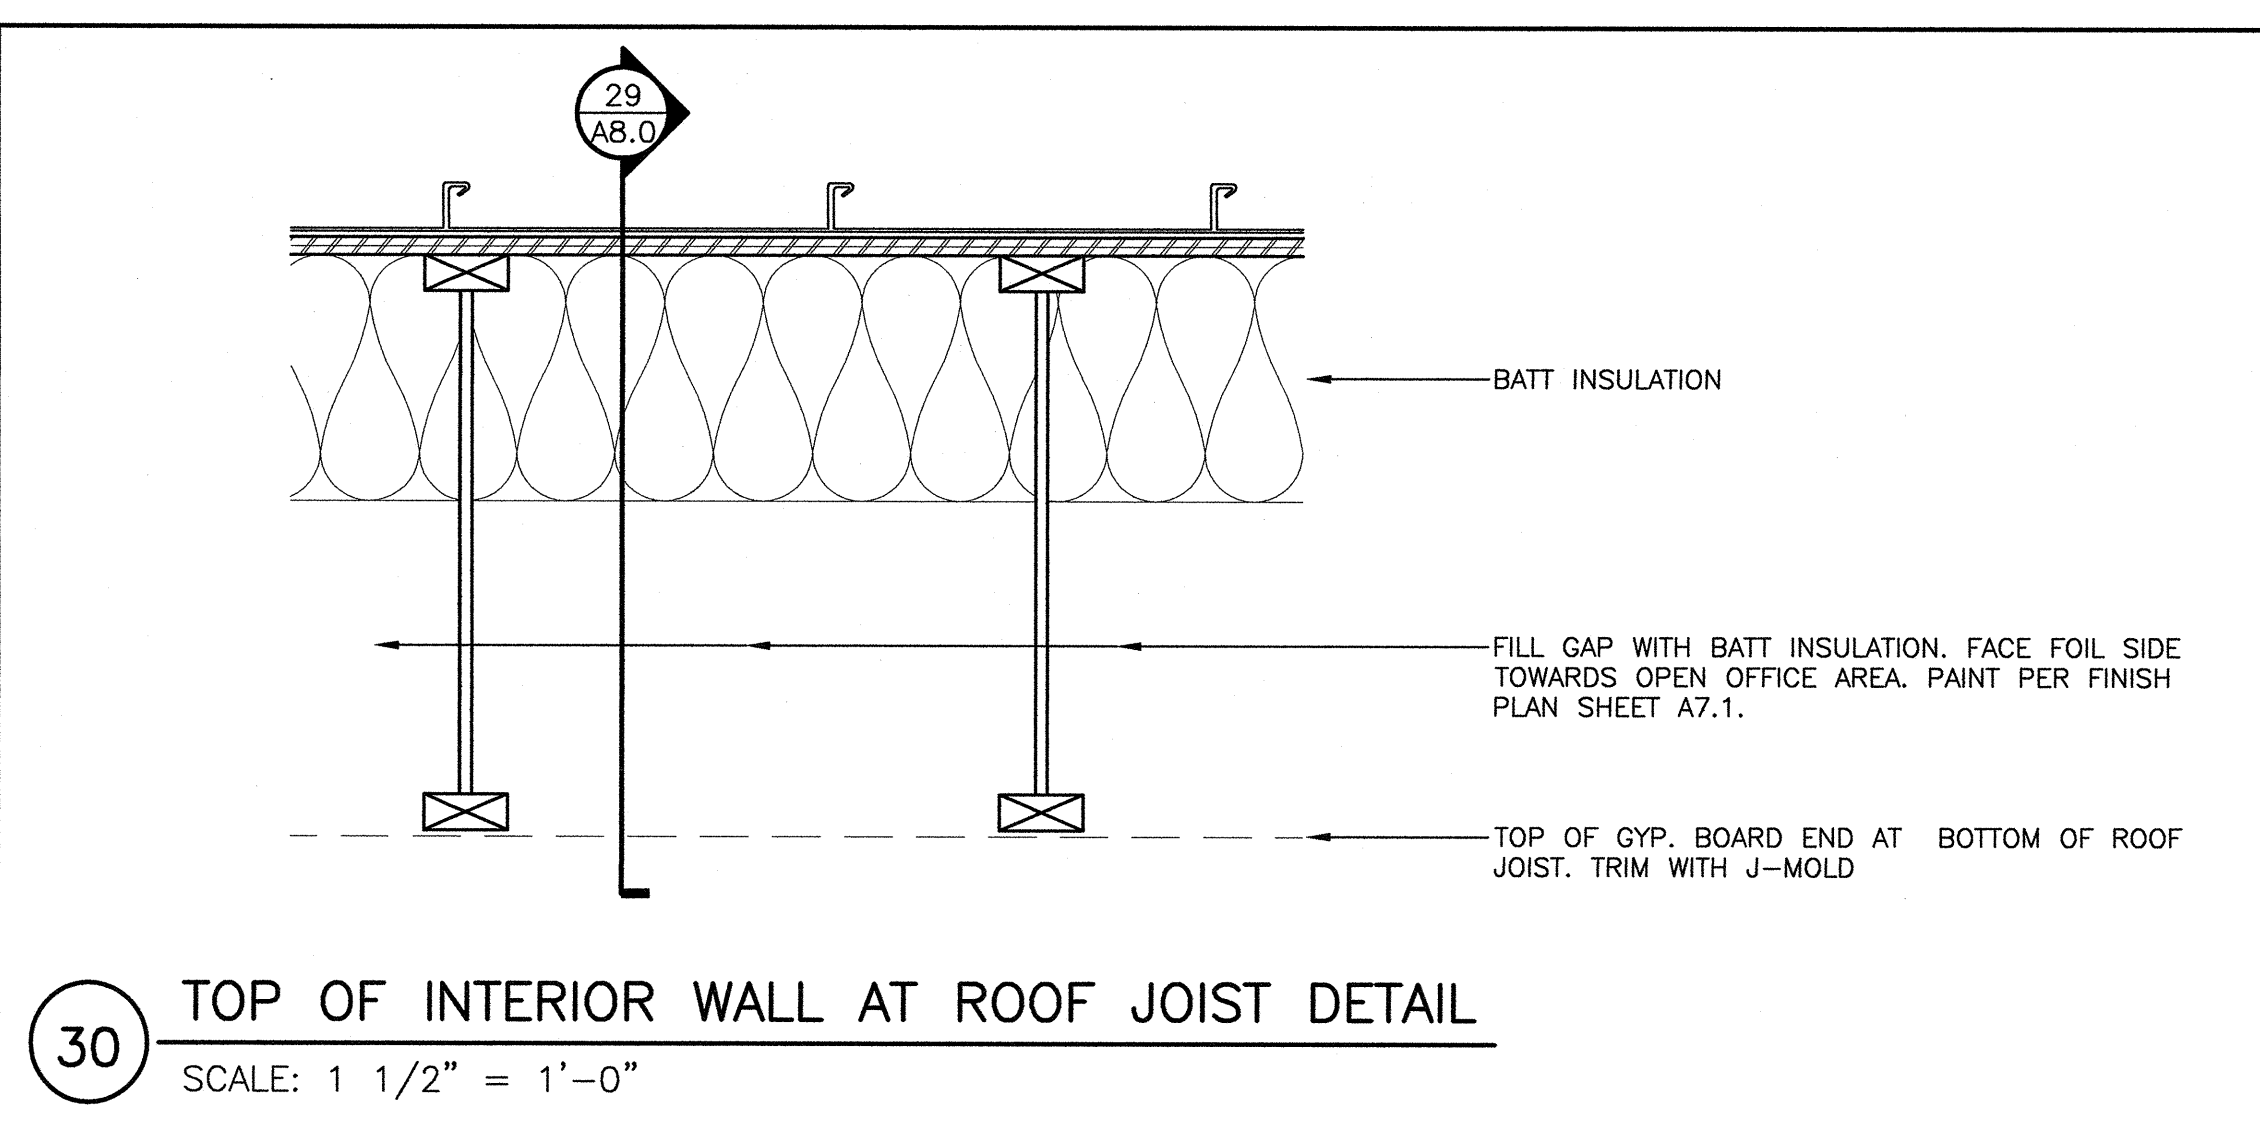

- GENERAL SHEET NOTES:**
- ALL PARTITIONS ARE FULL HEIGHT TO BOTTOM OF ROOF DECK UNLESS OTHERWISE NOTED.
 - ALL WALLS AND PARTITIONS SHALL HAVE GYP. BOARD FULL HEIGHT TO BOTTOM OF ROOF DECK UNLESS OTHERWISE NOTED.
 - ALL EXTERIOR WALLS SHALL HAVE THERMAL INSULATION PER SPECIFICATION SECTION 07 21 00 UNLESS OTHERWISE NOTED.
 - ALL INTERIOR PARTITIONS SHALL HAVE ACOUSTIC BATT INSULATION PER SPECIFICATION SECTION 07 21 00.
 - ALL ACOUSTIC BATT INSULATION AT PARTITIONS SHALL EXTEND FULL HEIGHT TO ROOF DECK, UNLESS OTHERWISE NOTED.
 - FOR SHEAR WALL CONDITIONS AND WALL SHEATHING REQUIREMENTS, SEE FOUNDATION AND SHEAR WALL DIAGRAM, SHEET S2.1.
 - PROVIDE FIRE BLOCKING AT ALL INTERIOR AND EXTERIOR WALLS IN ACCORDANCE WITH CBC CHAPTER 718. AT A MINIMUM, PROVIDE 2X LUMBER AT EACH STUD BAY PLACED TIGHTLY BETWEEN VERTICAL FRAMING MEMBERS. ROWS OF BLOCKING SHALL BE SPACED VERTICALLY AT 10'-0" O.C. MAXIMUM.
 - AT ALL CHASE WALLS, IN ADDITION TO 2X LUMBER, PROVIDE LAYERS OF BATT INSULATION PER CBC 718.2.1.5 SPANNING ACROSS GAP BETWEEN WALLS.


Dry Creek Joint Elementary School District
District Education Center
8849 Cook Riolo Road, Roseville, CA 95747
Dry Creek Joint Elementary School District

FILE NO. 31-15
IDENTIFICATION STAMP DIV. OF THE
STATE ARCHITECT OFFICE OF
REGULATION SERVICES
APPLICATION NO. 02-115456
AC. TIM FLS WMC SS JLP
DATE 4/24/19 CJA

DIVISION OF THE STATE ARCHITECT
revision date: by:

CONSULTANT

nacht&lewis
600 O Street, Suite 100
Sacramento, CA 95811
www.nachtandlewis.com
916.329.4000

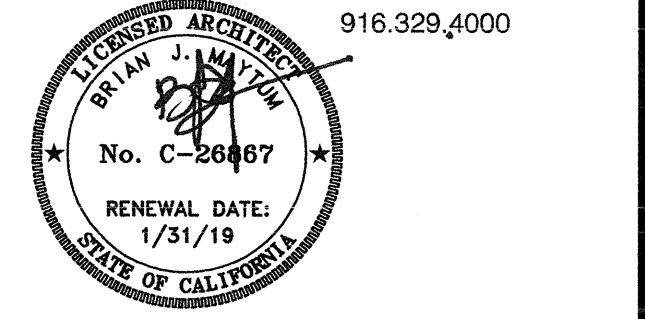

ARCHITECT



INITIAL BOX			
NO.	DWG BY	DATE	REVIEWED

REVISIONS			
NO.	DESCRIPTION	DATE	REV'D
	100% design development	1/26/19	
	75% construction documents	9/22/19	
	DSA submittal	12/31/19	
	DSA approval	02/23/17	

DATE February 23, 2017
JOB NO. Y1538.00
SHEET TITLE

Wall Types
and
Details

SHEET NO.
A8.0
SHEET ___ OF ___ TOTAL

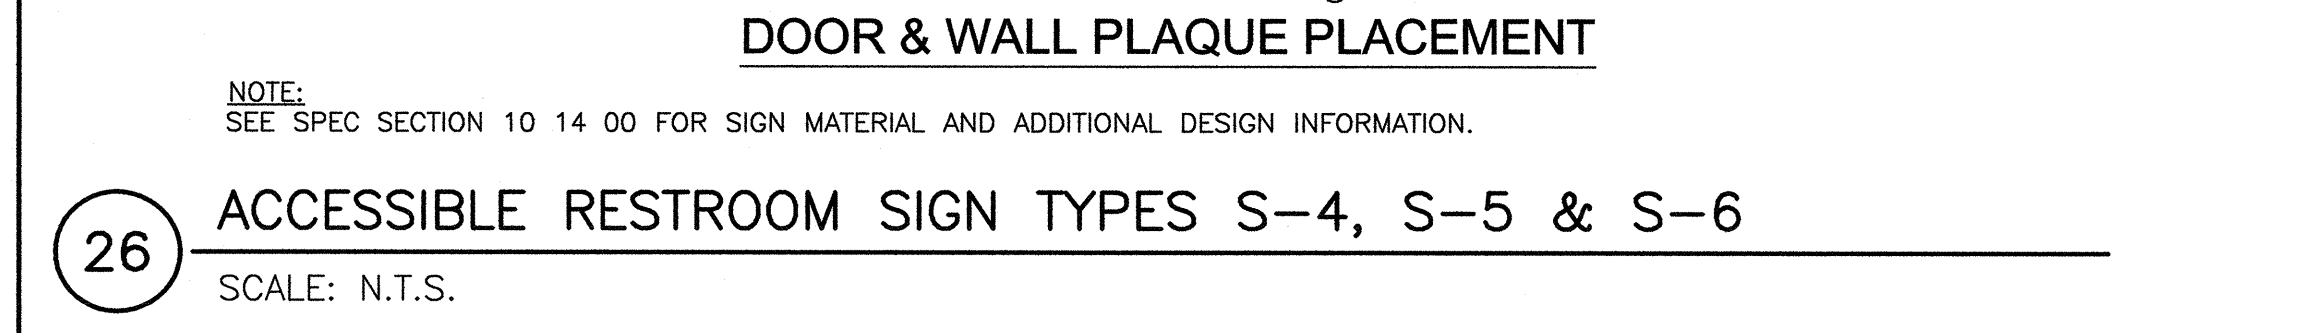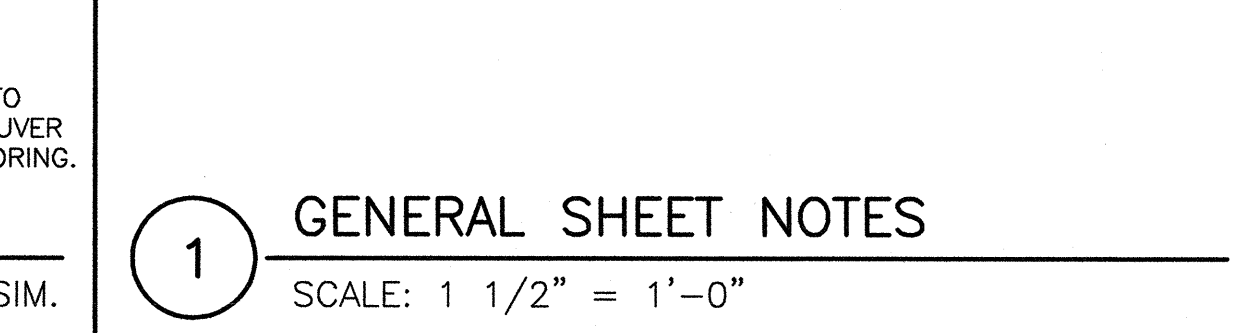

ONE INCH = TWENTY

