

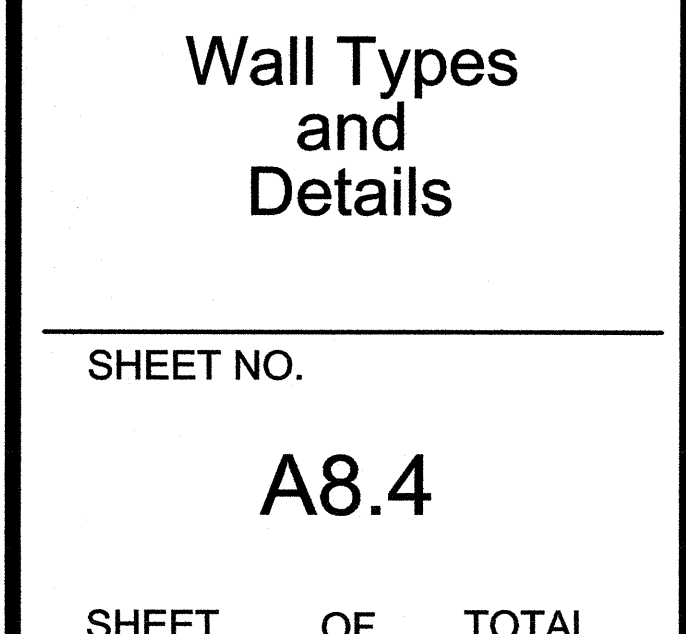
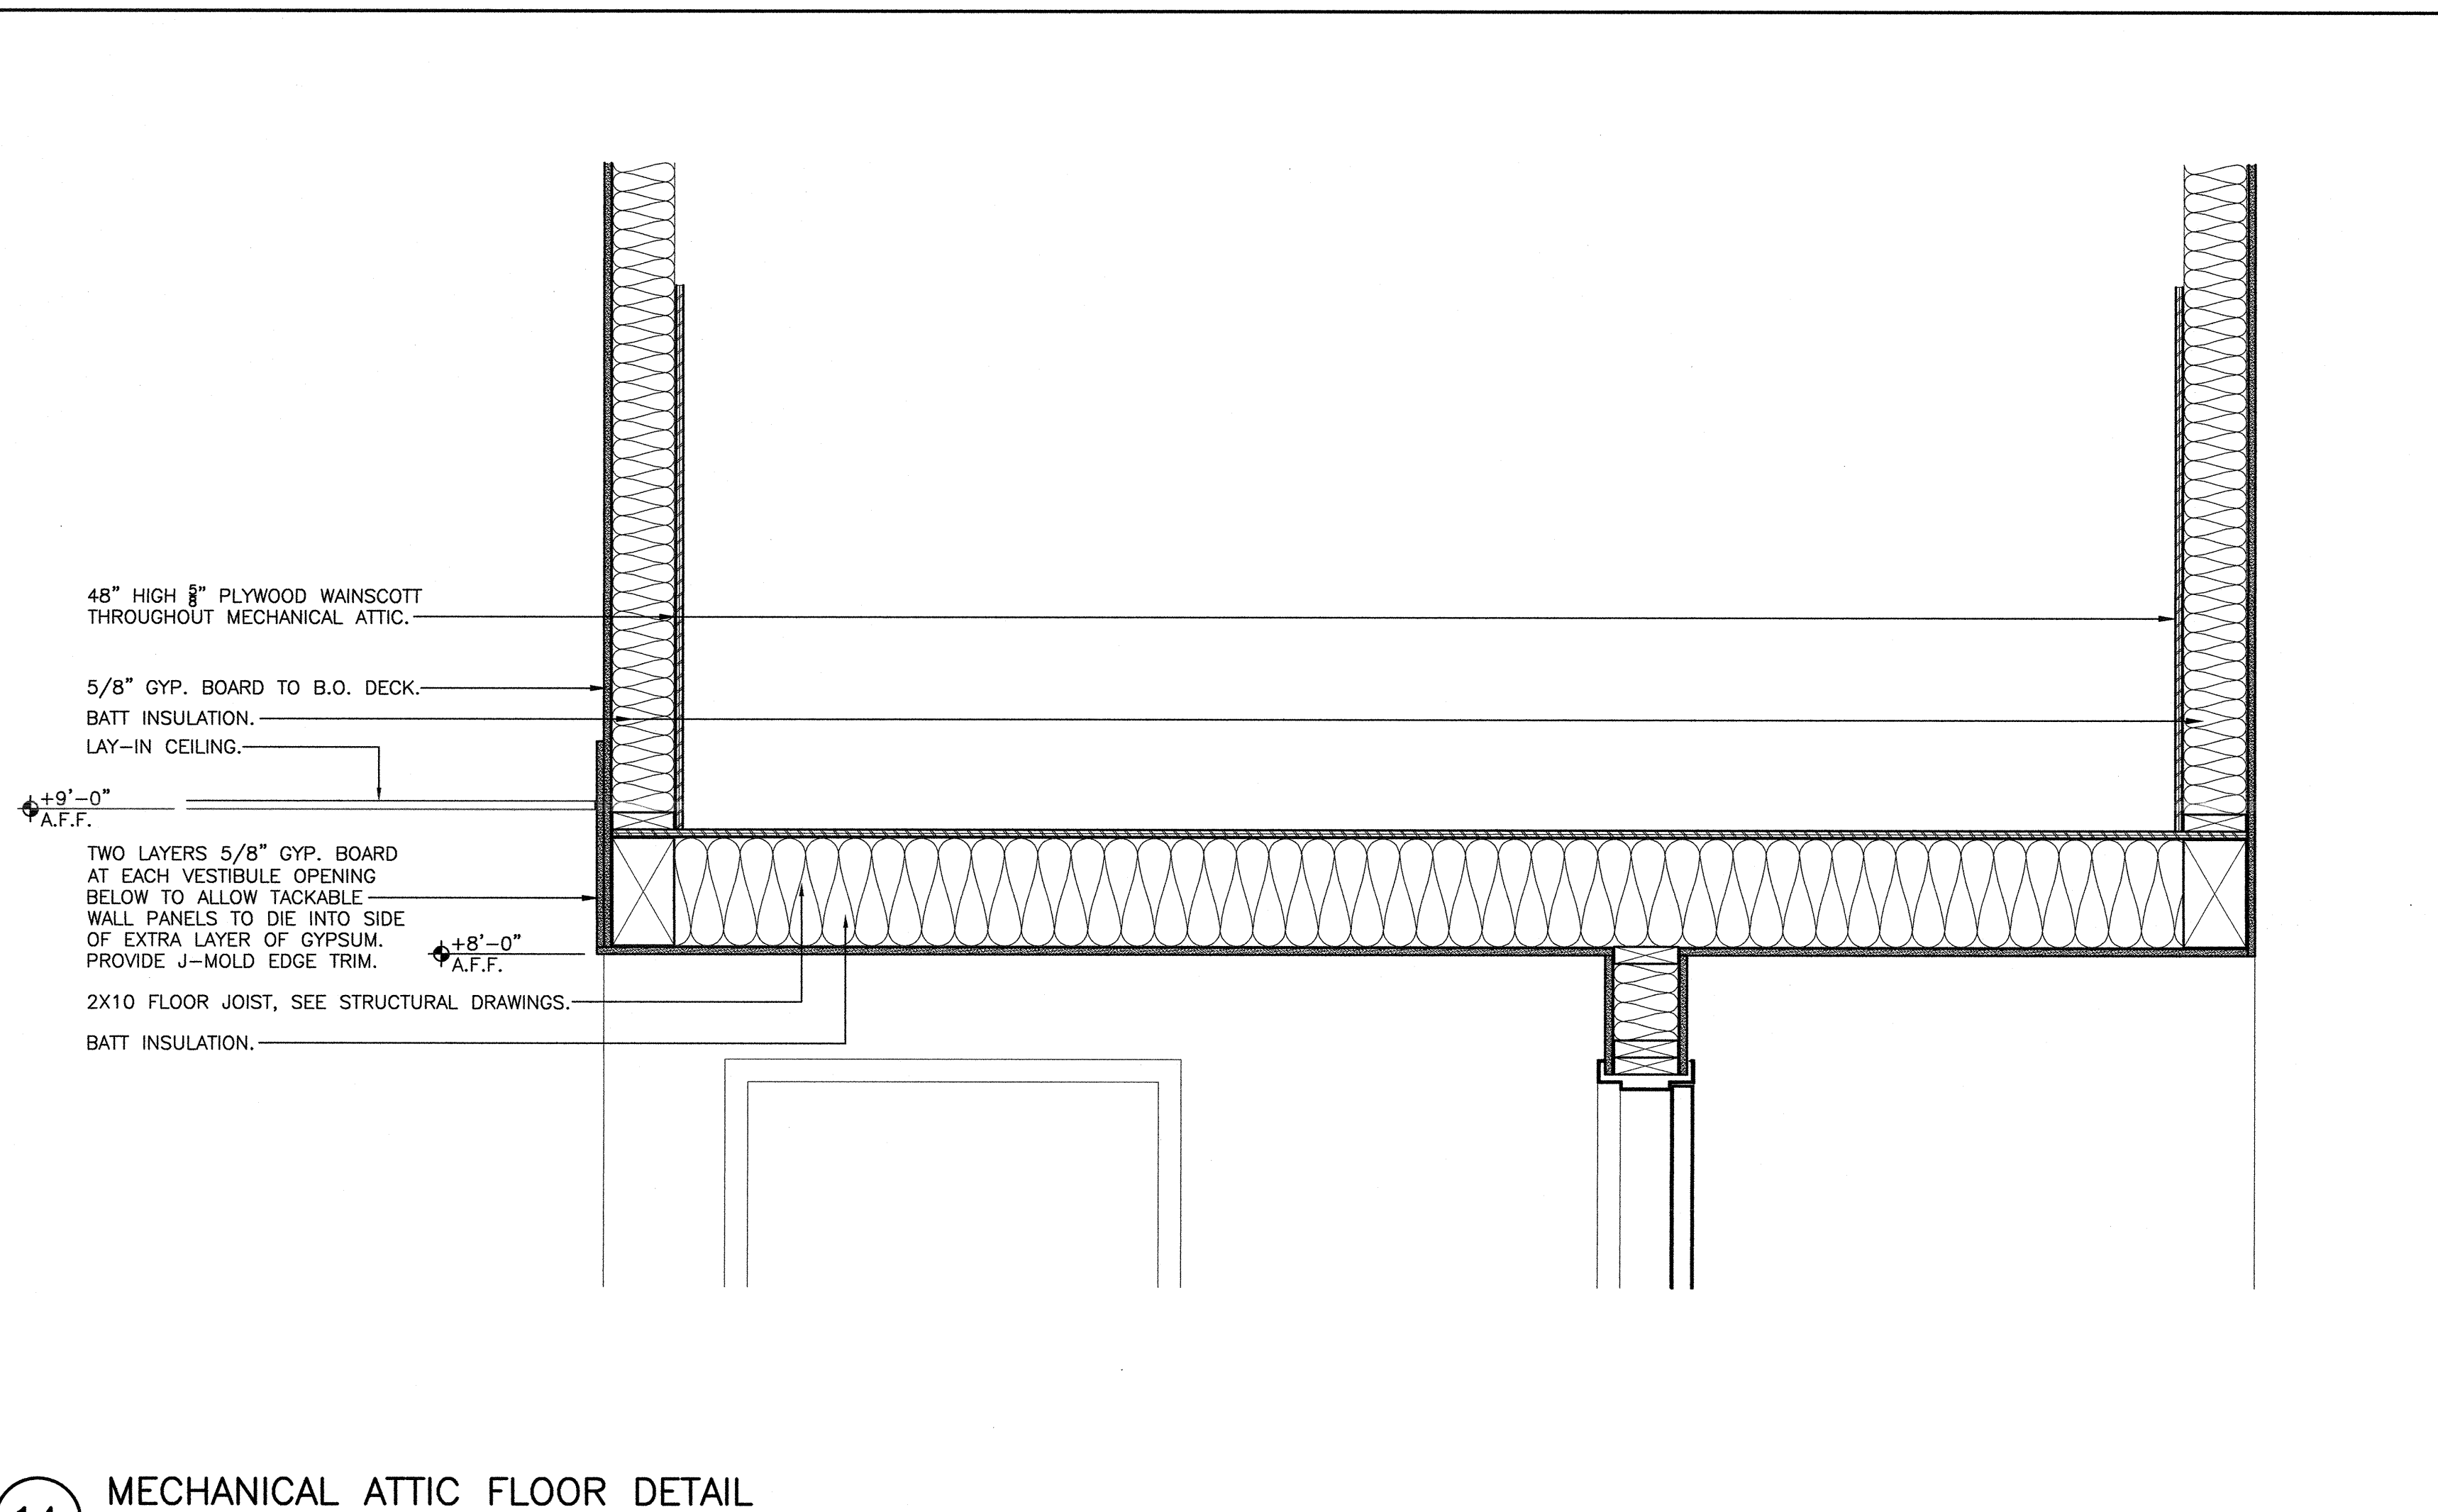
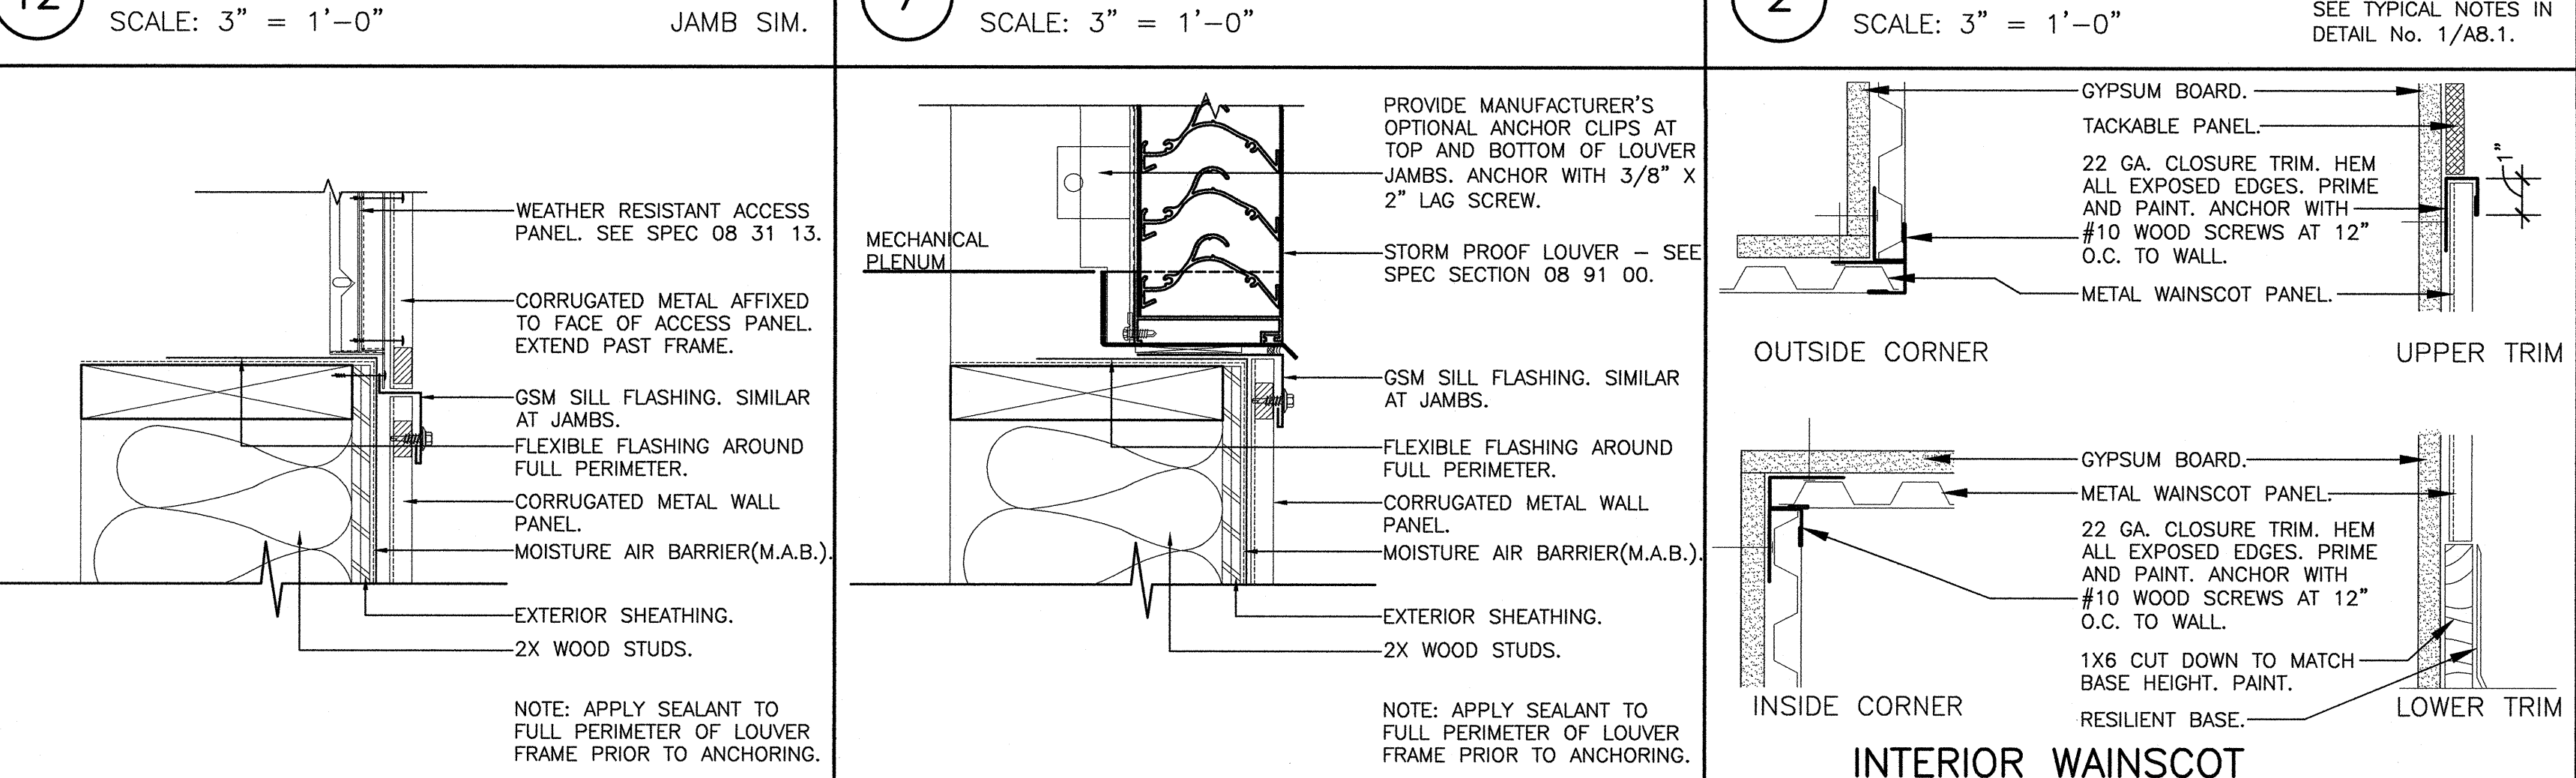
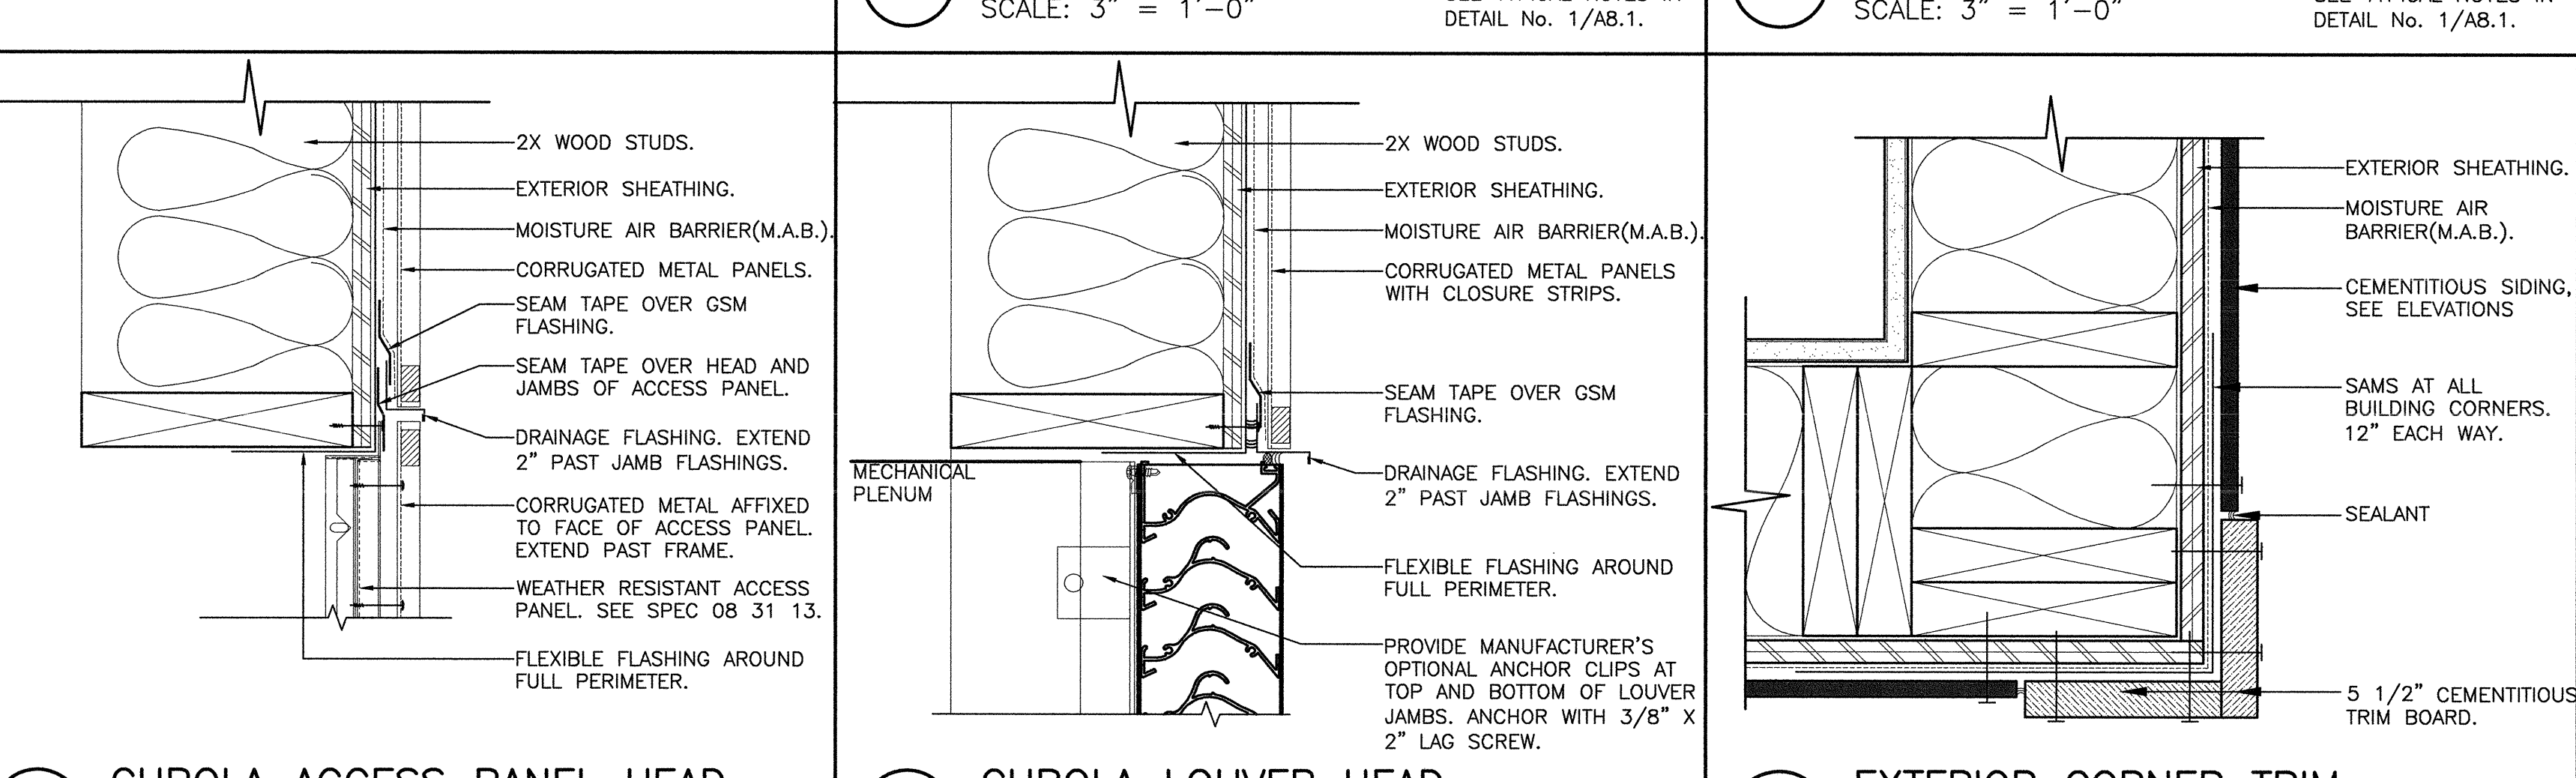
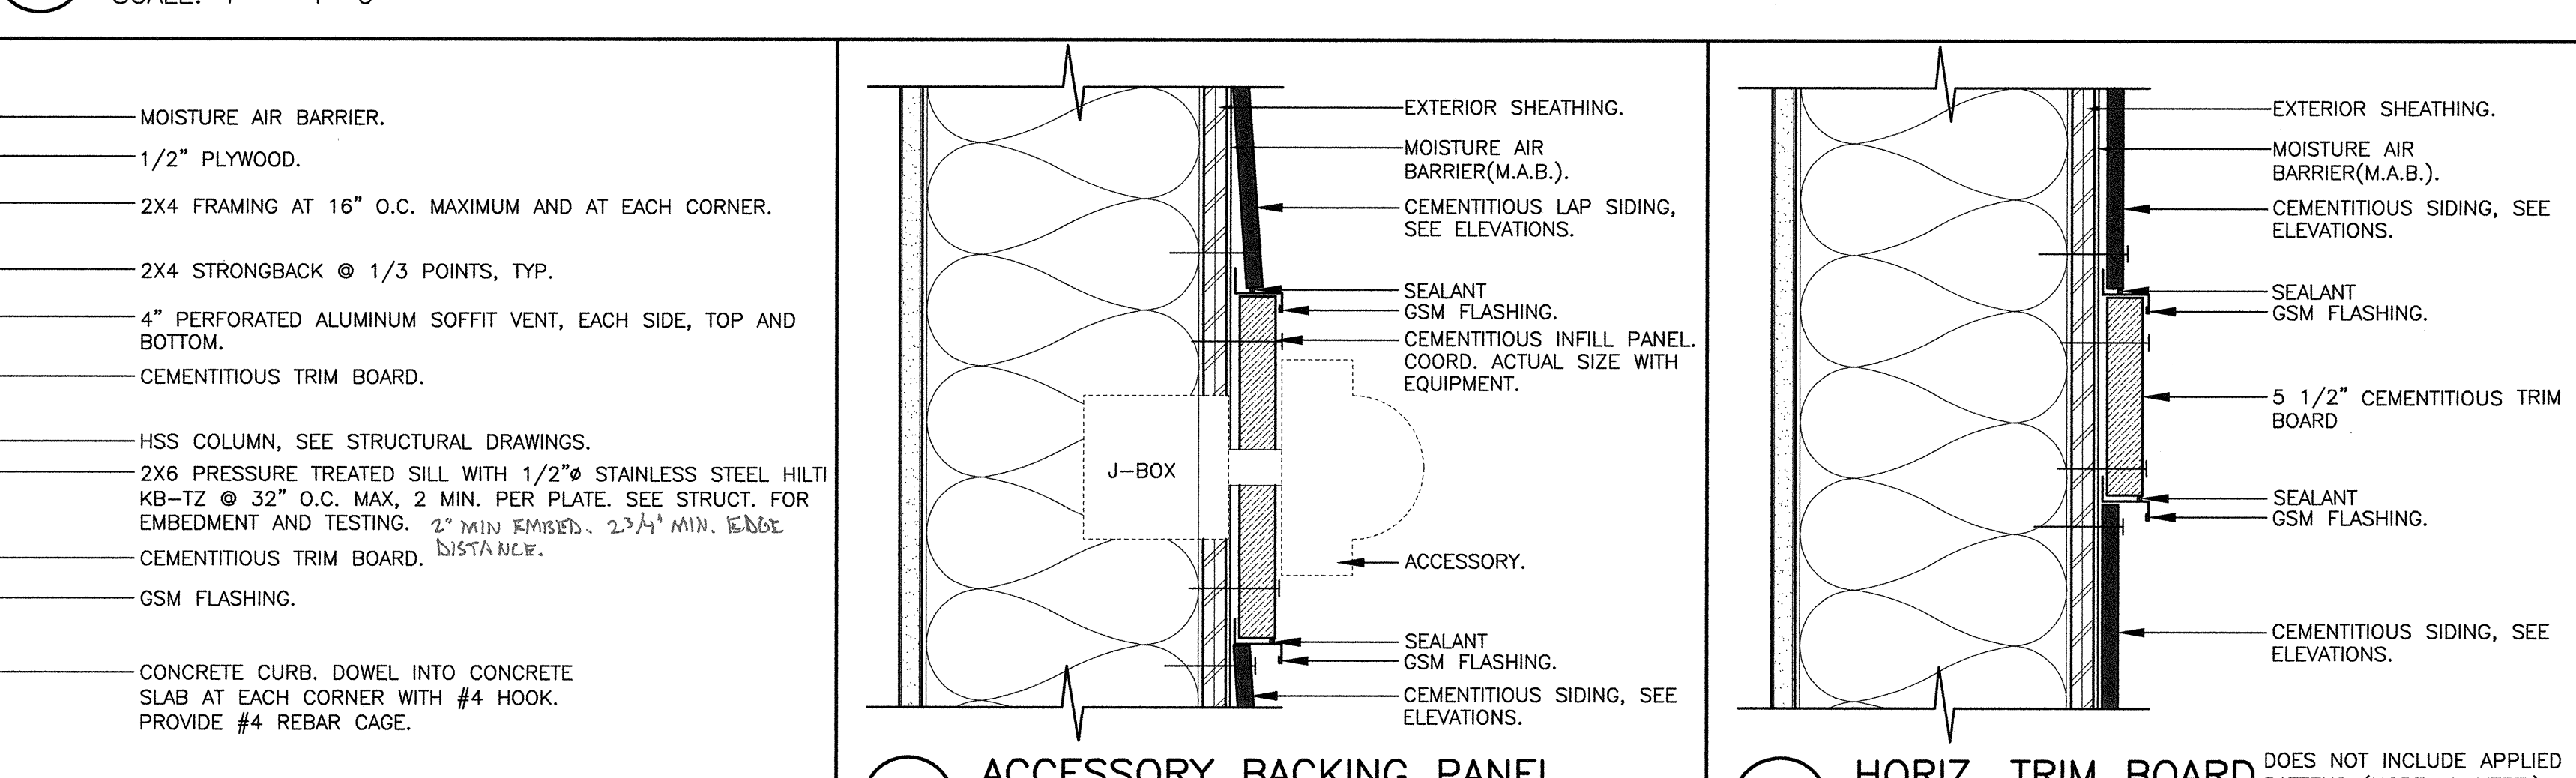
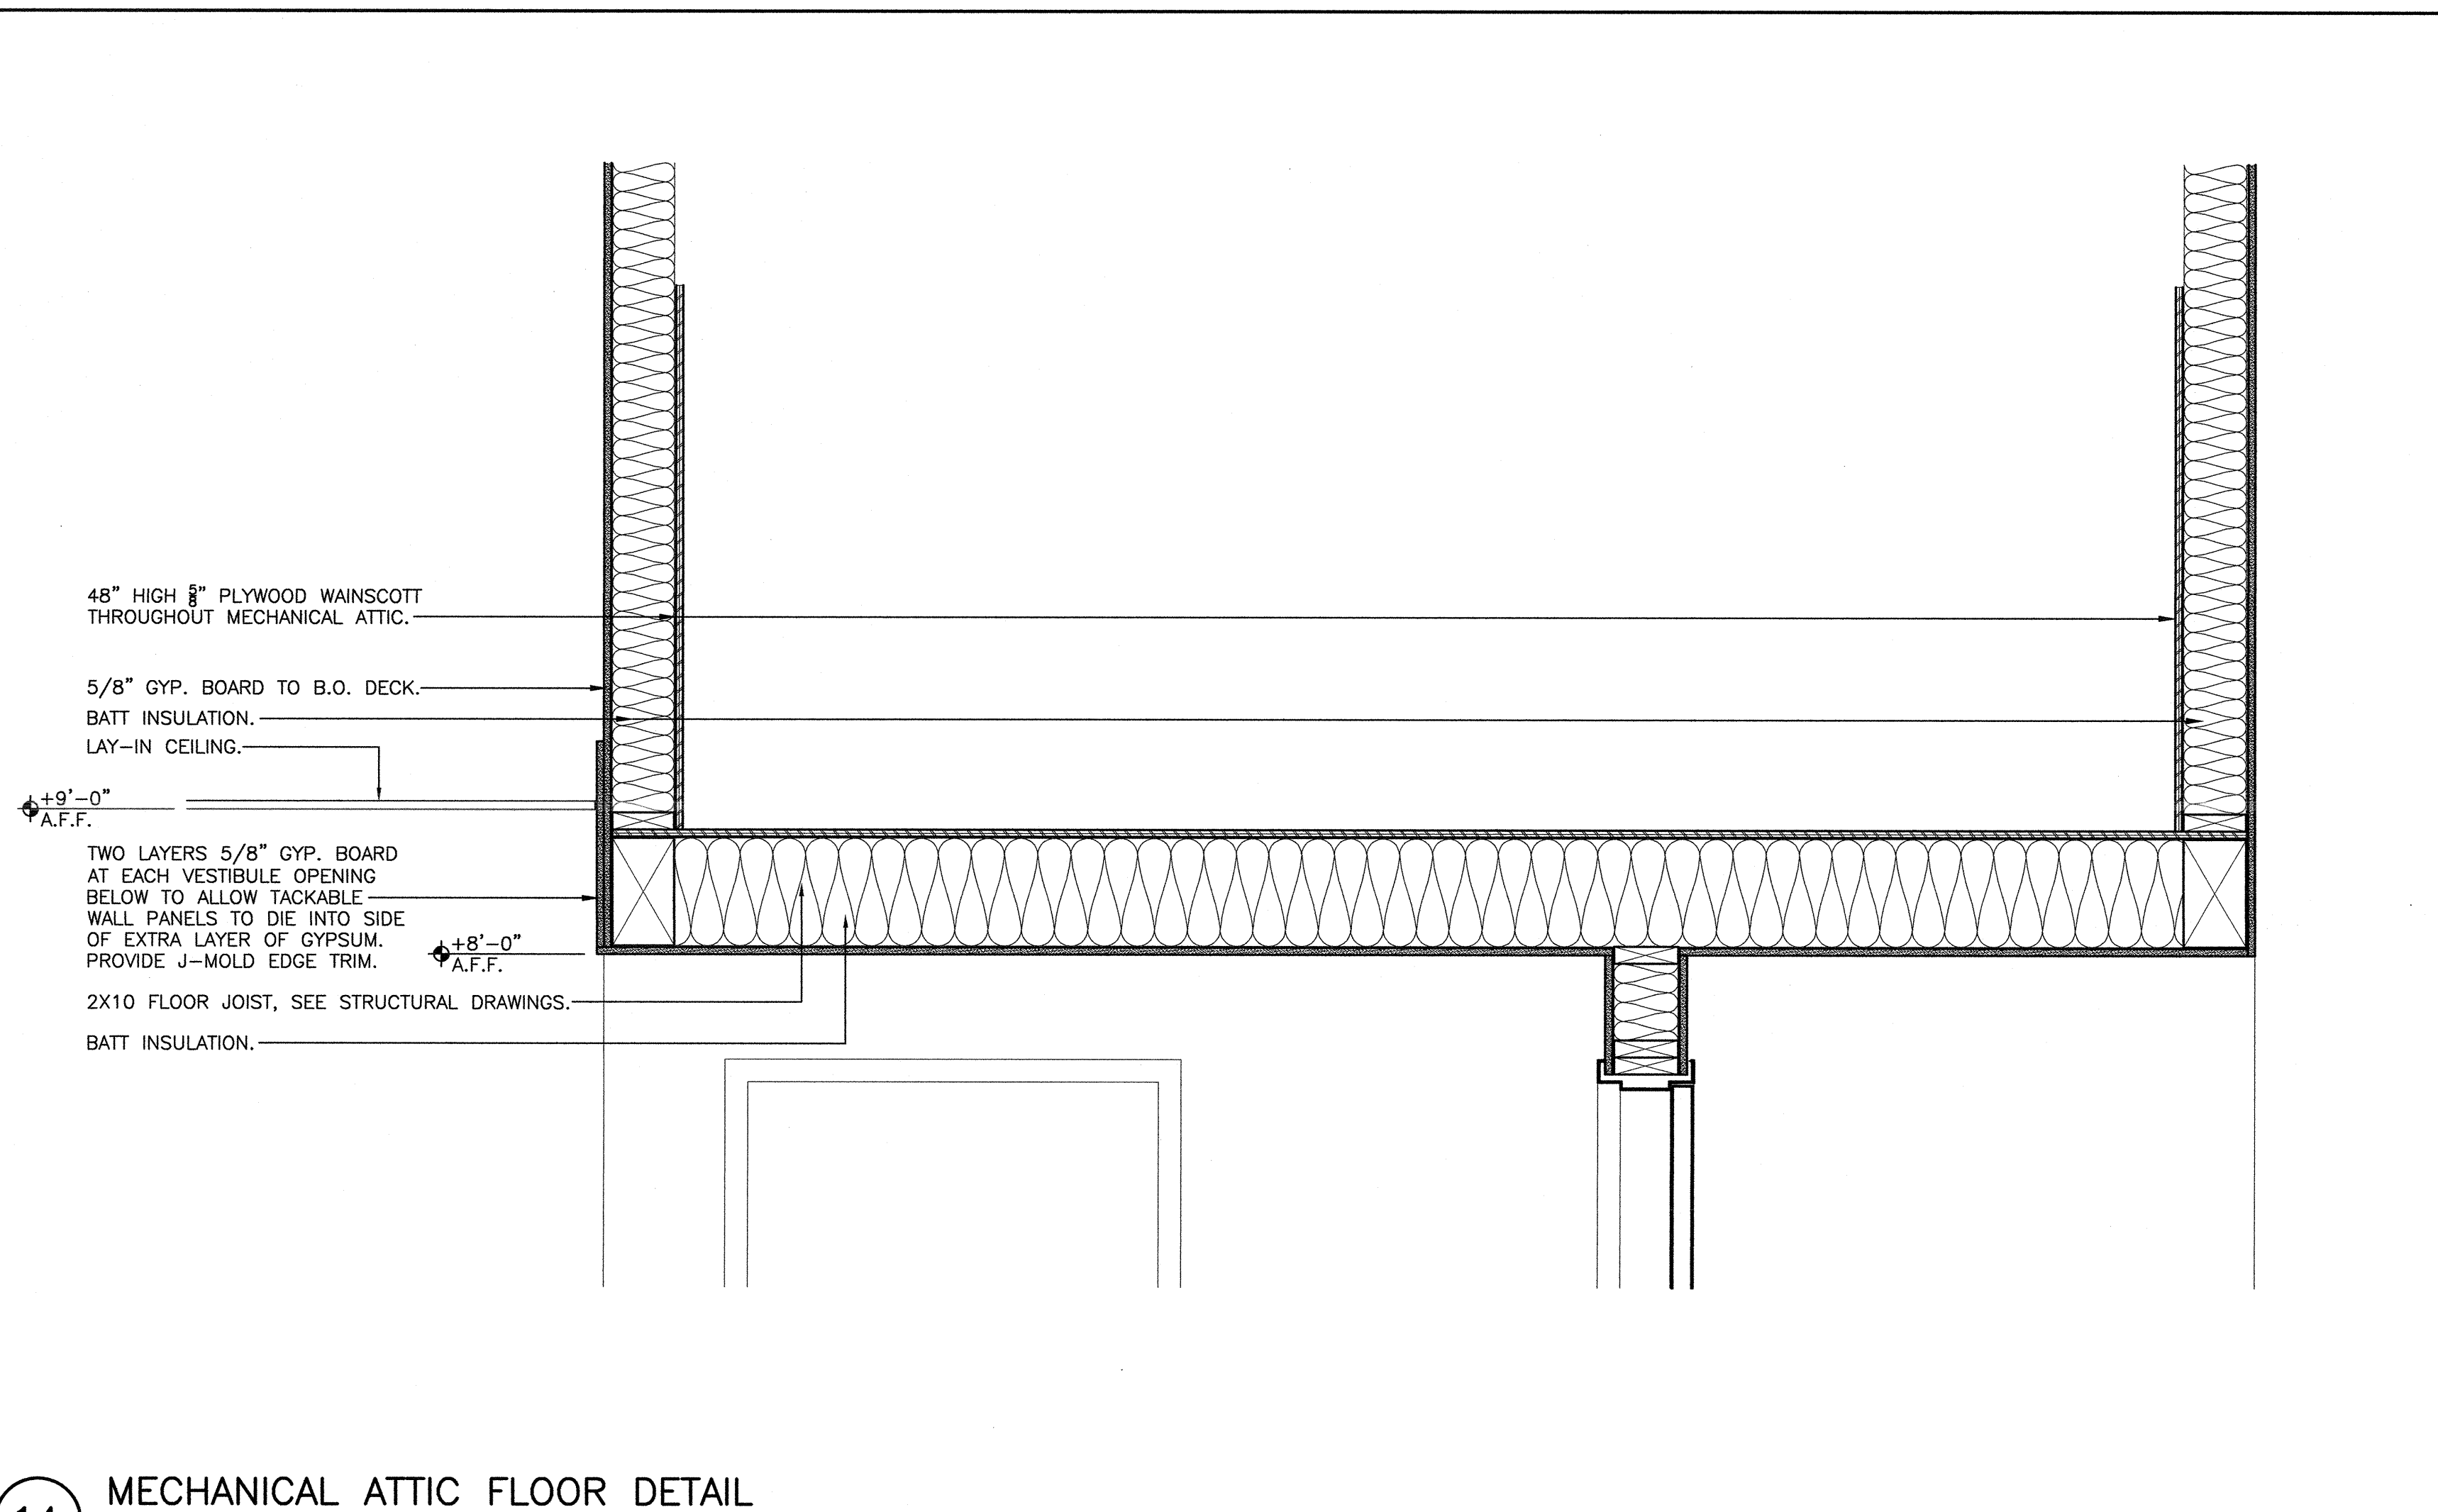
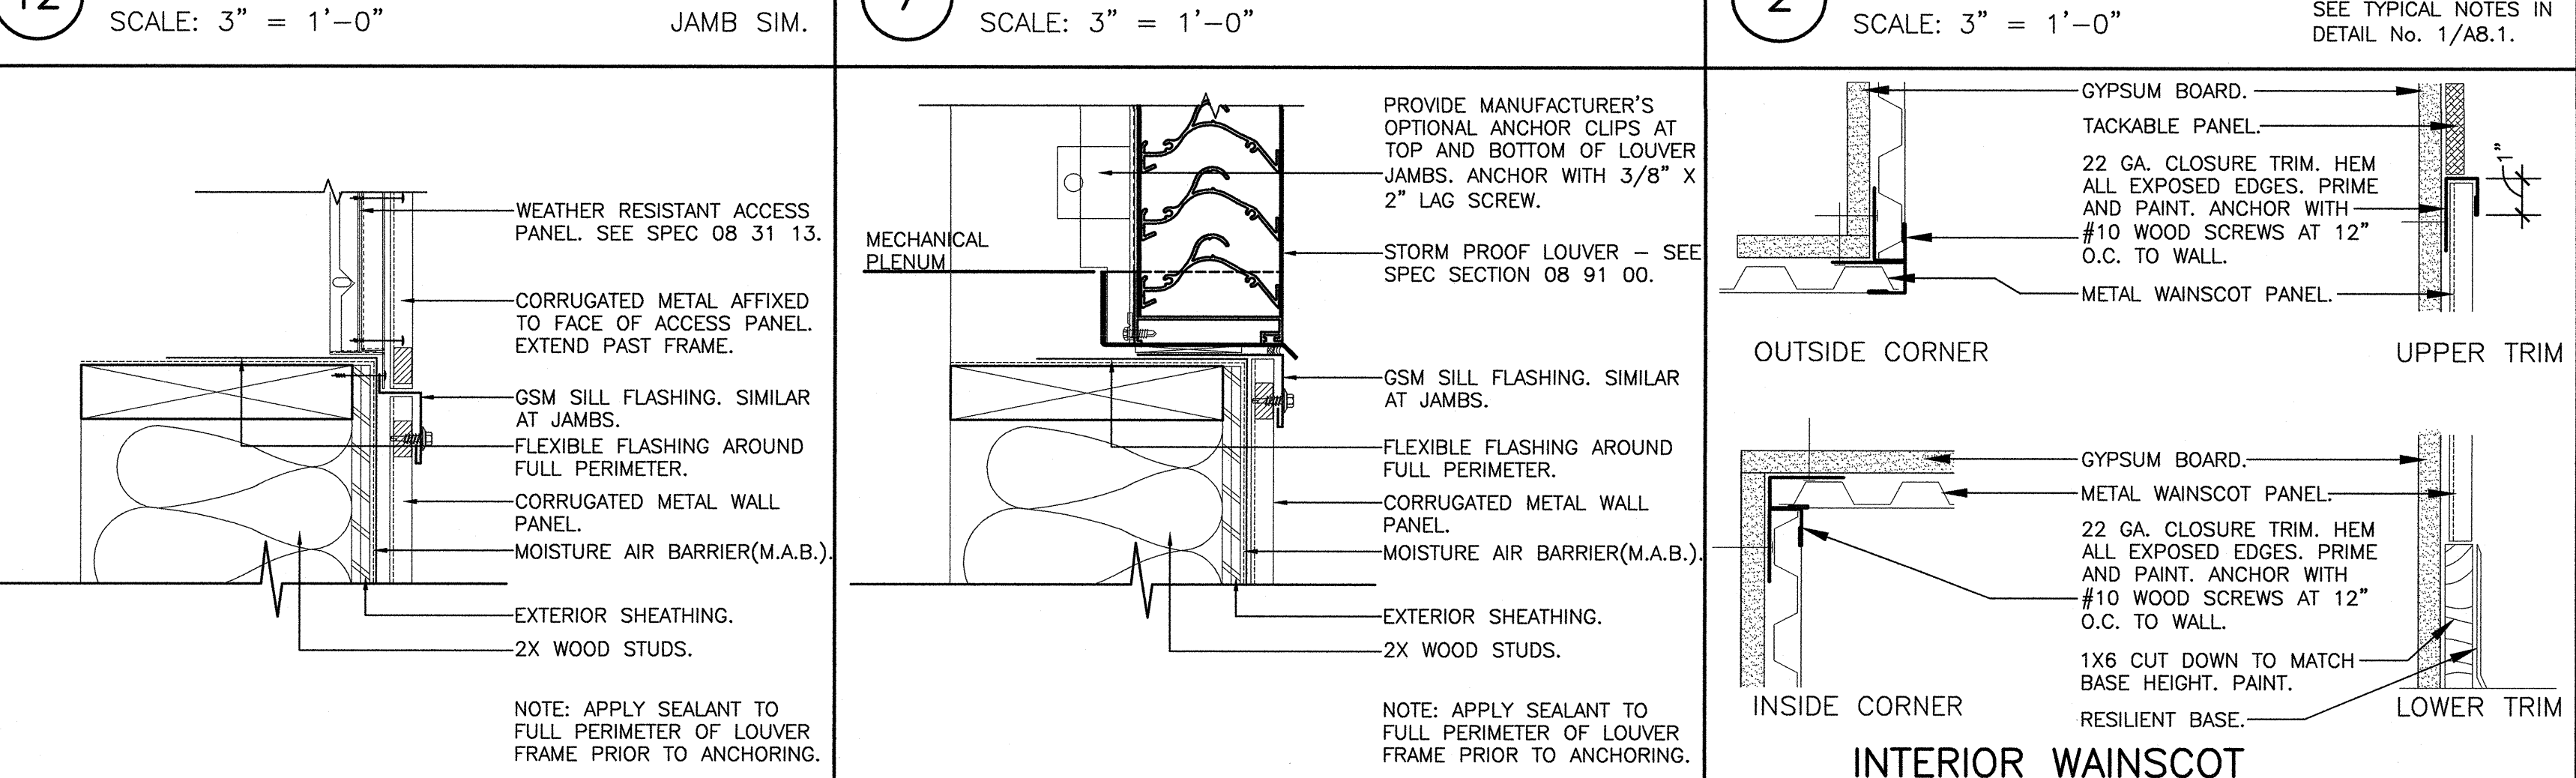
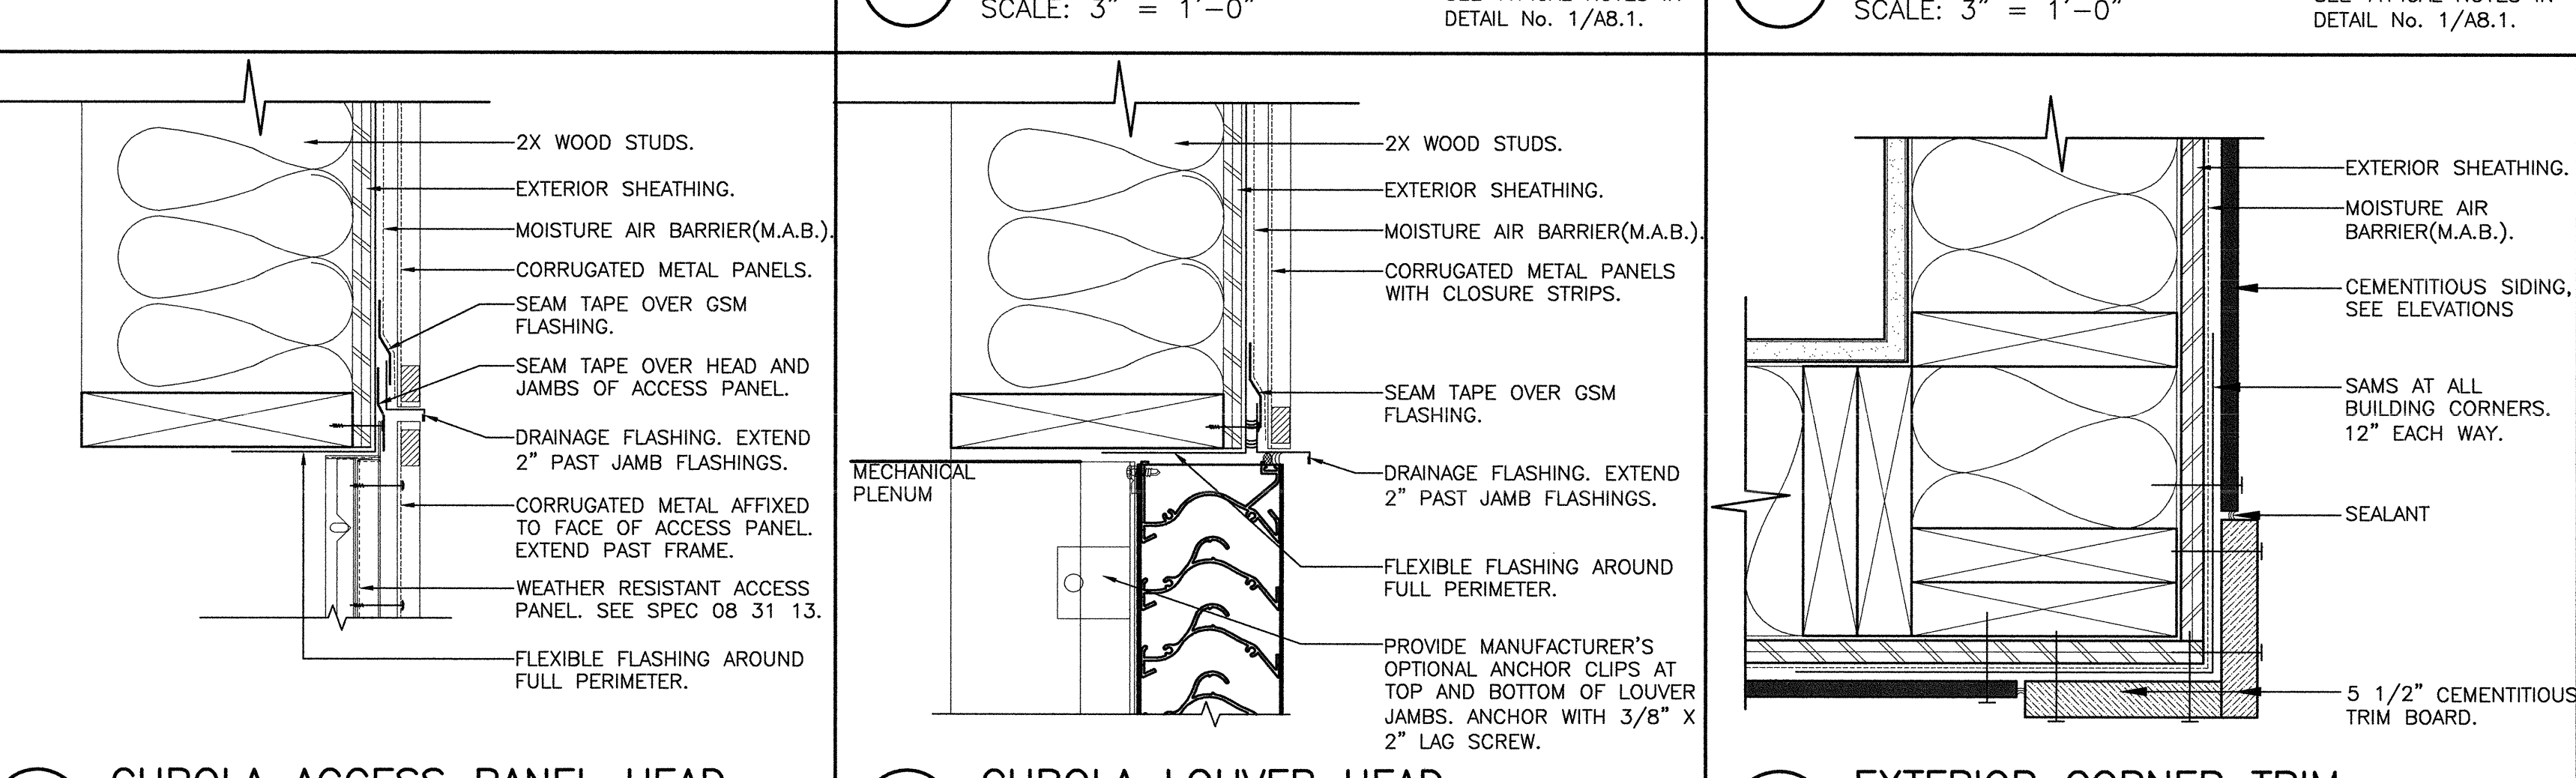
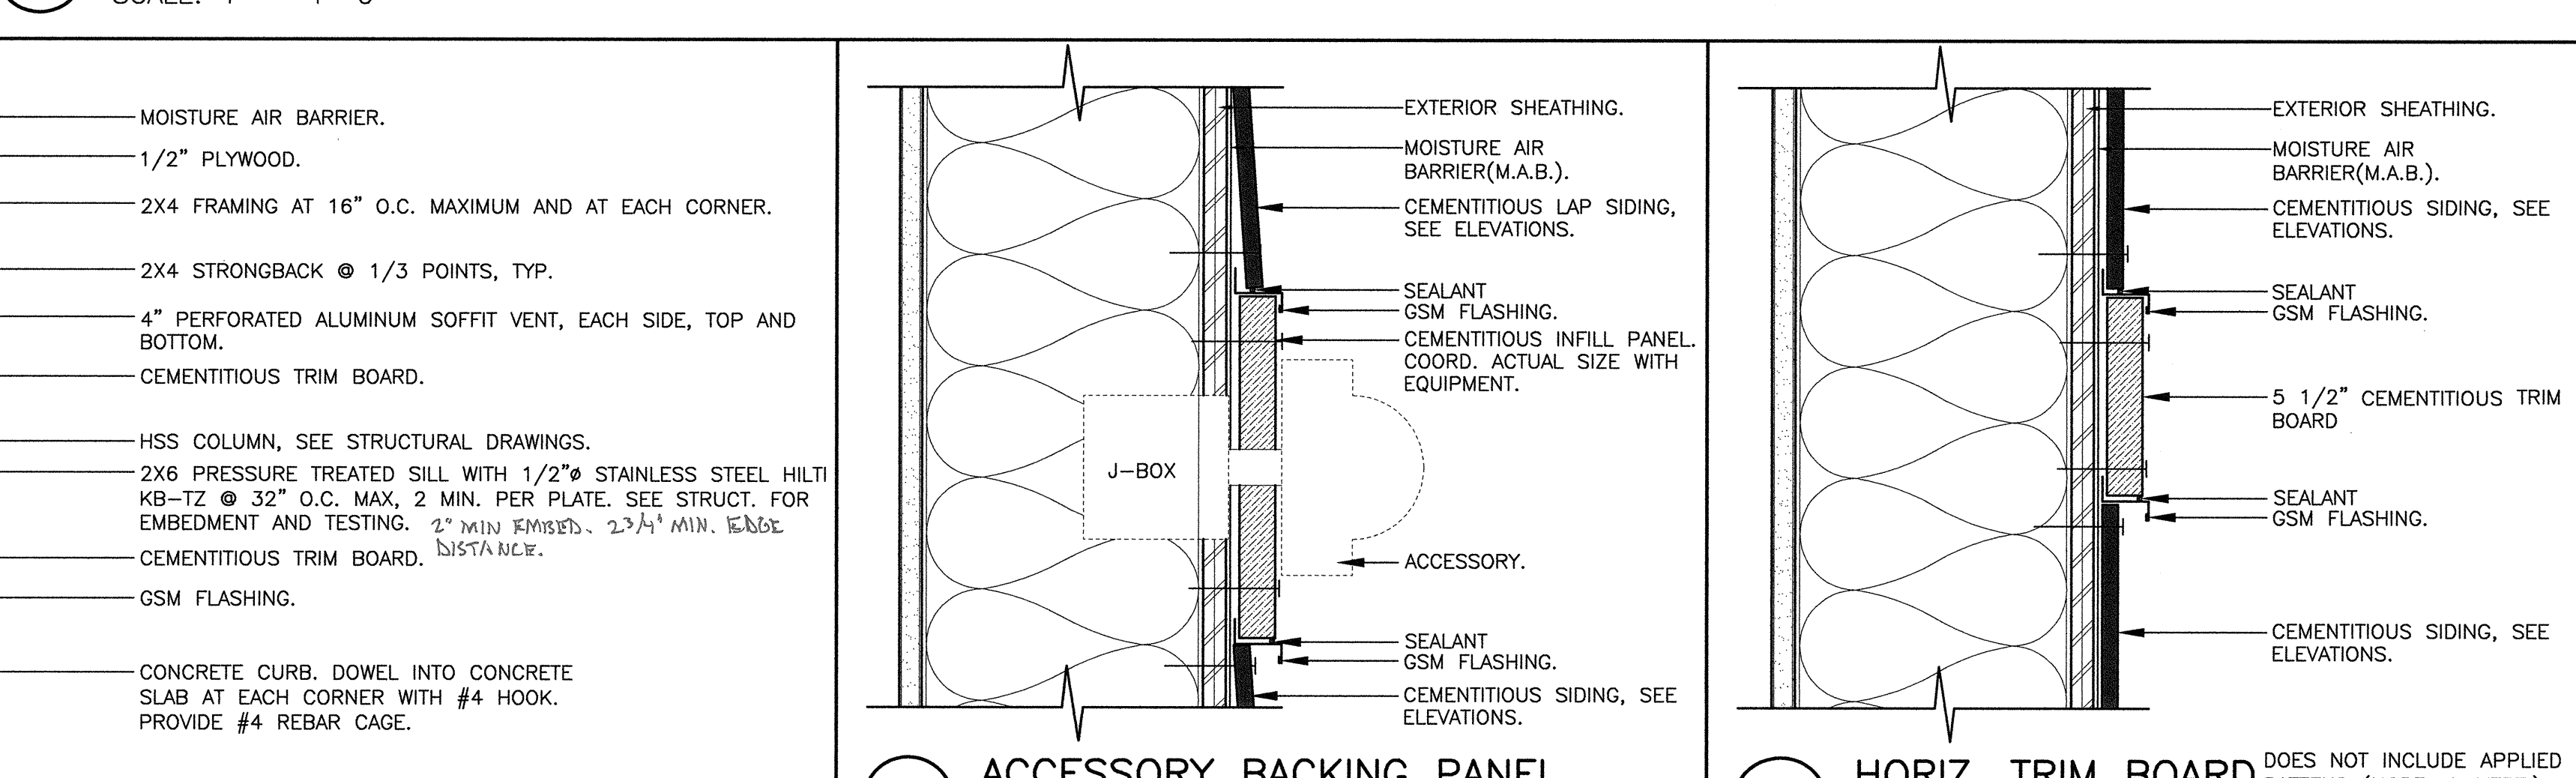
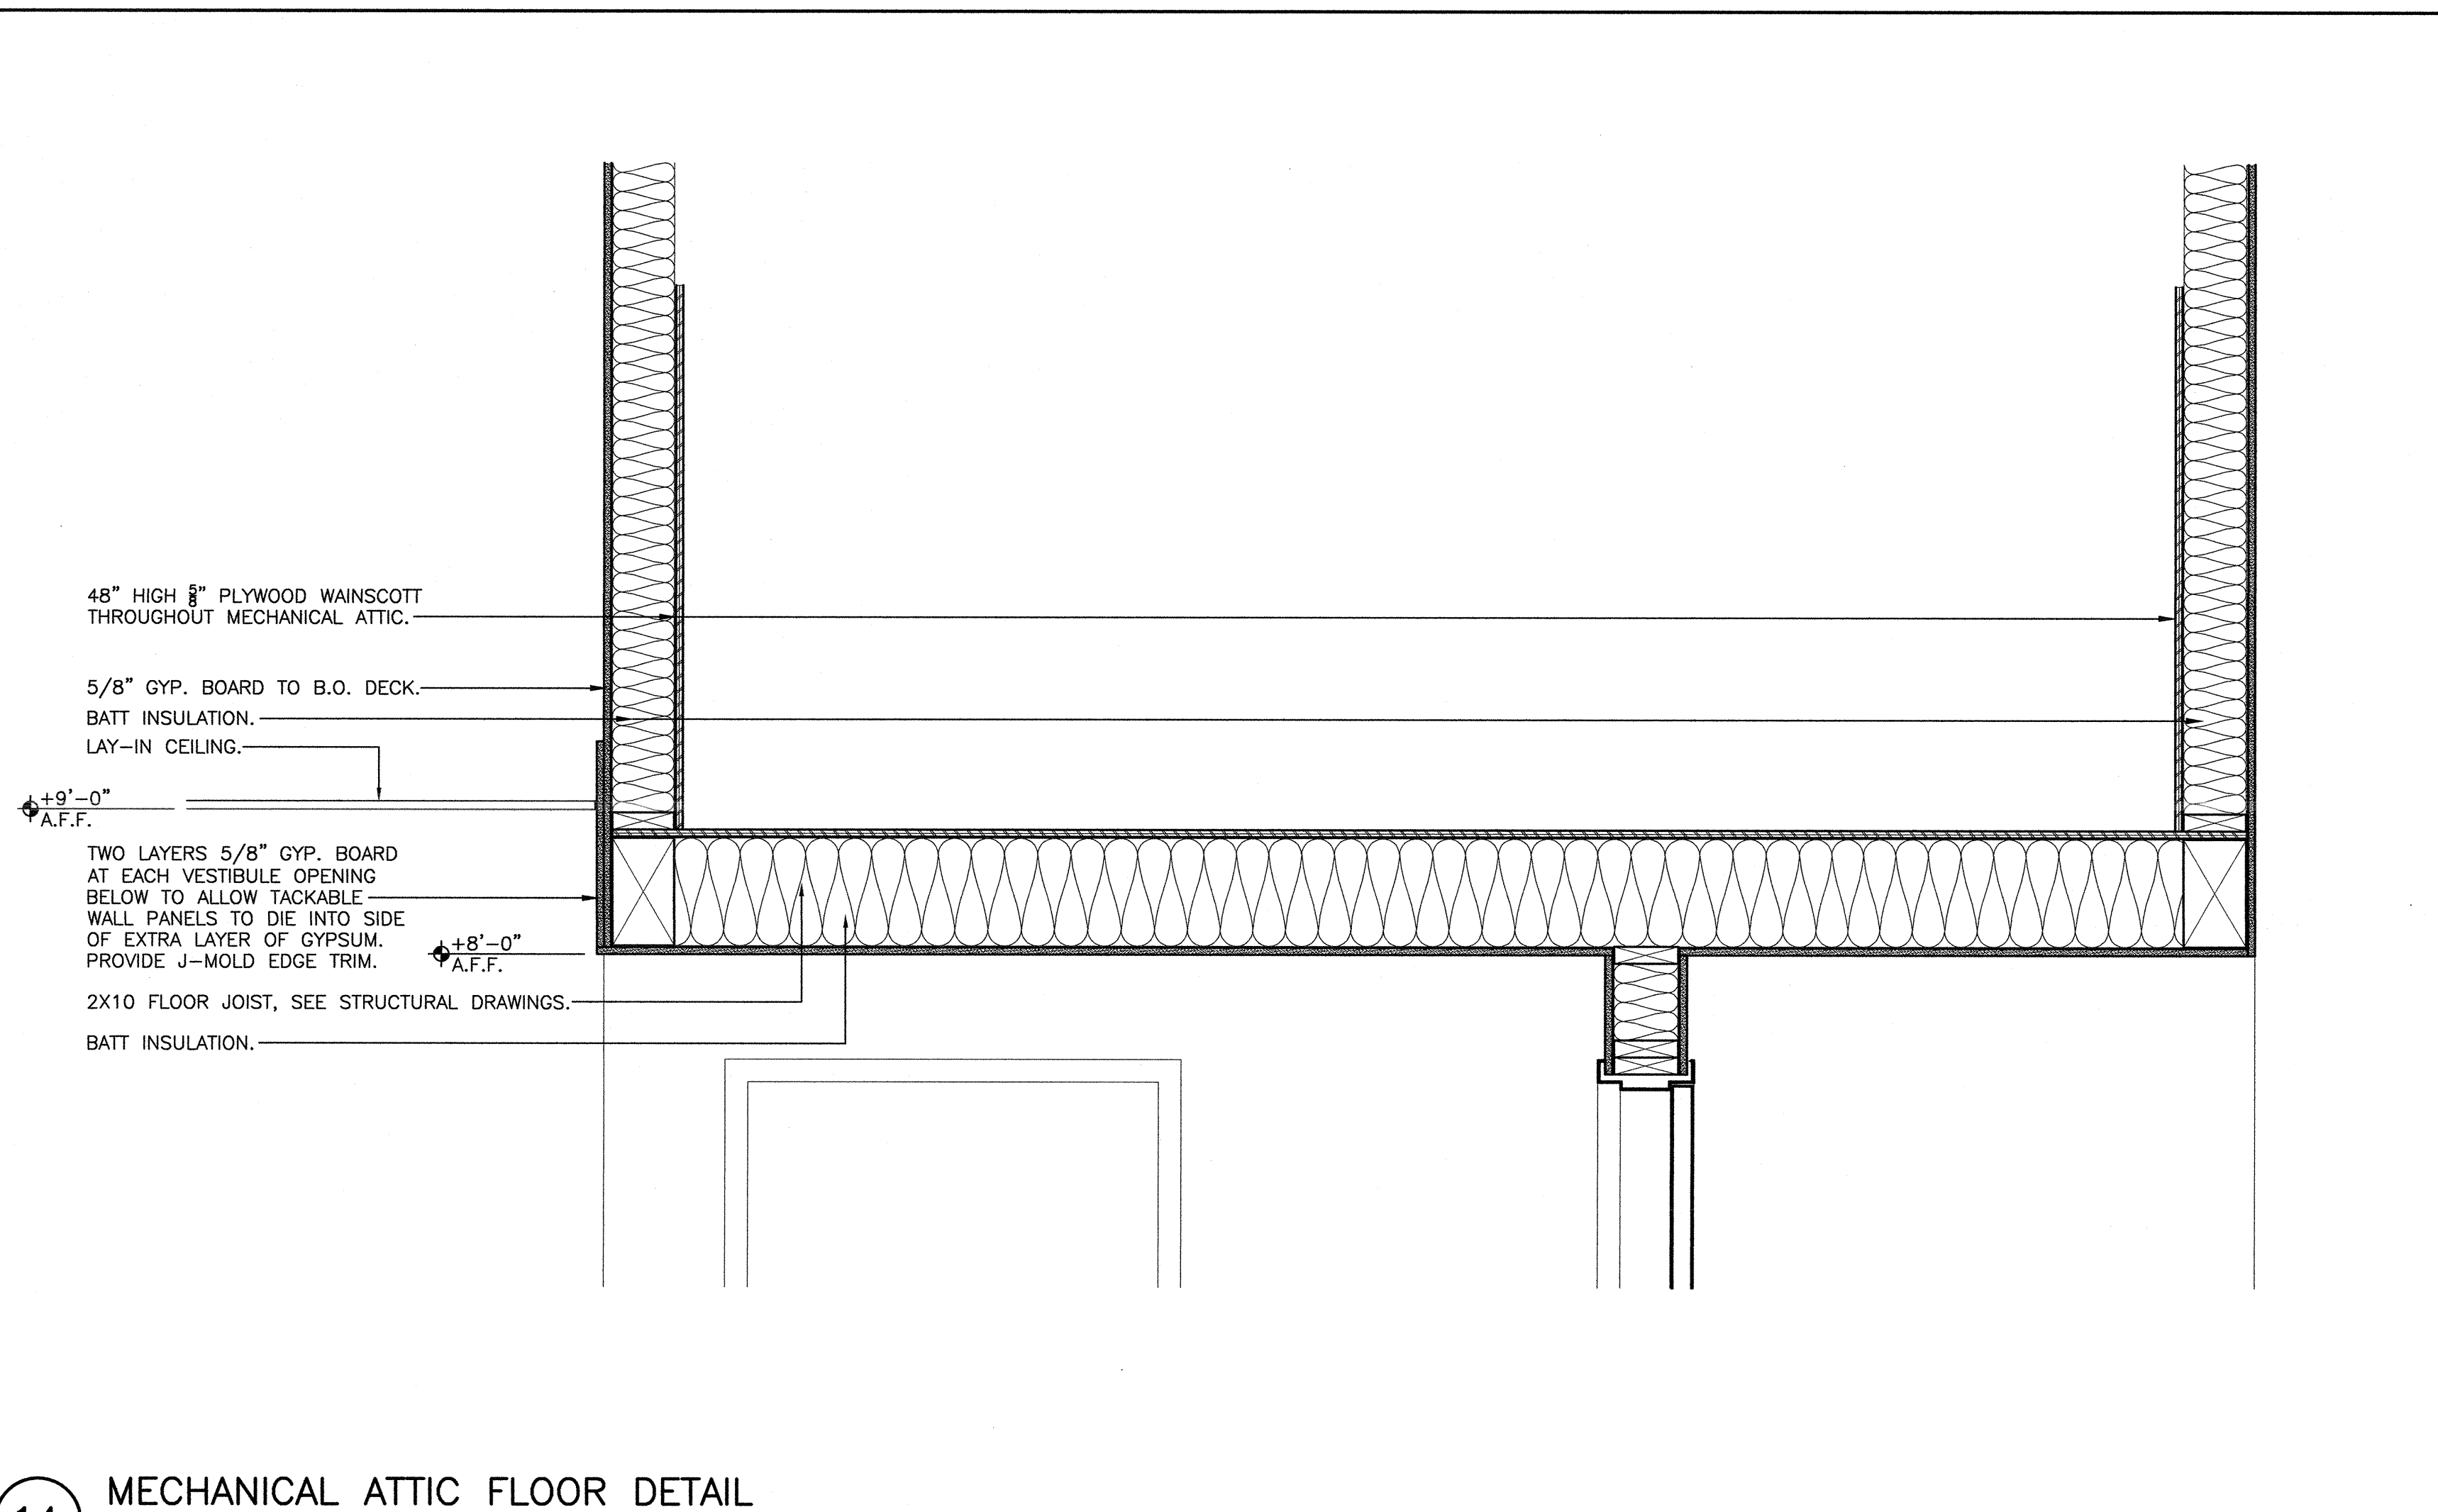
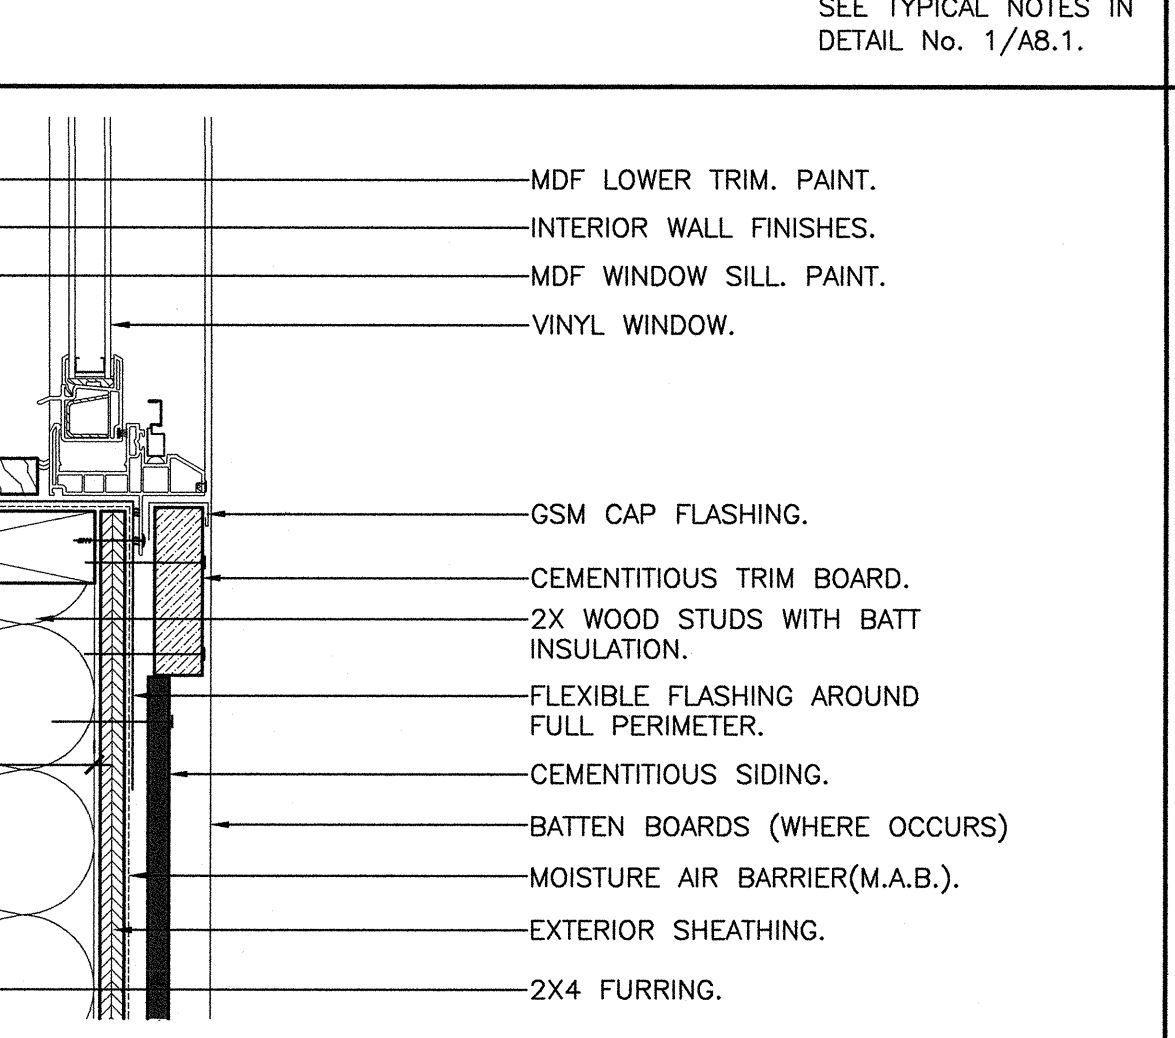
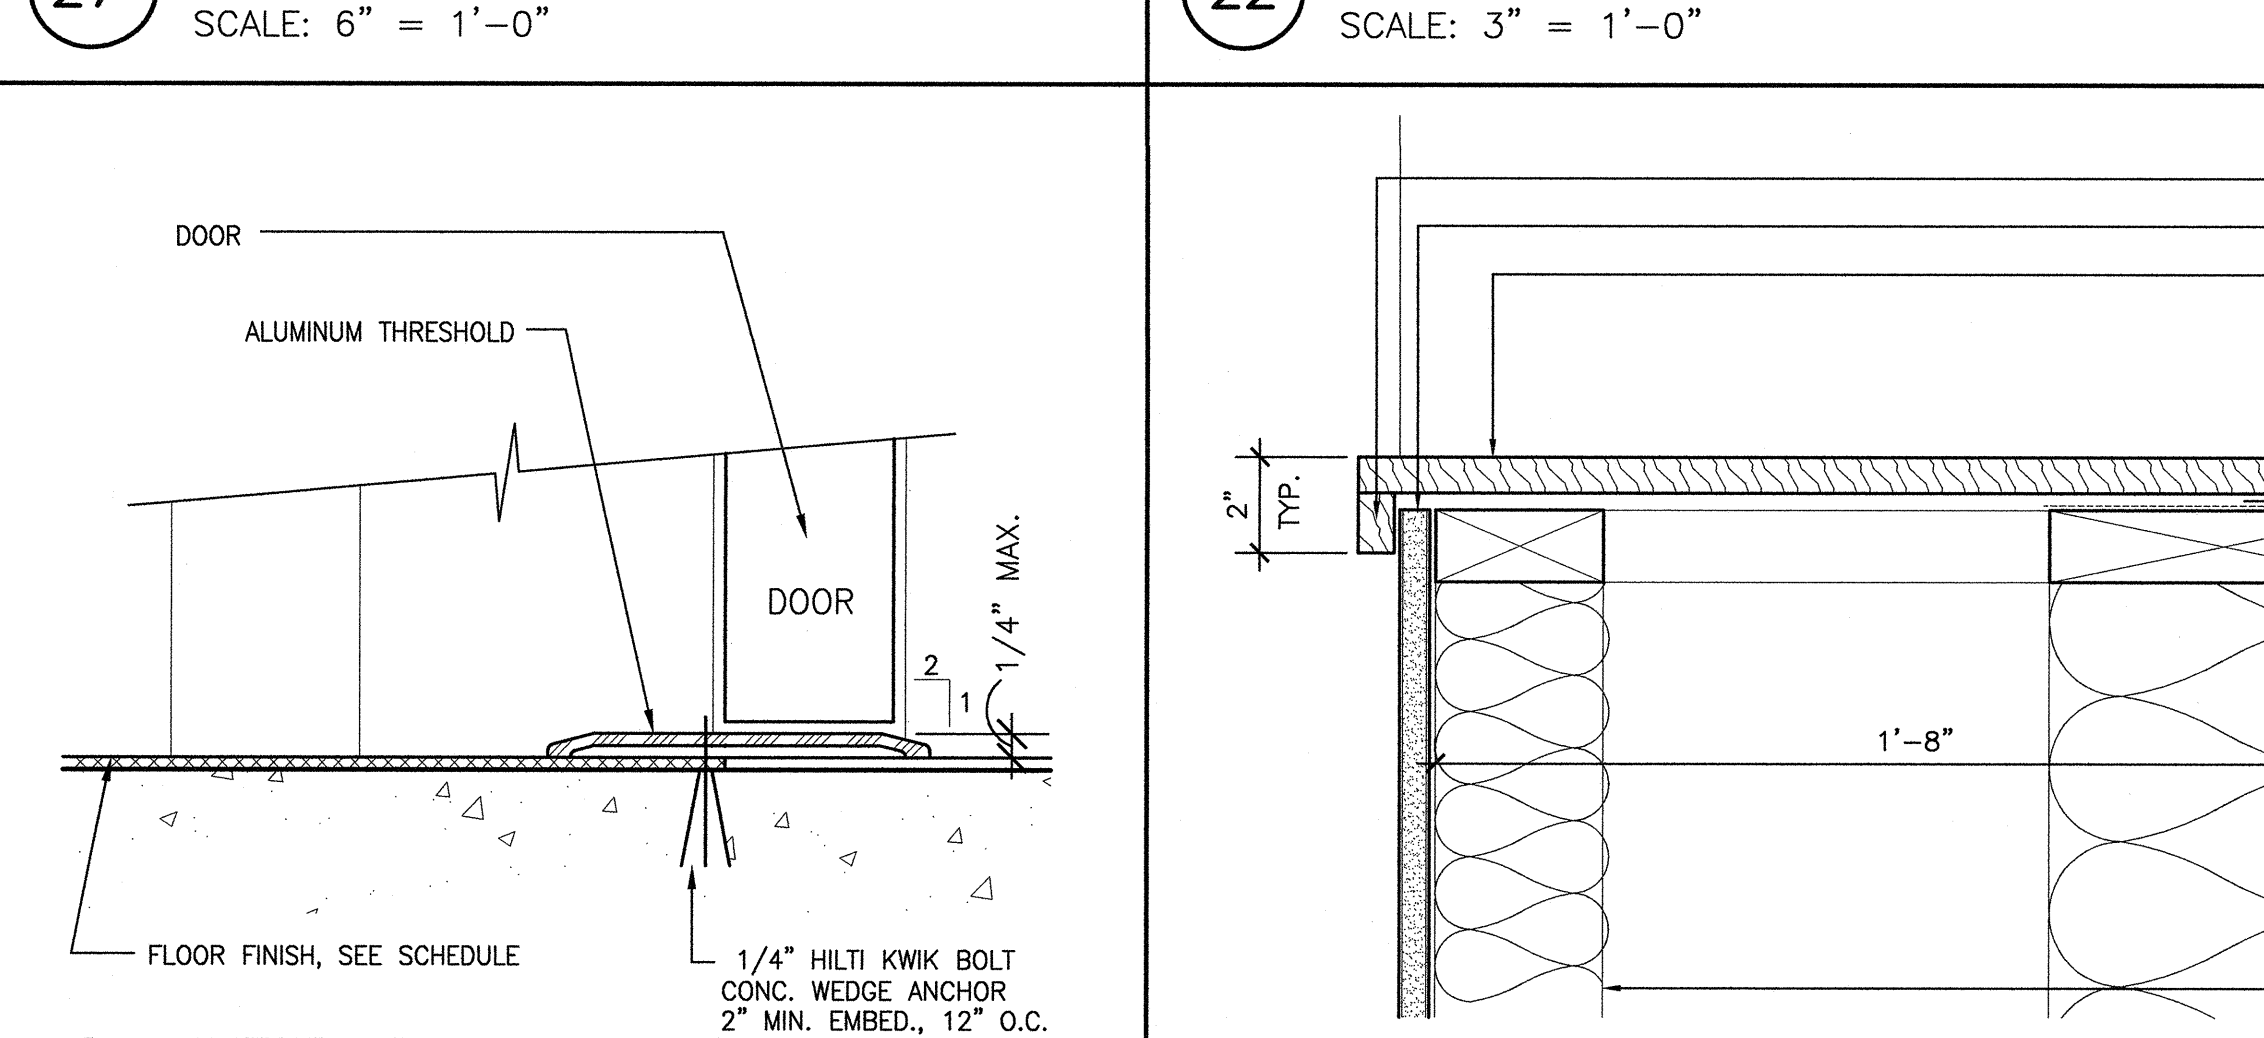
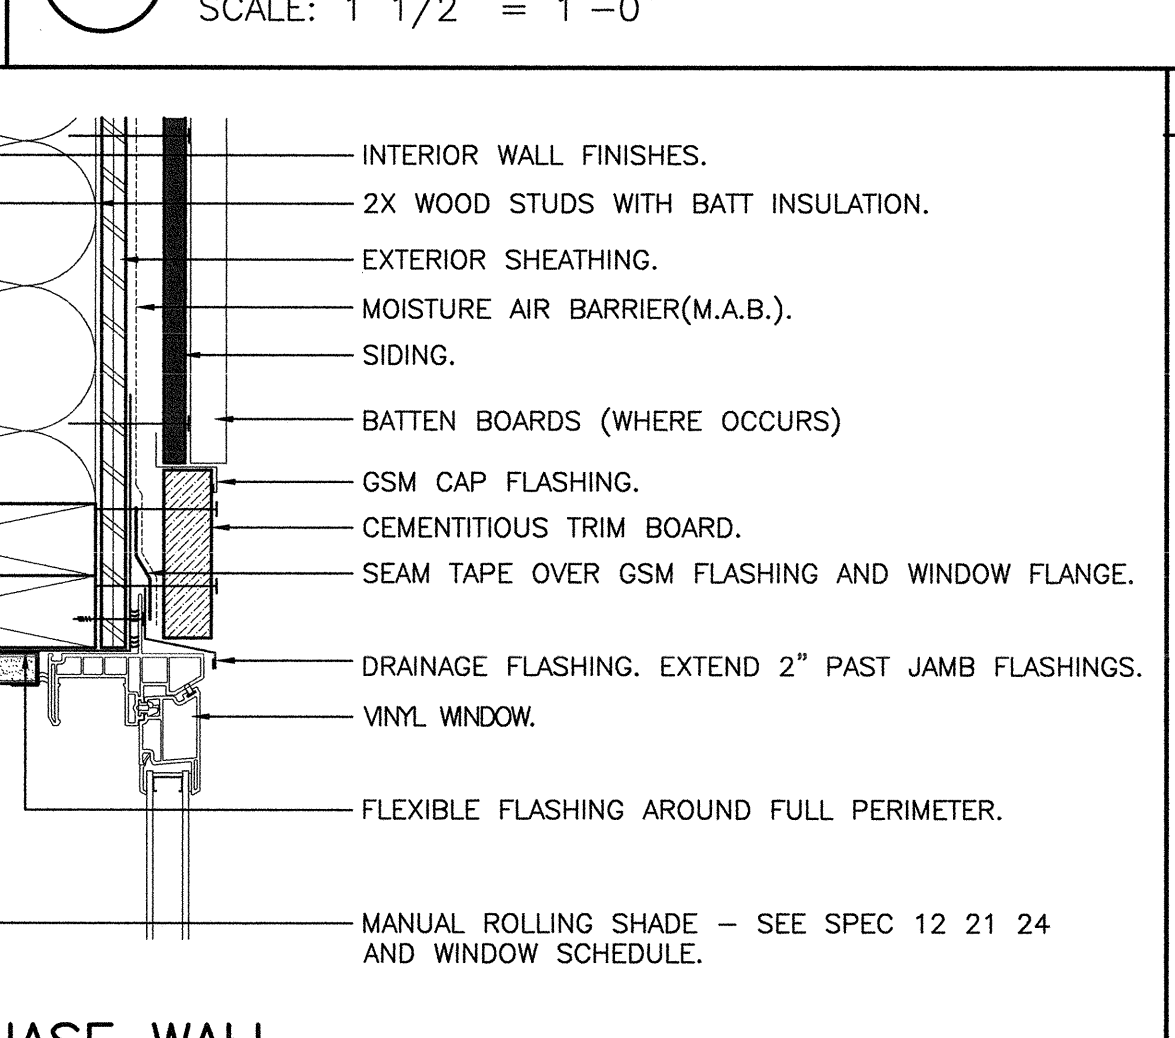
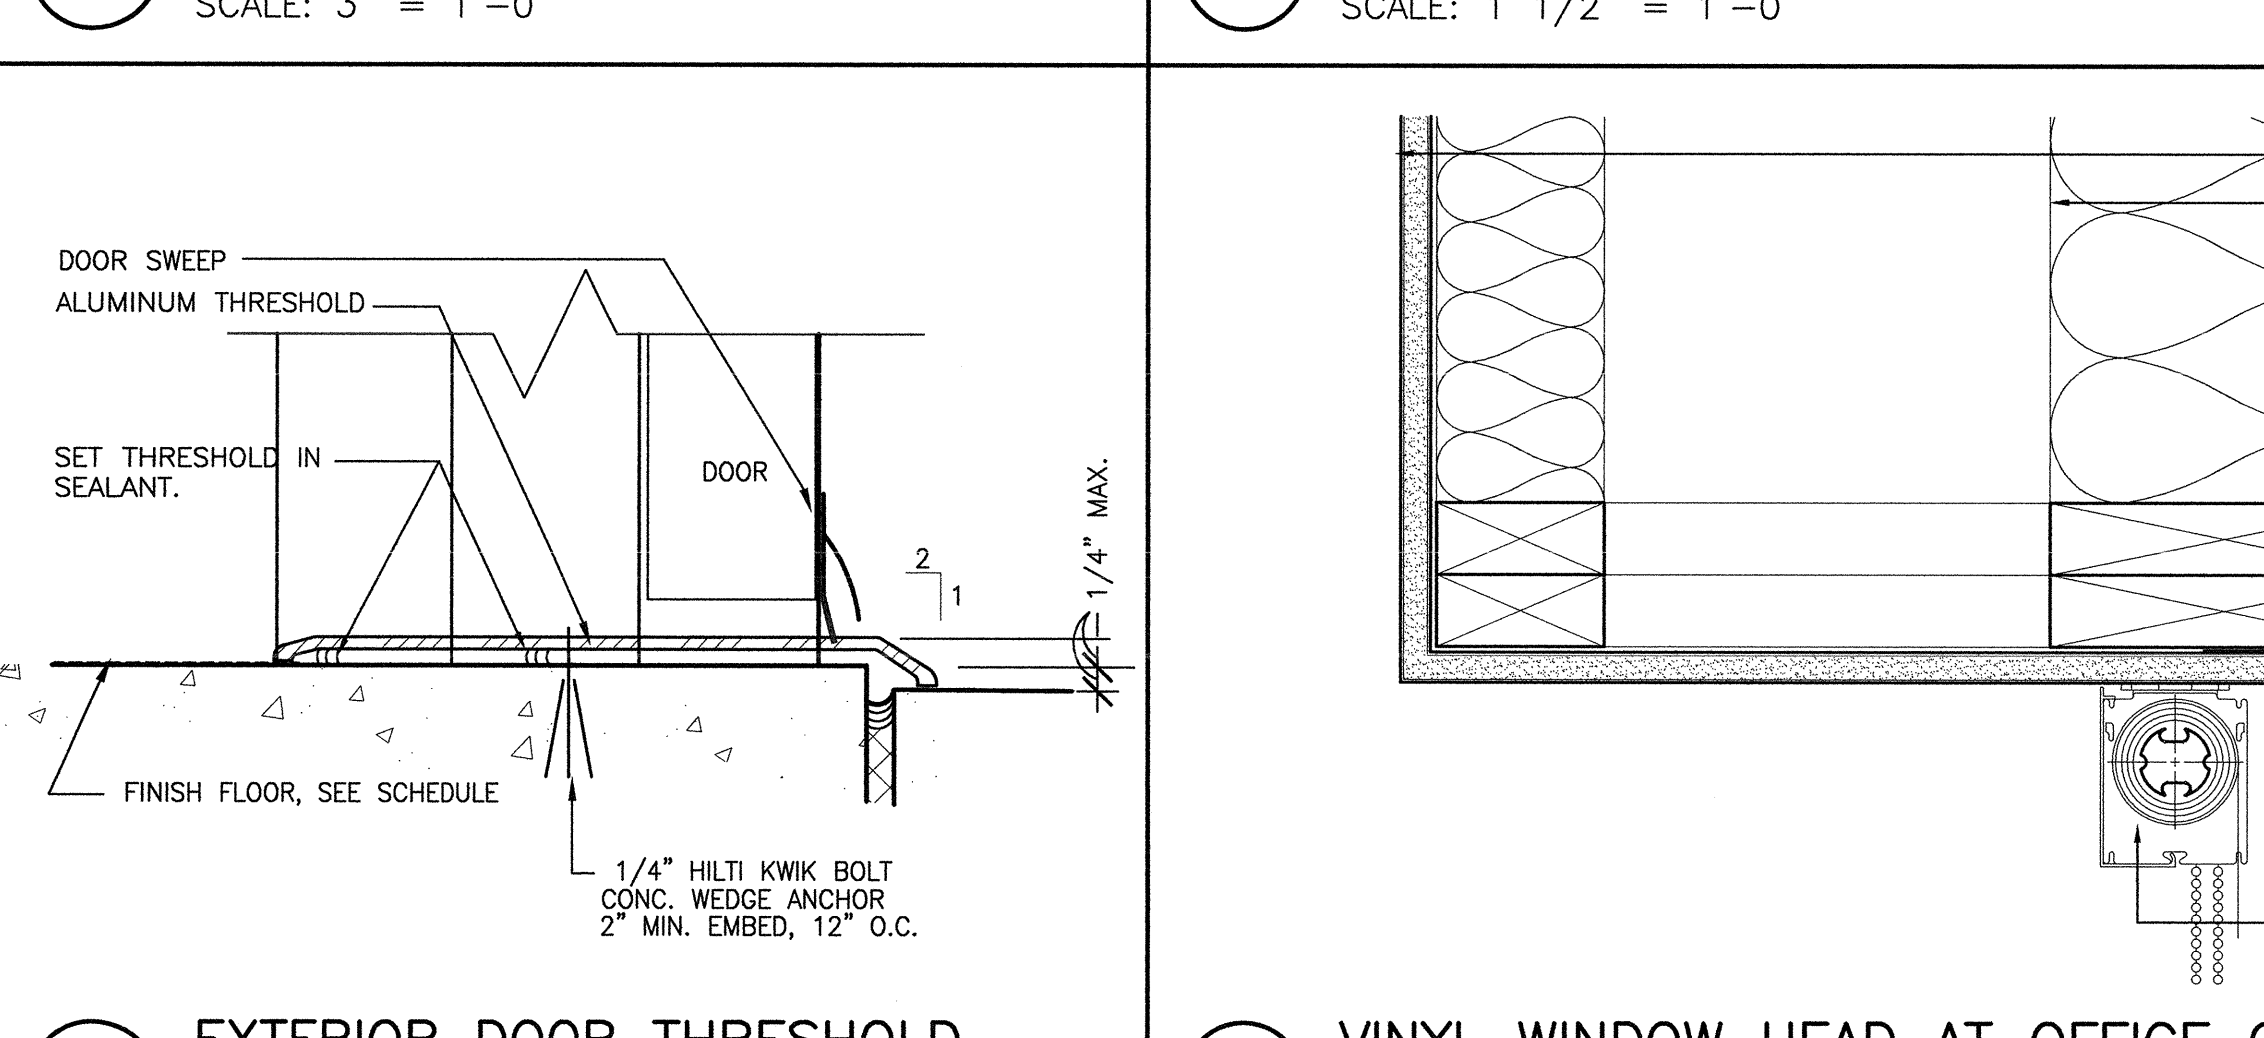
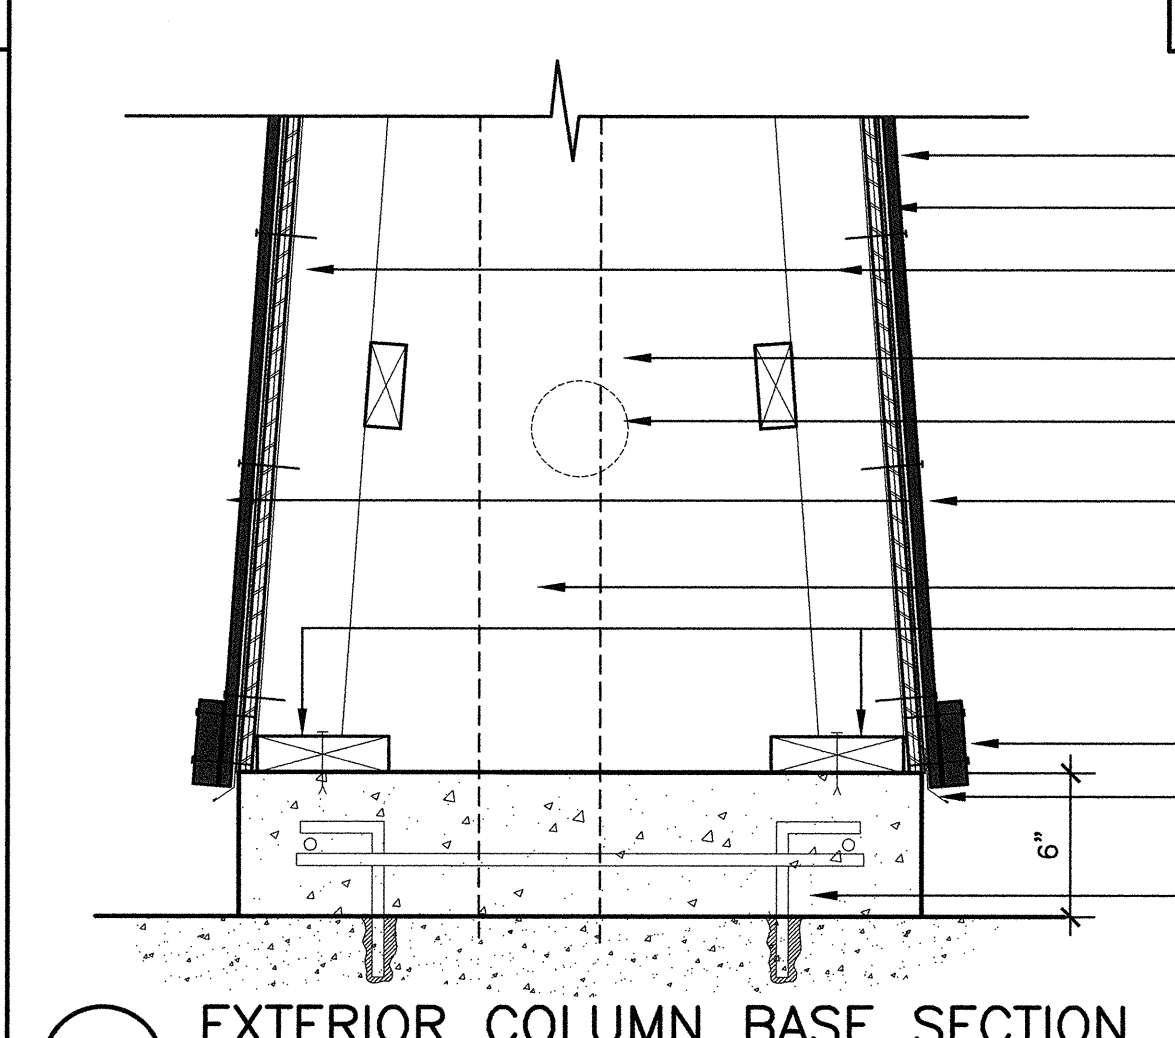
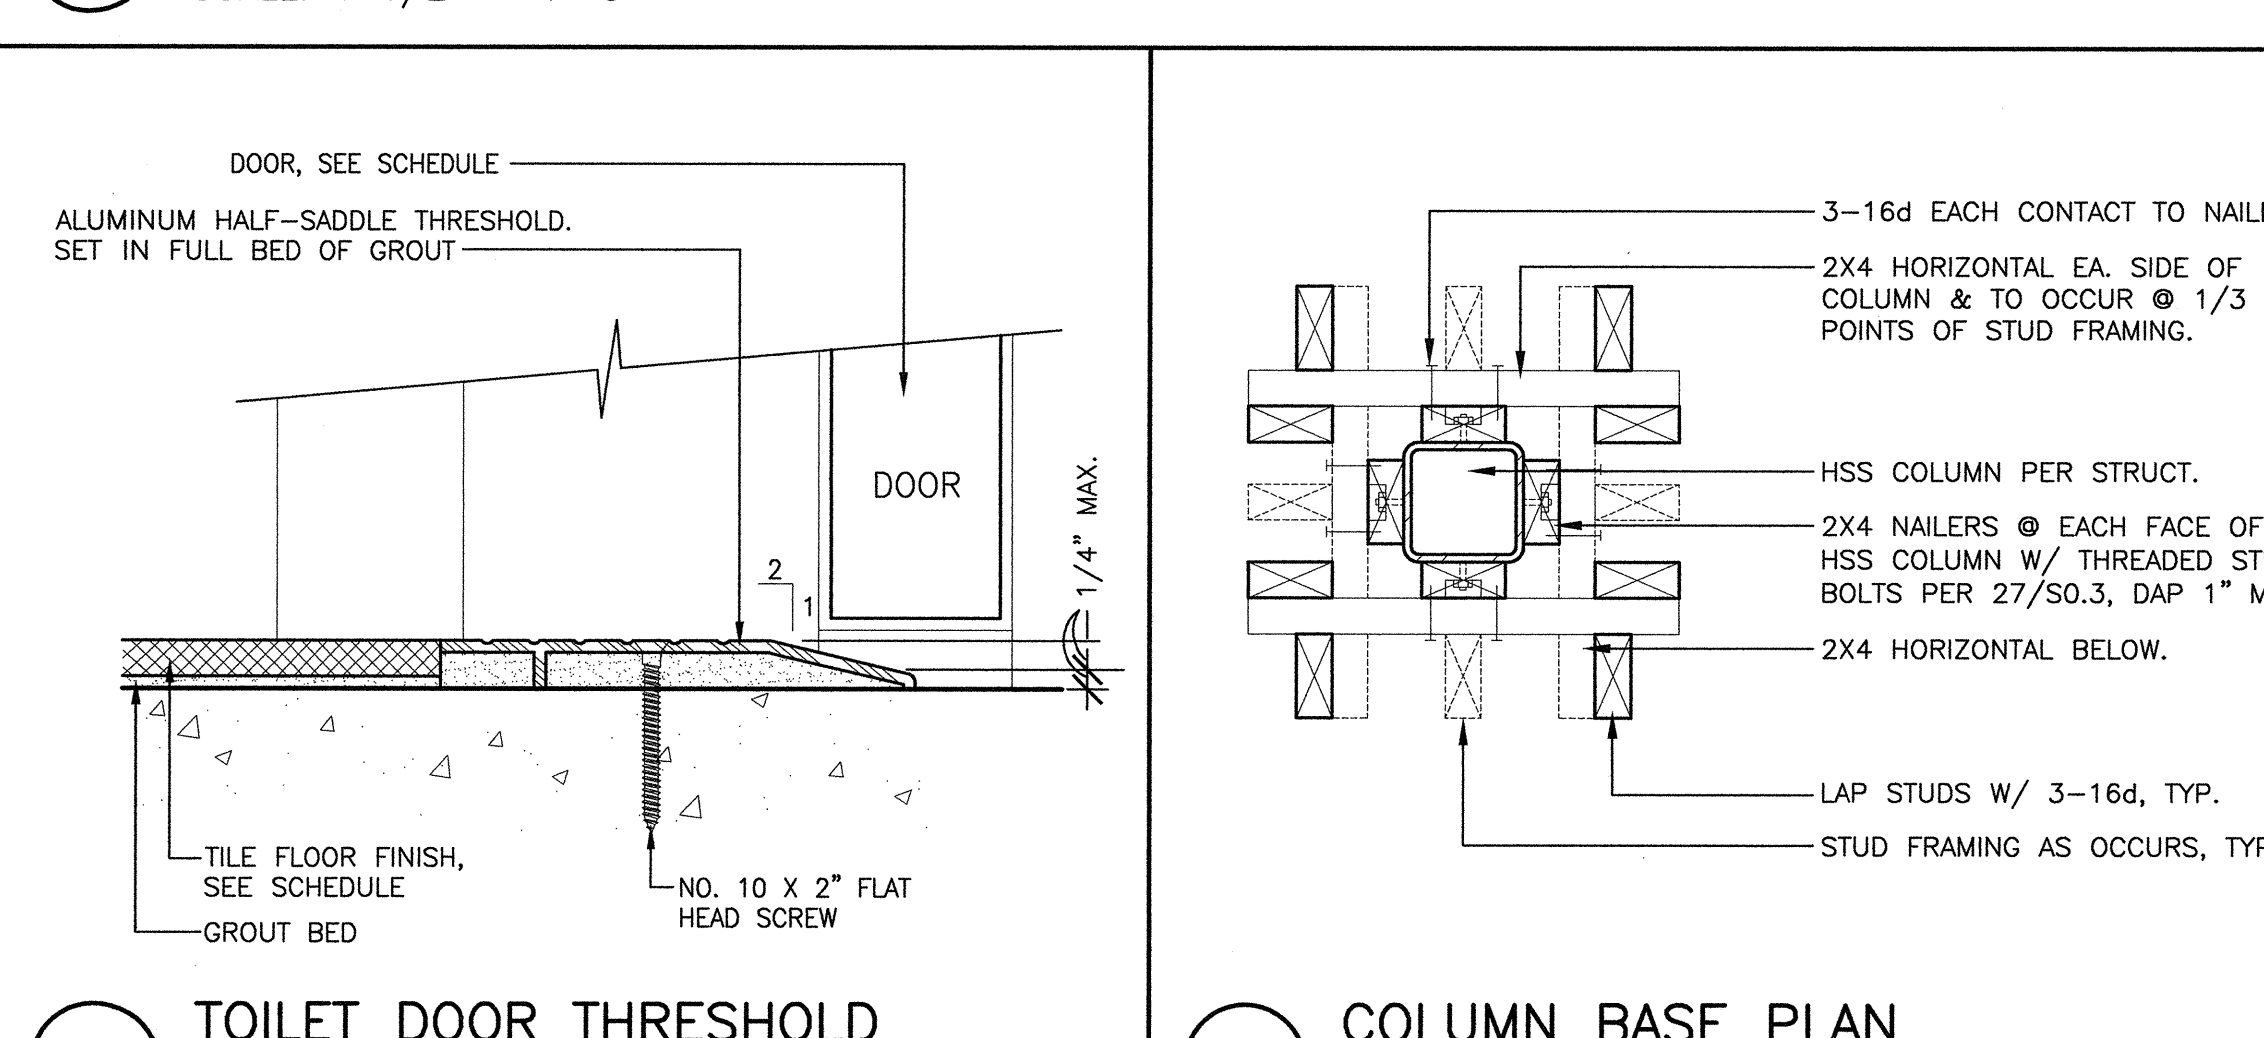
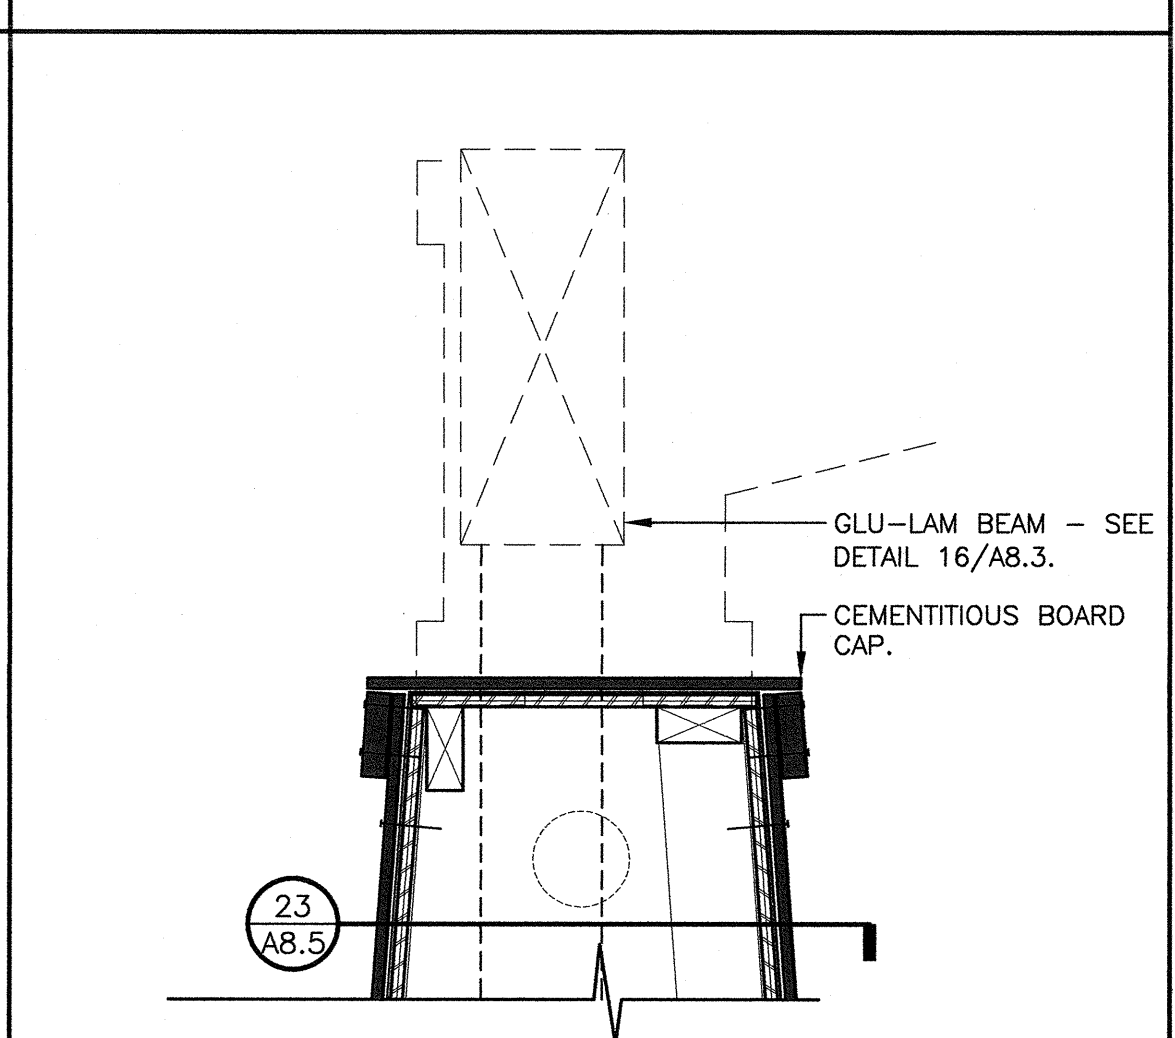
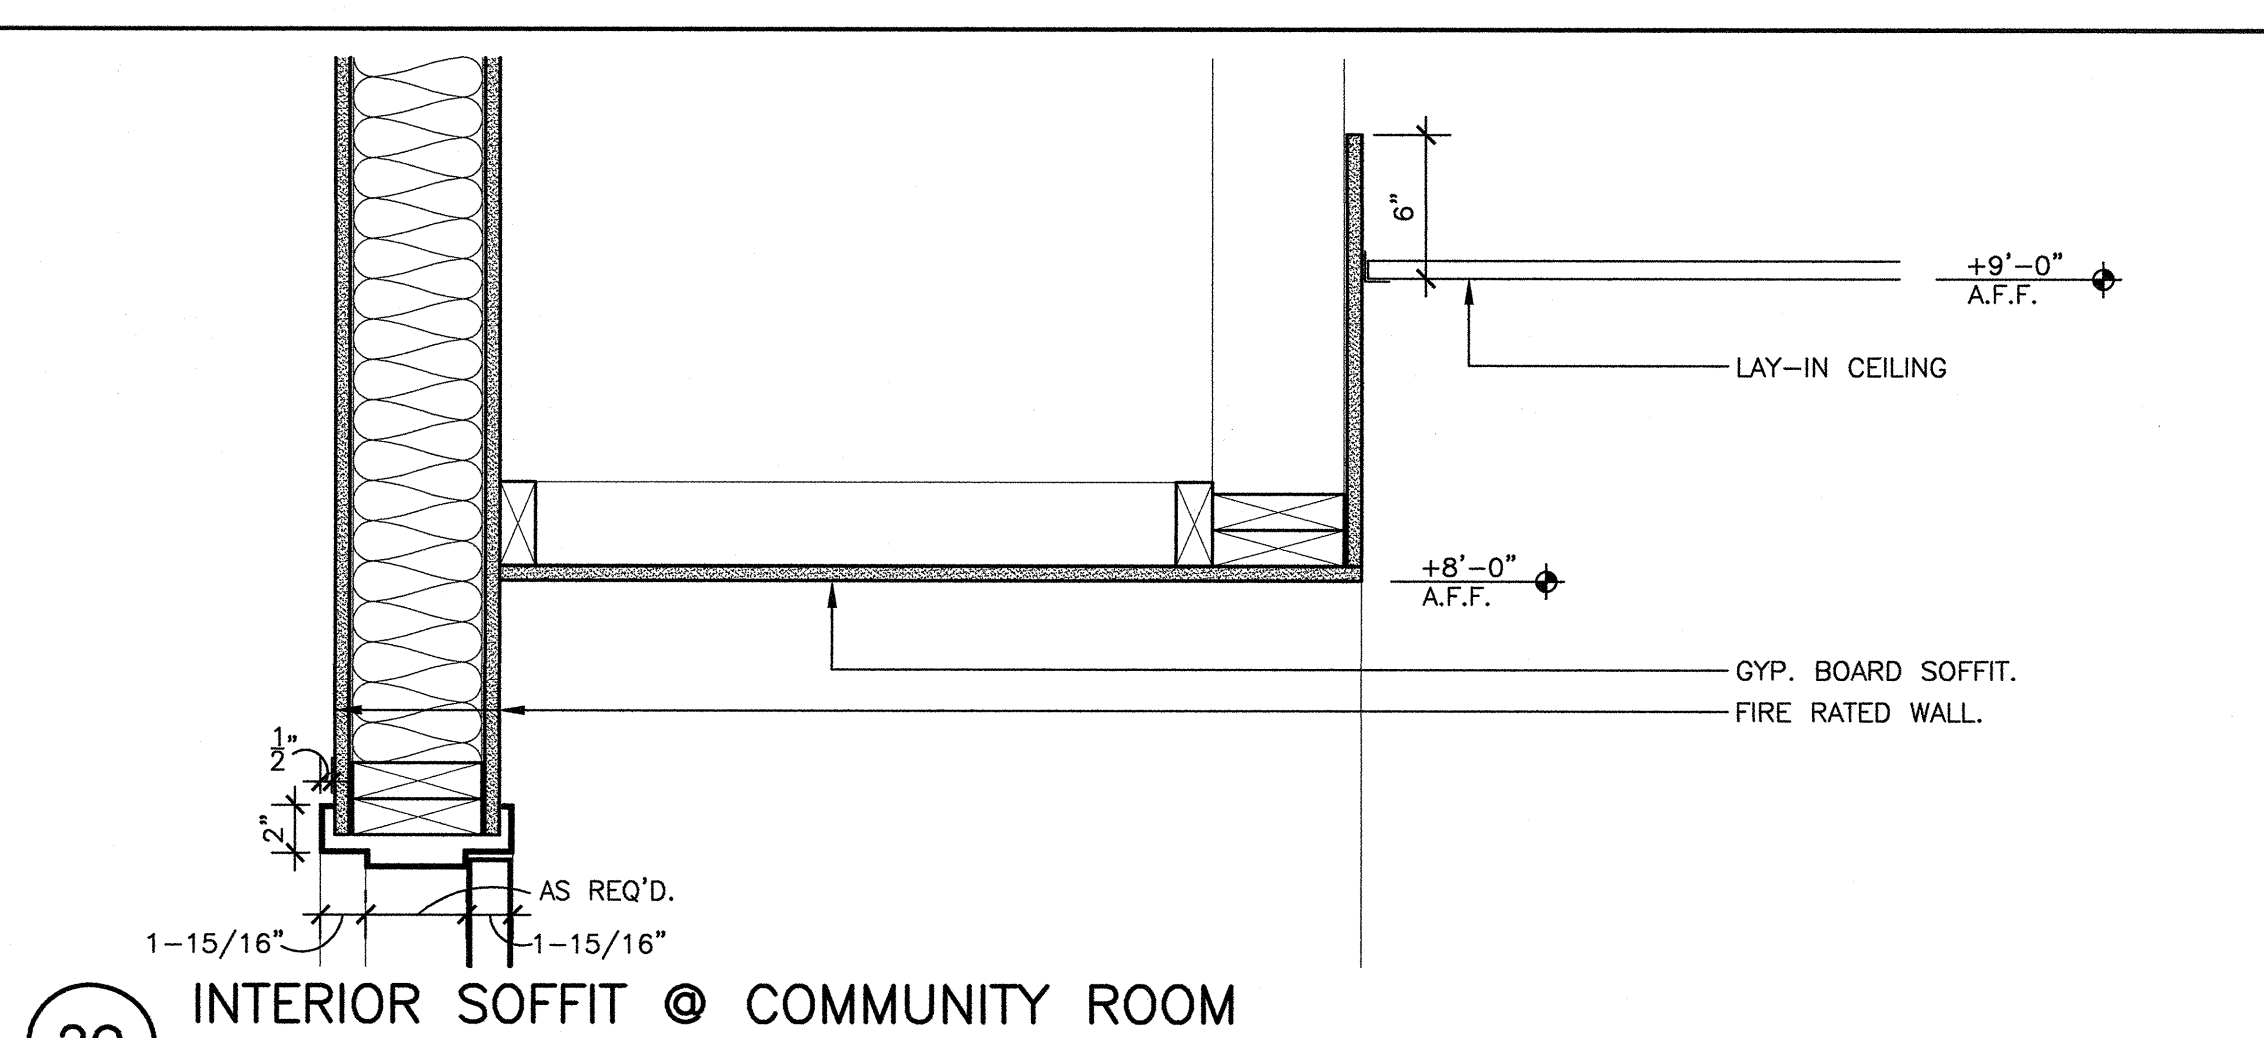


SHEET ____ OF ____ TOTAL

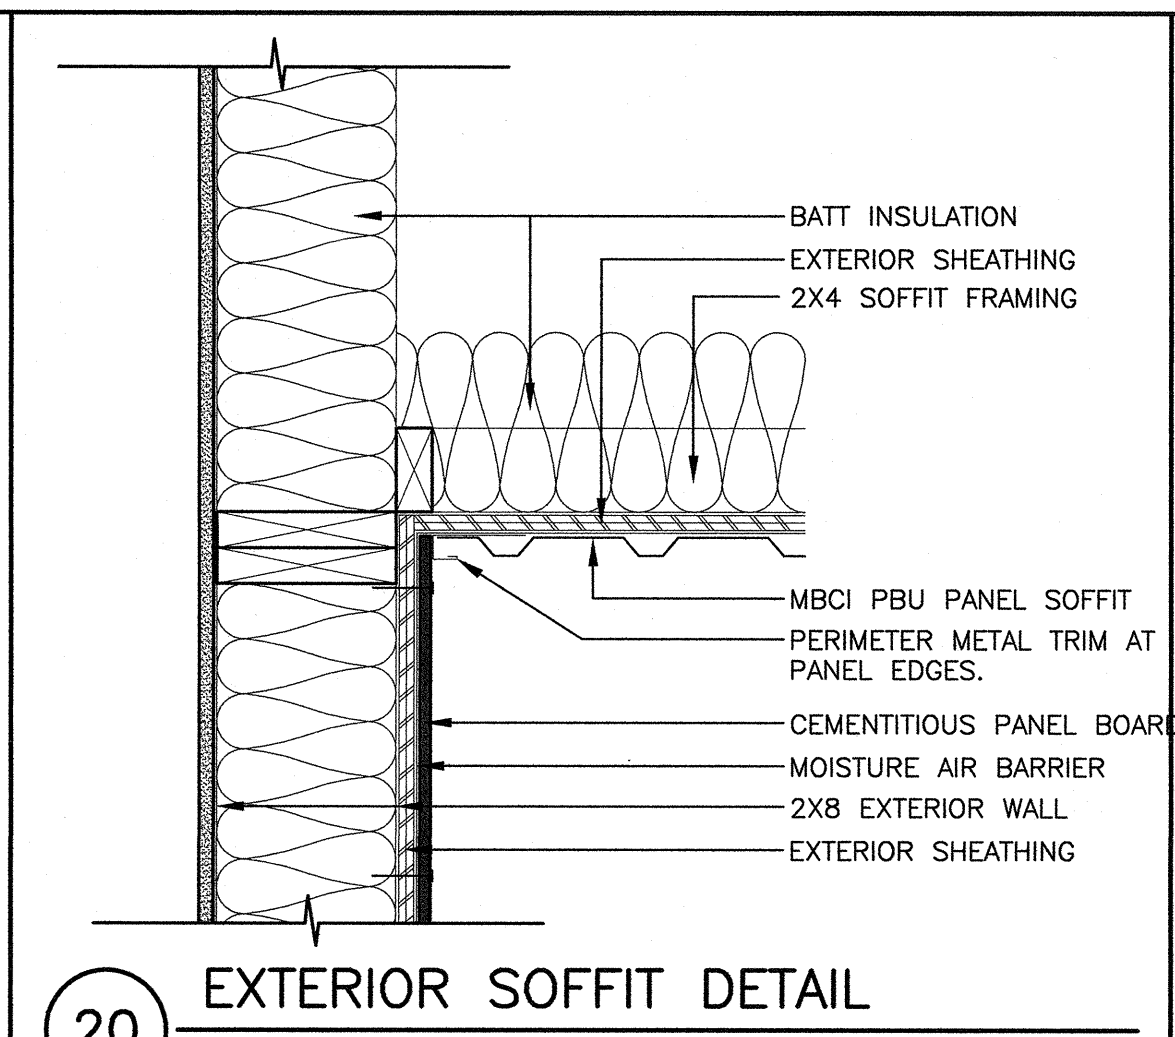

ONE AND ONE-HALF INCH = ONE FOOT
ONE INCH = ONE FOOT
THREE-QUARTERS INCH = ONE FOOT
ONE-HALF INCH = ONE FOOT
ONE-QUARTER INCH = ONE FOOT
ONE-EIGHTH INCH = ONE FOOT
ONE-SIXTEENTH INCH = ONE FOOT
ONE INCH = TWENTY FEET

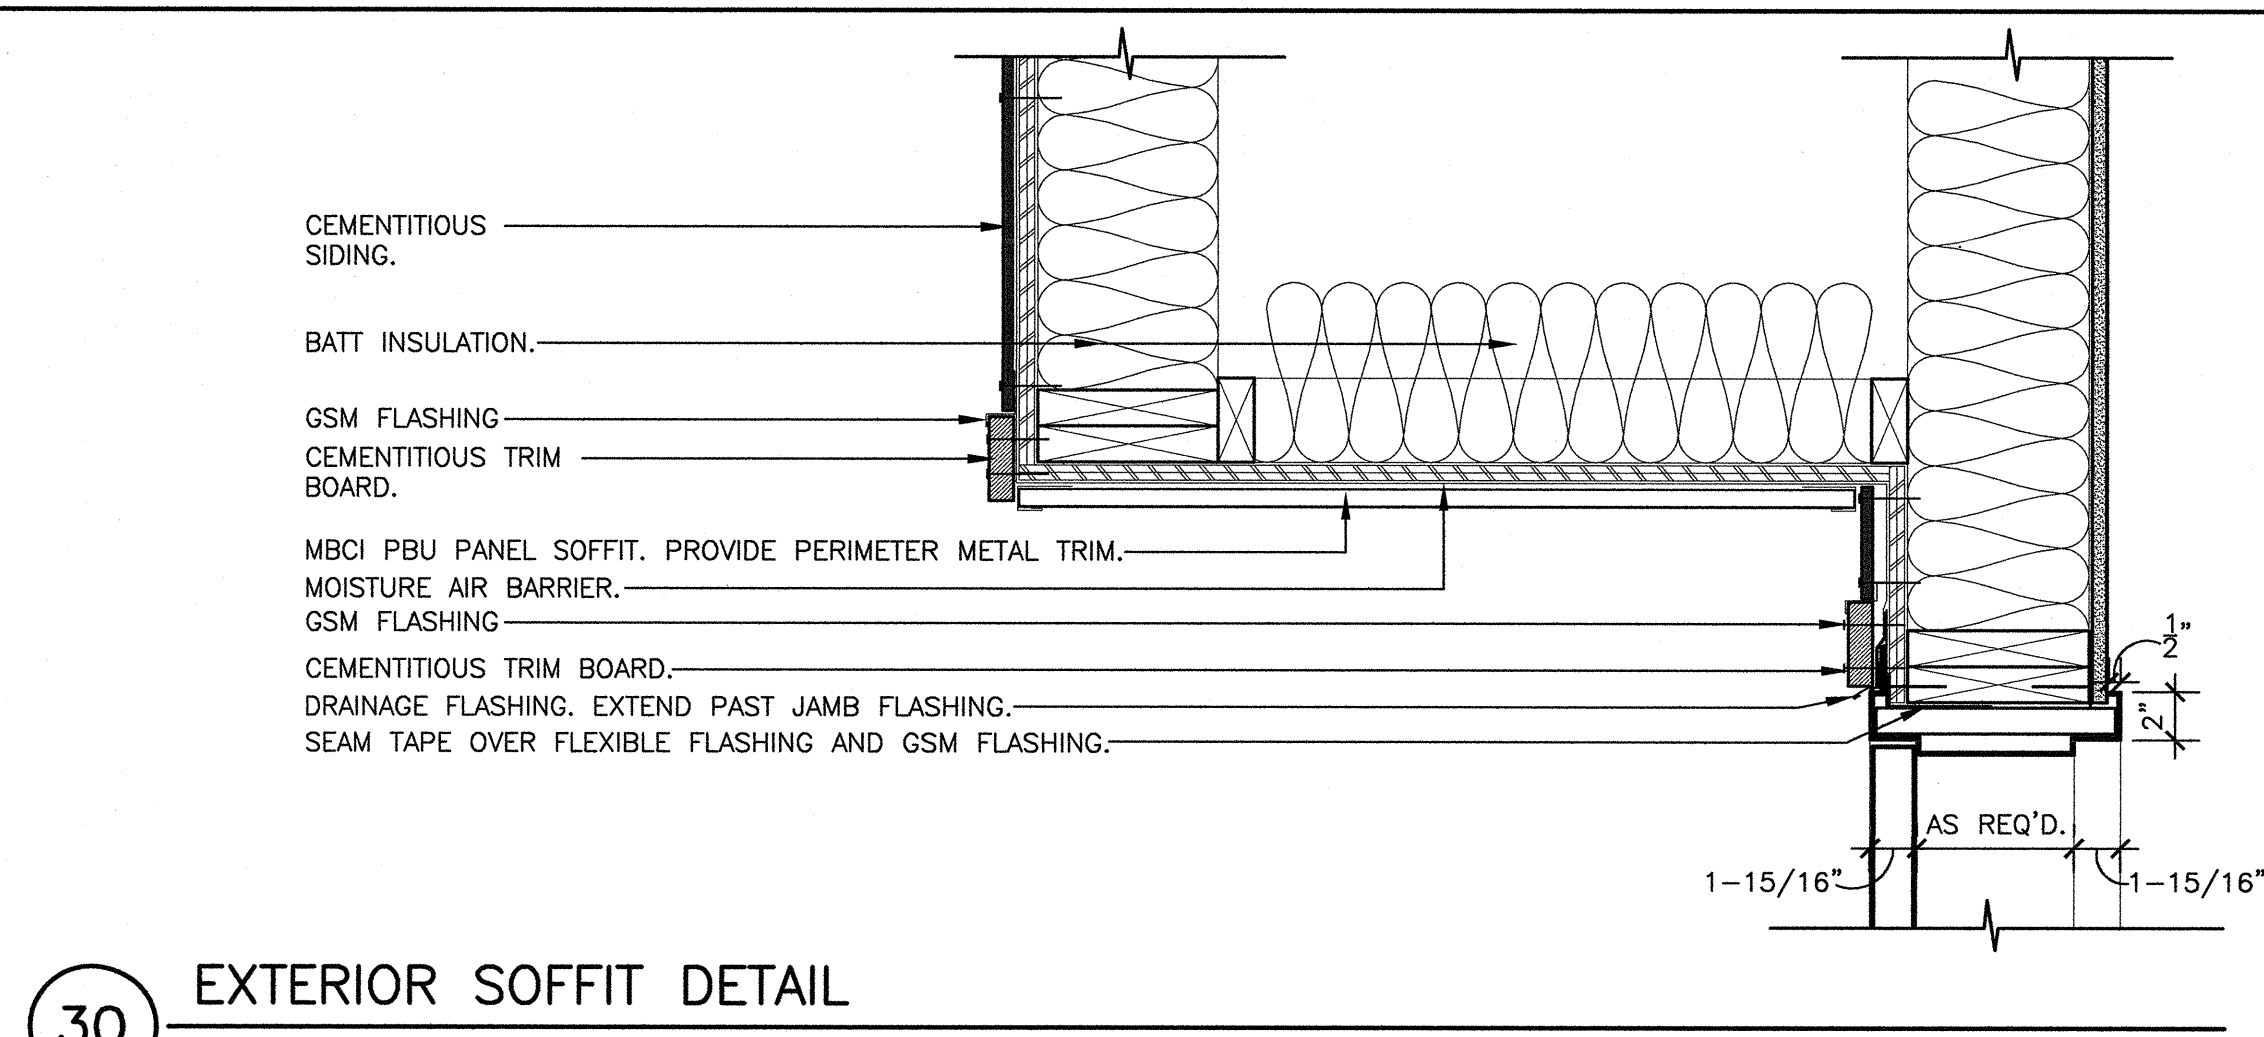

Dry Creek Joint Elementary School District
District Education Center

8849 Cook Riolo Road, Roseville, CA 95747

Dry Creek Joint Elementary School District

FILE NO. 31-15
IDENTIFICATION STAMP DIV. OF THE
STATE ARCHITECT OFFICE OF
REGULATION SERVICES
APPLICATION NO.
02-115456
AC. TM FLS NML SS PK
DATE 2/28/17 CC

DIVISION OF THE STATE ARCHITECT
revision date: _____ by: _____

CONSULTANT

nacht&lewis

600 O Street, Suite 100
Sacramento, CA 95811
www.nachtandlewis.com
916.329.4000

REGISTERED ARCHITECT
No. C-50867
RENEWAL DATE:
1/31/19
STATE OF CALIFORNIA

ARCHITECT

INITIAL BOX

NO.	DWG BY	DATE	REVIEWED

REVISIONS

NO.	DESCRIPTION	DATE	REV
	100% design development	7/6/16	
	75% construction documents	9/20/16	
	DSA submittal	12/31/16	
	DSA approval	02/23/17	

DATE February 23, 2017

JOB NO. Y1538.00

SHEET TITLE


Wall Types
and
Details

SHEET NO.

A8.5

SHEET ____ OF ____ TOTAL

SHEET ____ OF ____ TOTAL

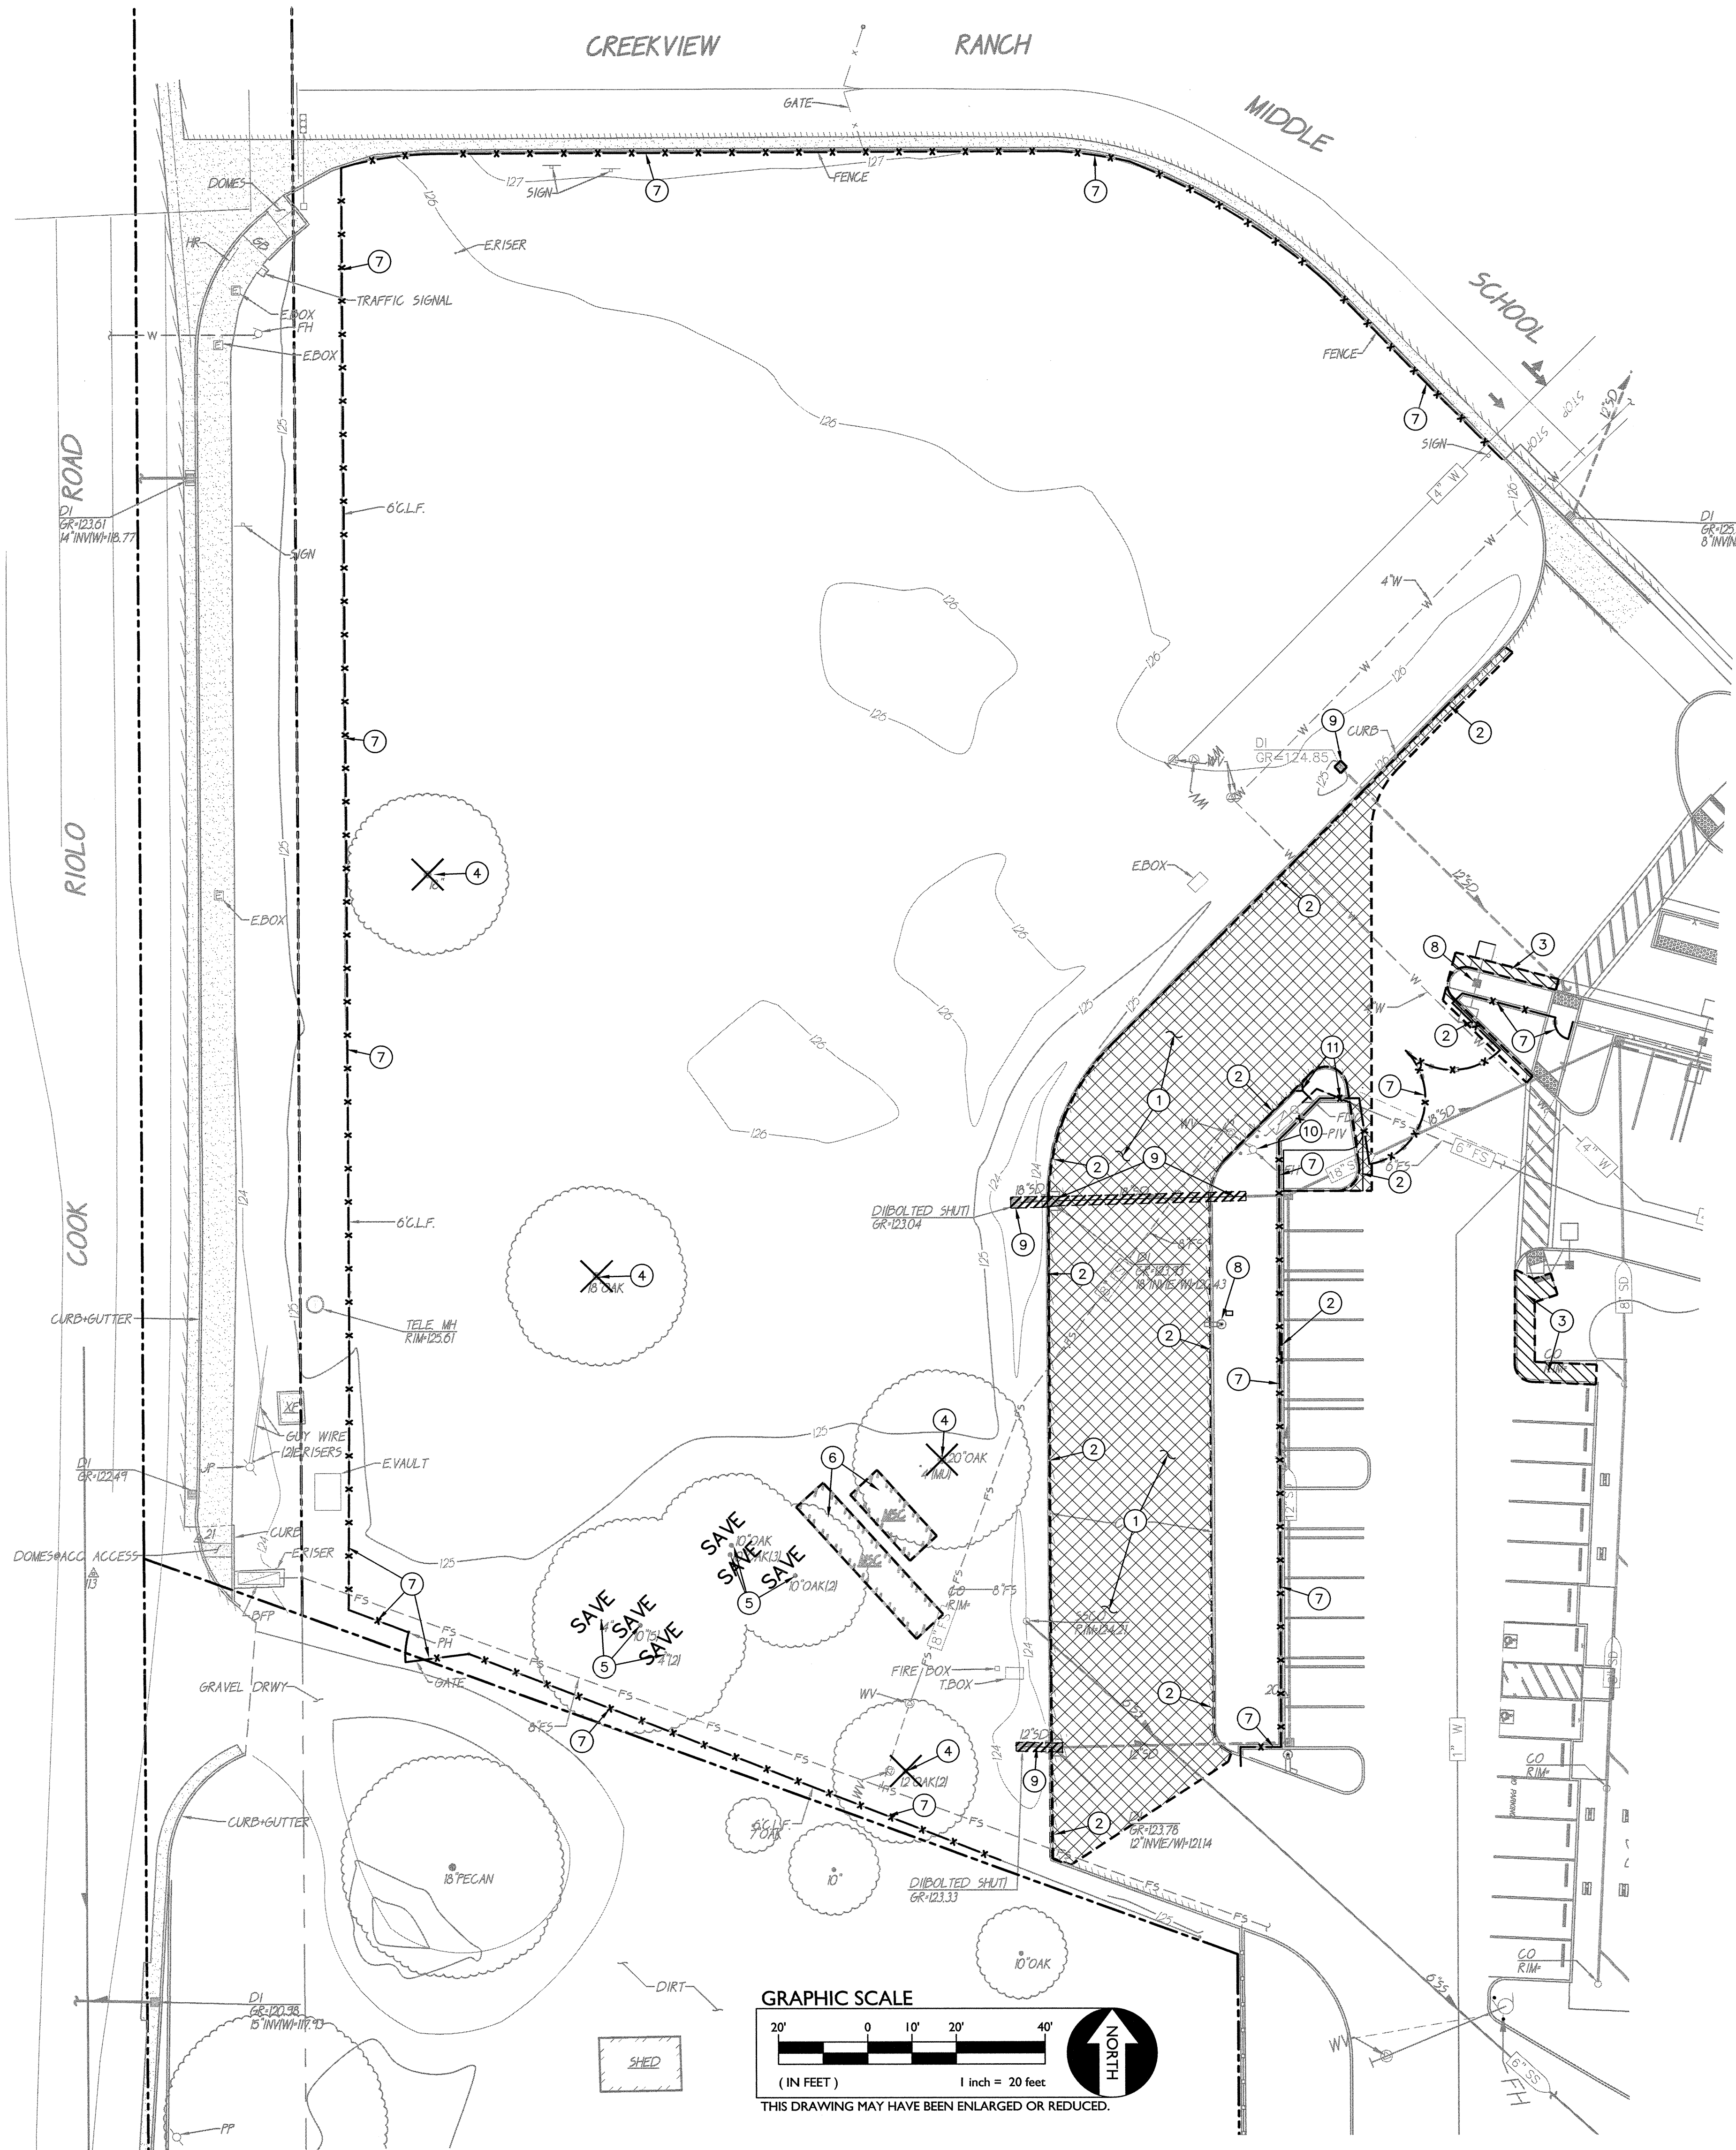

- DEMOLITION GENERAL NOTES**
- A. THE CONTRACTOR SHALL CONFORM TO CHAPTER 33, CALIFORNIA FIRE CODE (CFC), "FIRE SAFETY DURING CONSTRUCTION AND DEMOLITION, AT ALL TIMES DURING THE CONSTRUCTION PROCESS. A COPY OF THIS CHAPTER CAN BE PROVIDED TO THE CONTRACTOR AT HIS REQUEST.
- B. IN THE EVENT THAT ANY UNUSUAL CONDITIONS NOT COVERED BY THE GEOTECHNICAL INVESTIGATION REPORT OR ARE ENCOUNTERED DURING GRADING OPERATIONS THE GEOTECHNICAL ENGINEER AND THE ARCHITECT SHALL BE IMMEDIATELY NOTIFIED FOR DIRECTIONS.
- C. NO BURNING OR BLASTING SHALL BE PERMITTED.
- D. THE TYPES, LOCATIONS, SIZES AND/OR DEPTHS OF EXISTING UNDERGROUND UTILITIES AS SHOWN ON THESE PLANS WERE OBTAINED FROM SOURCES OF VARYING RELIABILITY. THE CONTRACTOR IS CAUTIONED THAT ONLY ACTUAL EXCAVATION WILL REVEAL THE TYPES, EXTENT, SIZES, LOCATIONS, AND DEPTHS OF SUCH UNDERGROUND UTILITIES. A REASONABLE EFFORT HAS BEEN MADE TO LOCATE AND DELINEATE ALL KNOWN UNDERGROUND UTILITIES. HOWEVER, WARREN CONSULTING ENGINEERS CAN ASSUME NO RESPONSIBILITY FOR THE COMPLETENESS OR ACCURACY OF ITS IDENTIFICATION OF SUCH UNDERGROUND UTILITIES, NOR FOR THE EXISTENCE OF OTHER BURIED OBJECTS OR UTILITIES WHICH MAY BE ENCOUNTERED BUT WHICH ARE NOT SHOWN ON THESE DRAWINGS. THE CONTRACTOR OR ANY SUBCONTRACTOR FOR THIS CONTRACT SHALL NOTIFY THE DISTRICT MEMBERS OF THE U.S.A. (2) WORKING DAYS IN ADVANCE OF PERFORMING ANY EXCAVATION WORK IN ORDER TO VERIFY TO THE GREATEST EXTENT POSSIBLE THE EXISTING UTILITY LINES, CONFLICTS AND PROPOSED UTILITY CONNECTION POINTS. CALL USA TOLL FREE AT 1-800-227-2600.
- E. ADDITIONAL DEMOLITION INFORMATION MAY BE SHOWN ON THE GRADING, DRAINAGE, UTILITY, LANDSCAPE PLANS AND THOSE PLANS PREPARED BY OTHER DISCIPLINES FOR THIS PROJECT.
- F. ALL DEMOLISHED ITEMS SHALL BE DISPOSED OFFSITE AT A SUITABLE, LEGAL, DUMP SITE OR OTHER FACILITY.
- G. ALL DISPOSED MATERIALS SHALL BE RECYCLED IF POSSIBLE.
- H. ALL TRENCHING THROUGH EXISTING ASPHALT PAVEMENT, CONCRETE OR LANDSCAPE SURFACES SHALL BE REMOVED AND REPLACED BACK TO ORIGINAL THICKNESS AND SURFACE.
- I. ALL EXISTING SURFACE-SUBSTRATE ADJACENT TO ITEMS OF WORK SHALL BE RESTORED TO ORIGINAL CONDITION.
- J. ALL TURF AREAS DISTURBED SHALL BE REPLACED WITH SOD.

Dry Creek Joint Elementary School District
District Education Center

8849 Cook Riolo Road, Roseville, CA 95747

Dry Creek Joint Elementary School District


FILE NO. 31-15

IDENTIFICATION STAMP DIV. OF THE
STATE ARCHITECT OFFICE OF
REGULATION SERVICES

APPLICATION NO.
02-115456

AC TM FLS 166 SS P2
DATE 2/23/17 CLAREAZ


revision date: _____ by: _____

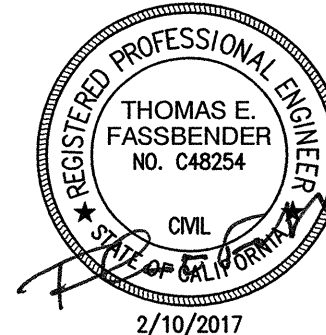

WARREN CONSULTING ENGINEERS, INC.
1117 WINDFIELD WAY, SUITE 110
EL DORADO HILLS, CA 95672
CONSULTANT

nacht&lewis

600 Q Street, Suite 110
Sacramento, CA 95811
www.nachtley.com
916.329.4000

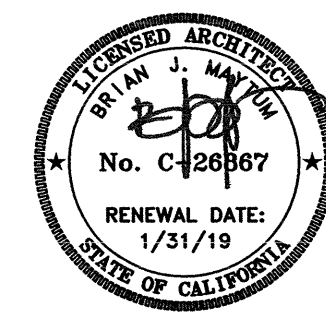

ARCHITECT

INITIAL BOX			
NO.	DWG BY	DATE	REVIEWED

REVISIONS			
NO.	DESCRIPTION	DATE	REV
	100% design development	7/8/16	
	75% construction documents	9/20/16	
	DSA submittal	10/18/16	
	DSA approval	02/23/17	

DATE	February 23, 2017
------	-------------------

JOB NO. Y1538.00

SHEET TITLE


Demolition Plan

SHEET NO. _____

C1.1

SHEET ____ OF ____ TOTAL

ONE AND ONE-HALF INCH = ONE FOOT
ONE INCH = ONE FOOT
THREE-QUARTERS INCH = ONE FOOT
ONE-HALF INCH = ONE FOOT
ONE-QUARTER INCH = ONE FOOT
ONE-EIGHTH INCH = ONE FOOT
ONE-SIXTEENTH INCH = ONE FOOT
ONE INCH = TWENTY FEET

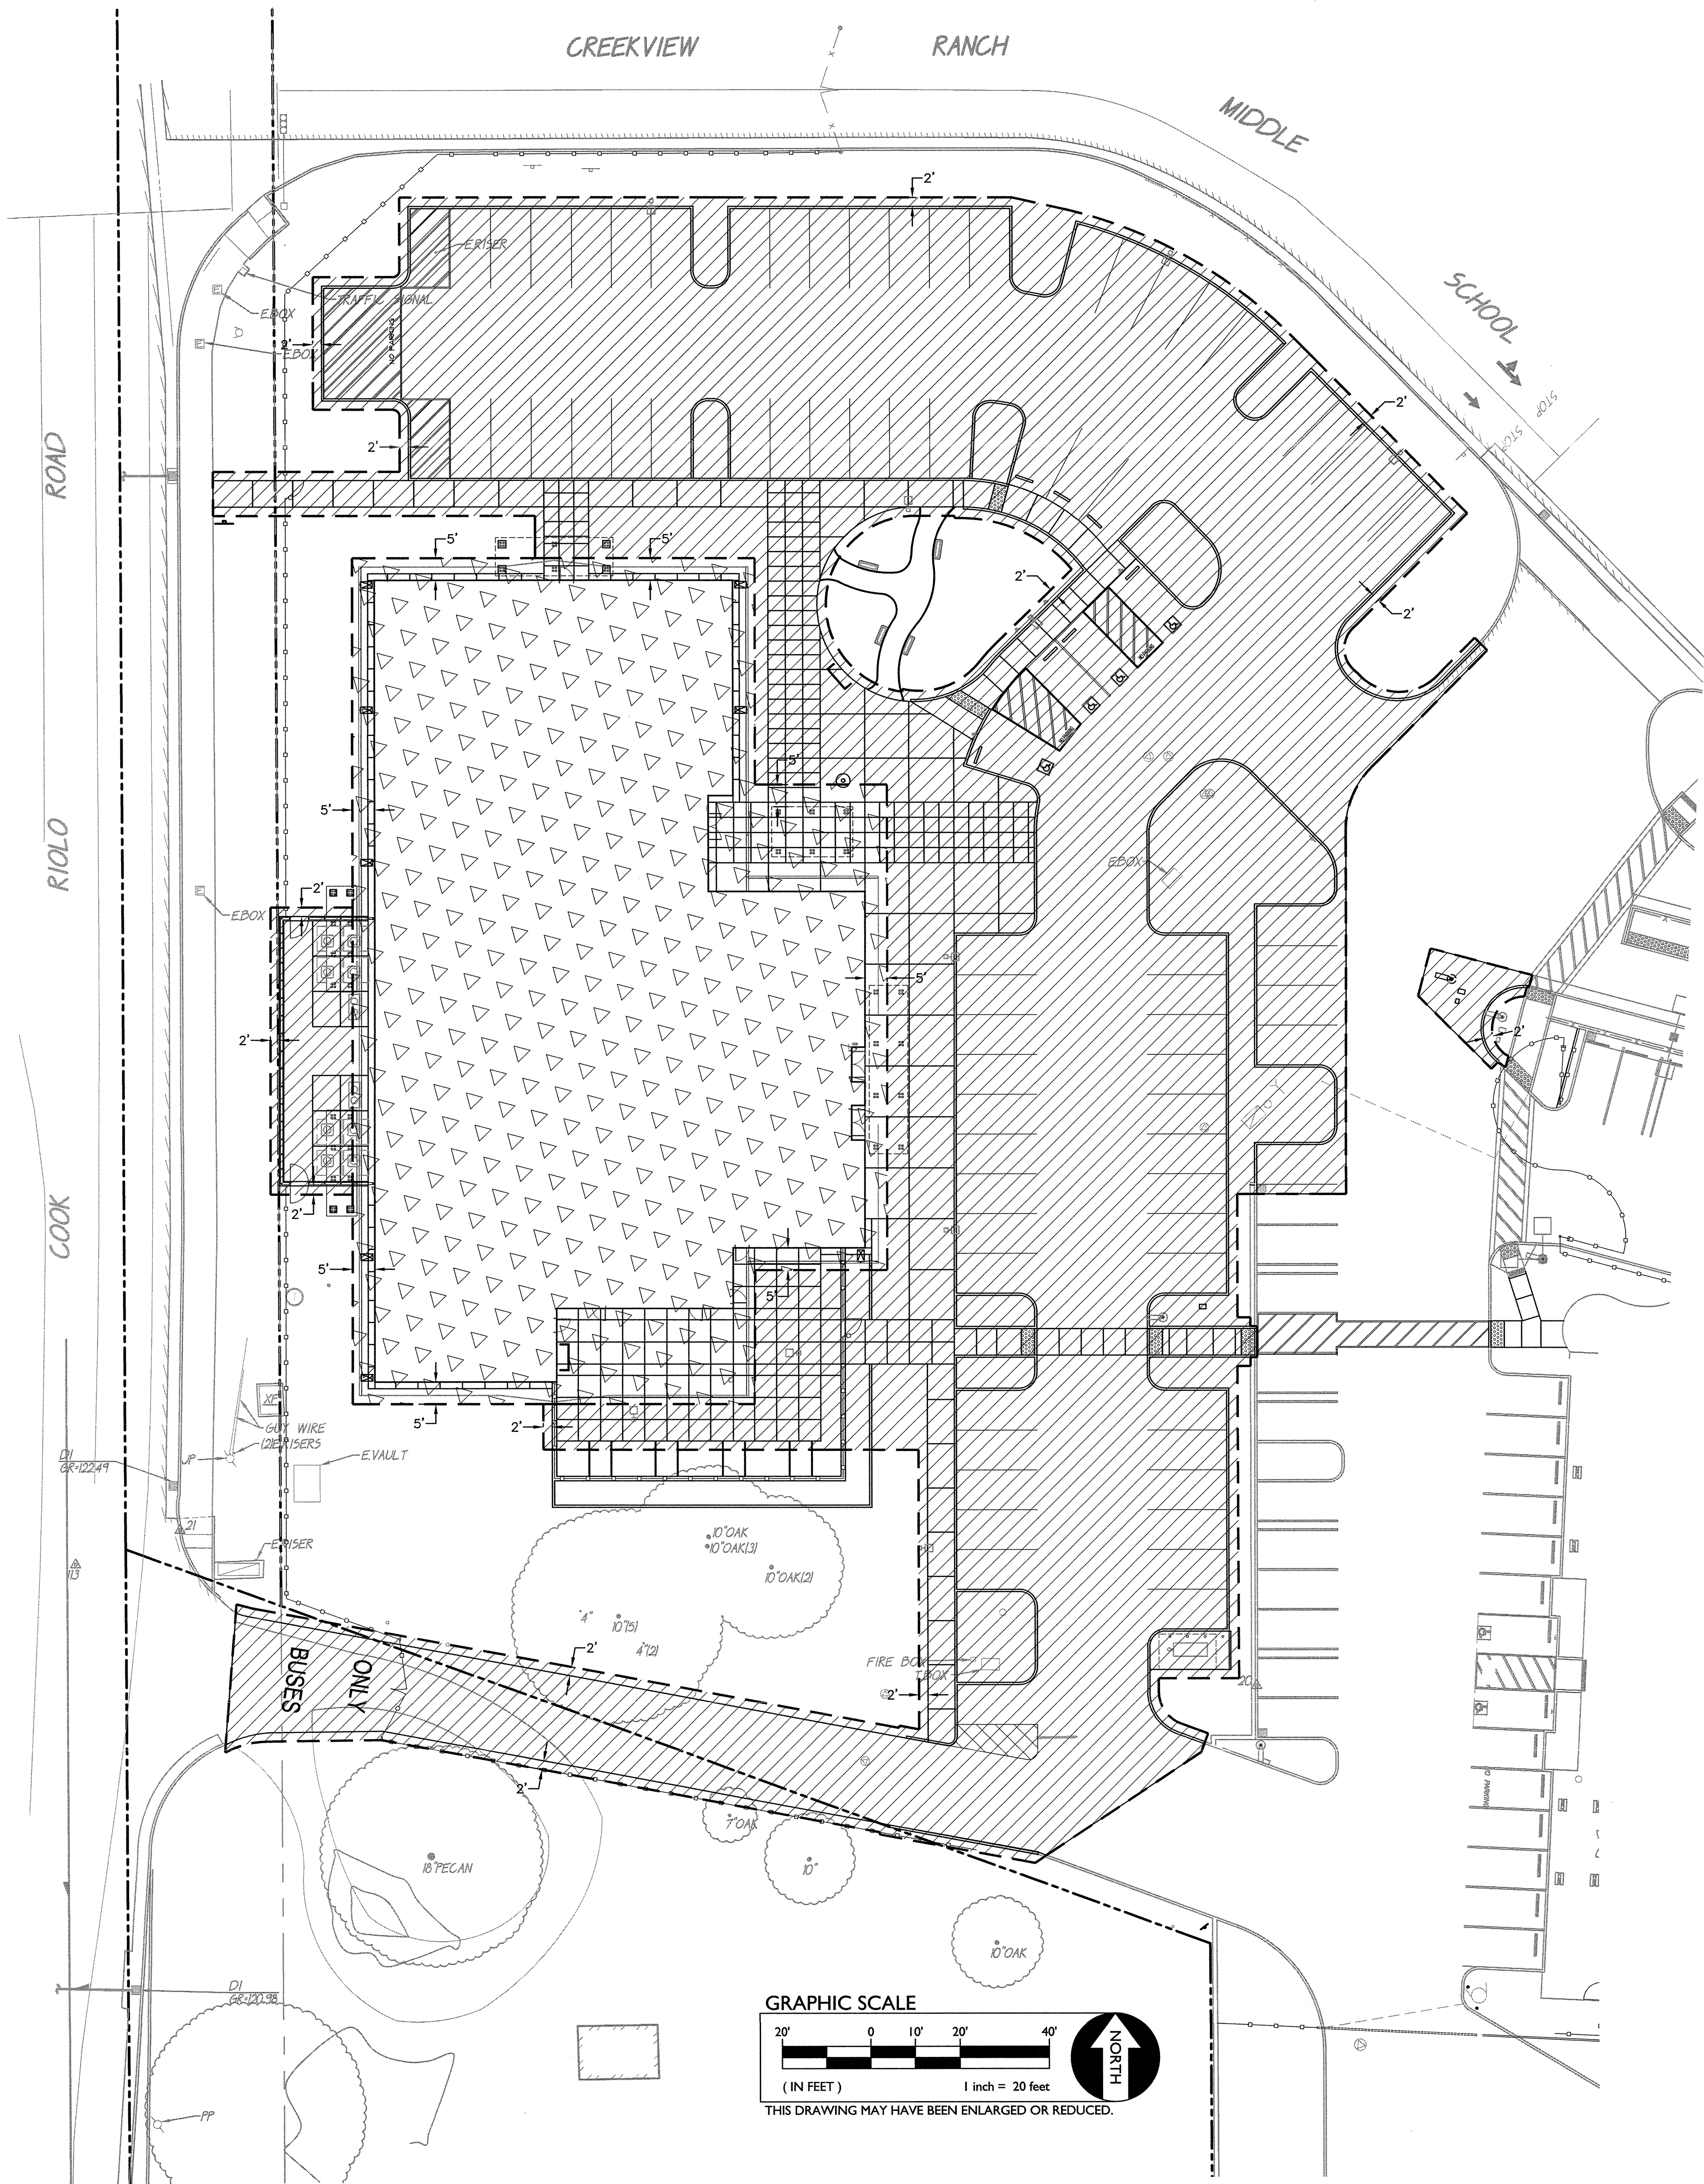

- SUBGRADE PREPARATION NOTES**
FOLLOWING SITE CLEARING, STRIPPING, AND DEMOLITION ACTIVITIES:
- BUILDING:**
- OVER-EXCAVATE BUILDING PAD TO A DEPTH 24" BELOW LOWEST FOOTING, A MINIMUM OF 3 1/2 FEET BELOW EXISTING SITE GRADES OR A DEPTH THAT COMPLETELY REMOVES THE UNDOCUMENTED FILLS, WHICHEVER IS DEEPER.
- FLATWORK/PAVING**
- OVER EXCAVATE 12" BELOW FLATWORK/PAVEMENT SUBGRADE, 12" BELOW EXISTING GRADE OR A DEPTH THAT COMPLETELY REMOVES THE UNDOCUMENTED FILLS, WHICHEVER IS DEEPER.
 - FOLLOWING OVER-EXCAVATION SCARIFY EXPOSED SOILS TO A DEPTH OF AT LEAST 12 INCHES AND MOISTURE CONDITION TO AT LEAST THE OPTIMUM MOISTURE CONTENT AND COMPACT TO AT LEAST 90 PERCENT OF THE MAXIMUM DRY DENSITY.
 - PLACE ENGINEERED FILL IN HORIZONTAL LIFTS NOT EXCEEDING SIX INCHES IN COMPACTED THICKNESS. EACH LAYER SHOULD BE THOROUGHLY MOISTURE CONDITIONED TO AT LEAST THE OPTIMUM MOISTURE CONTENT AND UNIFORMLY COMPACTED TO AT LEAST 90 PERCENT OF THE MAXIMUM DRY DENSITY.
 - THE UPPER 12 INCHES OF FINAL BUILDING PAD SUBGRADES SHALL BE BROUGHT TO AT LEAST THE OPTIMUM MOISTURE CONTENT AND UNIFORMLY COMPACTED TO NOT LESS THEN 90 PERCENT OF THE MAXIMUM DRY DENSITY. THE UPPER SIX INCHES OF FINAL PAVEMENT AND FLATWORK SUBGRADES SHALL BE UNIFORMLY MOISTURE CONDITIONED TO AT LEAST OPTIMUM MOISTURE CONTENT, PROCESSED, AND UNIFORMLY COMPACTED TO AT LEAST 95 PERCENT OF MAXIMUM DRY DENSITY.
 - SOIL TREATMENT AND SUBGRADE PREPARATION REQUIREMENTS FOR THE BUILDING PAD SHALL EXTEND AT LEAST 5 FEET BEYOND EDGE OF BUILDING.
 - SOIL TREATMENT AND SUBGRADE PREPARATION REQUIREMENTS FOR THE FLATWORK AND PAVEMENT SHALL BE AT LEAST TWO FEET BEYOND THE EDGE OF PAVEMENT WHEN NOT ABUTTING EXISTING PAVING.

Dry Creek Joint Elementary School District
District Education Center


FILE NO. 31-15
IDENTIFICATION STAMP DIV. OF THE
STATE ARCHITECT OFFICE OF
REGULATION SERVICES
APPLICATION NO.
02-115456
AC TM FLS HCSS
DATE 2/23/17

DIVISION OF THE STATE ARCHITECT
revision date: by:



WCE
WARREN CONSULTING ENGINEERS, INC.
1117 WINDFIELD WAY, SUITE 110
EL DORADO HILLS, CA 95672
CONSULTANT

nacht&lewis
600 Q Street, Suite 100
Sacramento, CA 95811
www.nachtandlewis.com
916.329.4000

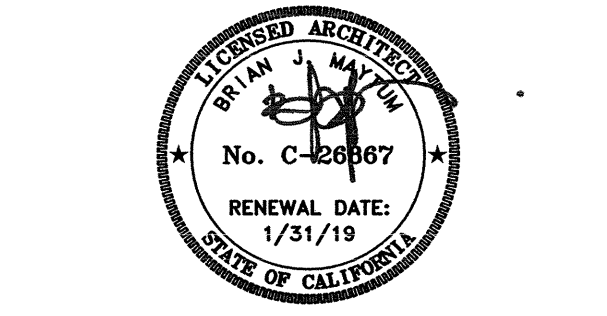

ARCHITECT

INITIAL BOX			
NO.	DWG BY	DATE	REVIEWED

REVISIONS			
NO.	DESCRIPTION	DATE	REV'D
	100% design development	7/8/16	
	75% construction documents	9/23/16	
	DSA submittal	10/18/16	
	DSA approval	02/23/17	

DATE February 23, 2017

JOB NO. Y1538.00

SHEET TITLE



Engineered Fill Plan

SHEET NO.


C1.2

SHEET OF TOTAL


ONE AND ONE-HALF INCH = ONE FOOT
THREE-QUARTERS INCH = ONE FOOT
ONE INCH = ONE FOOT
ONE-HALF INCH = ONE FOOT
ONE-QUARTER INCH = ONE FOOT
ONE-EIGHTH INCH = ONE FOOT
ONE-SIXTEENTH INCH = ONE FOOT
ONE INCH = TWENTY FEET

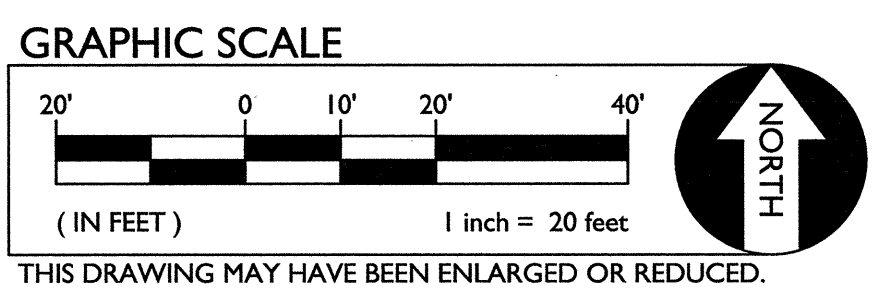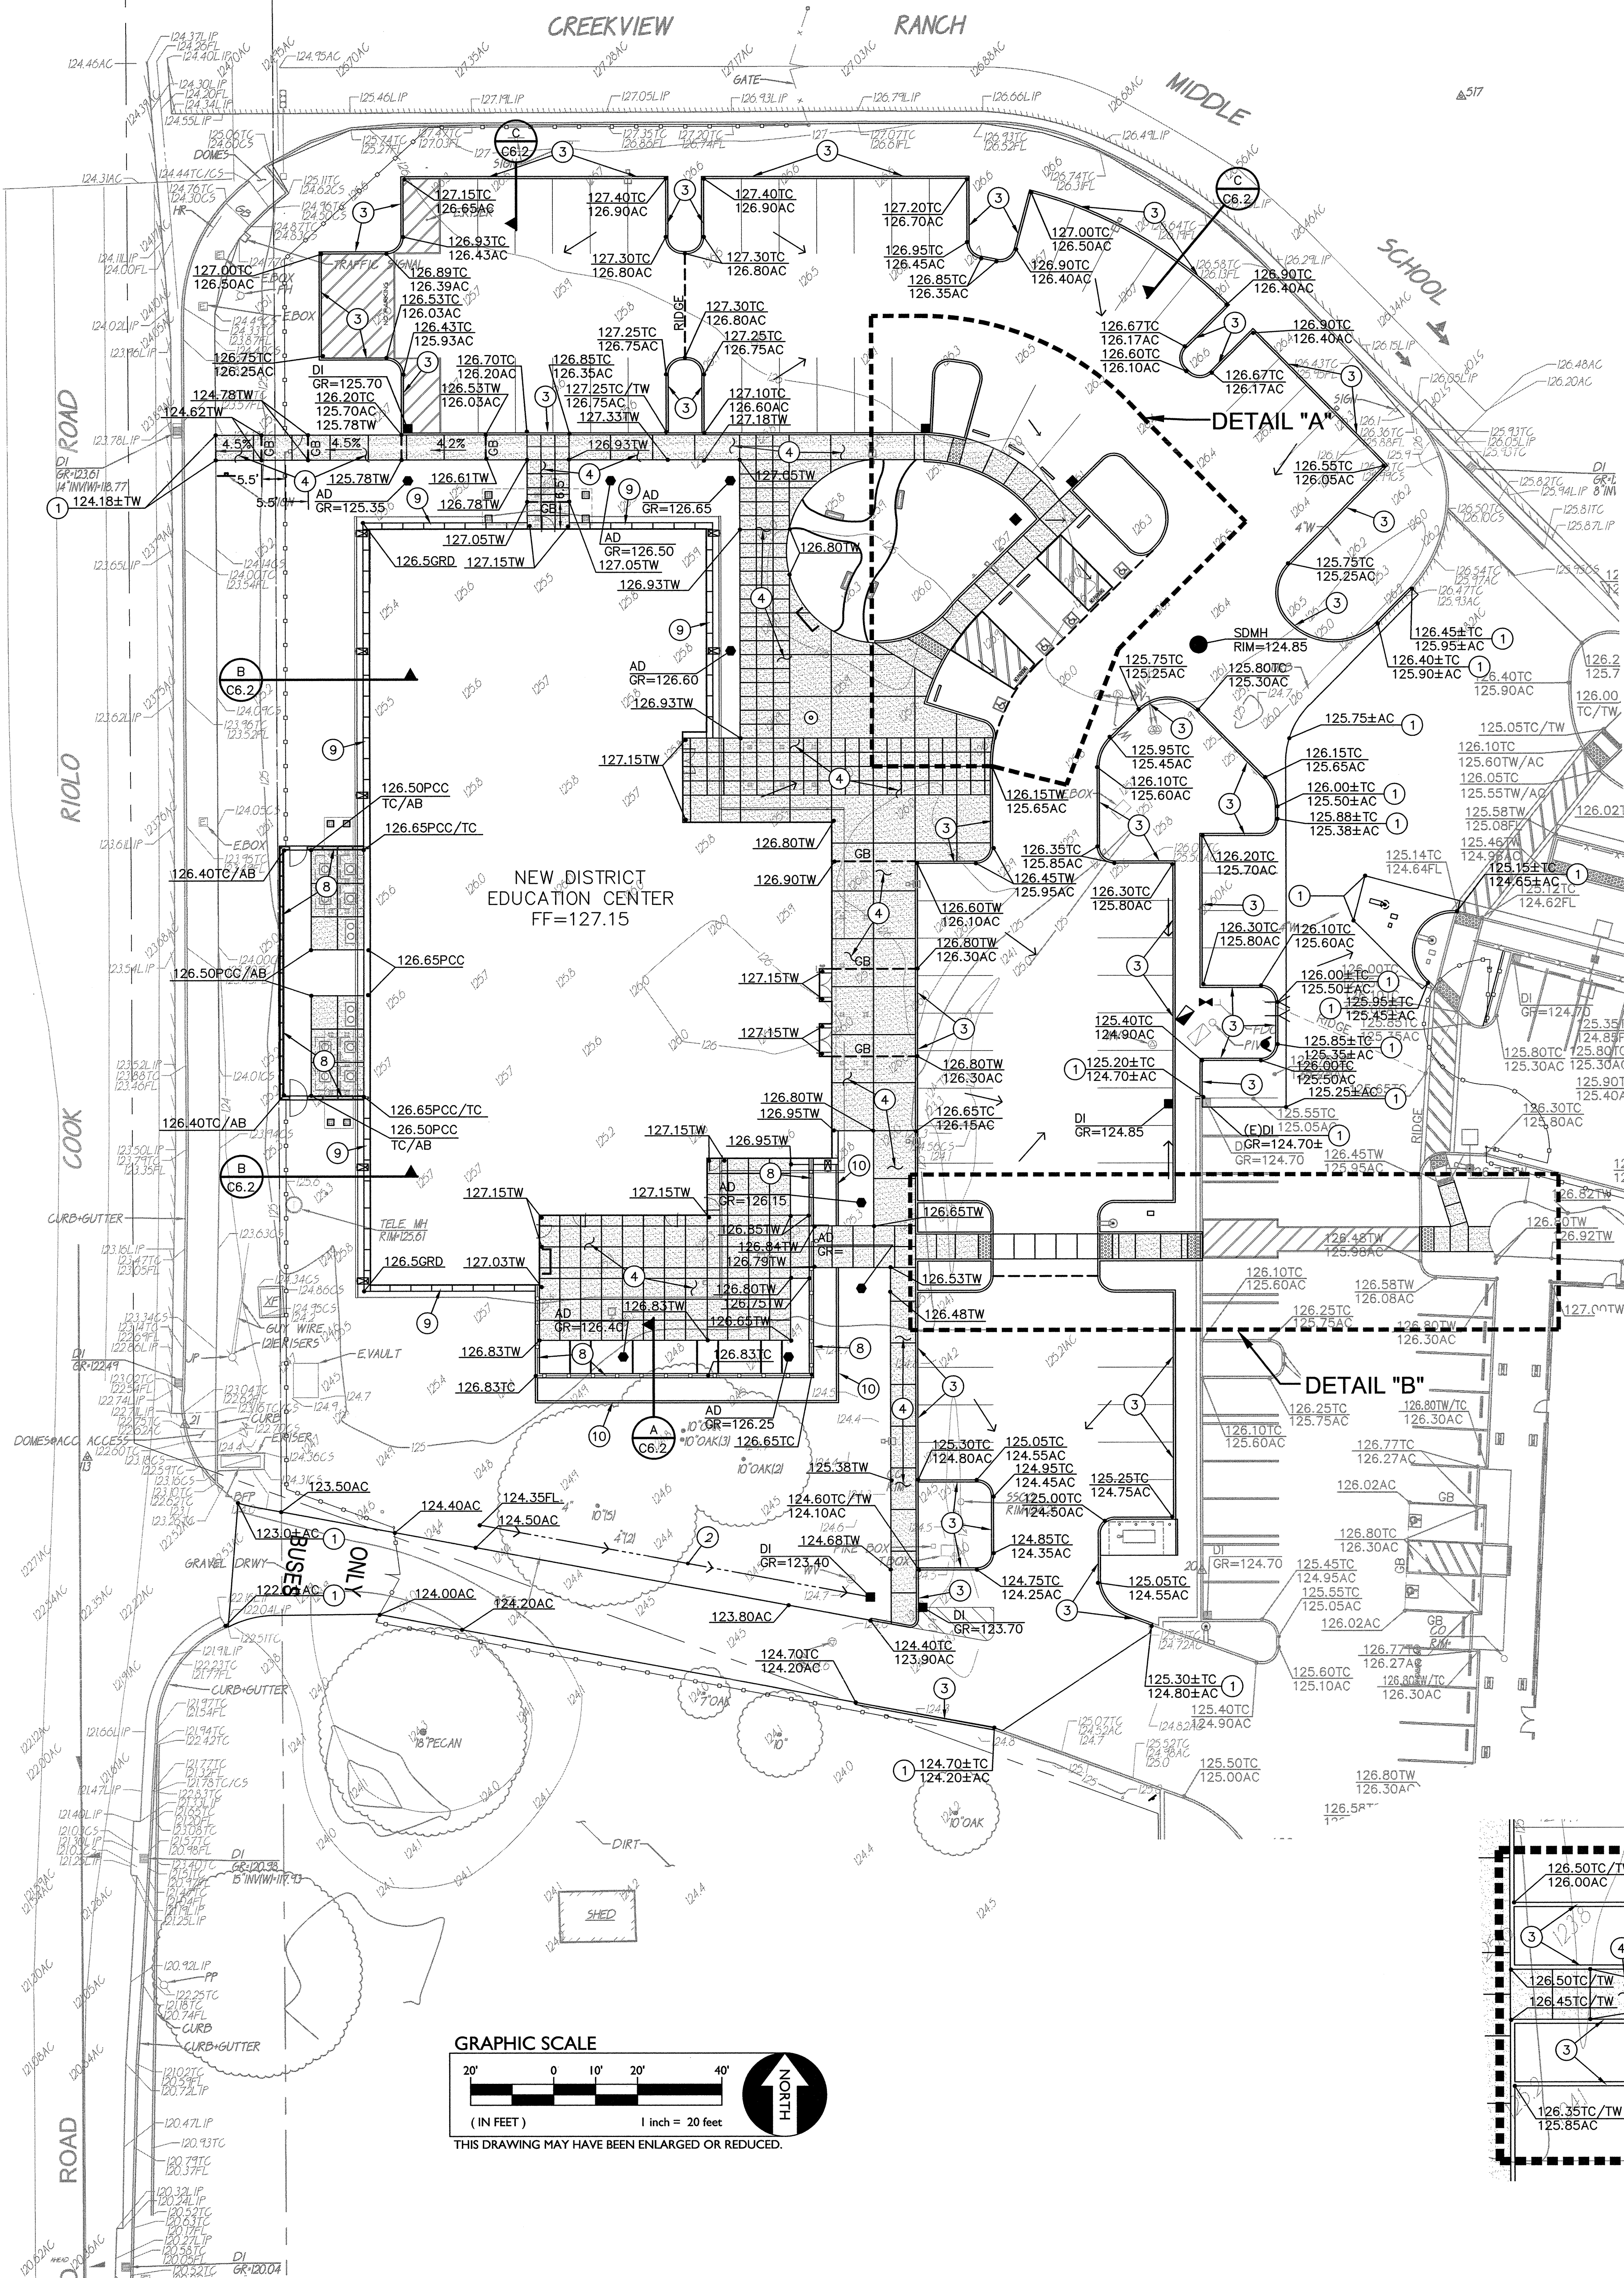

- GRADING NOTES
1. MATCH EXISTING GRADE/ELEVATION.
 2. GRADE UNIFORMLY.
 3. CONSTRUCT CONCRETE CURB PER C6.1
 4. CONSTRUCT CONCRETE SIDEWALK PER REFER TO PAVING PLAN FOR THICKNESS AND REINFORCEMENT REQUIREMENTS.
 5. PLACE CONCRETE WHEEL STOP PER C6.1
 6. CONSTRUCT CONCRETE CURB AND GUTTER PER C6.1
 7. CONSTRUCT VARIABLE HEIGHT CURB PER C6.1
 8. CONSTRUCT CURB FENCE APRON PER C6.2
 9. CONSTRUCT MOW STRIP PER C6.2
 10. CONSTRUCT LANDSCAPE CURB PER C6.2
 11. PLACE TRUNCATED DOMES PER ARCHITECTURAL PLANS.

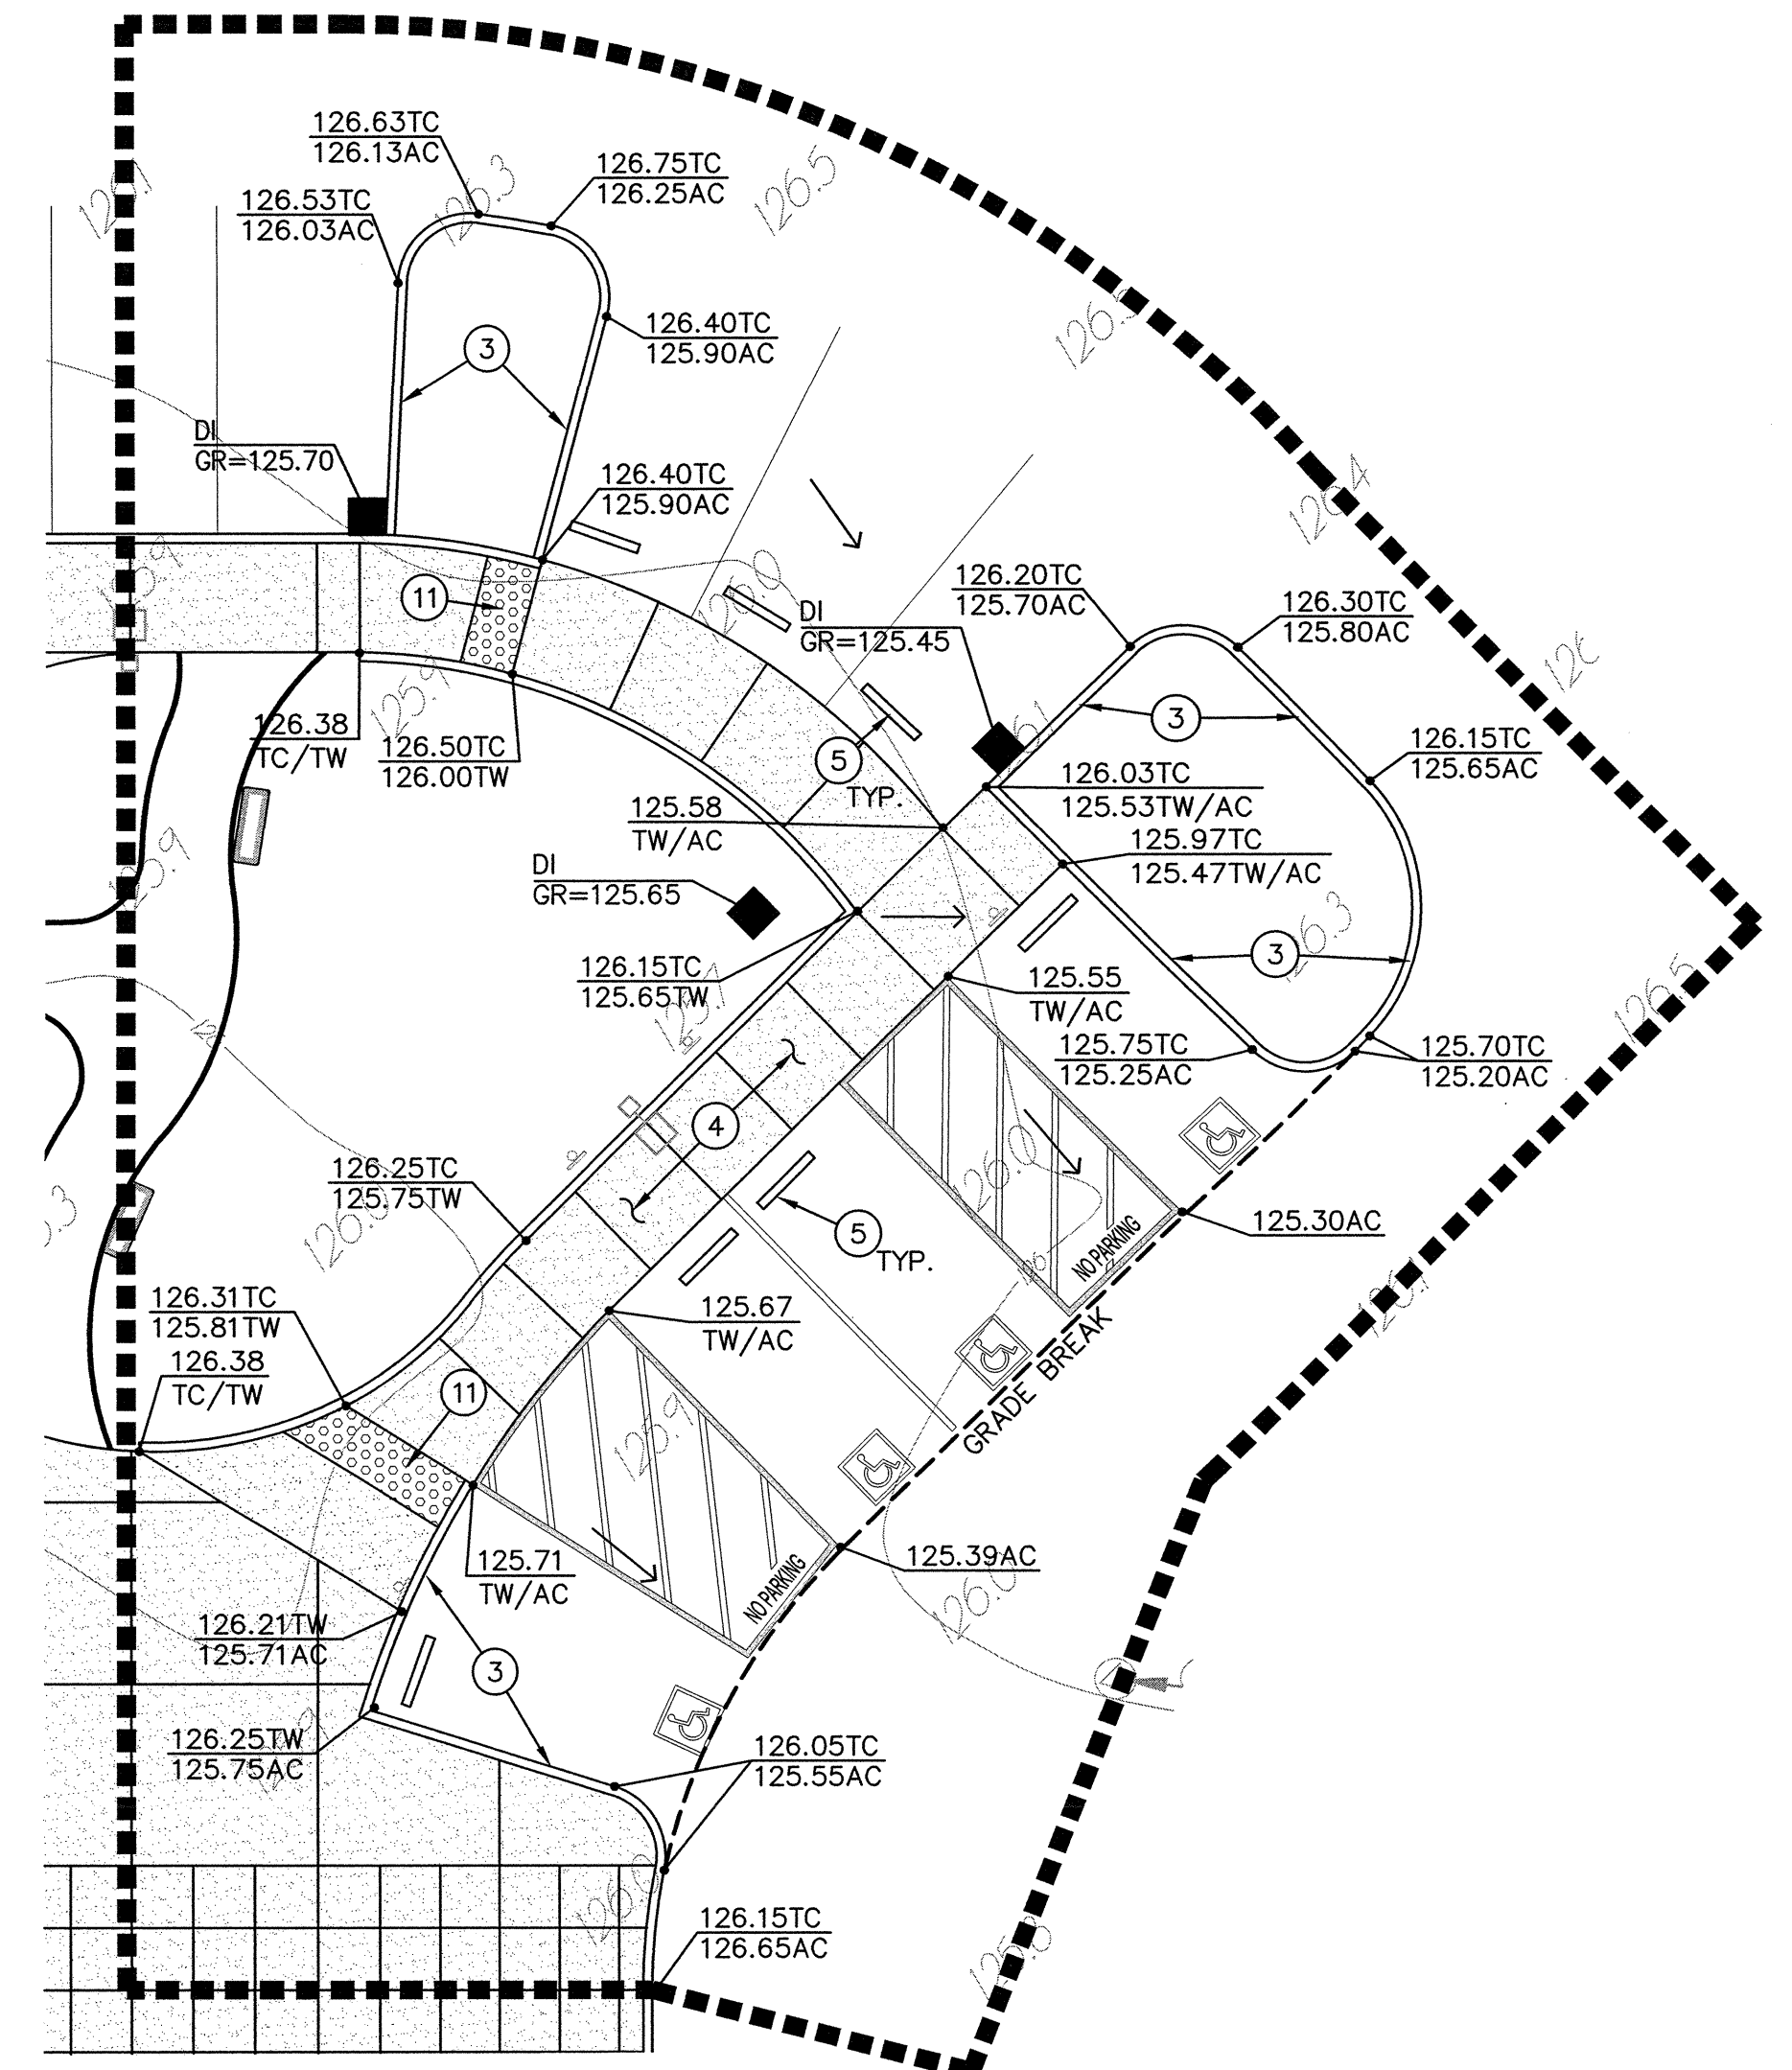

DETAIL "A"

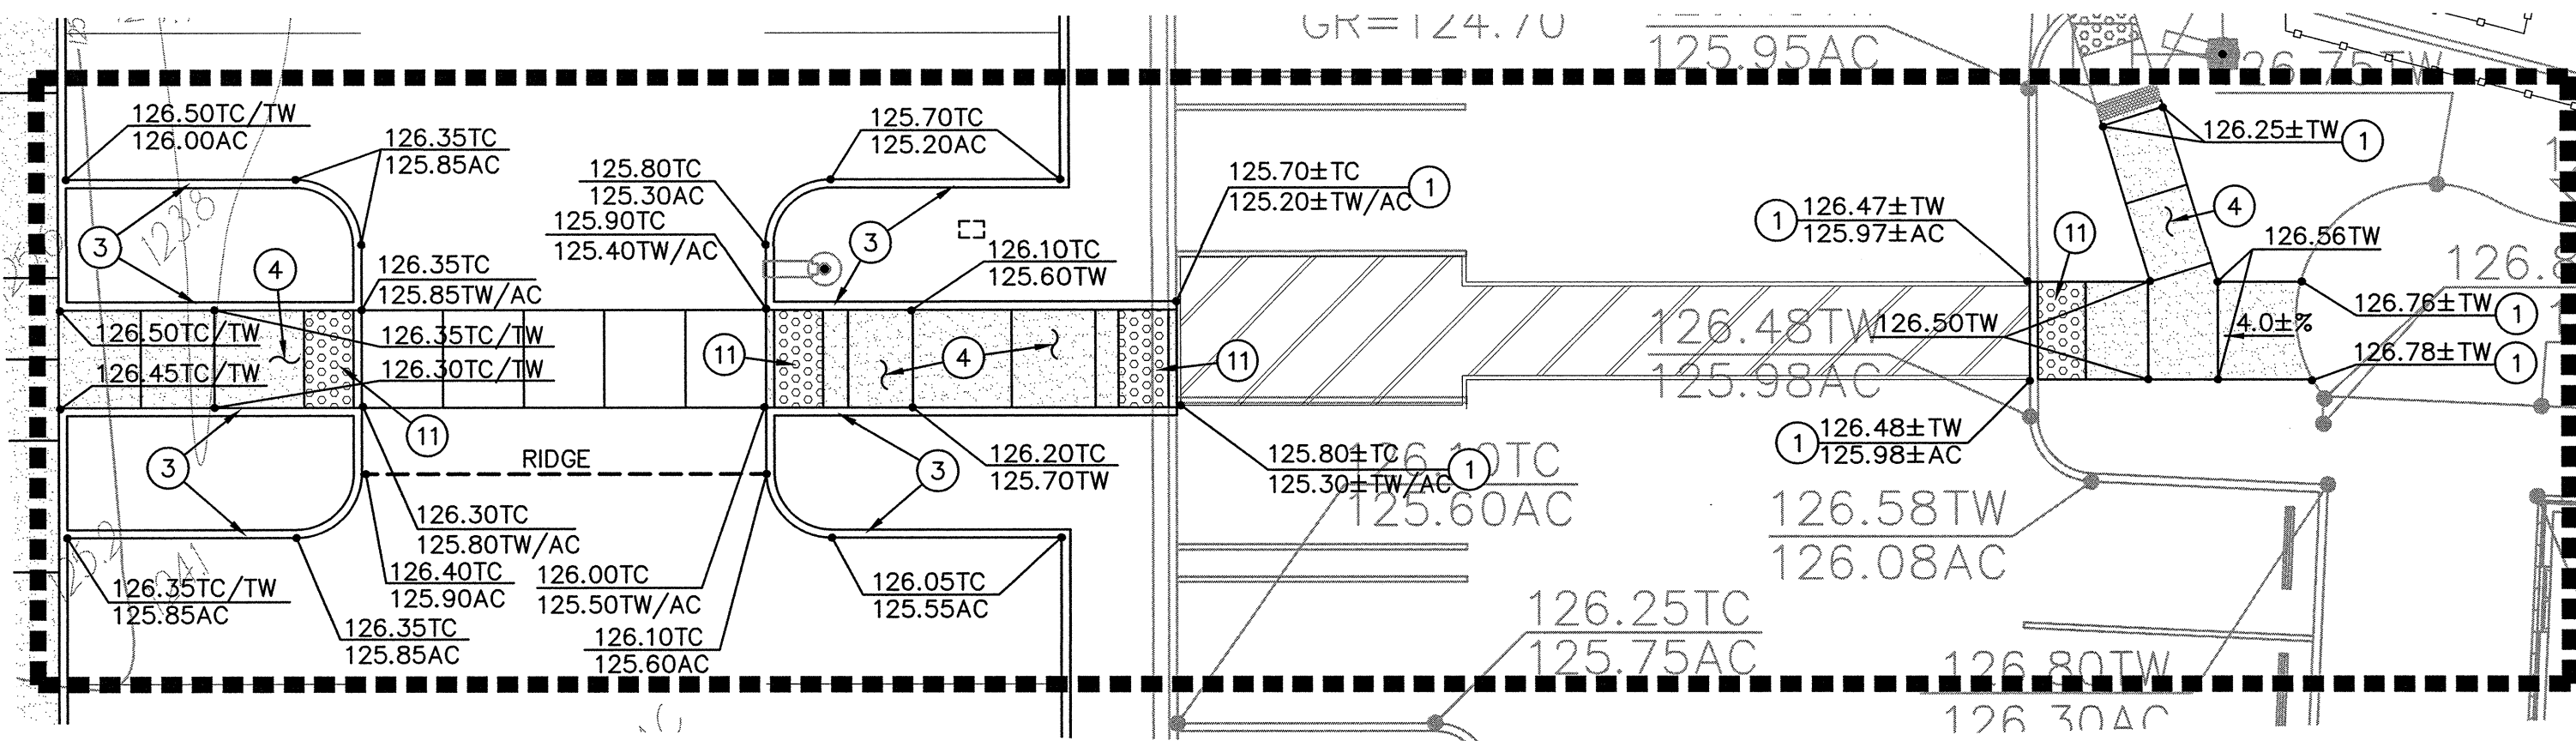

DETAIL "B"

Dry Creek Joint Elementary School District
District Education Center
8849 Cook Riolo Road, Roseville, CA 95747
Dry Creek Joint Elementary School District

FILE NO. 31-15
IDENTIFICATION STAMP DIV. OF THE
STATE ARCHITECT OFFICE OF
REGULATION SERVICES
APPLICATION NO.
02-115456
AC TM FL SS
DATE 2/23/17
DIVISION OF THE STATE ARCHITECT
revision date: by:
REGISTERED PROFESSIONAL ENGINEER
THOMAS E. FASSBENDER
No. 048254
2/10/2017
WCE
WARREN CONSULTING ENGINEERS, INC.
1117 WINDFIELD WAY, SUITE 110
EL DORADO HILLS, CA 95672
CONSULTANT

nacht&lewis
600 O Street, Suite 100
Sacramento, CA 95811
www.nachtandlewis.com
916.329.4000
REGISTERED ARCHITECT
No. C-53667
RENEWAL DATE:
1/31/19
STATE OF CALIFORNIA

ARCHITECT

INITIAL BOX			
NO.	DWG BY	DATE	REVIEWED


REVISIONS

NO.	DESCRIPTION	DATE	REV
1	100% design development	7/8/16	
2	75% construction documents	9/20/16	
3	DSA submittal	10/18/16	
4	DSA approval	02/23/17	

DATE February 23, 2017
JOB NO. Y1538.00
SHEET TITLE

Grading Plan
SHEET NO.
C2.1
SHEET OF TOTAL

ONE INCH = TWENTY FEET
ONE-SIXTEENTH INCH = ONE FOOT
ONE-EIGHTH INCH = ONE FOOT
ONE-FOURTH INCH = ONE FOOT
ONE-HALF INCH = ONE FOOT
THREE-QUARTERS INCH = ONE FOOT
ONE INCH = ONE FOOT
ONE AND ONE-HALF INCH = ONE FOOT

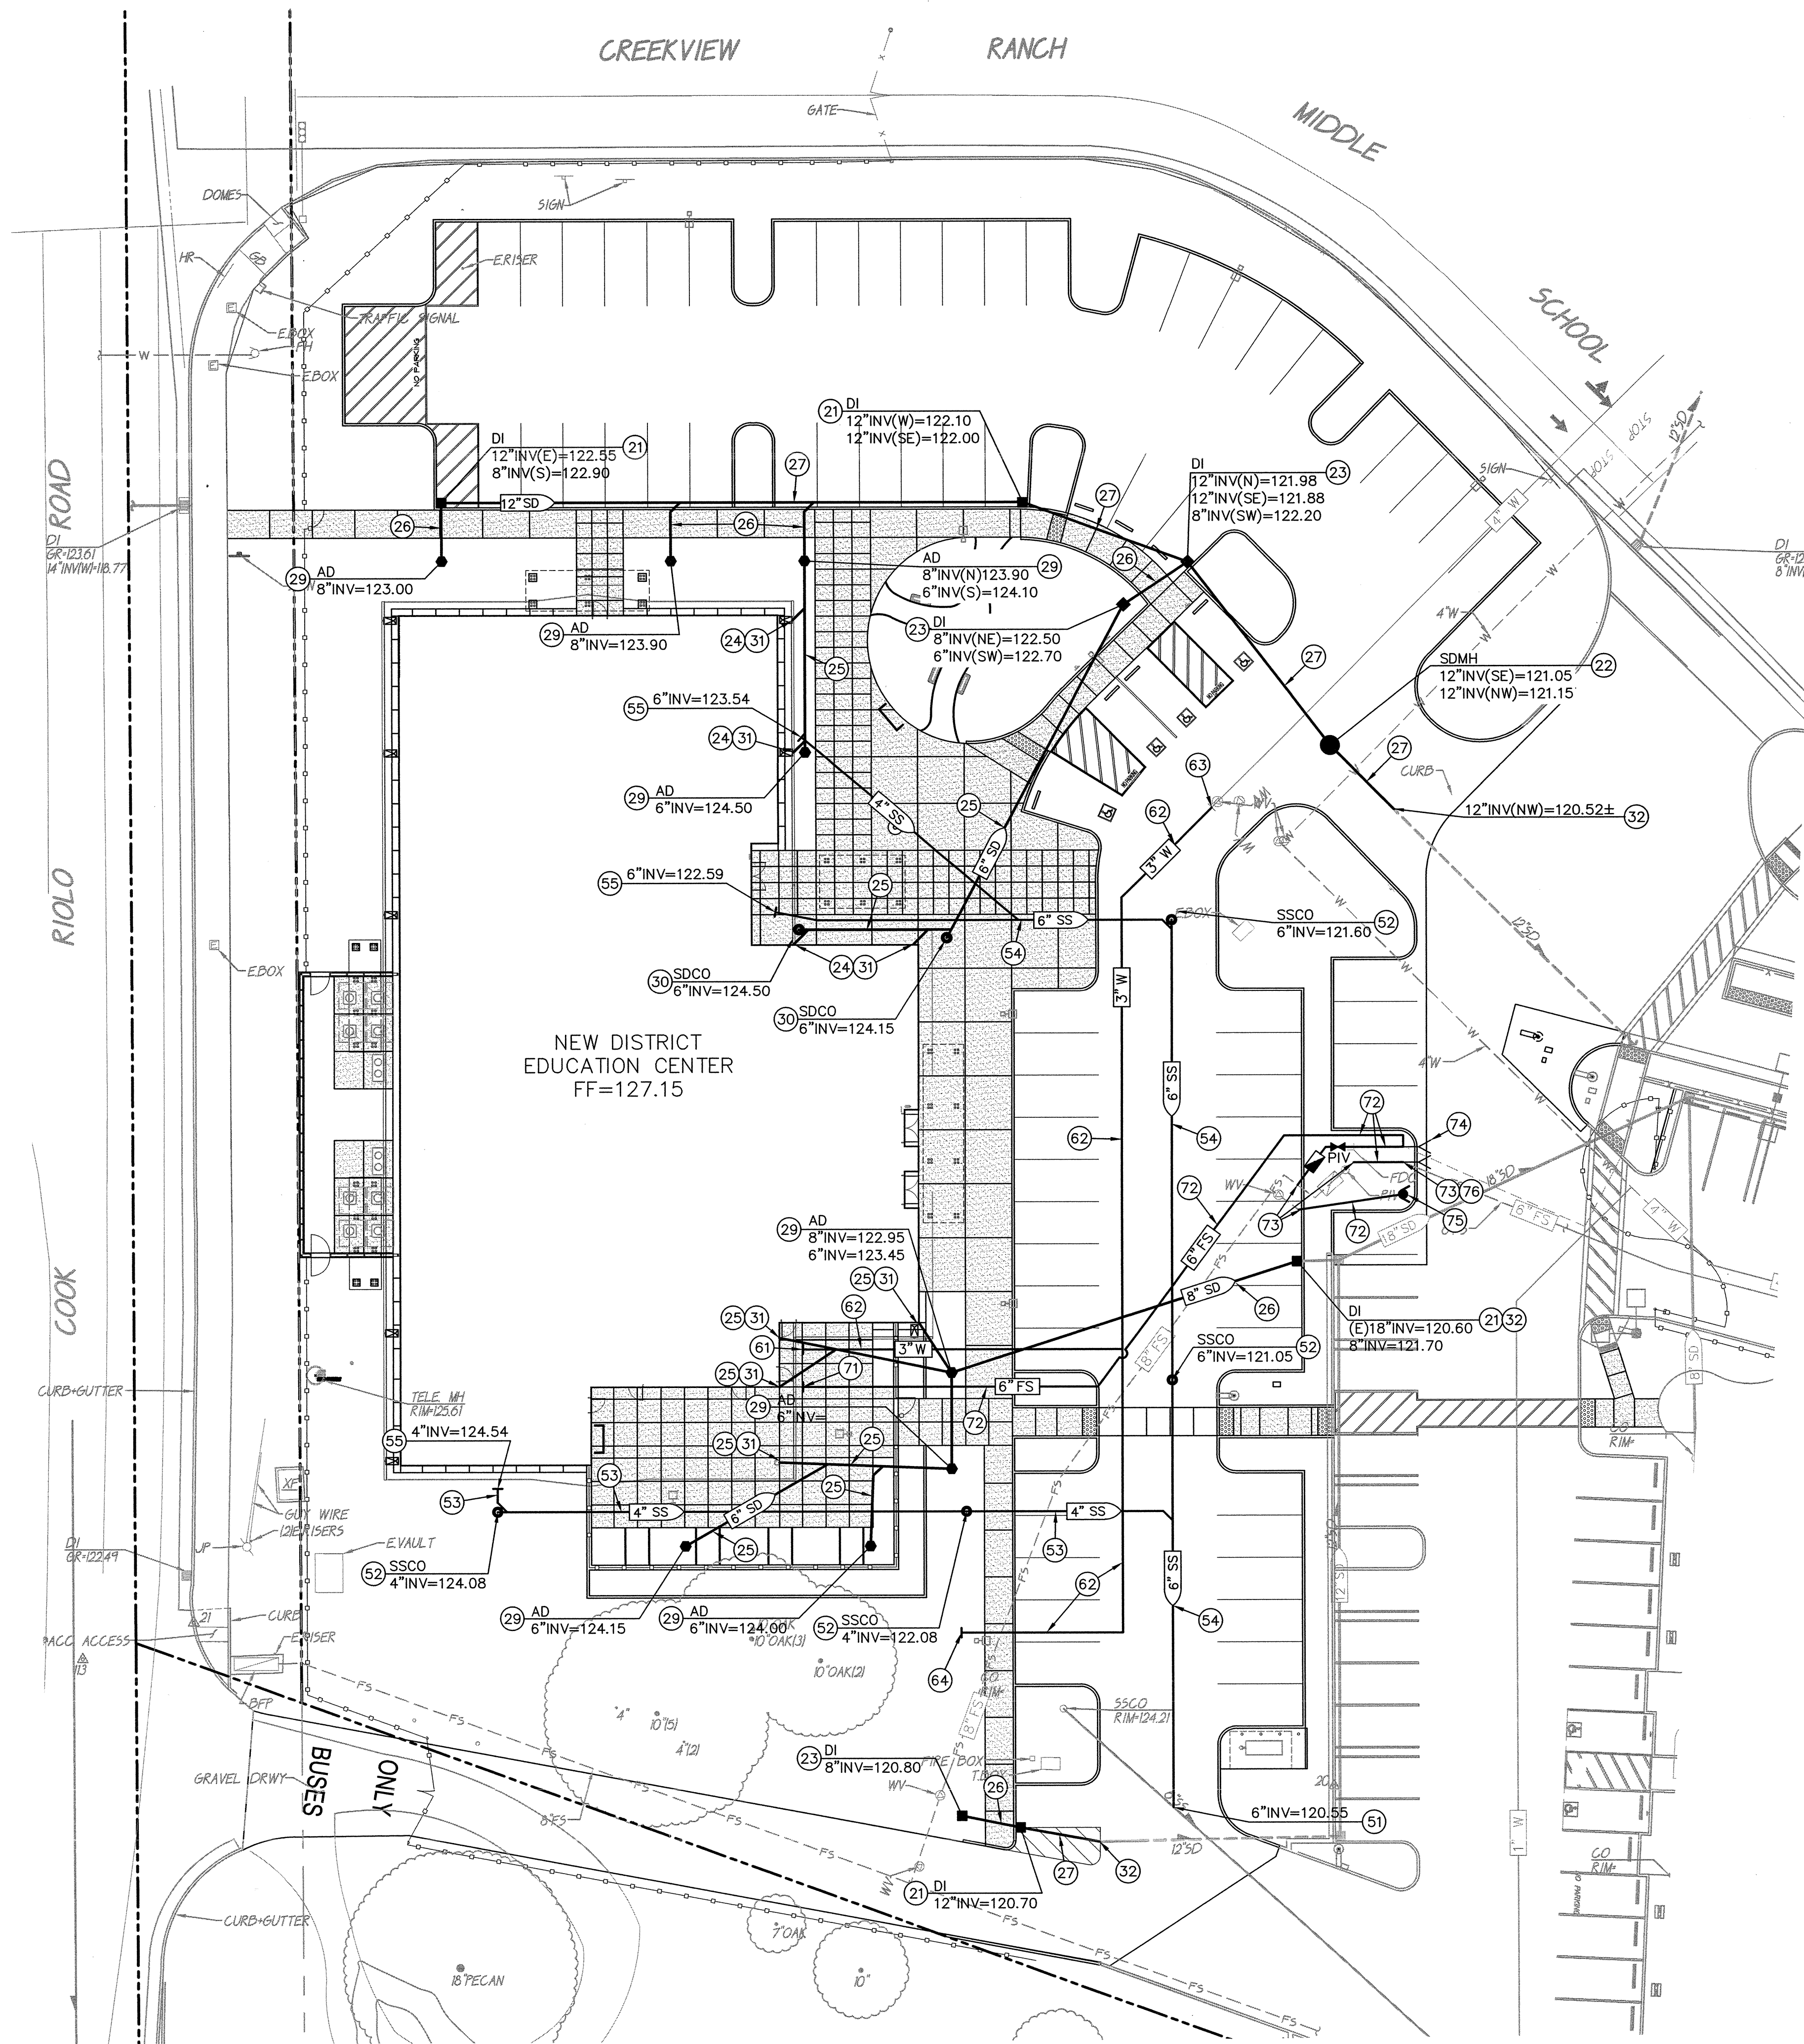

DRAINAGE NOTES

21. CONSTRUCT CURB INLET PER 6" CB.1
22. CONSTRUCT MANHOLE PER 12" CB.1
23. CONSTRUCT DROP INLET PER 13" CB.1
24. PLACE 4" STORM DRAIN PIPE PER 7" CB.1
25. PLACE 6" STORM DRAIN PIPE PER 7" CB.1
26. PLACE 8" STORM DRAIN PIPE PER 7" CB.1
27. PLACE 12" STORM DRAIN PIPE PER 7" CB.1
28. PLACE 18" STORM DRAIN PIPE PER 14" CB.1
29. CONSTRUCT AREA DRAIN PER 4" CB.1
30. CONSTRUCT STORM DRAIN CLEANOUT PER 15" CB.1
31. PROVIDE DOWNSPOUT CONNECTION. COORDINATE THE LAYOUT AND EXACT LOCATIONS WITH THE ARCHITECTURAL DRAWINGS. COORDINATE INVERT ELEVATION WITH THE SITE PLUMBING CONTRACTOR AND DETAIL PROVIDED PRIOR TO EXCAVATION.
32. CONNECT TO EXISTING STORM DRAIN. PROVIDE ALL FITTINGS NECESSARY TO MAKE CONNECTION.

SEWER NOTES

51. CONNECT TO EXISTING SANITARY SEWER LINE.
52. CONSTRUCT SANITARY SEWER CLEANOUT PER 4" CB.1
53. PLACE 4" SDR 35 SANITARY SEWER PIPE PER 7" CB.1
54. PLACE 6" SDR 35 SANITARY SEWER PIPE PER 7" CB.1
55. CONNECT TO BUILDING SANITARY SEWER SERVICE. PROVIDE ALL FITTINGS NECESSARY TO MAKE CONNECTION. COORDINATE POINT OF CONNECTION WITH PLUMBING PLANS PRIOR TO TRENCHING.

WATER NOTES

61. CONNECT TO BUILDING WATER SERVICE. PROVIDE ALL FITTINGS NECESSARY TO MAKE CONNECTION.
62. PLACE 3" WATER PIPE PER 9" CB.1
63. CONNECT TO EXISTING WATER SERVICE. PROVIDE ALL FITTINGS NECESSARY TO MAKE CONNECTION.
64. CAP AND MARK END.

FIRE PROTECTION NOTES


71. CONNECT TO BUILDING FIRE SPRINKLER SERVICE. PROVIDE ALL FITTINGS NECESSARY TO MAKE CONNECTION.
72. PLACE 6" FIRE SPRINKLER PIPE PER 9" CB.1
73. CONNECT TO EXISTING FIRE SERVICE. PROVIDE ALL FITTINGS NECESSARY TO MAKE CONNECTION.
74. PROVIDE FIRE DEPARTMENT CONNECTION WITH POST INDICATOR AND SINGLE CHECK VALVE PER 11" CB.1
75. PROVIDE FIRE HYDRANT PER 8" CB.1
76. RE-INSTALL EXISTING FIRE DEPARTMENT CONNECTION.

Dry Creek Joint Elementary School District
District Education Center

8849 Cook Riolo Road, Roseville, CA 95747
Dry Creek Joint Elementary School District


FILE NO. 31-15
IDENTIFICATION STAMP ONLY OF THE
STATE ARCHITECT OFFICE OF
REGULATION SERVICES
APPLICATION NO.
02-115456
AC TM FLS LMS SS BR
DATE 2/23/17 CLABER

DIVISION OF THE STATE ARCHITECT
revision date: by:

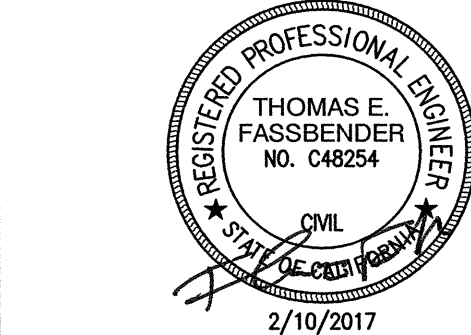

WCE
WARREN CONSULTING ENGINEERS, INC.
1117 WINDFIELD WAY, SUITE 110
EL DORADO HILLS, CA 95672
CONSULTANT

nacht&lewis
600 Q Street, Suite 100
Sacramento, CA 95811
www.nachtlewis.com
916.329.4000

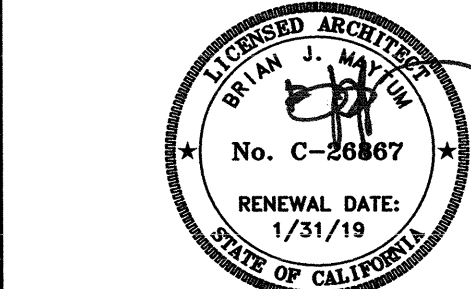

ARCHITECT

INITIAL BOX			
NO.	DWG BY	DATE	REVIEWED


REVISIONS			
NO.	DESCRIPTION	DATE	REV'D
	100% design development	7/8/16	
	75% construction documents	9/20/16	
	DSA submittal	10/18/16	
	DSA approval	02/23/17	

DATE February 23, 2017
JOB NO. Y1538.00

SHEET TITLE
Utility Plan

SHEET NO.
C3.1
SHEET OF TOTAL

ONE INCH = TWENTY FEET
ONE-SIXTEENTH INCH = ONE FOOT
ONE-EIGHTH INCH = ONE FOOT
ONE-FOURTH INCH = ONE FOOT
ONE-HALF INCH = ONE FOOT
THREE-QUARTERS INCH = ONE FOOT
ONE INCH = ONE FOOT
ONE AND ONE-HALF INCH = ONE FOOT

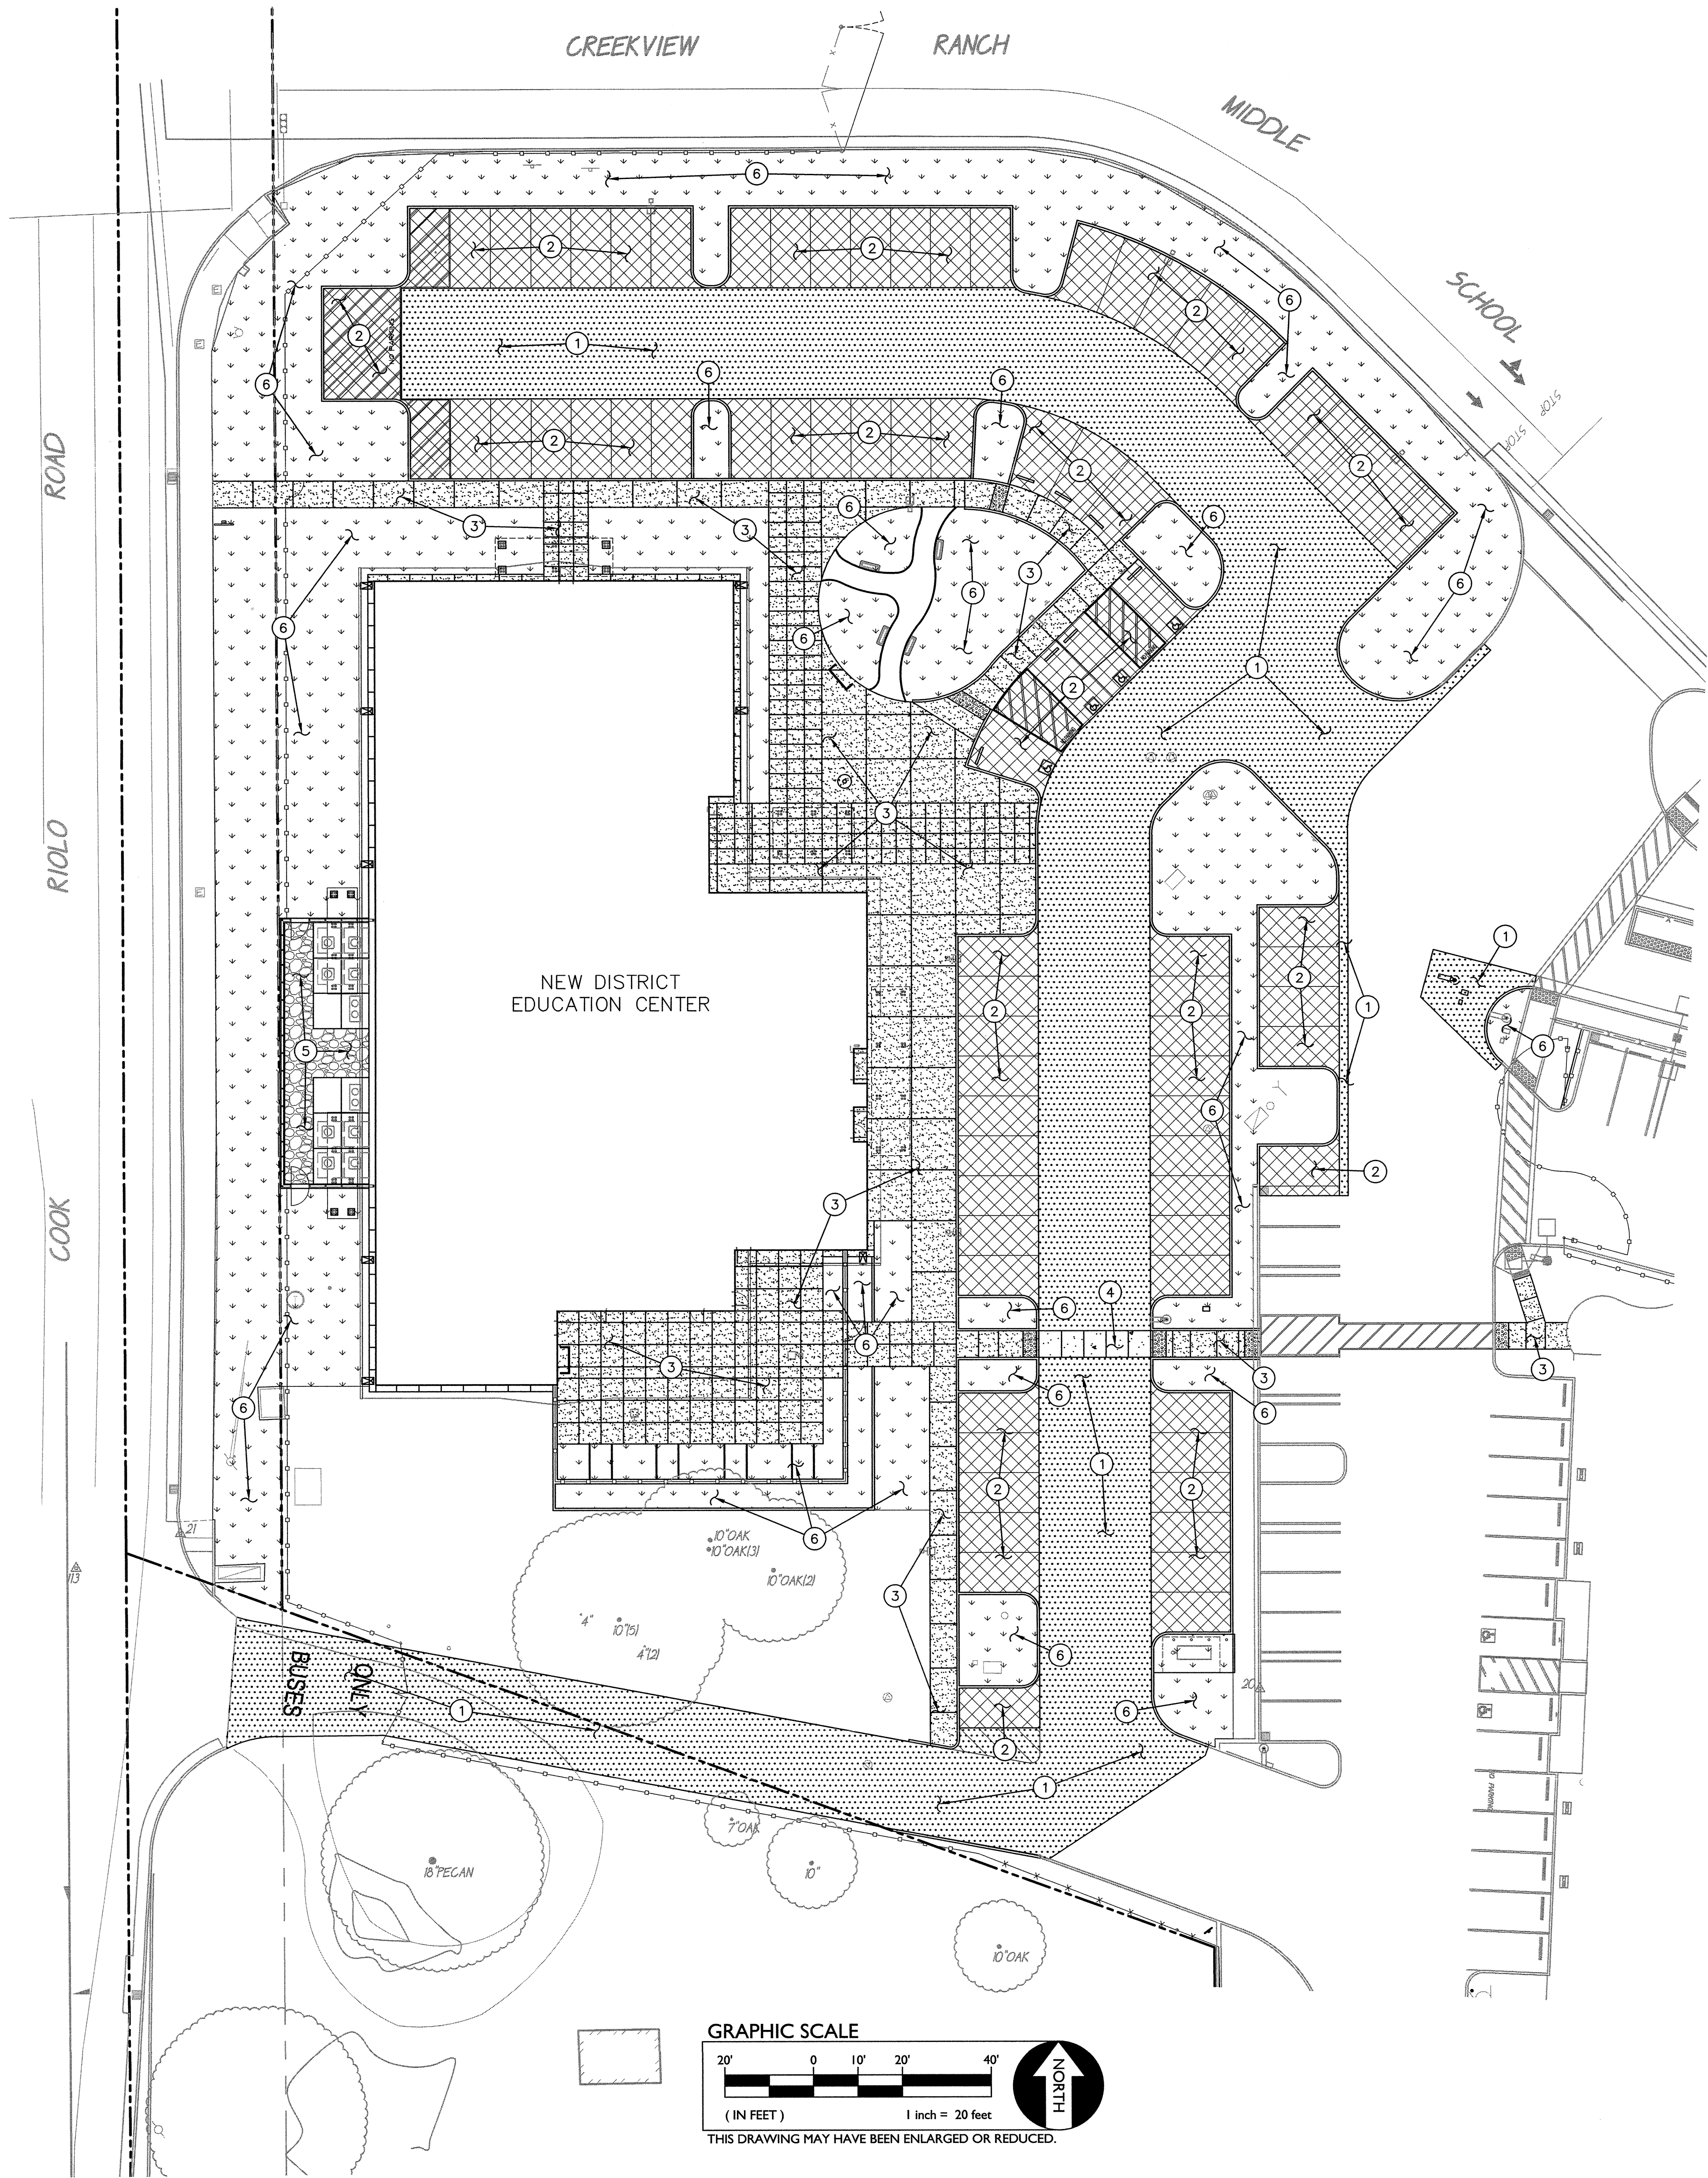

- GENERAL PAVING NOTES:
1. REFER TO ARCHITECTURAL PLANS FOR STRIPING LAYOUT.
 2. ALL NEW ASPHALT PAVING TO BE PROVIDED WITH TWO COATS SEALCOAT.
 3. PRIOR TO NEW SEALCOAT ON EXISTING ASPHALT SURFACES, FILL ALL CRACKS 1/4" INCHES OR WIDER WITH AN APPROVED CRACK FILLER.
 4. ALL EXPOSED ASPHALT EDGES SHALL HAVE HEADER BOARDS WHETHER SHOWN OR NOT.
 5. IN NEW ASPHALT AREAS, ALL EXISTING UTILITY BOXES WHETHER SHOWN OR NOT SHALL BE RAISED TO FINISH GRADE.
 6. REFER TO ARCHITECTURAL PLANS FOR CONCRETE COLORING AND JOINT PATTERNS.

- PAVING LEGEND
- 1 TYPE 1 PAVING
3" AC OVER 9" AB ON COMPACTED SUBGRADE.
 - 2 TYPE 2 PAVING
PLACE 2.5" AC OVER 5" AB ON COMPACTED SUBGRADE.
 - 3 TYPE 3 PAVING
PLACE 4" PCC WITH WELDED WIRE FABRIC OVER 4" AB ON COMPACTED SUBGRADE.
 - 4 TYPE 4 PAVING
PLACE 7" PCC WITH #4 REBAR AT 24" O.C. EACH WAY OVER 6" AB ON COMPACTED SUBGRADE.
 - 5 TYPE 5 CRUSHED ROCK
PLACE 4" OF 3/4" CRUSHED ROCK OVER COMPACTED SUBGRADE.
 - 6 TYPE 6 TOPSOIL
PLACE 12" TOPSOIL PER LANDSCAPE SPECIFICATIONS.

Dry Creek Joint Elementary School District
District Education Center

8849 Cook Riolo Road, Roseville, CA 95747
Dry Creek Joint Elementary School District

FILE NO. 31-15
IDENTIFICATION STAMP DIV. OF THE
STATE ARCHITECT OFFICE OF
REGULATION SERVICES
APPLICATION NO.
02-115456
AC TM FLS SS BR
DATE 2/23/17

DIVISION OF THE STATE ARCHITECT
revision date: by:

REGISTERED PROFESSIONAL ENGINEER
THOMAS E. FASSBENDER
No. 048254
CIVIL
2/10/2017
WCE
WARREN CONSULTING ENGINEERS, INC.
1117 WINDFIELD WAY, SUITE 110
EL DORADO HILLS, CA 95672
CONSULTANT

nacht&lewis
600 Q Street, Suite 100
Sacramento, CA 95811
www.nachtlewis.com
916.329.4000

REGISTERED ARCHITECT
No. C-24987
RENEWAL DATE:
1/31/19
STATE OF CALIFORNIA

ARCHITECT

INITIAL BOX			
NO.	DWG BY	DATE	REVIEWED


REVISIONS

NO.	DESCRIPTION	DATE	REV'D
	100% design development	7/8/16	
	75% construction documents	9/20/16	
	DSA submittal	10/18/16	
	DSA approval	02/23/17	

DATE February 23, 2017
JOB NO. Y1538.00
SHEET TITLE
Paving Plan

SHEET NO.
C4.1
SHEET ___ OF ___ TOTAL

ONE INCH = TWENTY FEET
ONE-SIXTEENTH INCH = ONE FOOT
ONE-EIGHTH INCH = ONE FOOT
ONE-FOURTH INCH = ONE FOOT
ONE-HALF INCH = ONE FOOT
THREE-QUARTERS INCH = ONE FOOT
ONE INCH = ONE FOOT
ONE AND ONE-HALF INCH = ONE FOOT

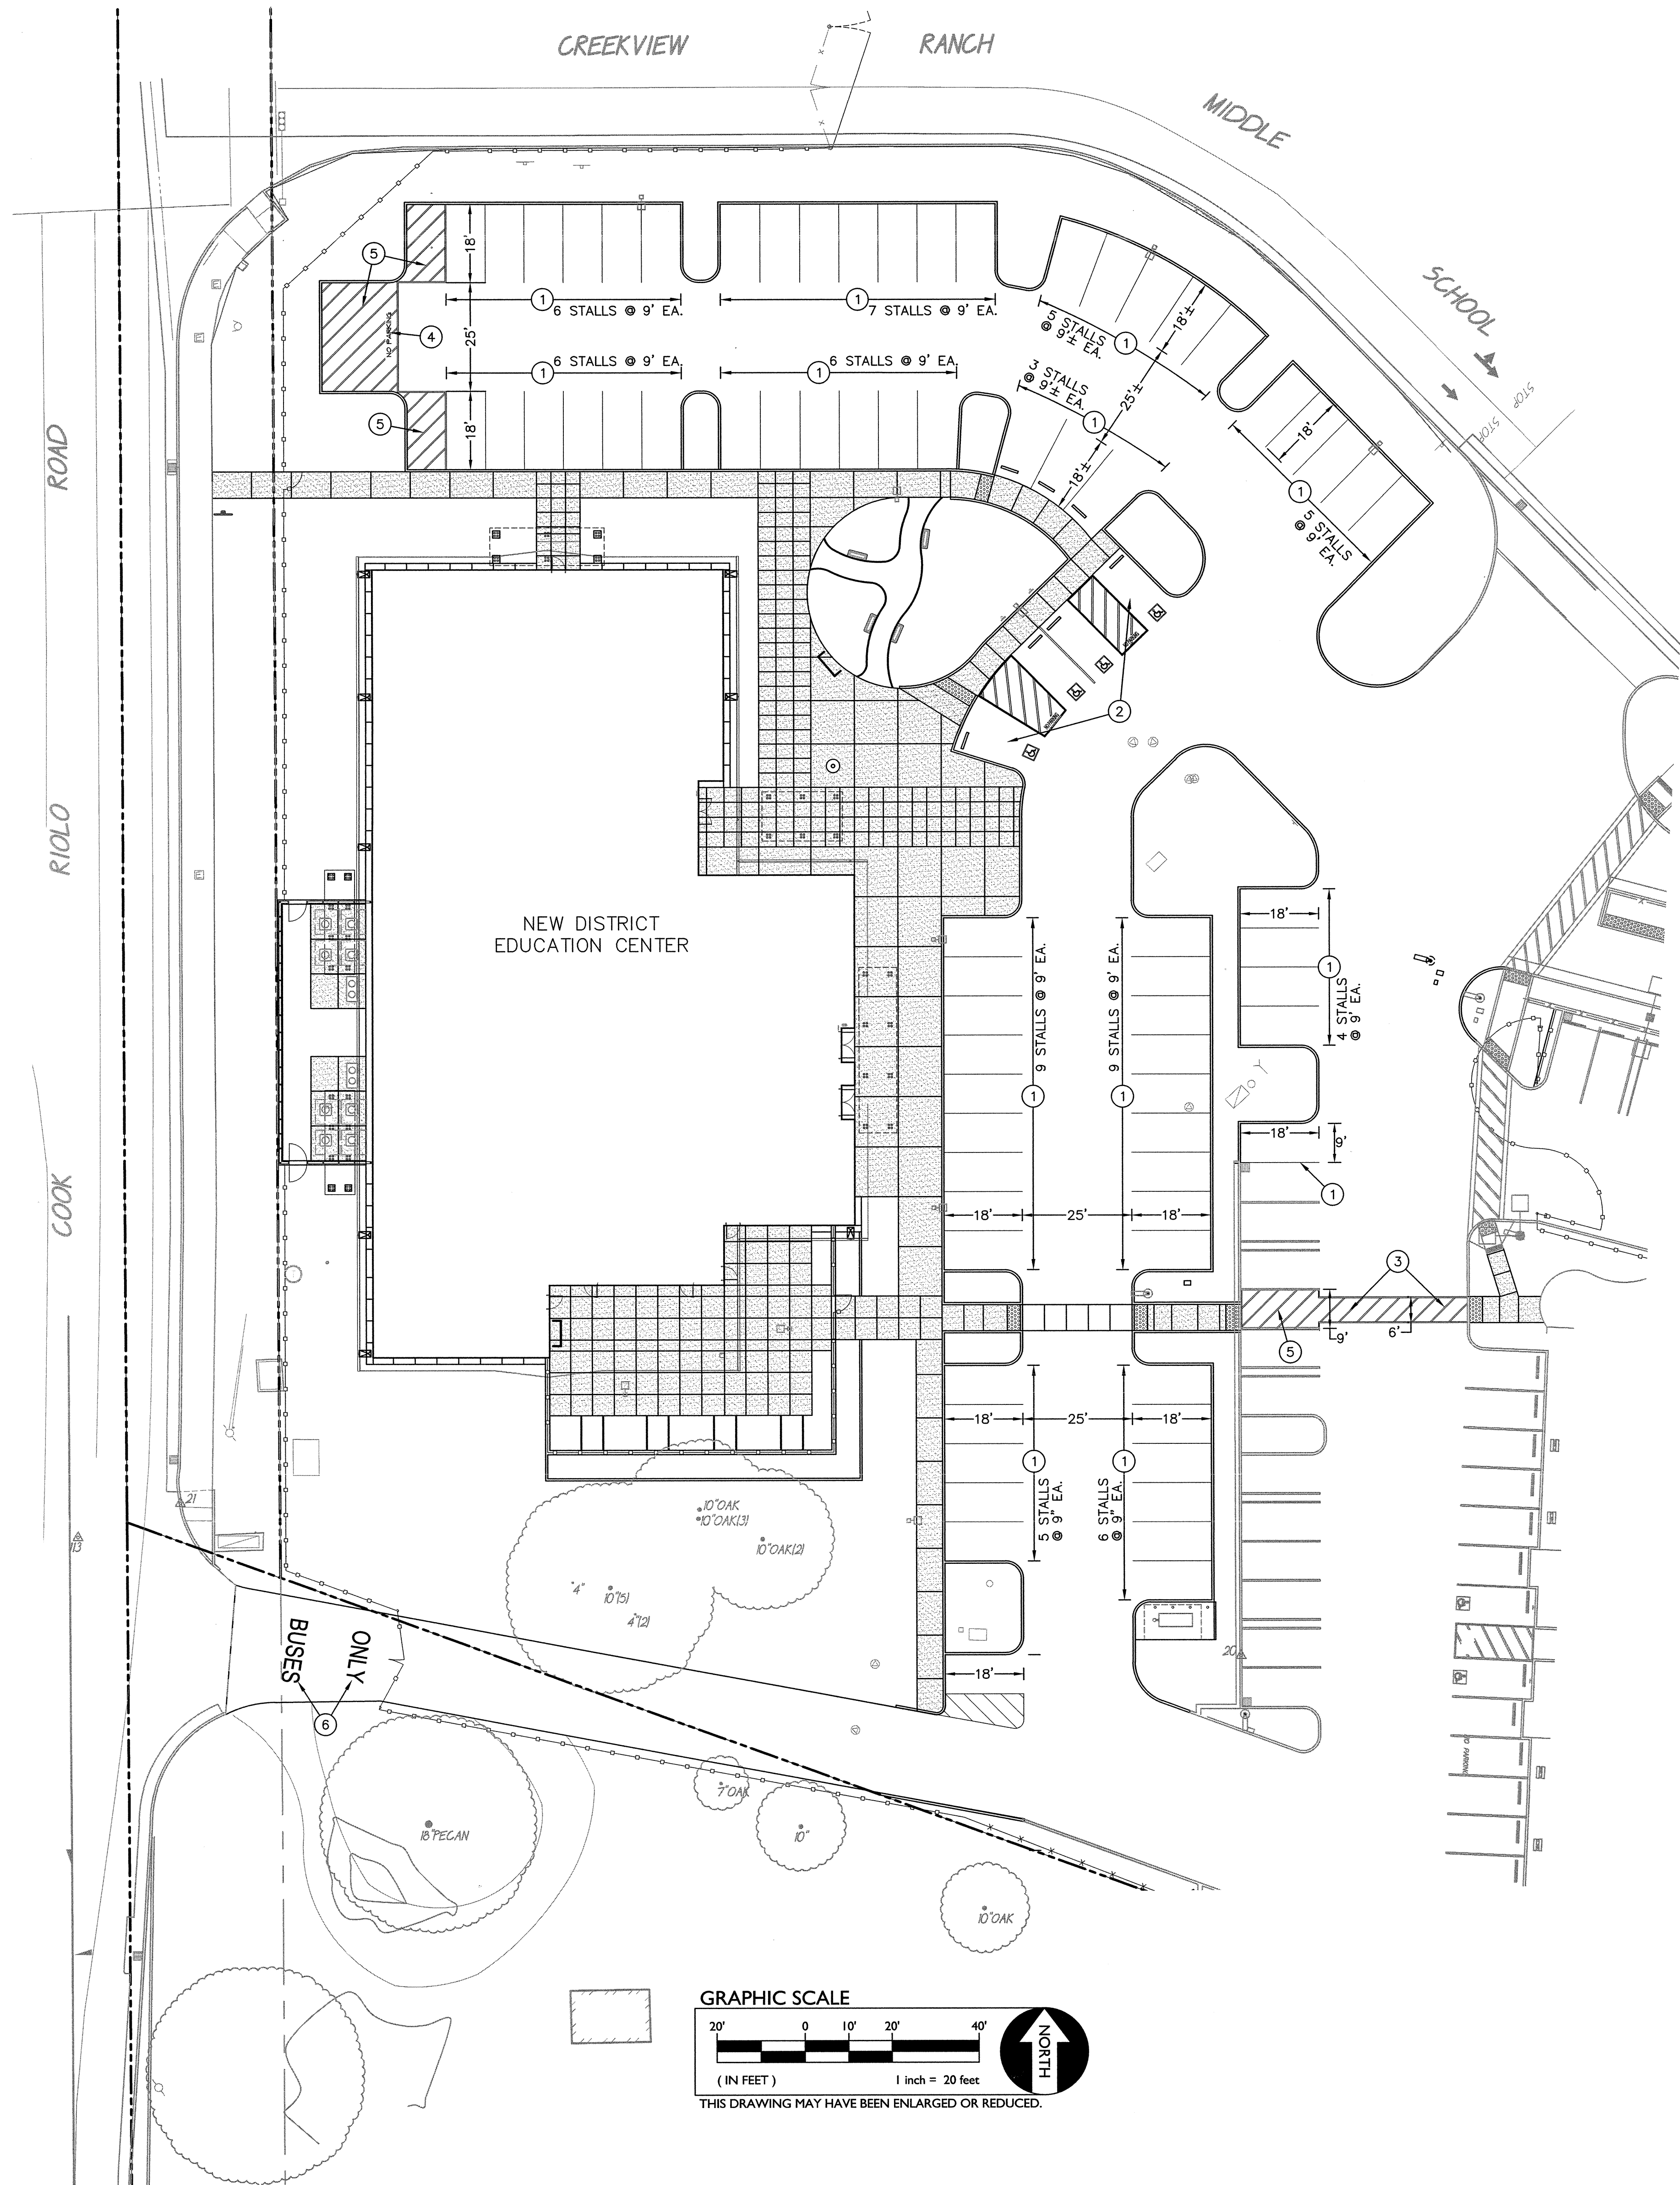

STRIPING SIGNAGE LEGEND


1. PROVIDE 4" WIDE WHITE PARKING STALL STRIPING.
2. PROVIDE ACCESSIBLE PARKING STRIPING PER ARCHITECTURAL PLANS.
3. PROVIDE CROSSWALK DIAGONAL STRIPING, YELLOW AT 3' O.C.
4. PAINT WHITE LETTERS 12" HIGH.
5. PROVIDE WHITE "NO PARKING" STRIPING, DIAGONAL, 3' O.C.
6. PROVIDE 4' TALL WHITE LETERING " BUSES ONLY".

Dry Creek Joint Elementary School District
District Education Center

8849 Cook Riolo Road, Roseville, CA 95747
Dry Creek Joint Elementary School District


FILE NO. 31-15
IDENTIFICATION STAMP DIV. OF THE
STATE ARCHITECT OFFICE OF
REGULATION SERVICES
APPLICATION NO.
02-115456
AC TM FLS TM SS PR
DATE 2/23/17 UP

DIVISION OF THE STATE ARCHITECT
revision date: by:

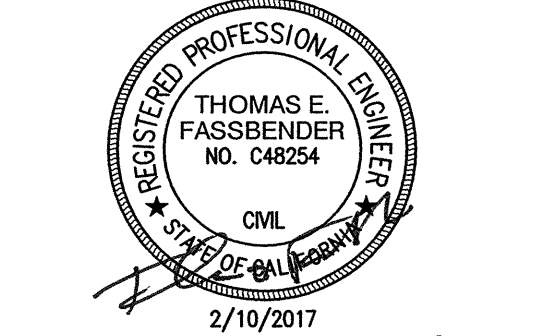

WCE
WARREN CONSULTING ENGINEERS, INC.
1117 WINDFIELD WAY, SUITE 110
EL DORADO HILLS, CA 95672
CONSULTANT

nacht&lewis
600 Q Street, Suite 100
Sacramento, CA 95811
www.nachtlewis.com
916.329.4000

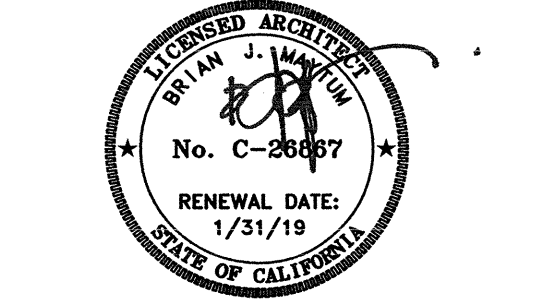

ARCHITECT

INITIAL BOX			
NO.	DWG BY	DATE	REVIEWED

REVISIONS			
NO.	DESCRIPTION	DATE	REV
	100% design development	7/8/16	
	75% construction documents	9/20/16	
	DSA submittal	10/18/16	
	DSA approval	02/23/17	

DATE February 23, 2017

JOB NO. Y1538.00

SHEET TITLE

Striping Plan

SHEET NO.

C4.2

SHEET OF TOTAL