

SECTION SHEET NOTES:

- 1 Roof SP per plan

2 Roof frmg per plan

3 GL beam per plan

4 W beam per plan

5 Floor frmg w/SP per plan

6 Wall frmg per plan

7 Conc slab & reinf per plan

8 Non-struct wall per plan

9 Frame ext opng per 2/S0.3

10 Frame int opng per 1/S0.3
- 11 Soffit frmg per plan

12 NOT USED

13 HSS col per plan





14 Cupola frmg per plan

15 California frmg

16 Ceiling per Arch dwgs

17 Operable partition per Arch dwgs


18 Storefront per Arch dwgs

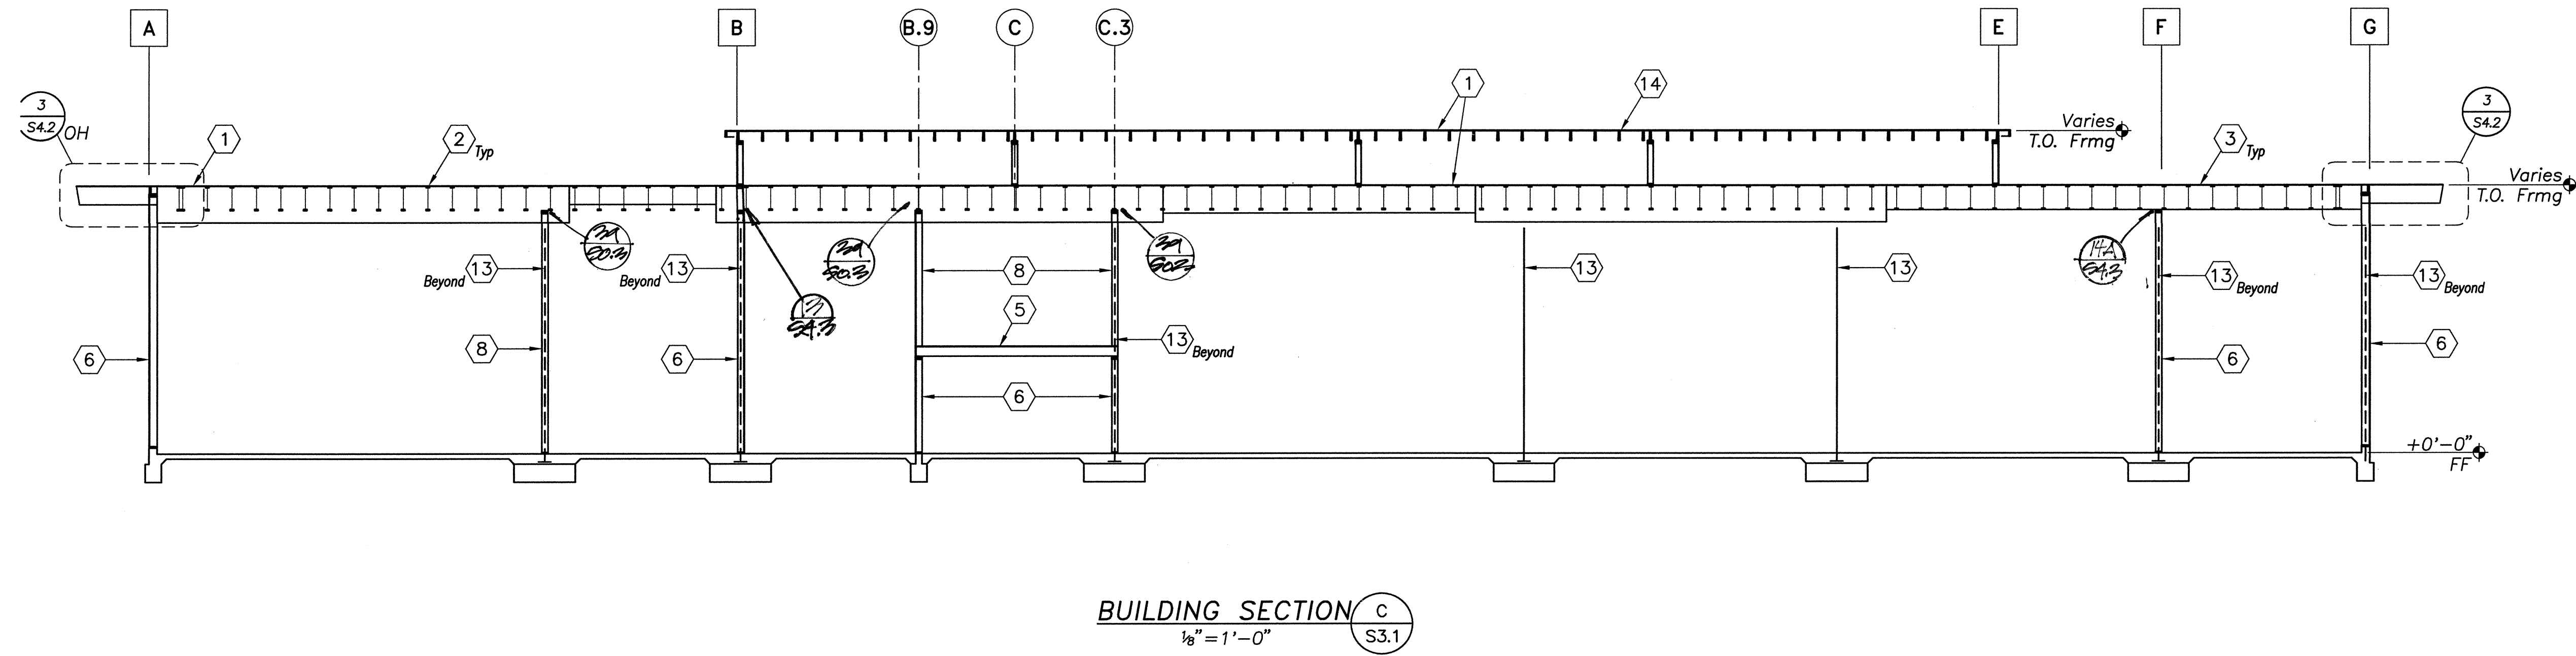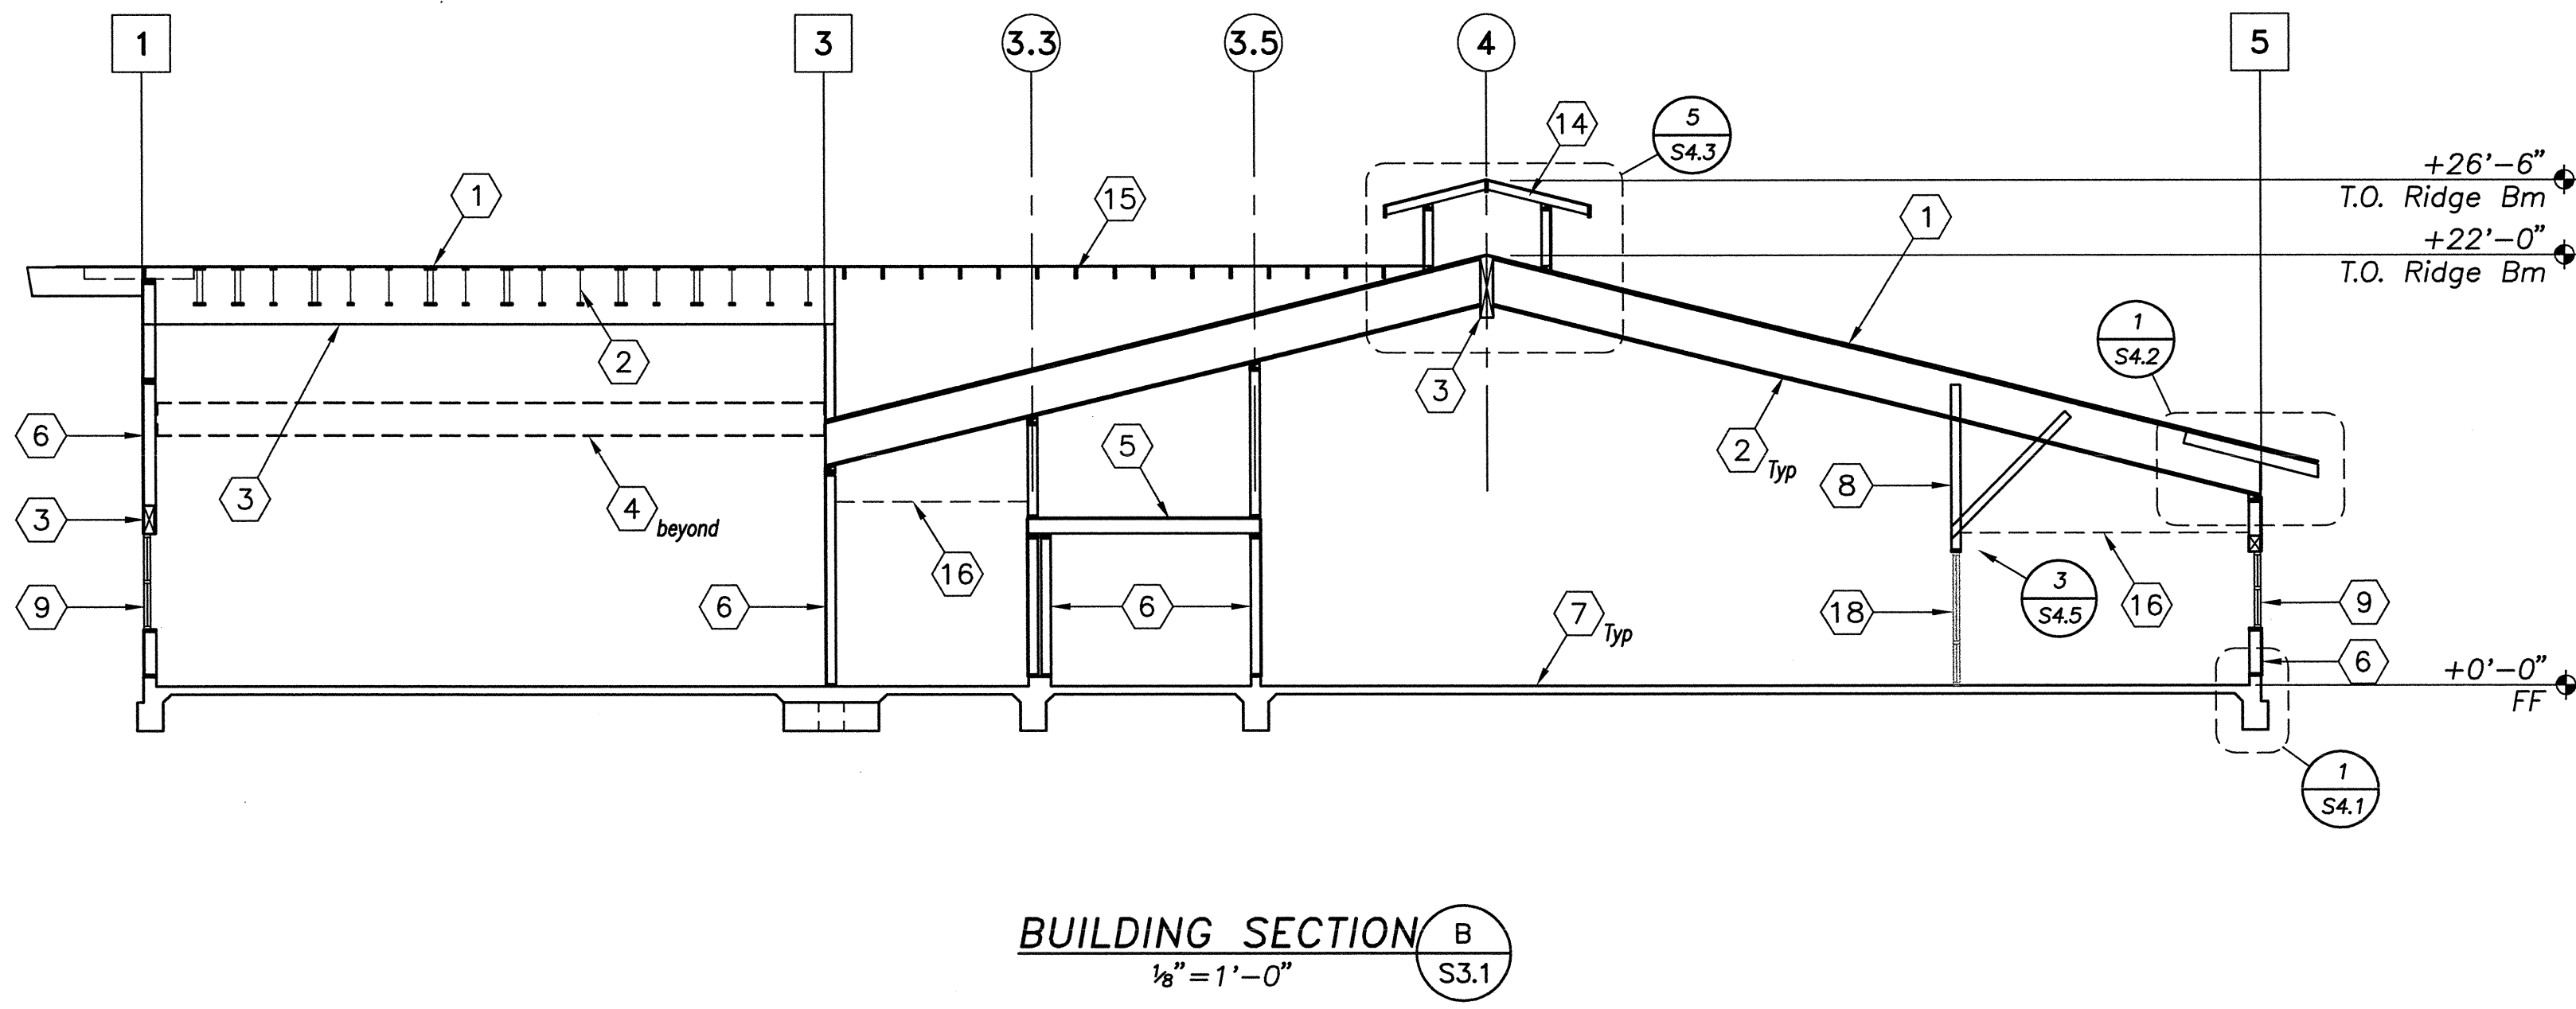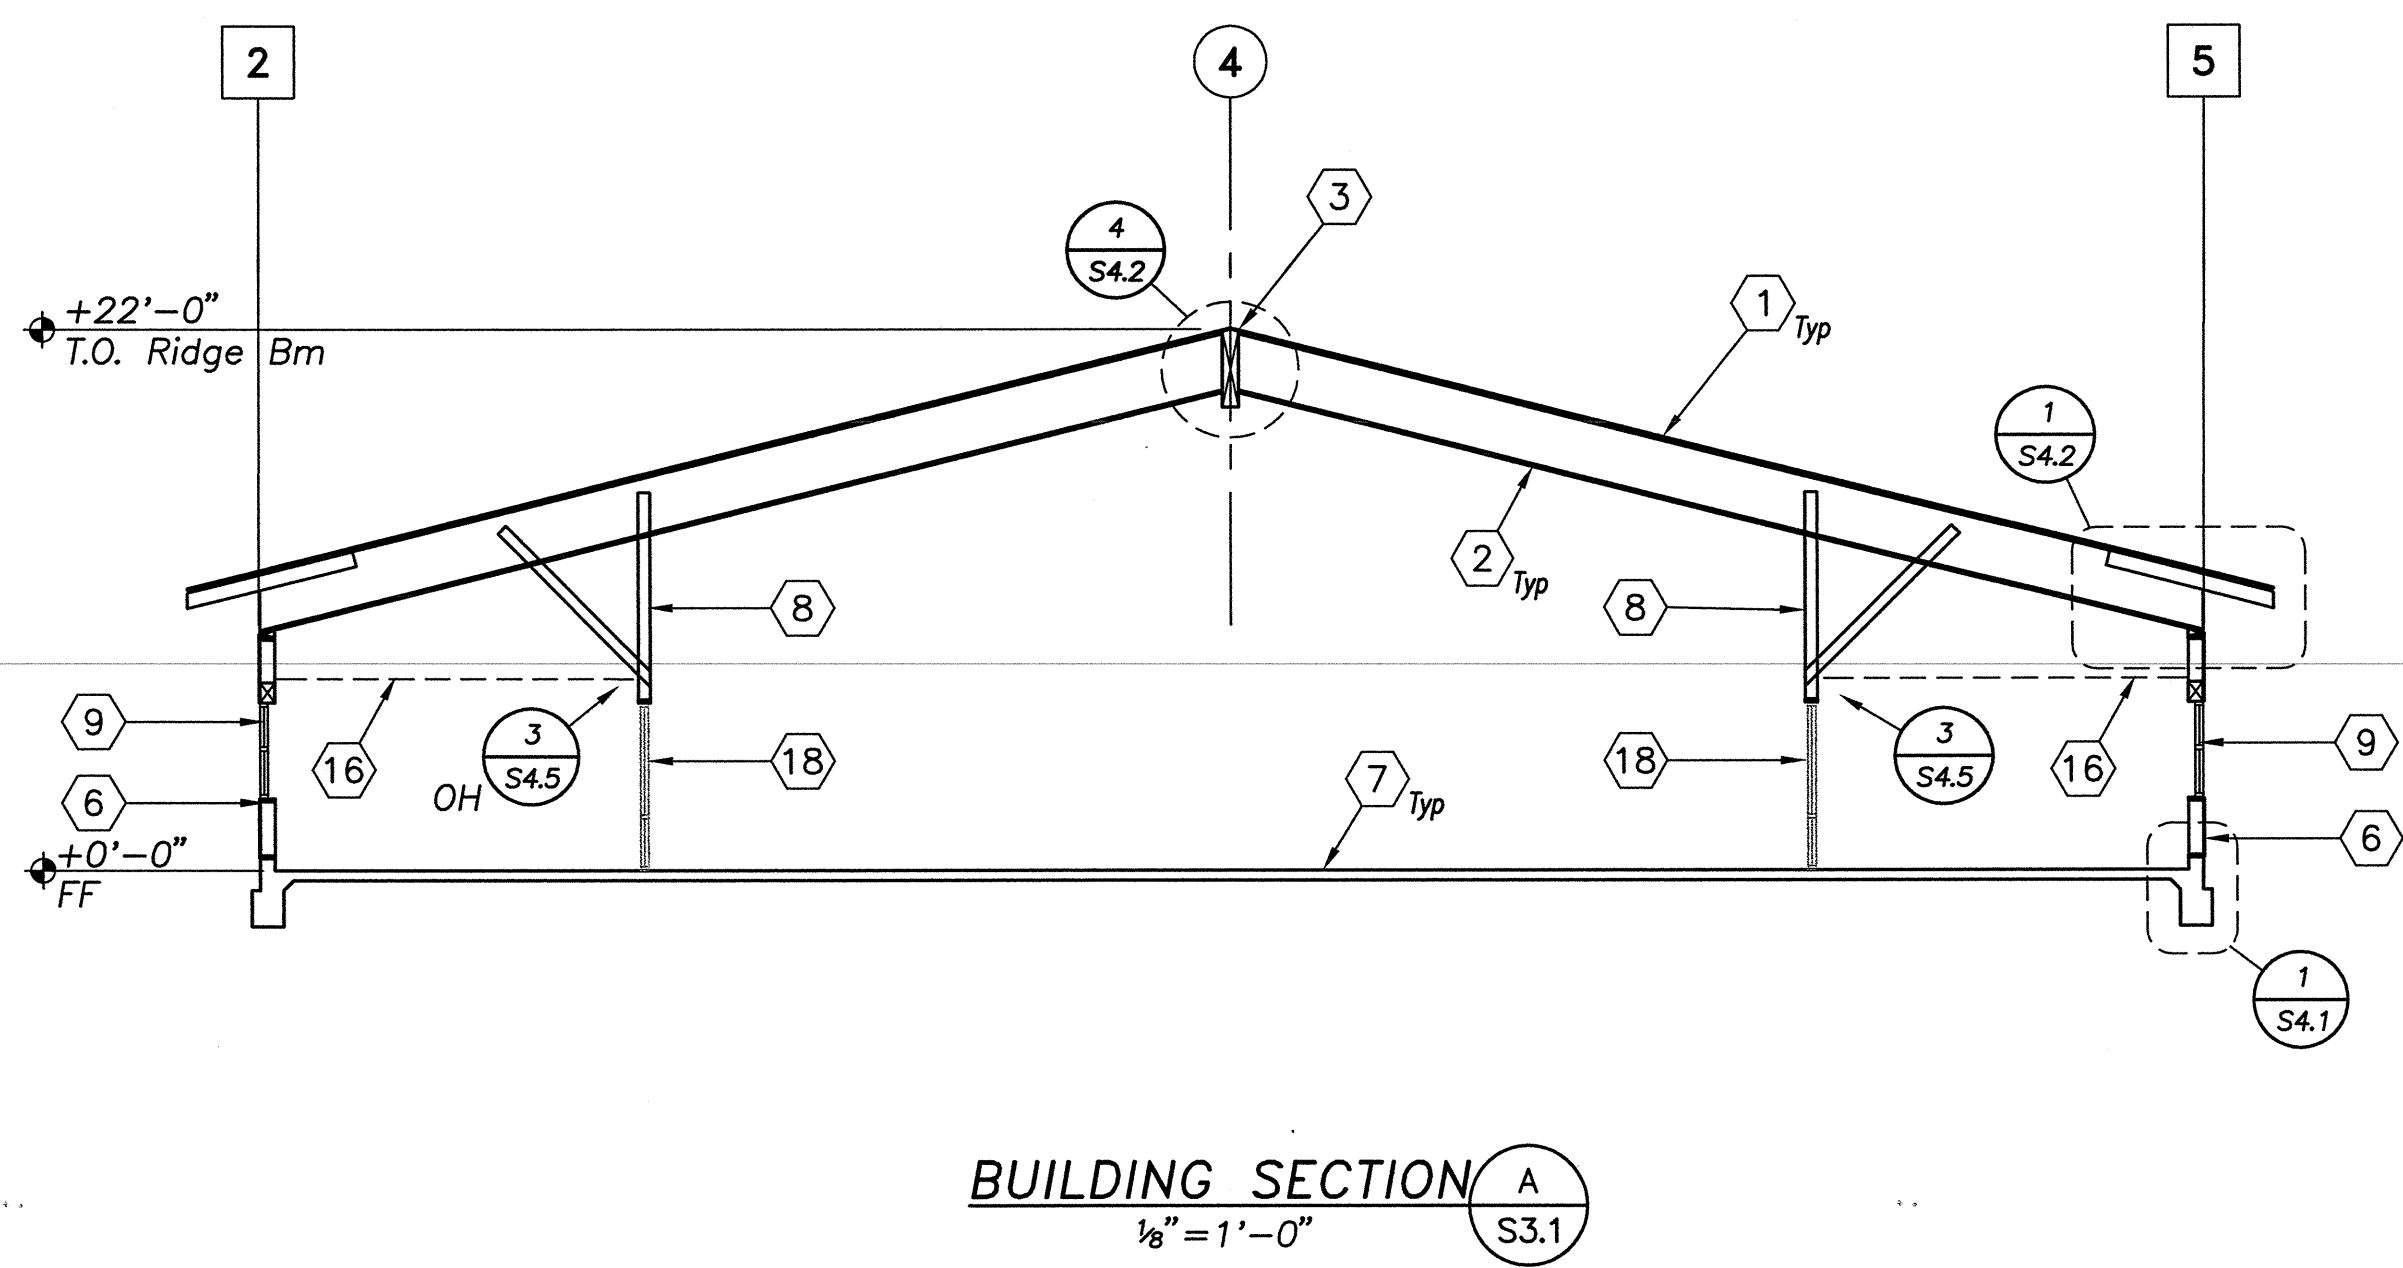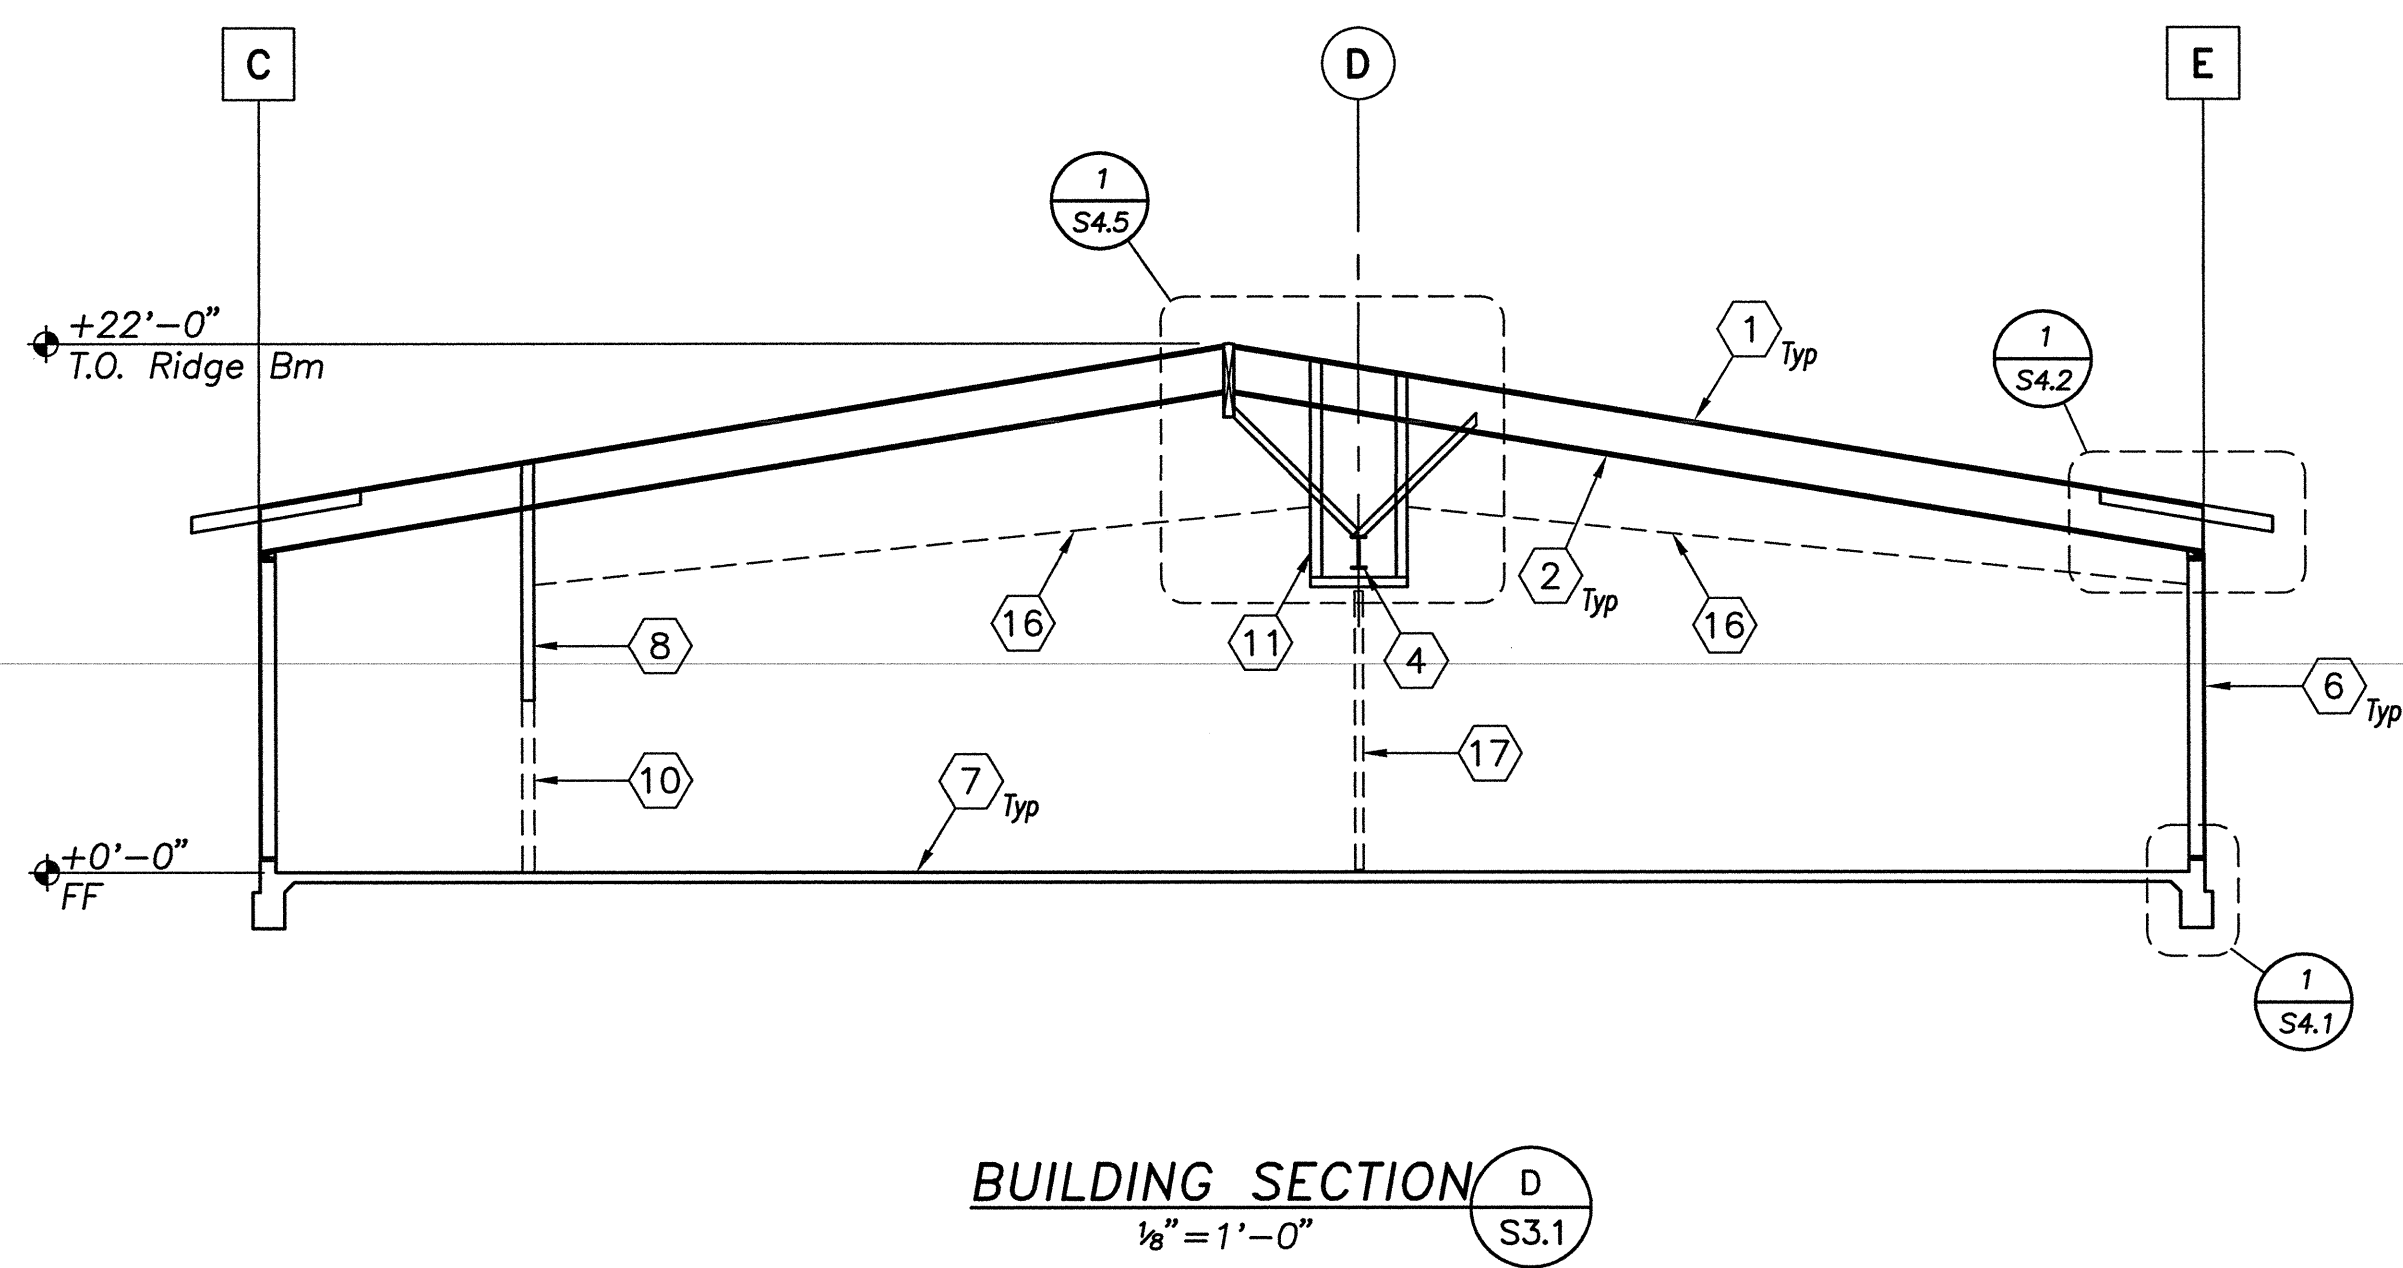

FILE NO. 31-15
IDENTIFICATION STAMP DIV. OF THE
STATE ARCHITECT OFFICE OF
REGULATION SERVICES
APPLICATION NO.
02-115456
AC _____ FLS _____ SS *BR*
DATE *2/23/17* *CAZ*


DIVISION OF THE STATE ARCHITECT
revision date: _____ by: _____

www.barrish.com
bp
barrish pelham
Consulting Engineers
Sacramento Walnut Creek Tahoe Reno

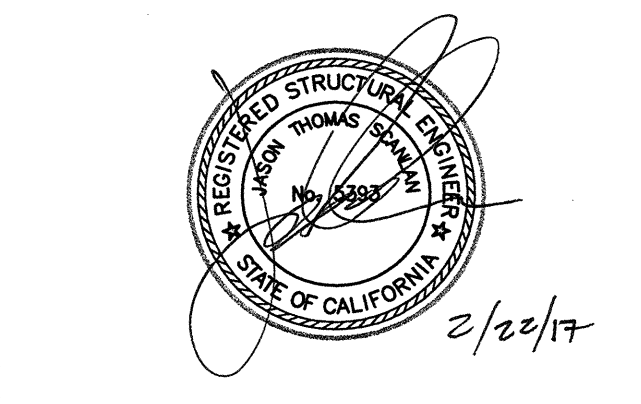

CONSULTANT

nacht&lewis
600 Q Street, Suite 100
Sacramento, CA 95811
www.nachtandlewis.com
916.329.4000

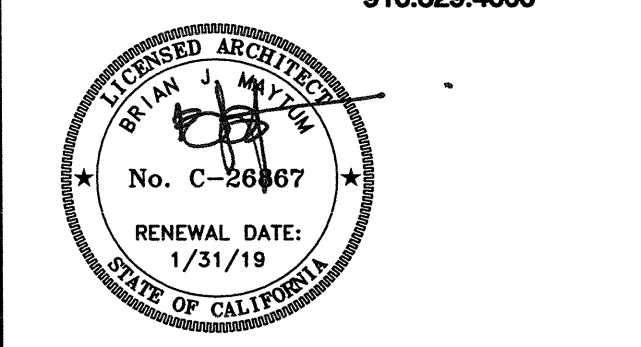

ARCHITECT

INITIAL BOX			
NO.	DWG BY	DATE	REVIEWED


REVISIONS			
NO.	DESCRIPTION	DATE	REV'D
	100% design development	7/8/16	
	75% construction documents	9/20/16	
	DSA Submittal	12/31/16	
	DSA Backcheck	02/23/17	

DATE February 23, 2017
JOB NO. Y1538.00
SHEET TITLE


Building Sections

SHEET NO.
S3.1


ONE AND ONE-HALF INCH = ONE FOOT
ONE INCH = ONE FOOT
THREE-QUARTERS INCH = ONE FOOT
ONE-HALF INCH = ONE FOOT
ONE-QUARTER INCH = ONE FOOT
ONE-EIGHTH INCH = ONE FOOT
ONE-SIXTEENTH INCH = ONE FOOT
ONE INCH = TWENTY FEET

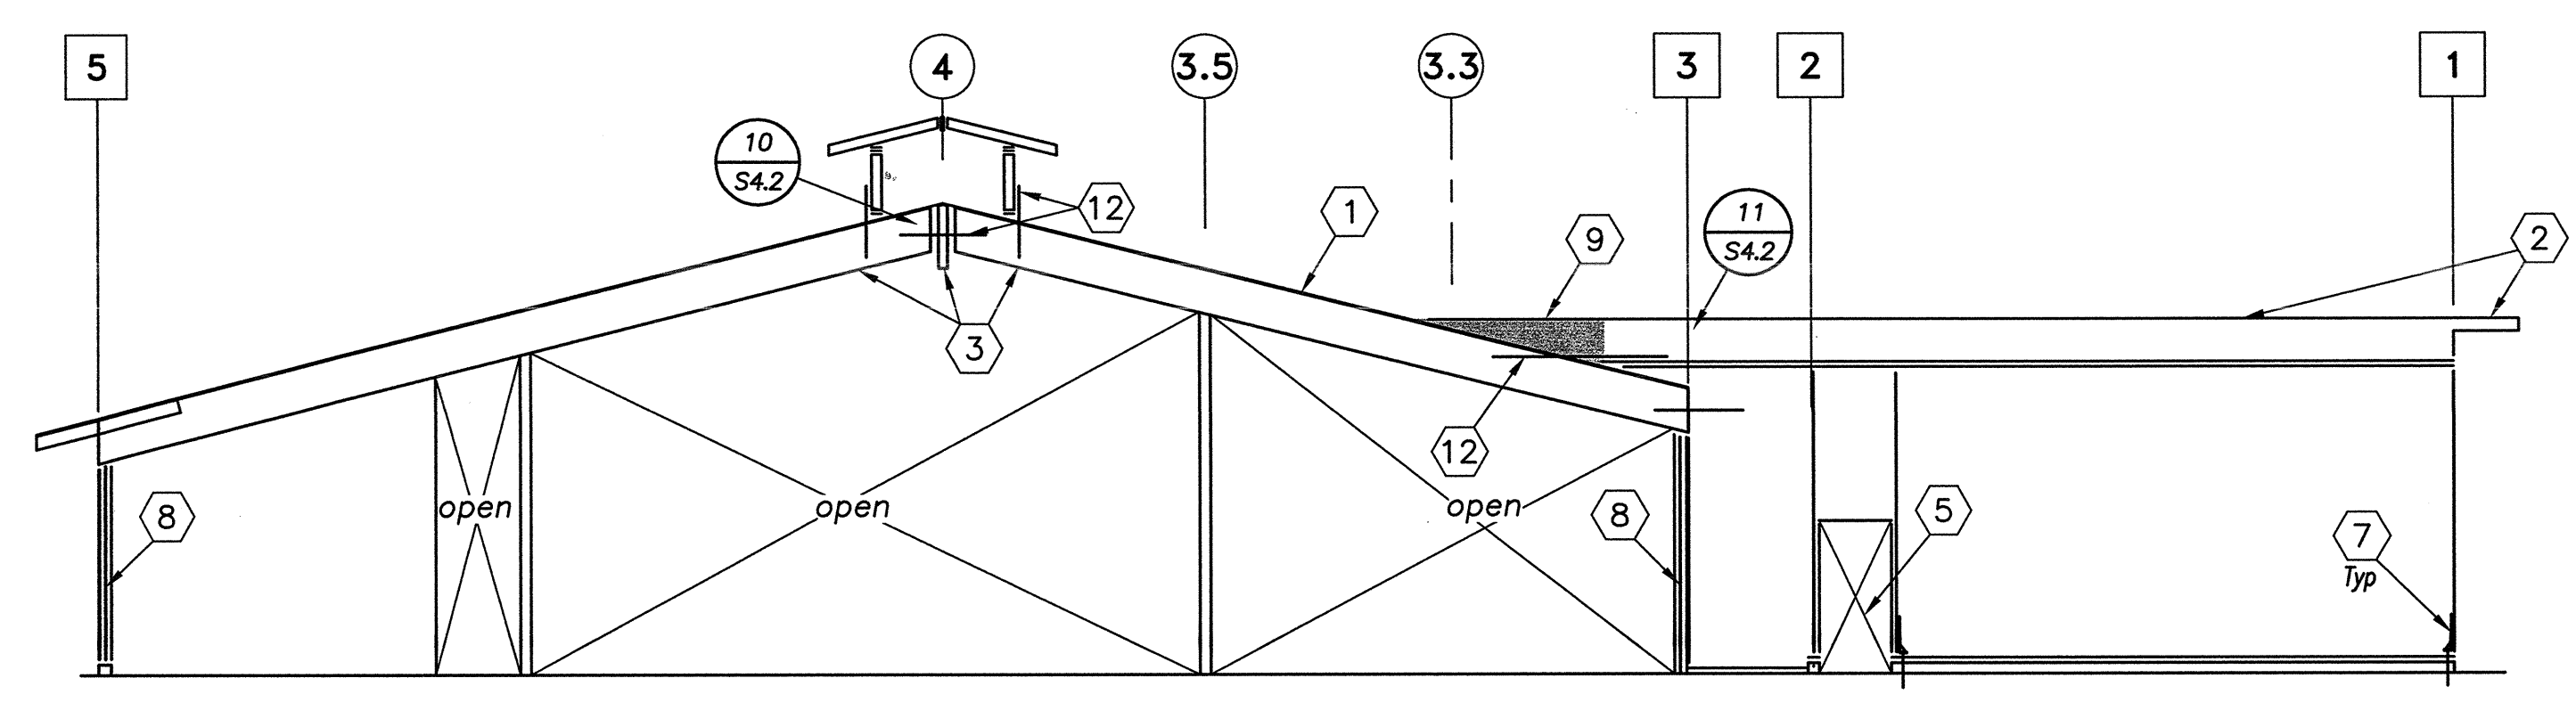


WALL FRAMING ELEVATION - LINE E $\frac{1}{8}'' = 1'-0''$

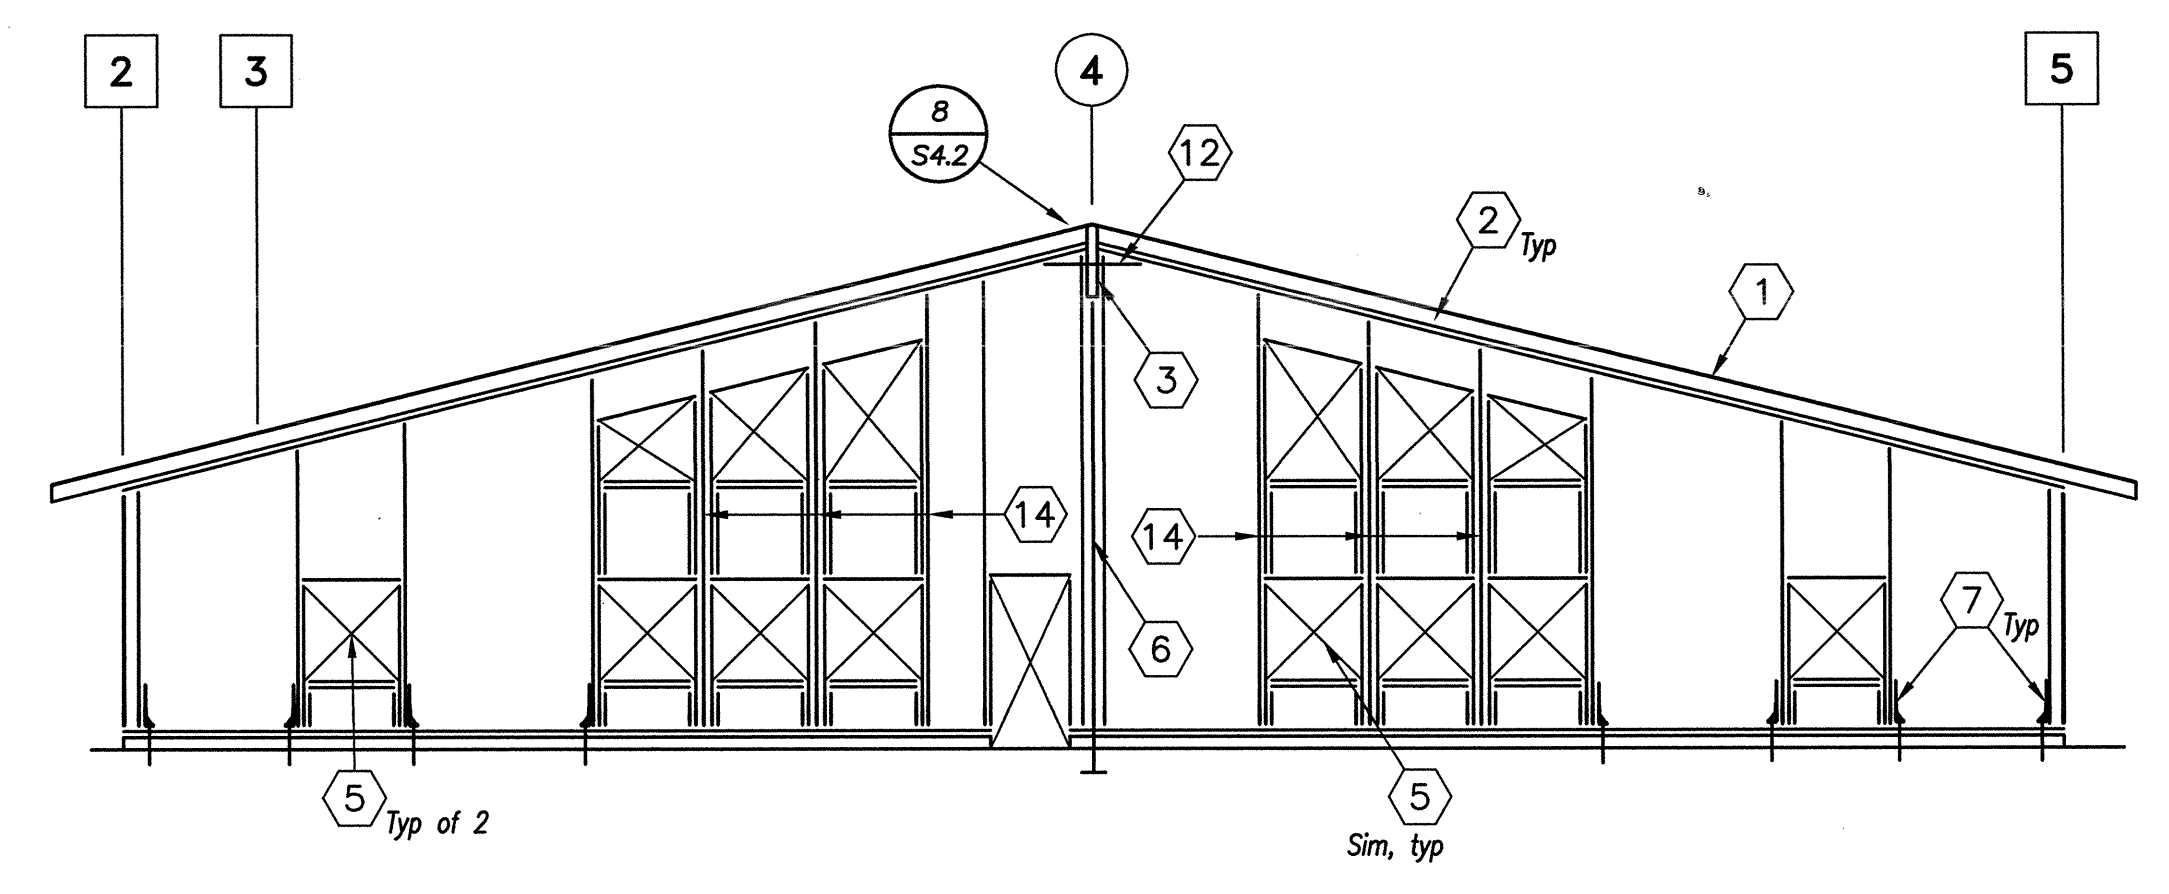


WALL FRAMING ELEVATION - LINE A $\frac{1}{8}'' = 1'-0''$

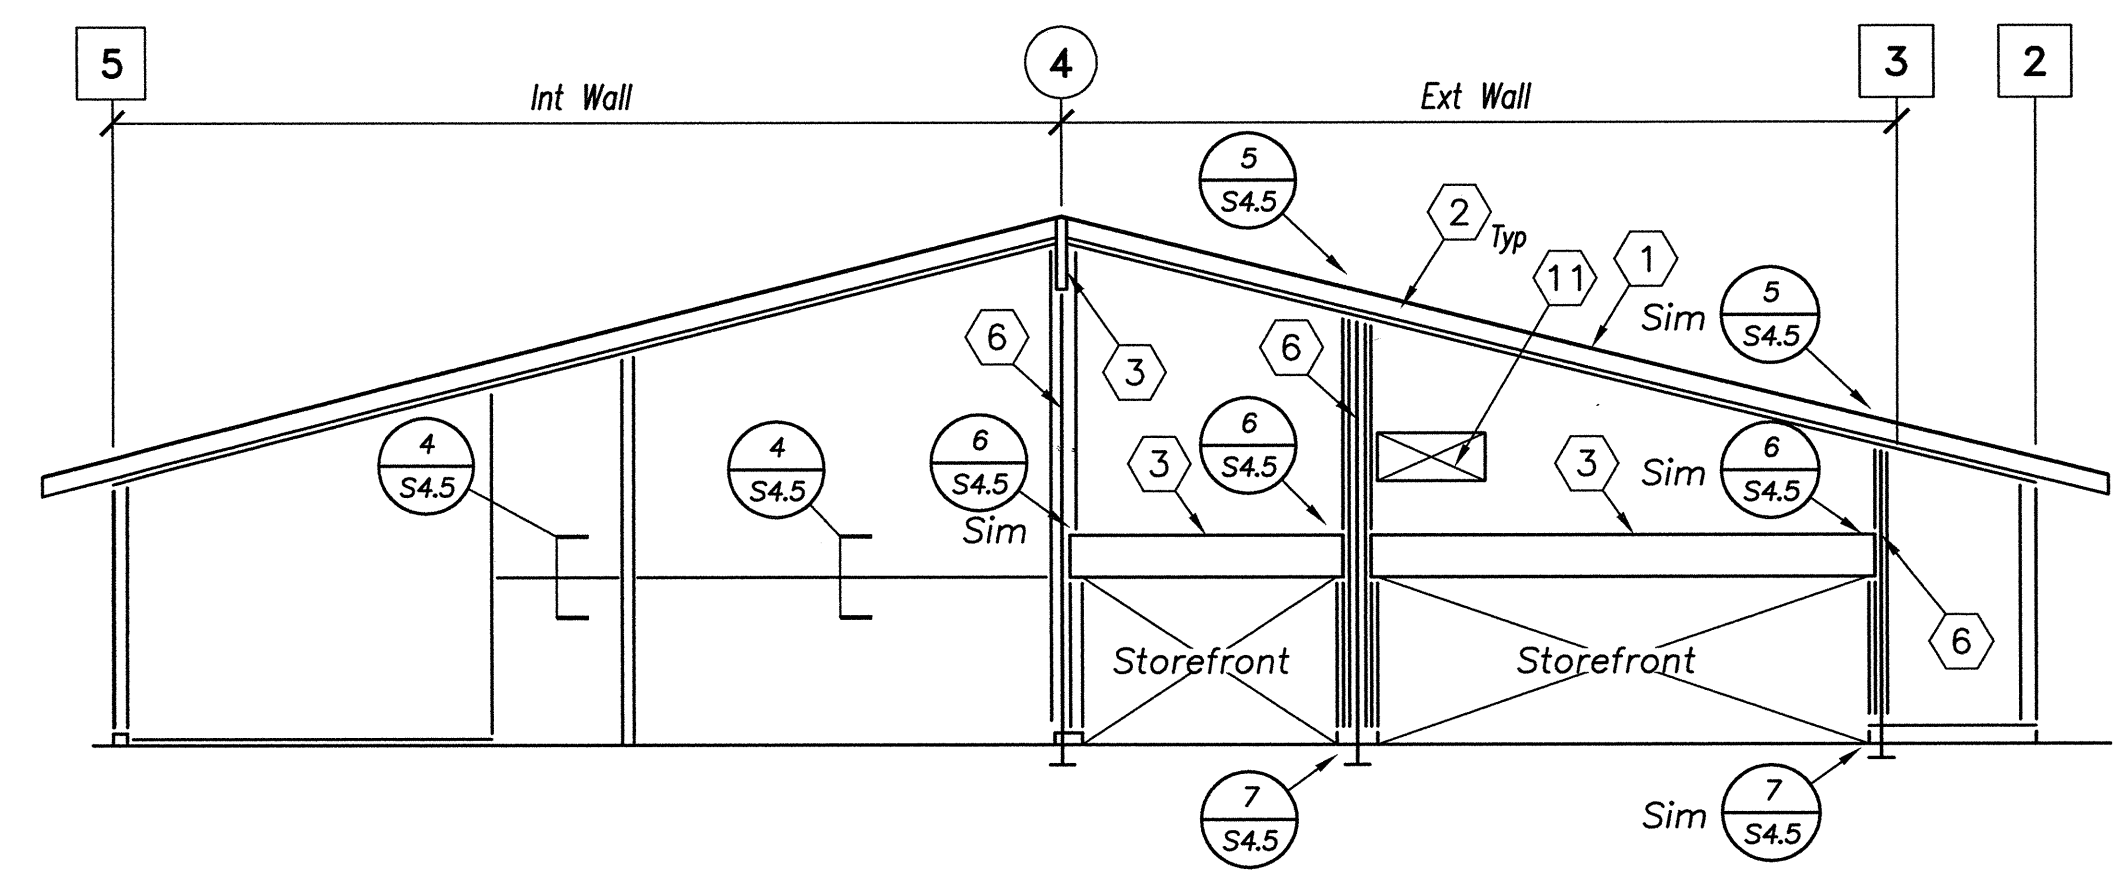


WALL FRAMING ELEVATION - LINE F $\frac{1}{8}'' = 1'-0''$

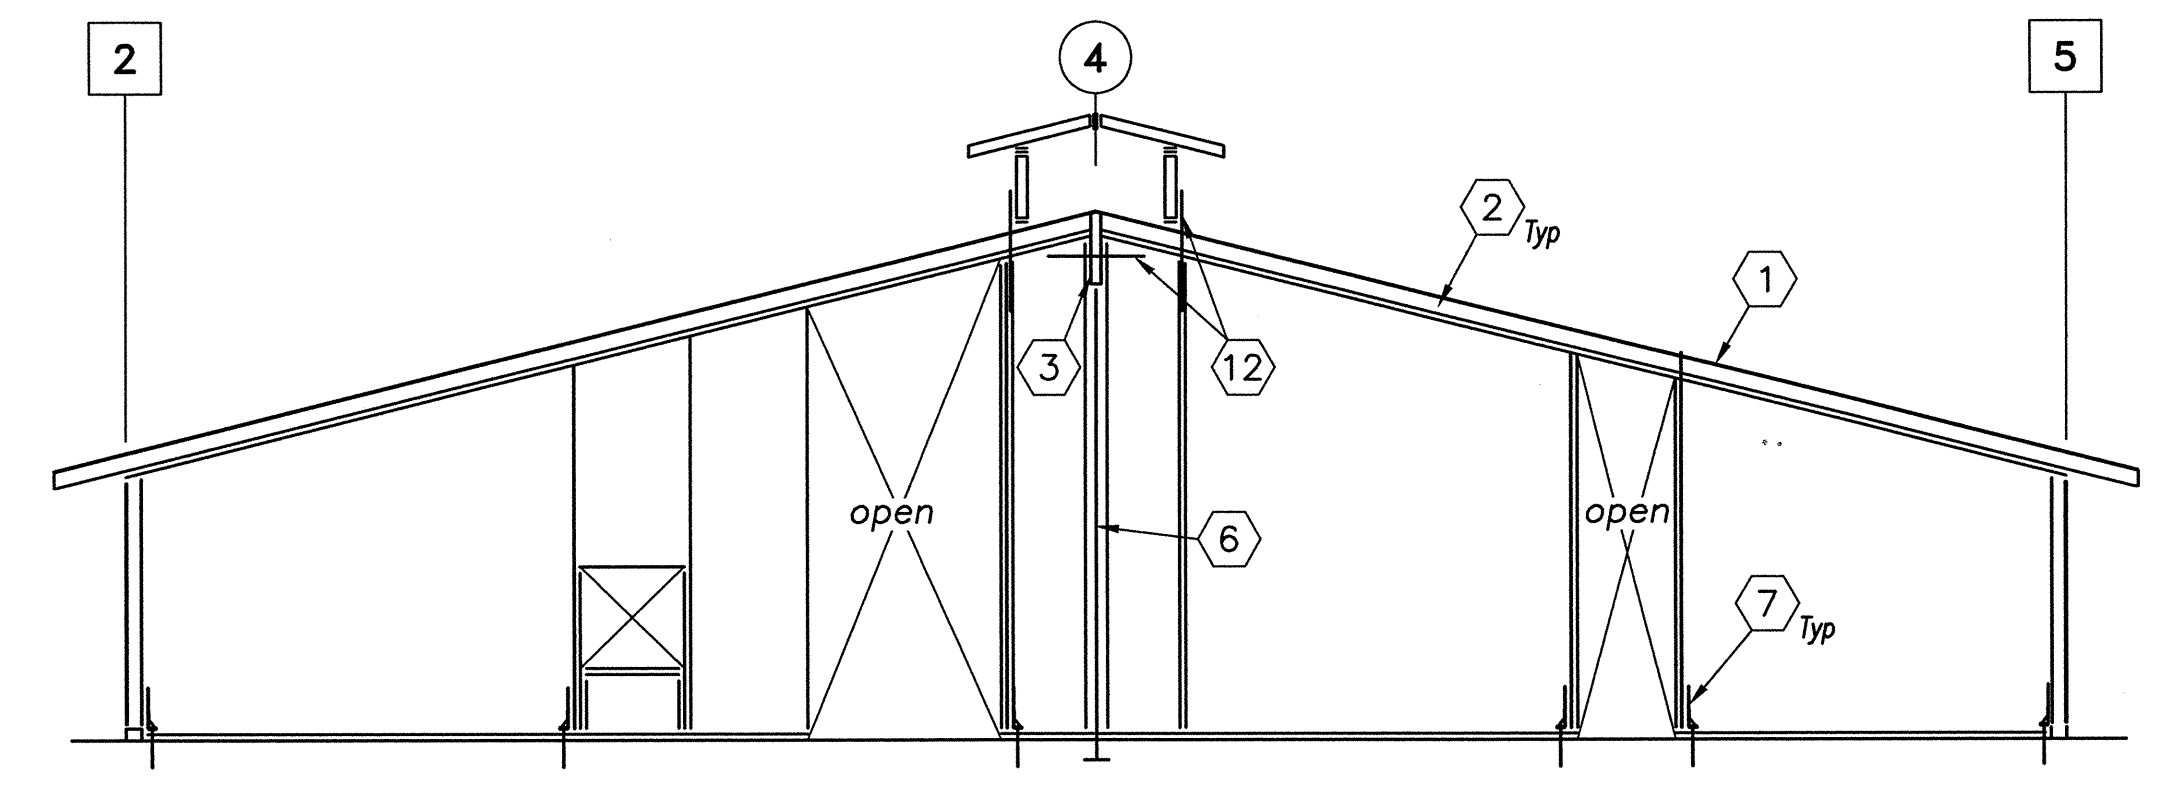

WALL FRAMING ELEVATION - LINE B $\frac{1}{8}'' = 1'-0''$

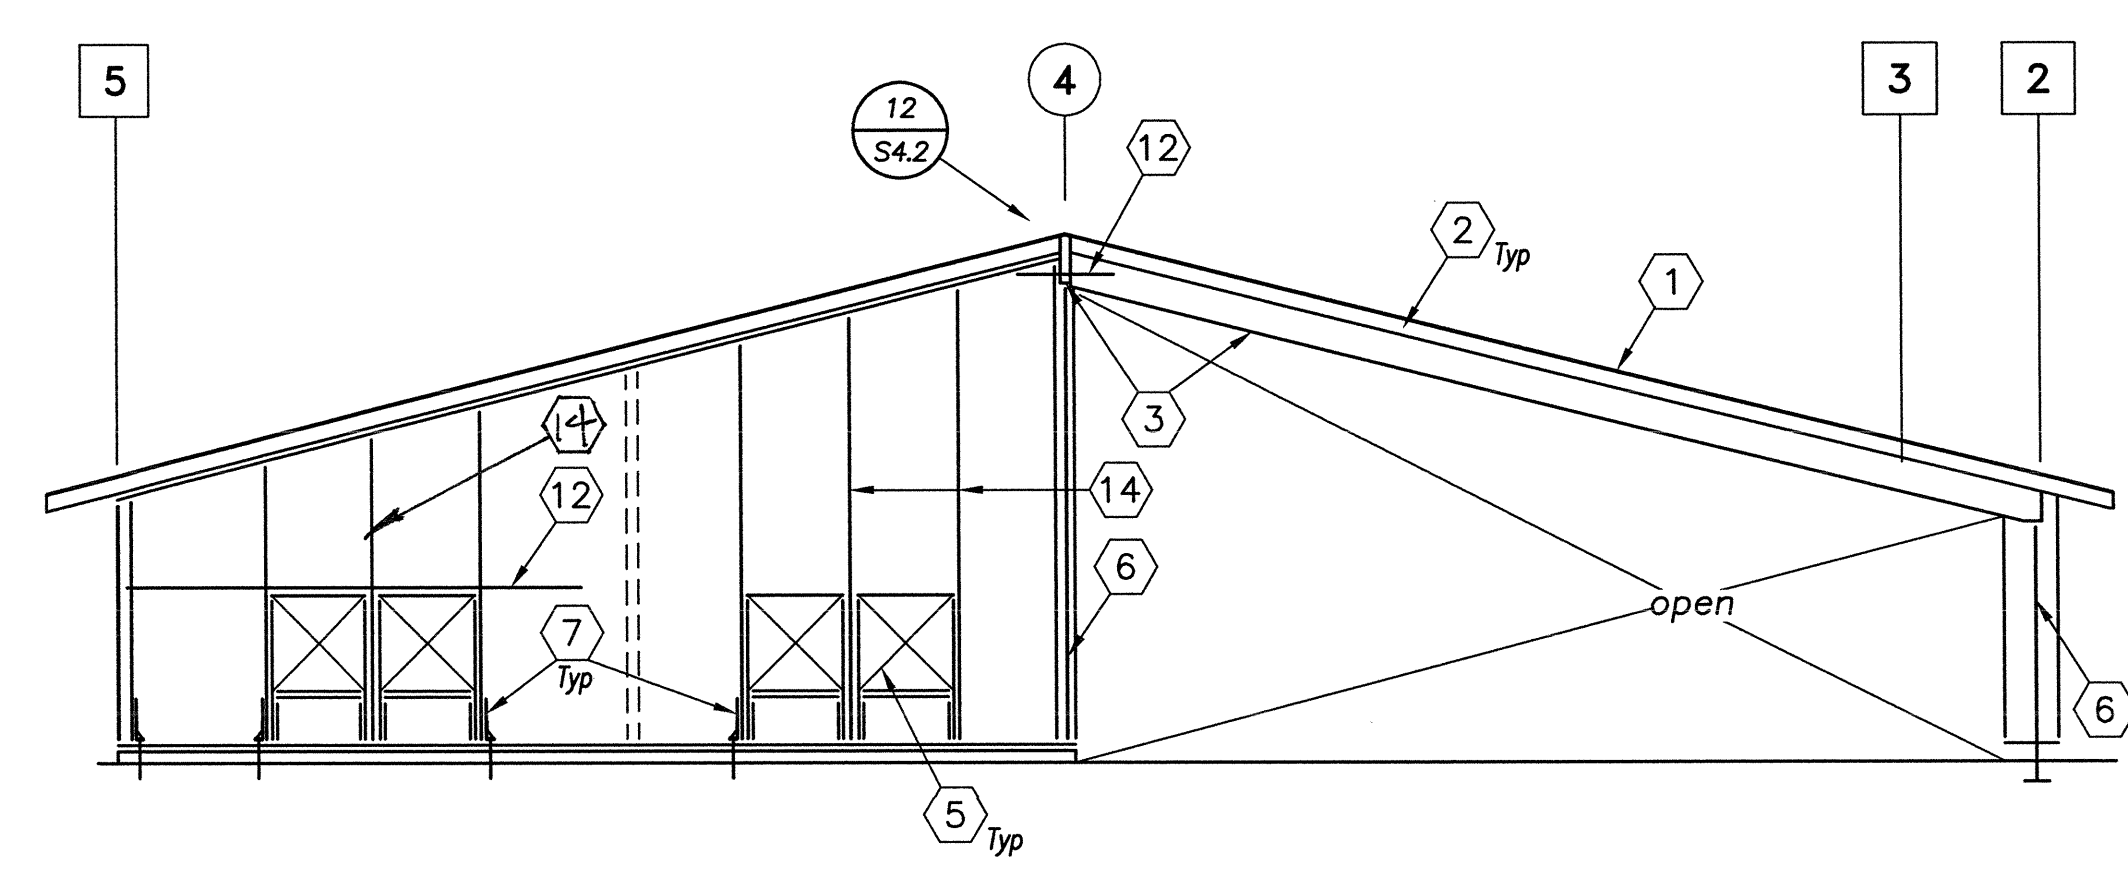

WALL FRAMING ELEVATION - LINE G $\frac{1}{8}'' = 1'-0''$

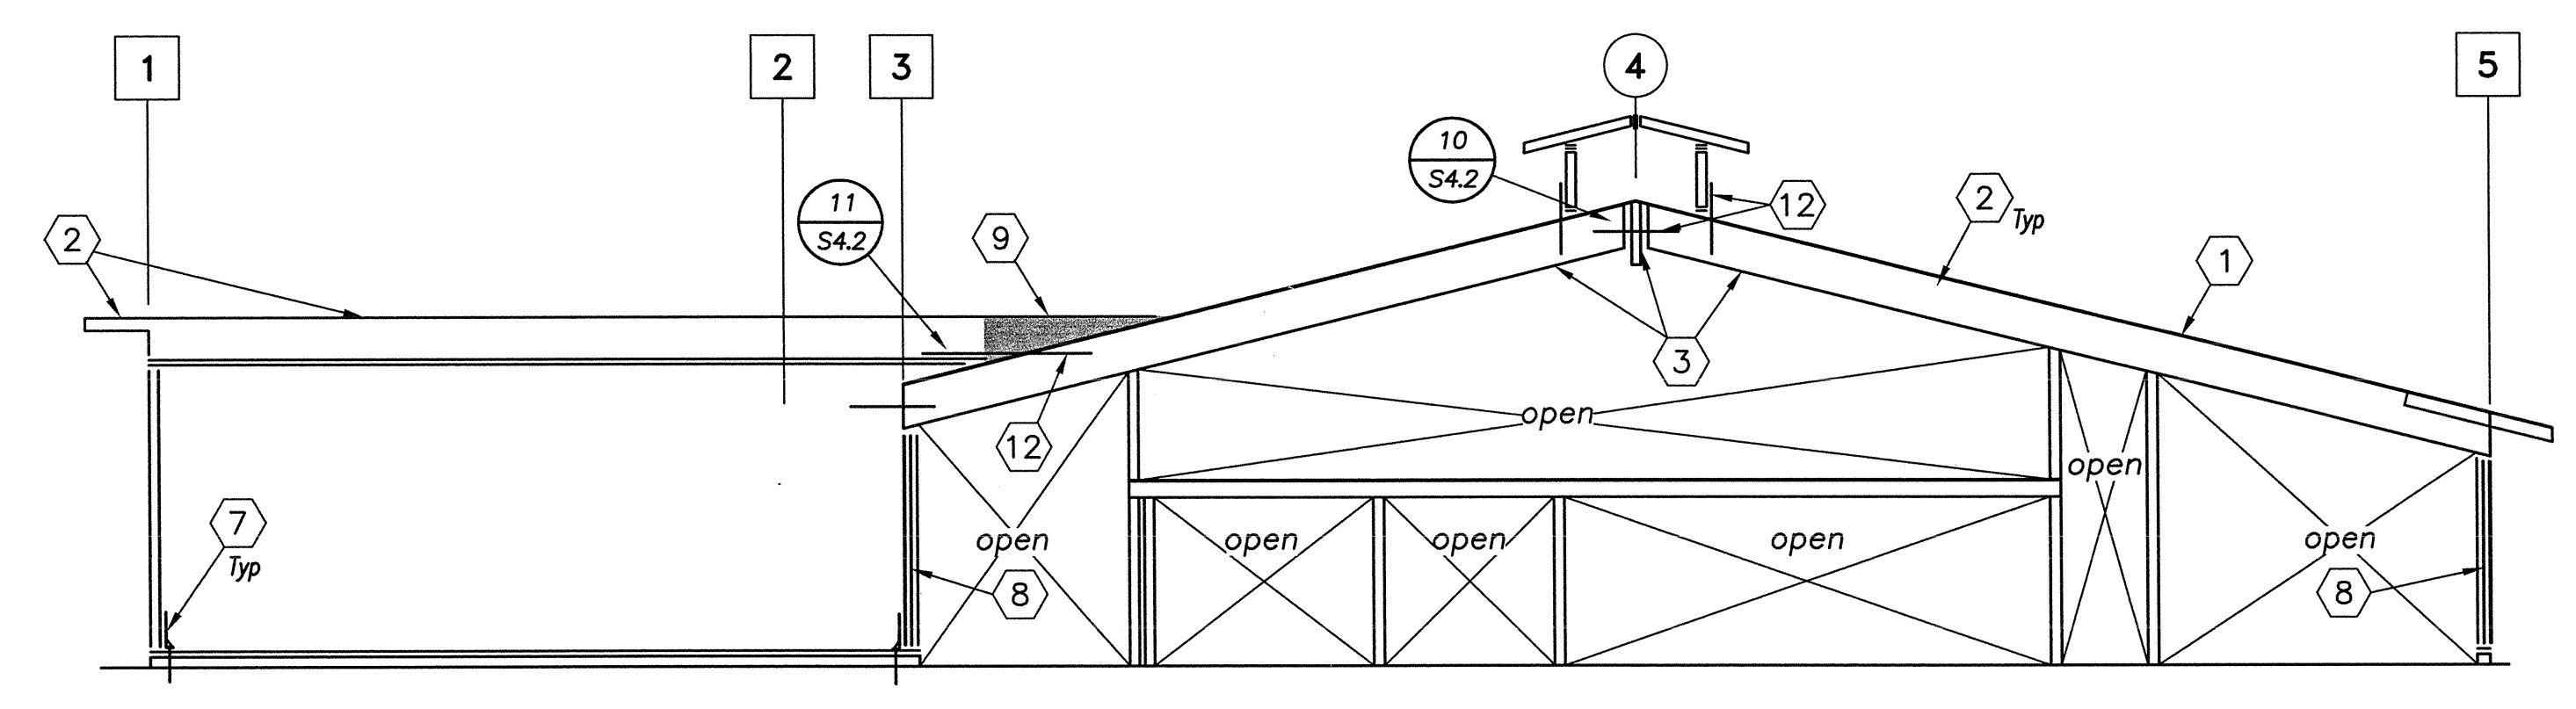

WALL FRAMING ELEVATION - LINE C $\frac{1}{8}'' = 1'-0''$

ELEVATION SHEET NOTES:

- 1 Roof SP per plan
- 2 Roof frmg per plan
- 3 GL beam per plan
- 4 NOT USED
- 5 Frame ext opng per $\frac{2}{S0.3}$
- 6 HSS col per plan
- 7 HD & post per plan
- 8 Post per plan
- 9 California frmg
- 10 NOT USED
- 11 Mech duct opng typ per $\frac{4}{S0.3}$
- 12 Strap per plan
- 13 NOT USED
- 14 3-2x8 king stud w/A35 ea side T&B
- 15 NOT USED

Dry Creek Joint Elementary School District
District Education Center
8849 Cook Riolo Road, Roseville, CA 95747
Dry Creek Joint Elementary School District

FILE NO. 31-15
IDENTIFICATION STAMP DIV. OF THE
STATE ARCHITECT OFFICE OF
REGULATION SERVICES
APPLICATION NO.
02-115456
AC FLS SS
DATE 1/21/18

DIVISION OF THE STATE ARCHITECT
revision date: by:

www.barrish.com
barrish pelham
Consulting Engineers
Sacramento-Walnut Creek, Tehono
CONSULTANT

nacht&lewis
600 Q Street, Suite 100
Sacramento, CA 95811
www.nachtandlewis.com
916.329.4000

ARCHITECT
No. C-28467
RENEWAL DATE: 1/21/18
STATE OF CALIFORNIA

INITIAL BOX			
NO.	DWG BY	DATE	REVIEWED


REVISIONS			
NO.	DESCRIPTION	DATE	REV
	100% design development	7/8/16	
	75% construction documents	9/20/16	
	DSA Submittal	12/31/16	
	DSA Backcheck	02/23/17	

DATE February 23, 2017
JOB NO. Y1538.00
SHEET TITLE


Wall Framing
Elevations

SHEET NO.
S3.2


ONE INCH = TWENTY FEET
ONE-SIXTEENTH INCH = ONE FOOT
ONE-EIGHTH INCH = ONE FOOT
ONE-FOURTH INCH = ONE FOOT
ONE-HALF INCH = ONE FOOT
THREE-QUARTERS INCH = ONE FOOT
ONE INCH = ONE FOOT
ONE AND ONE-HALF INCH = ONE FOOT

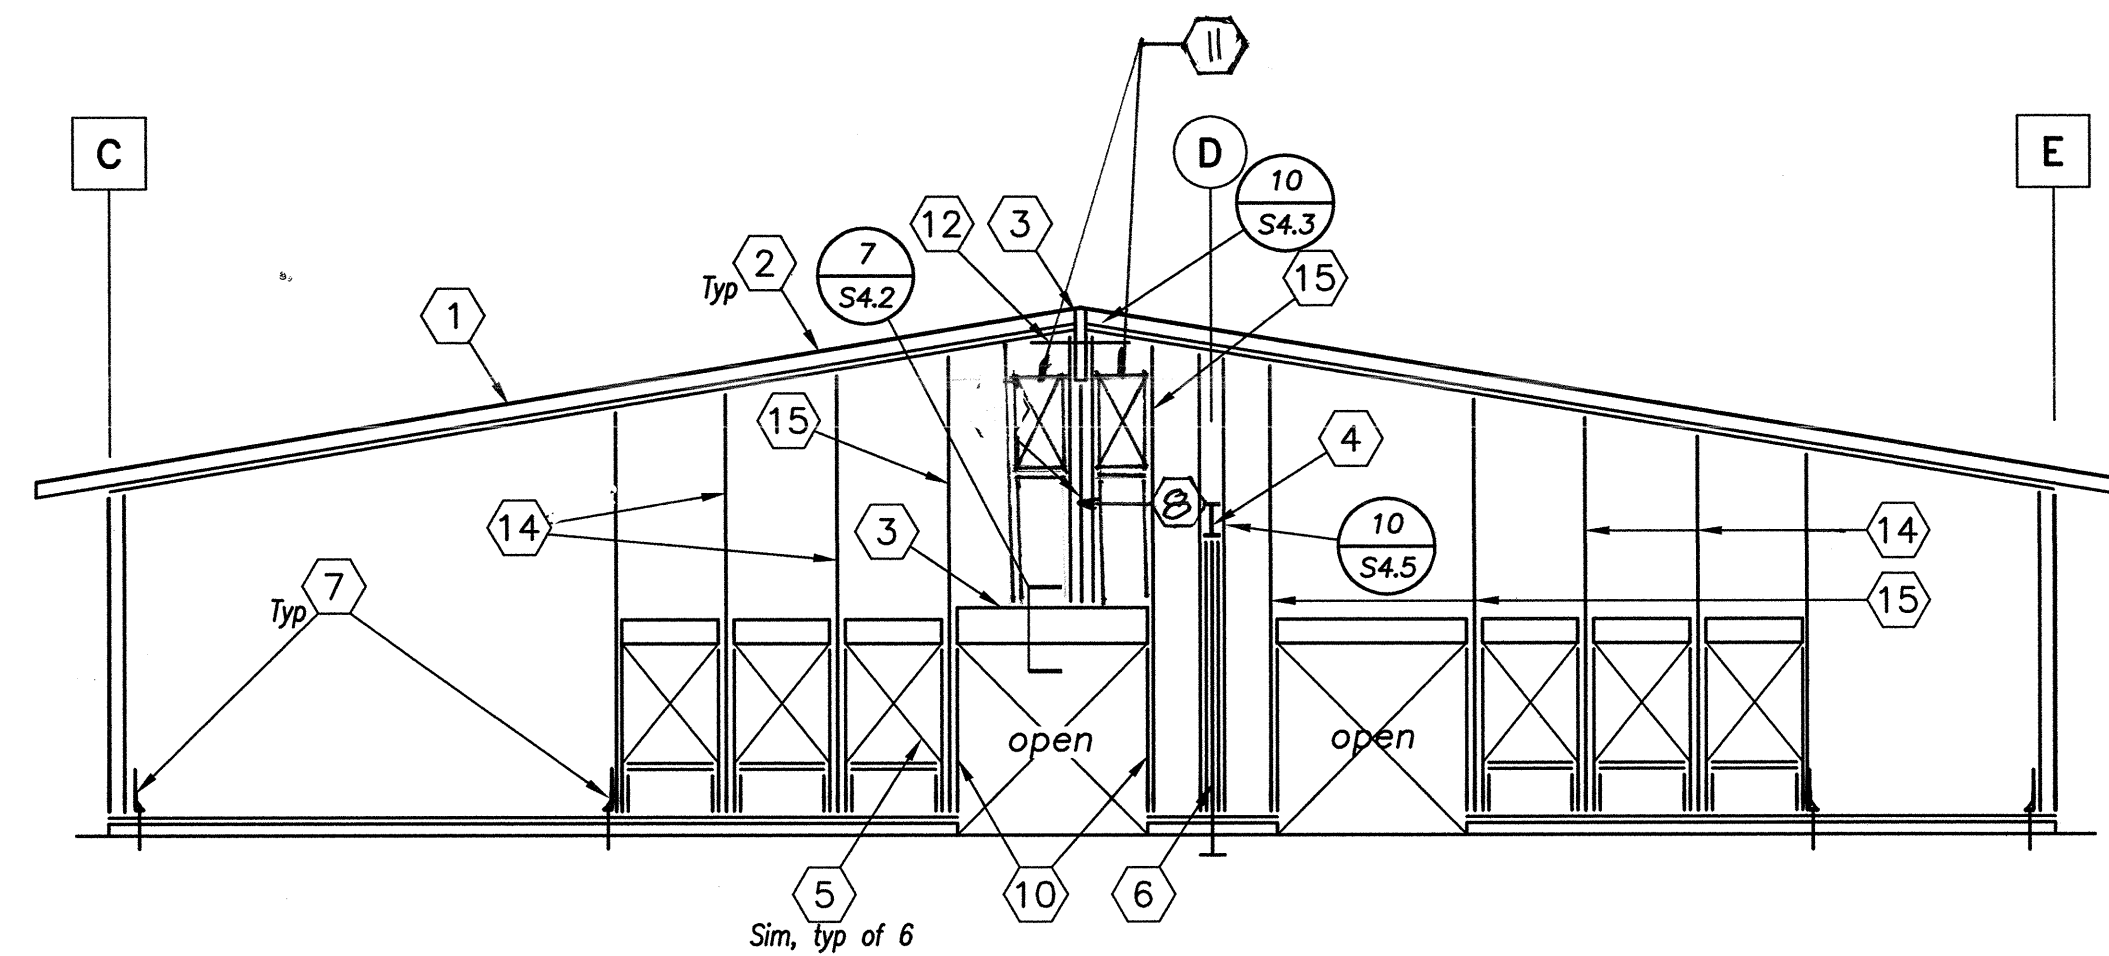


WALL FRAMING ELEVATION - LINE 1
1/8" = 1'-0"

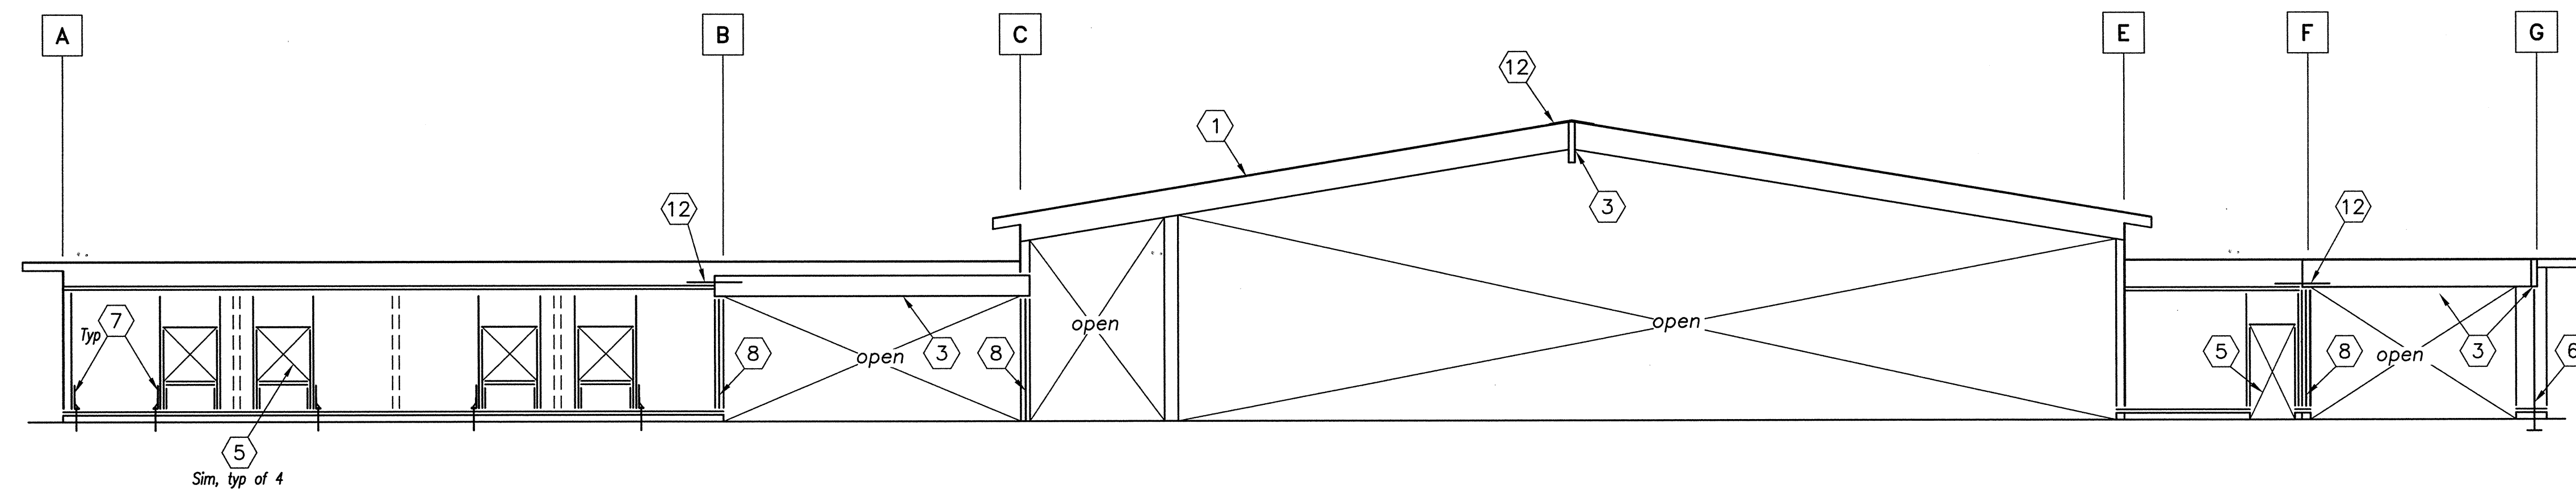

WALL FRAMING ELEVATION - LINE 2
1/8" = 1'-0"

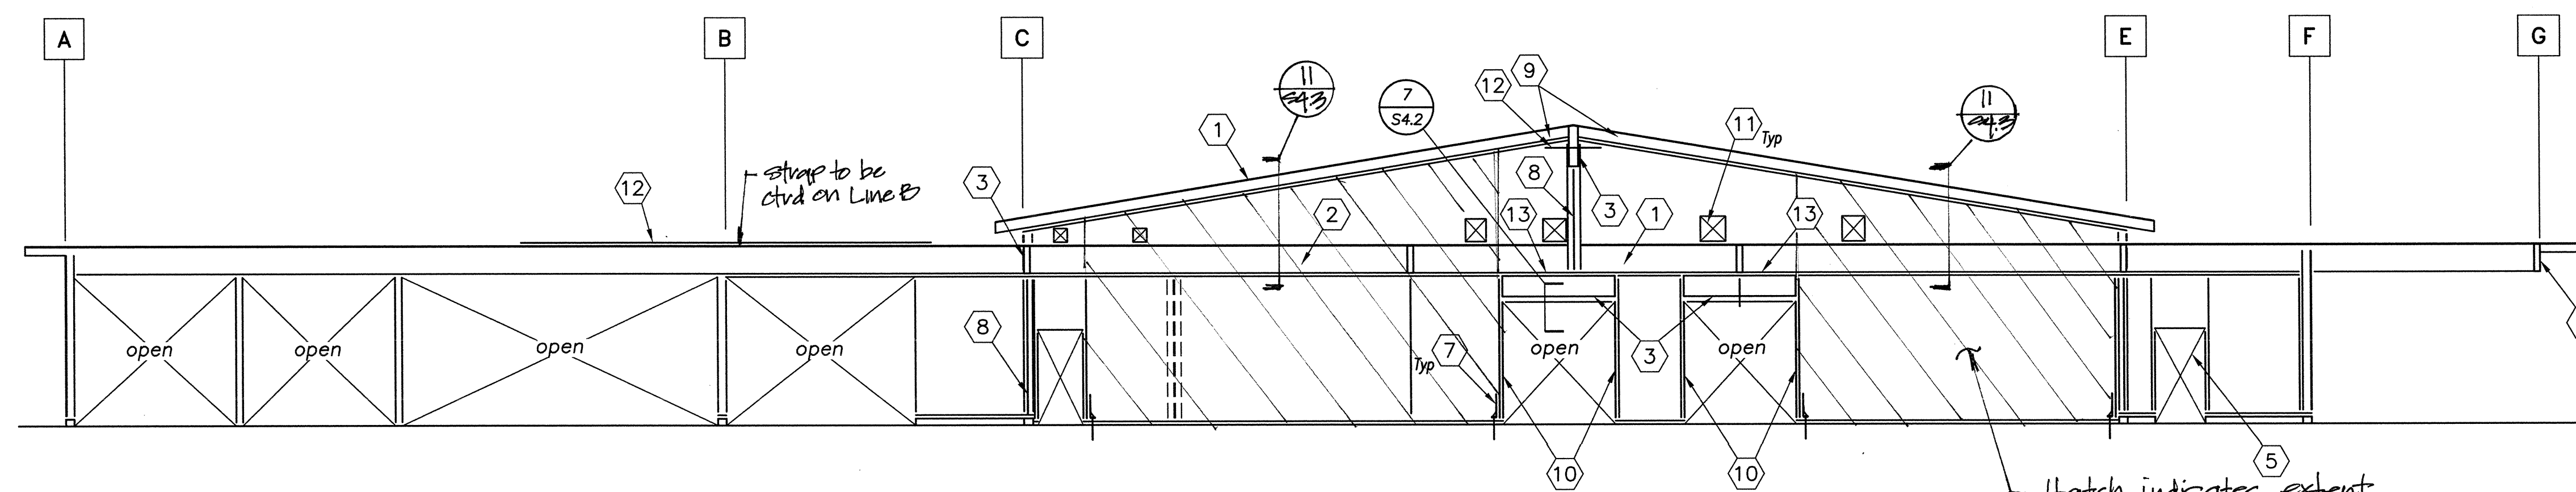

WALL FRAMING ELEVATION - LINE 3
1/8" = 1'-0"

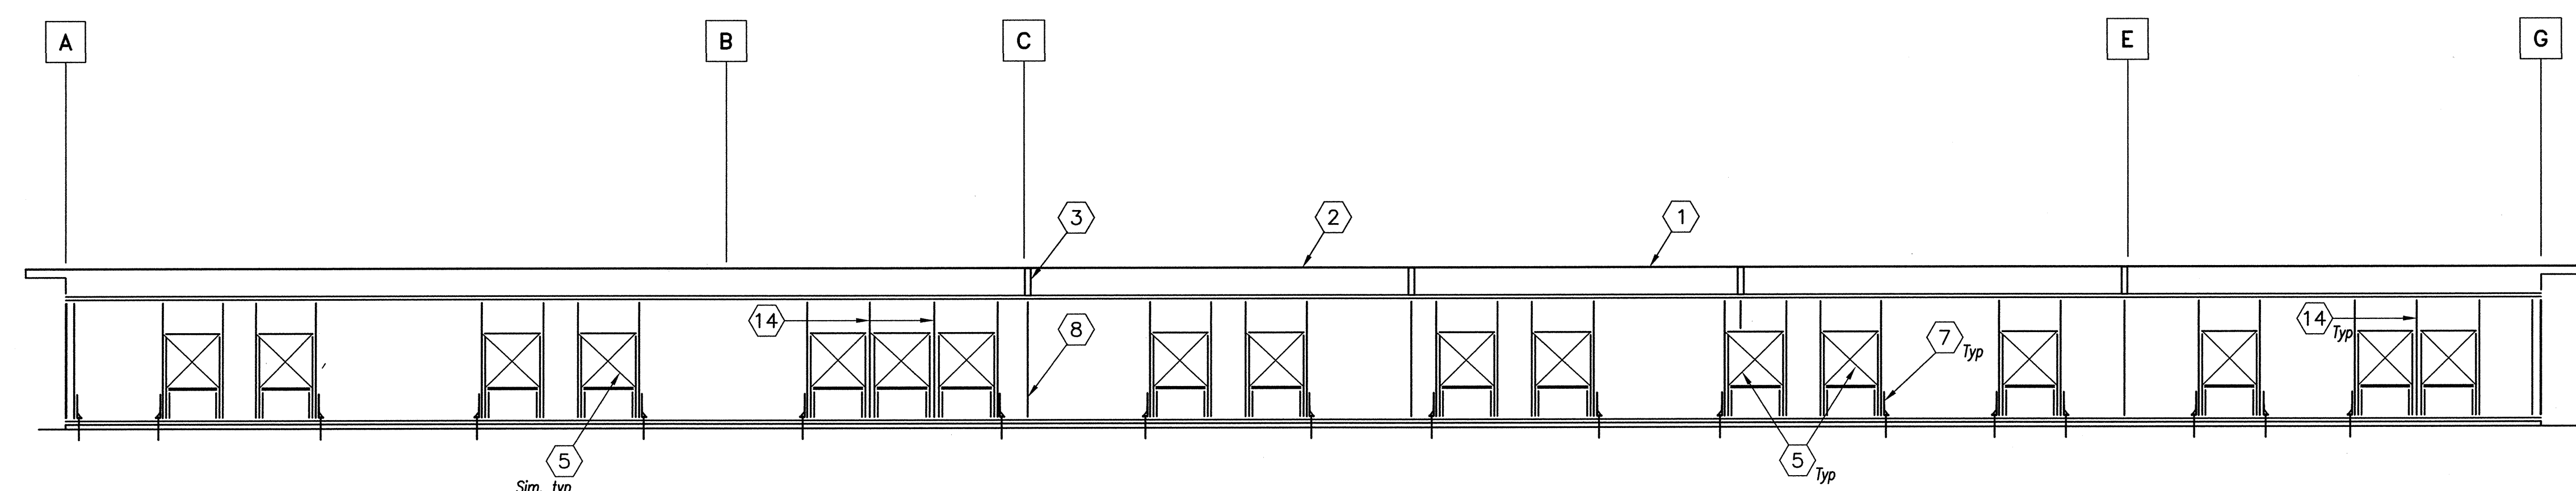

WALL FRAMING ELEVATION - LINE 5
1/8" = 1'-0"

ELEVATION SHEET NOTES:

- 1 Roof SP per plan
- 2 Roof frmg per plan
- 3 GL beam per plan
- 4 W beam per plan
- 5 Frame ext opng per $\frac{2}{S0.3}$
- 6 HSS col per plan
- 7 HD & post per plan
- 8 Post per plan
- 9 California frmg
- 10 4x8 trimmer under hdr
- 11 Mech duct opng typ per $\frac{4}{S0.3}$
- 12 Strap per plan
- 13 Upper top PL to extend 4'-0" min onto GL bm - nail w/20-16d
- 14 3-2x8 king stud w/A35 ea side T&B
- 15 6x8 king stud w/A35 ea side T&B

Dry Creek Joint Elementary School District
District Education Center


8849 Cook Riolo Road, Roseville, CA 95747

Dry Creek Joint Elementary School District

FILE NO. 31-15
IDENTIFICATION STAMP DIV. OF THE
STATE ARCHITECT OFFICE OF
REGULATION SERVICES
APPLICATION NO.
02-115456
AC FLS SS
DATE 2/23/17


DIVISION OF THE STATE ARCHITECT
revision date: by:

www.barrish.com
barrish pelham
Consulting Engineers
Sacramento-Walnut Creek-Turlock

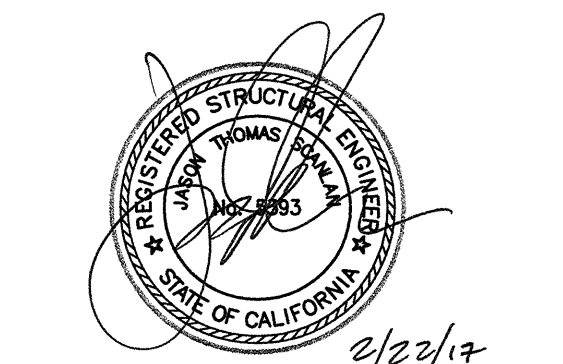

CONSULTANT

nacht&lewis
600 Q Street, Suite 100
Sacramento, CA 95811
www.nachtandlewis.com
916.329.4000

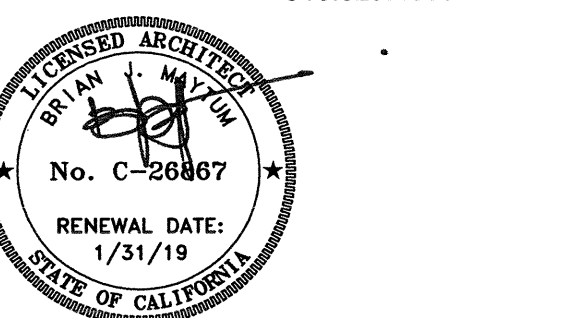

ARCHITECT

INITIAL BOX			
NO.	DWG BY	DATE	REVIEWED

REVISIONS			
NO.	DESCRIPTION	DATE	REV
	100% design development	7/6/16	
	75% construction documents	9/20/16	
	DSA Submittal	12/31/16	
	DSA Backcheck	02/23/17	













DATE February 23, 2017
JOB NO. Y1538.00
SHEET TITLE

Wall Framing
Elevations

SHEET NO.

S3.3

ONE AND ONE-HALF INCH = ONE FOOT
THREE-QUARTERS INCH = ONE FOOT
ONE-HALF INCH = ONE FOOT
ONE-QUARTER INCH = ONE FOOT
ONE-EIGHTH INCH = ONE FOOT
ONE-SIXTEENTH INCH = ONE FOOT
ONE INCH = TWENTY FEET

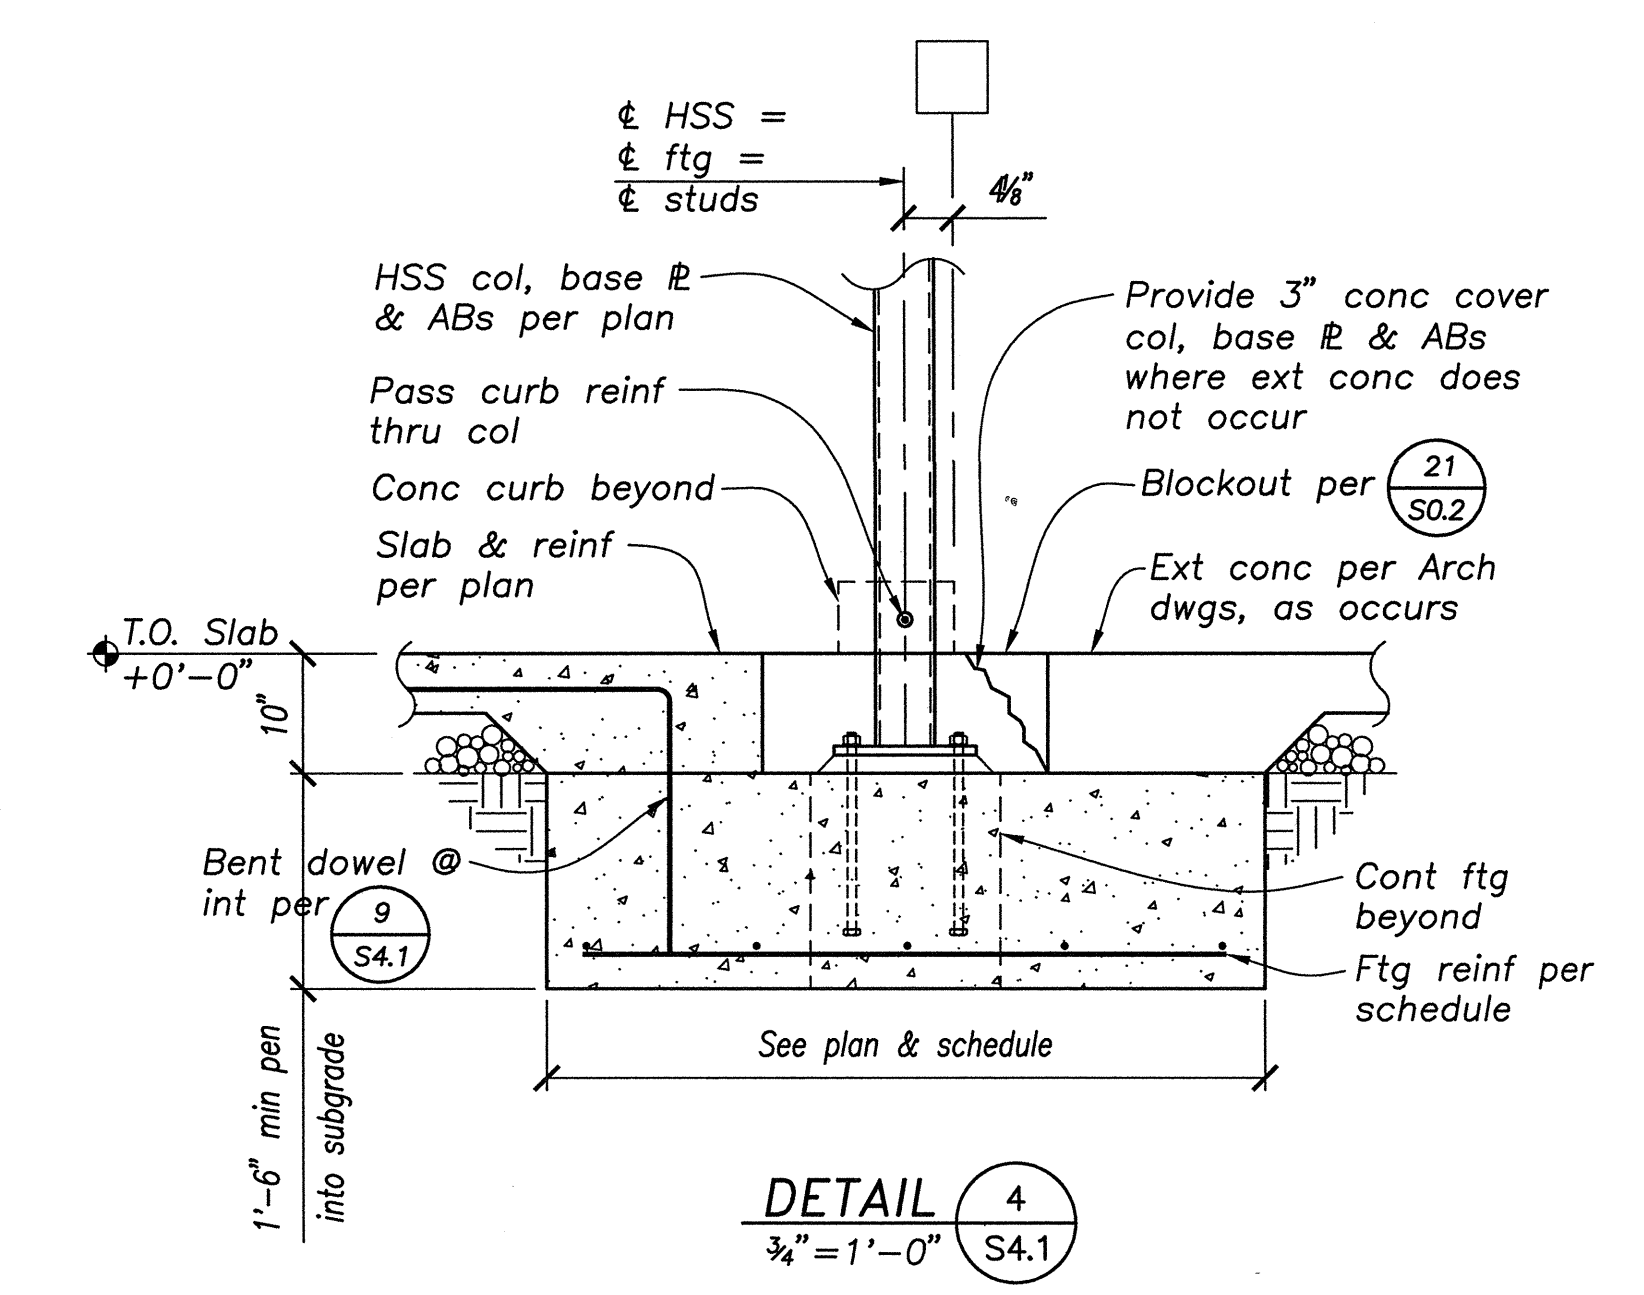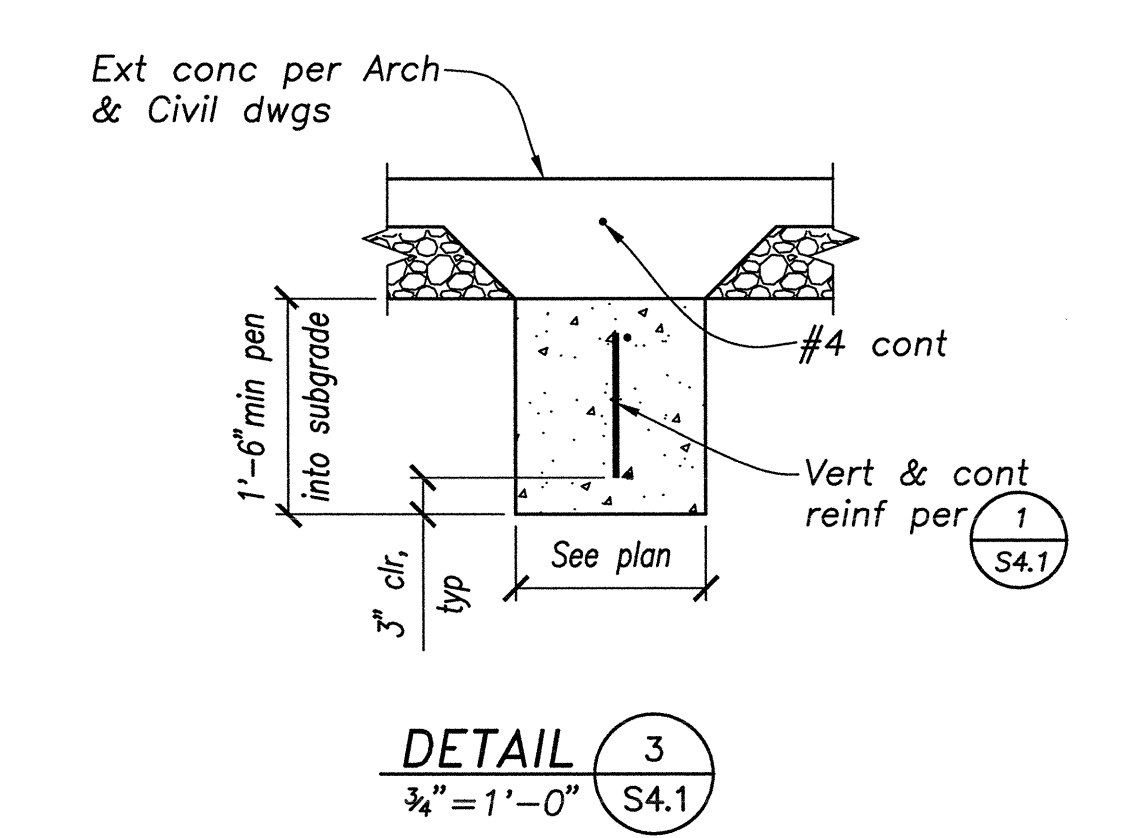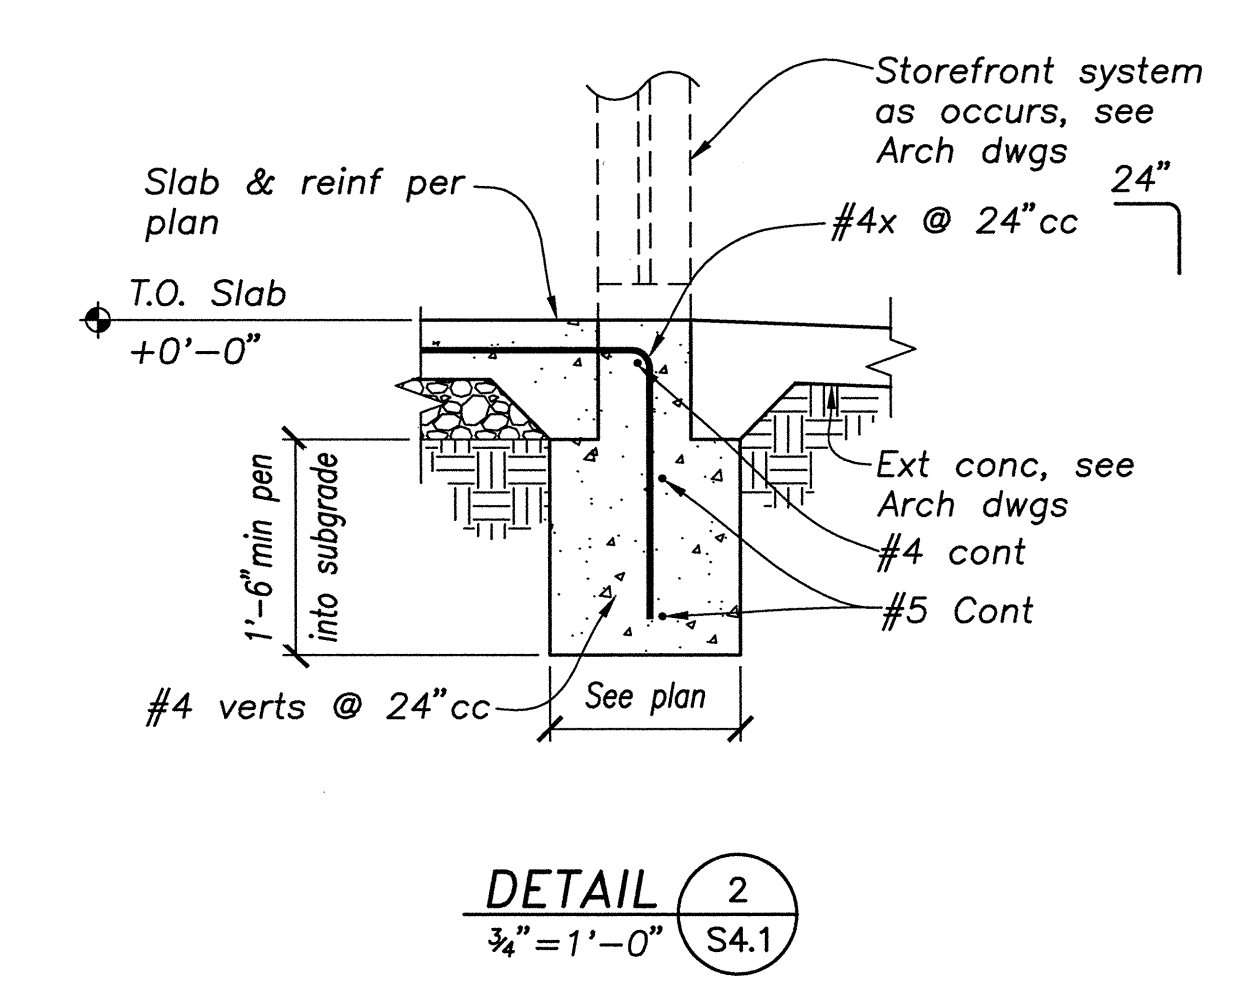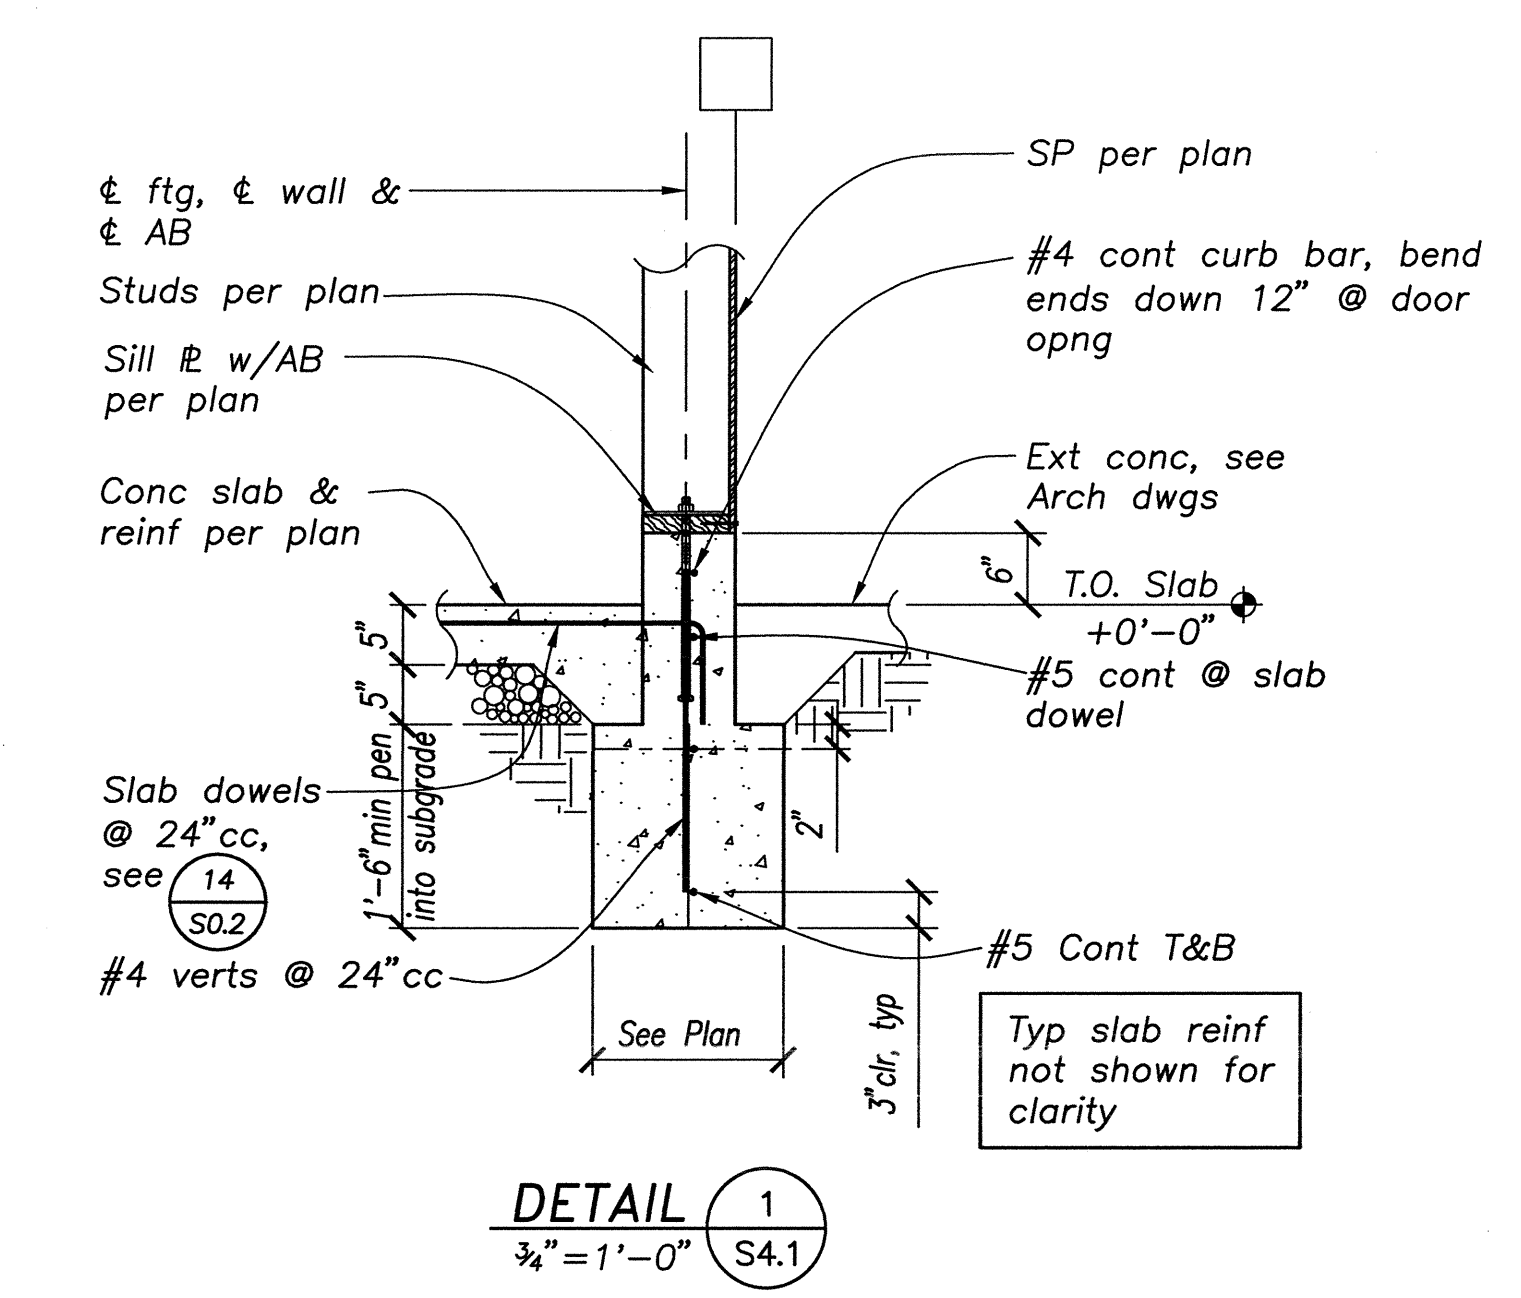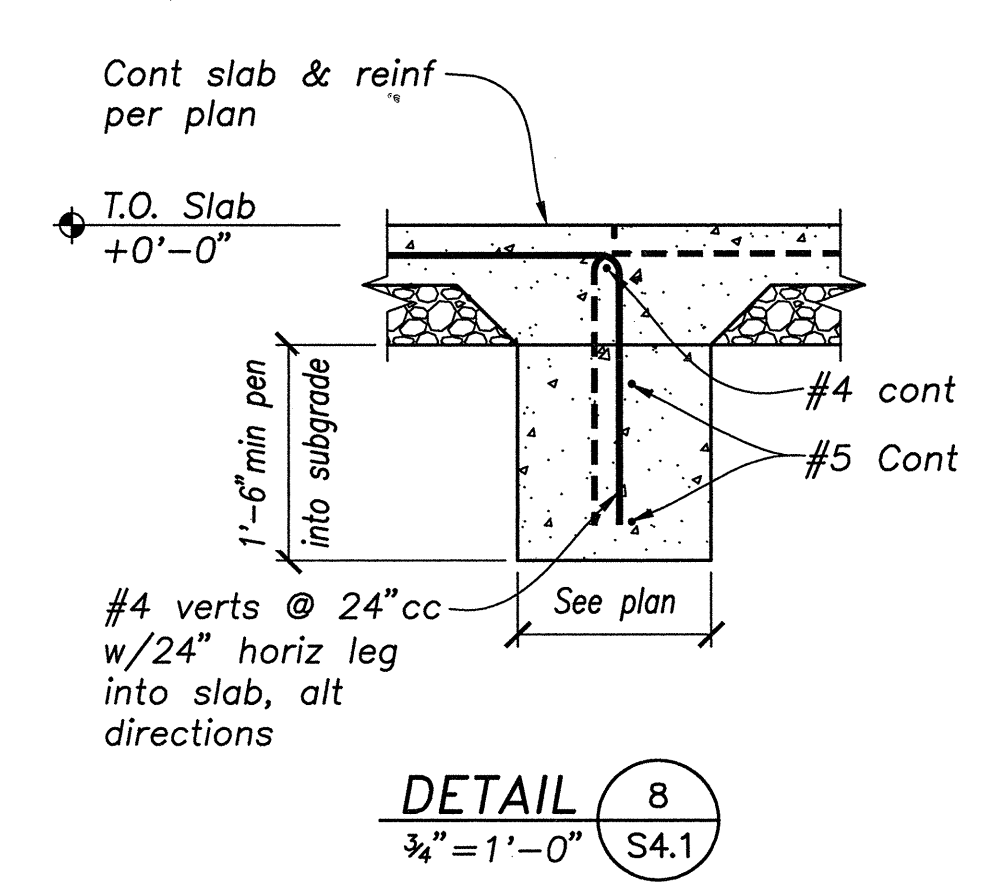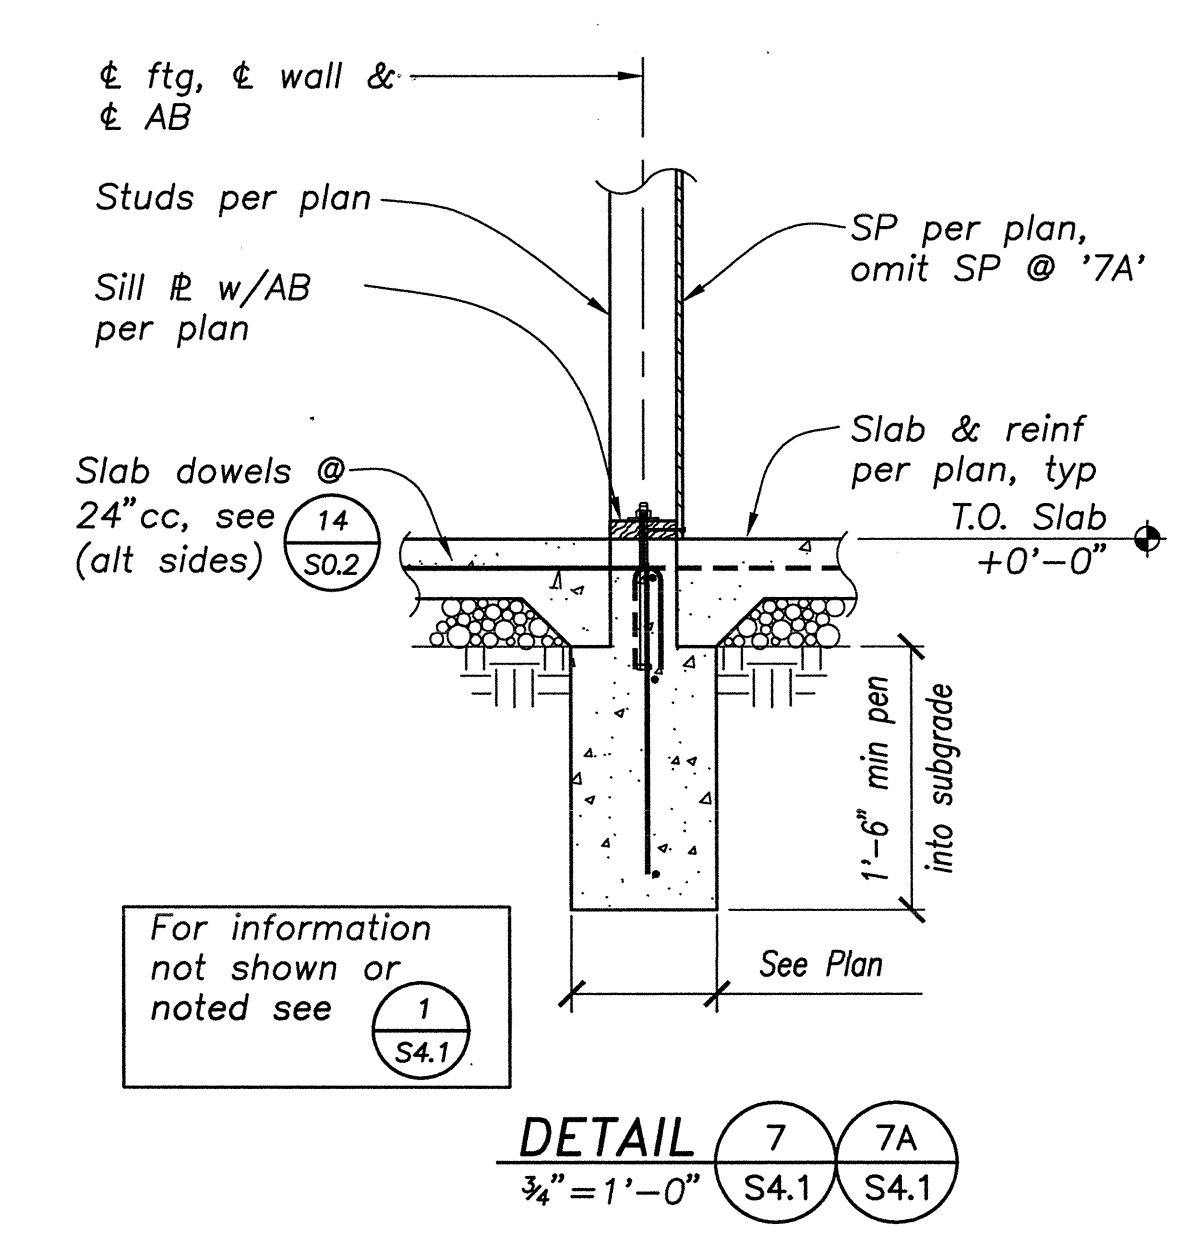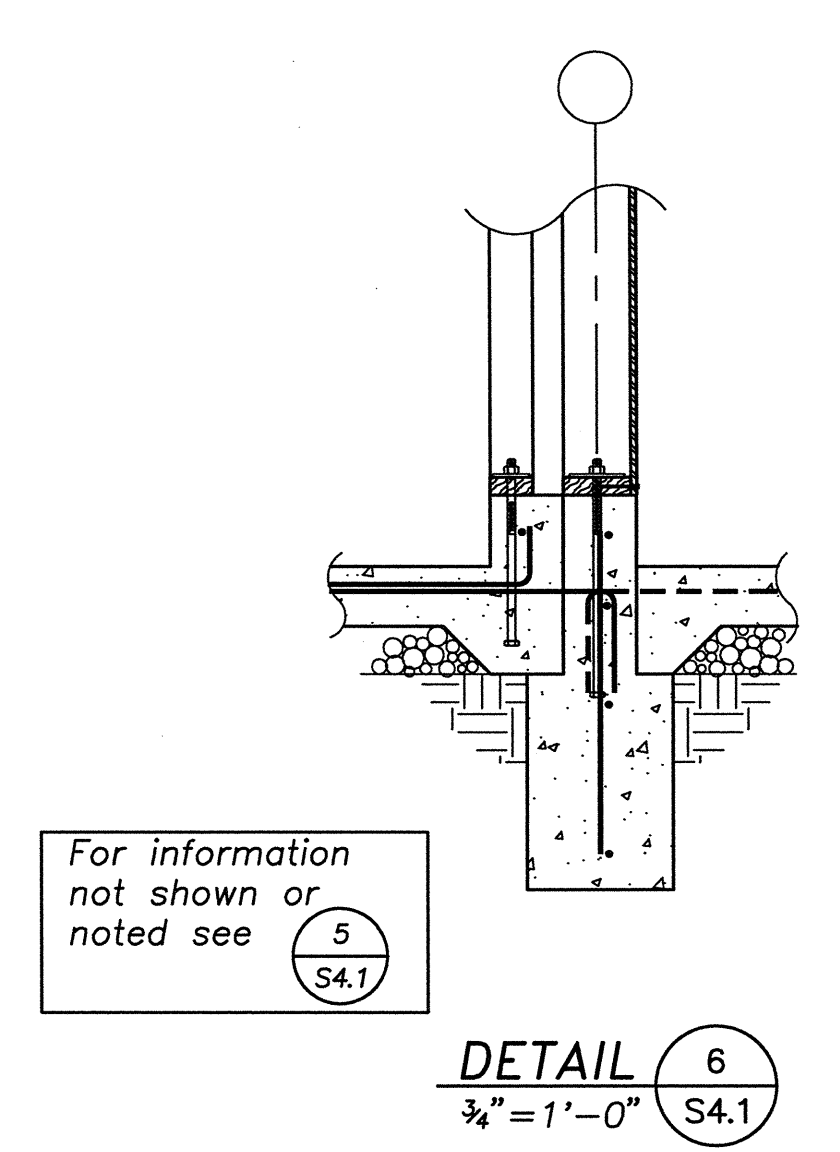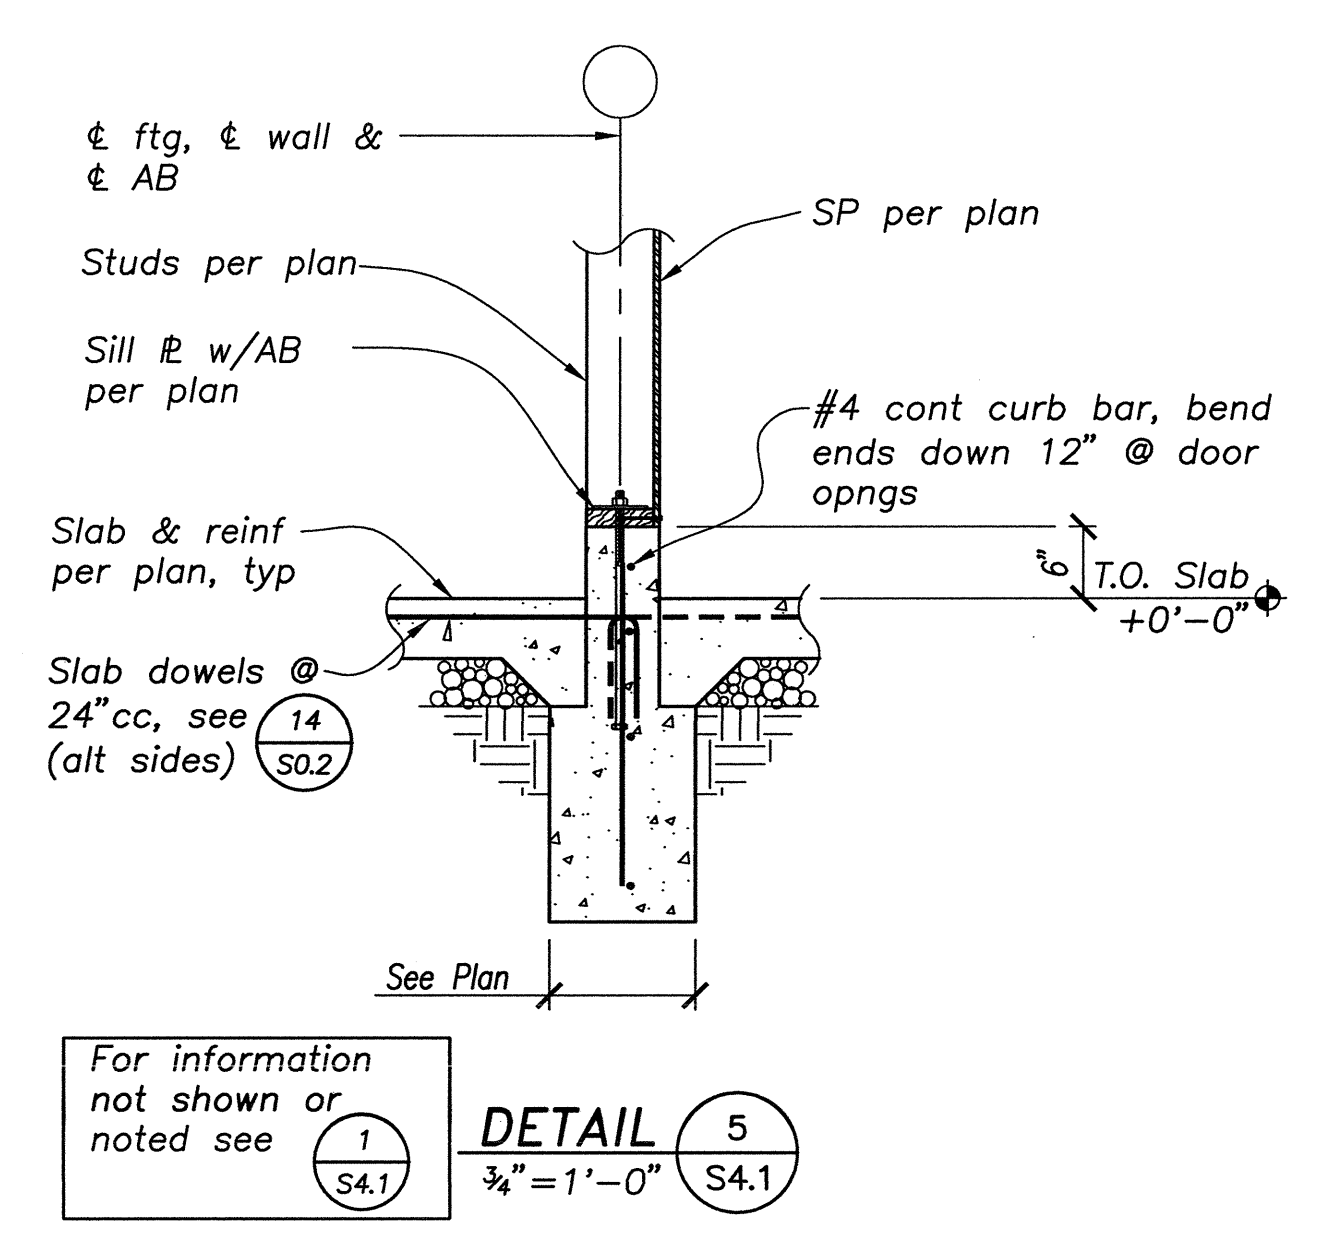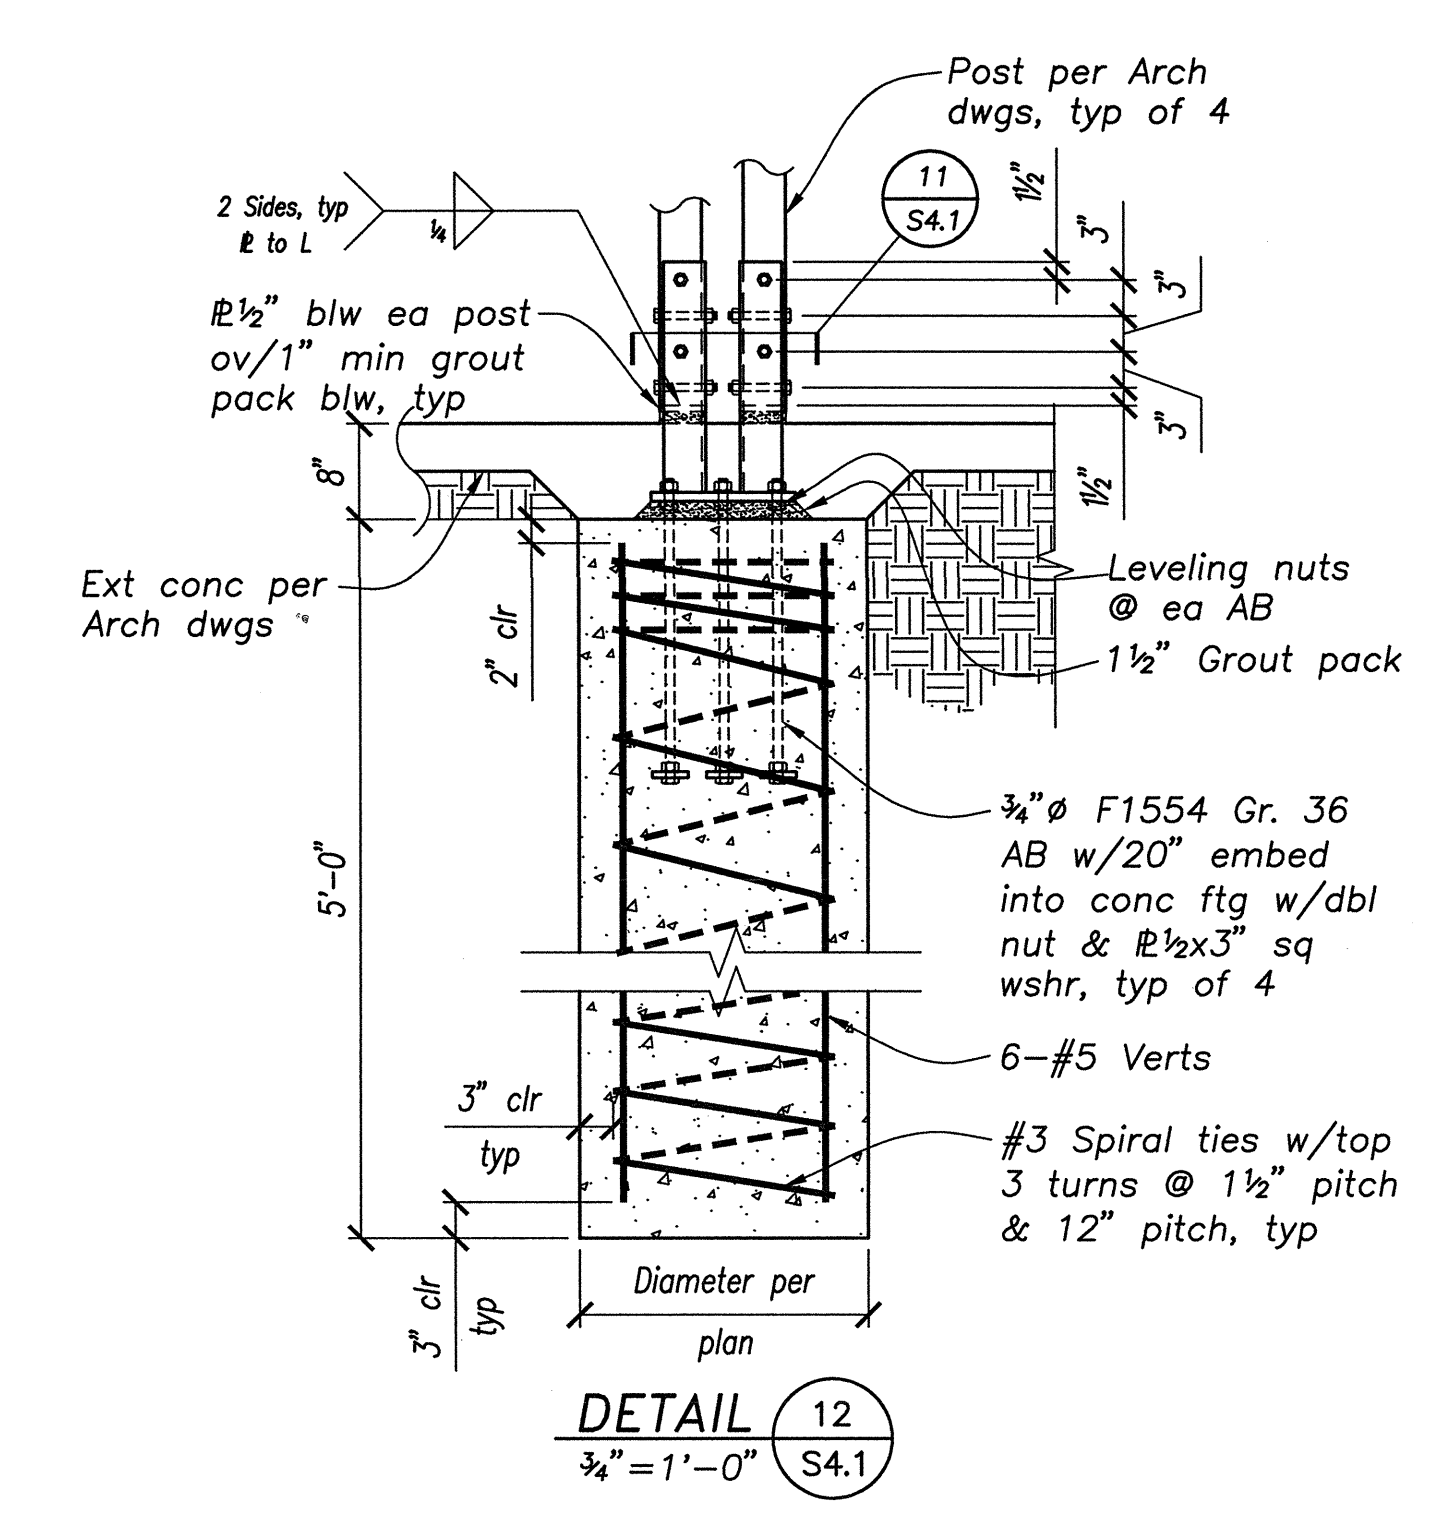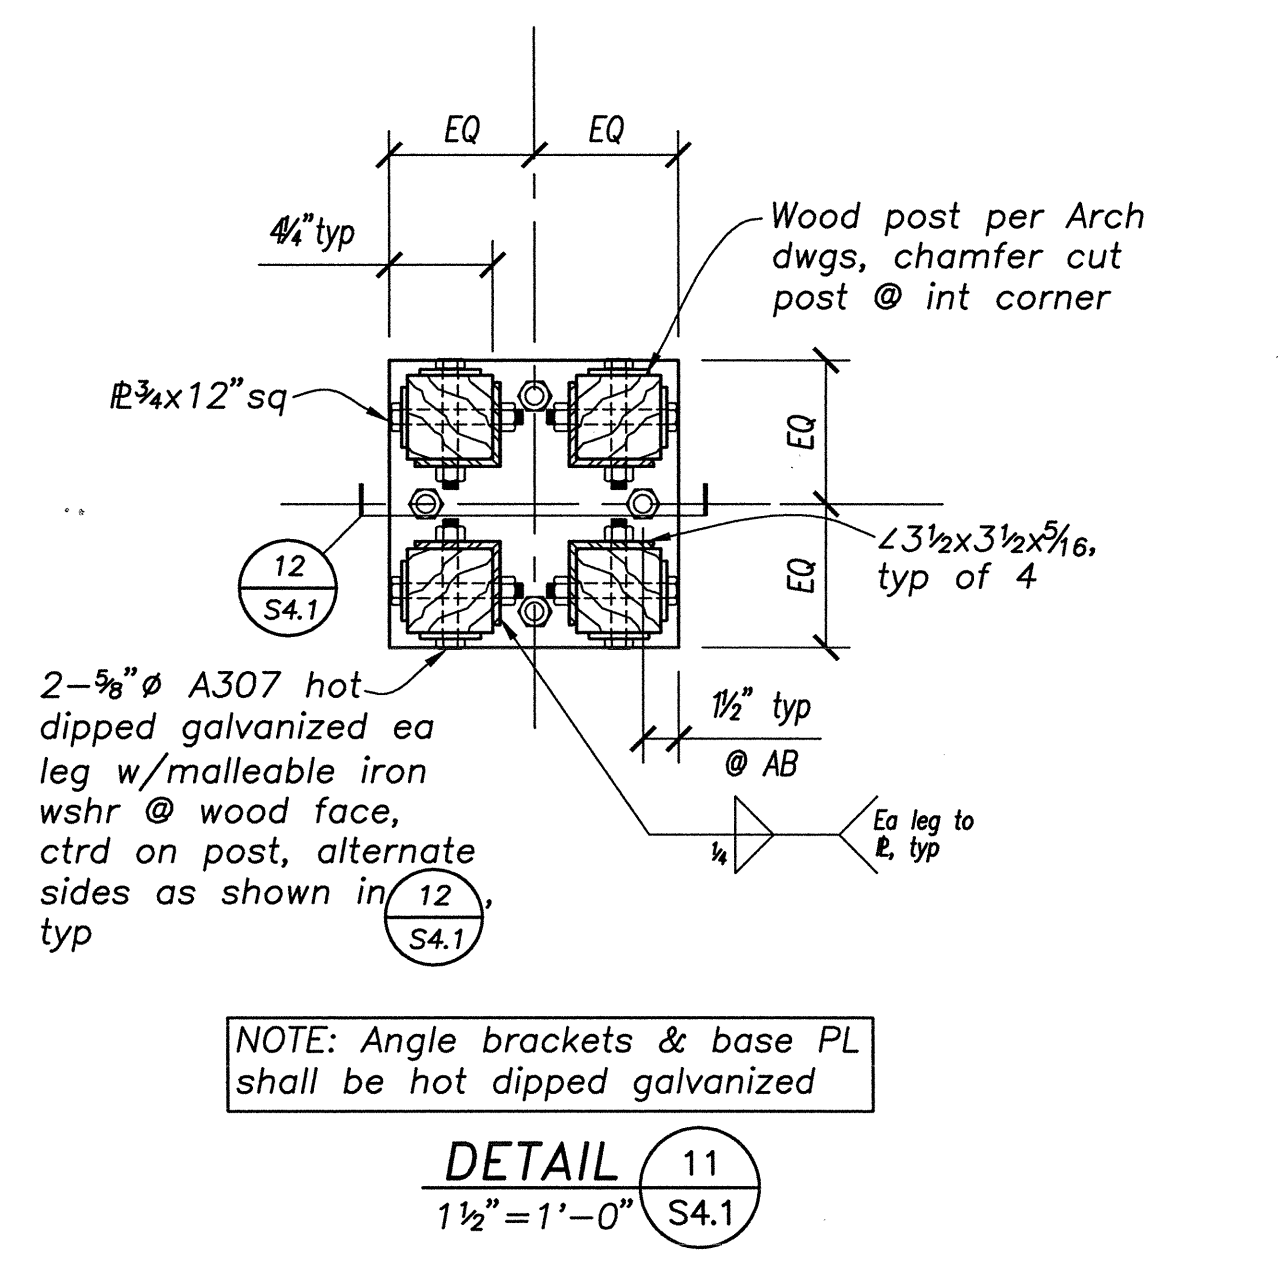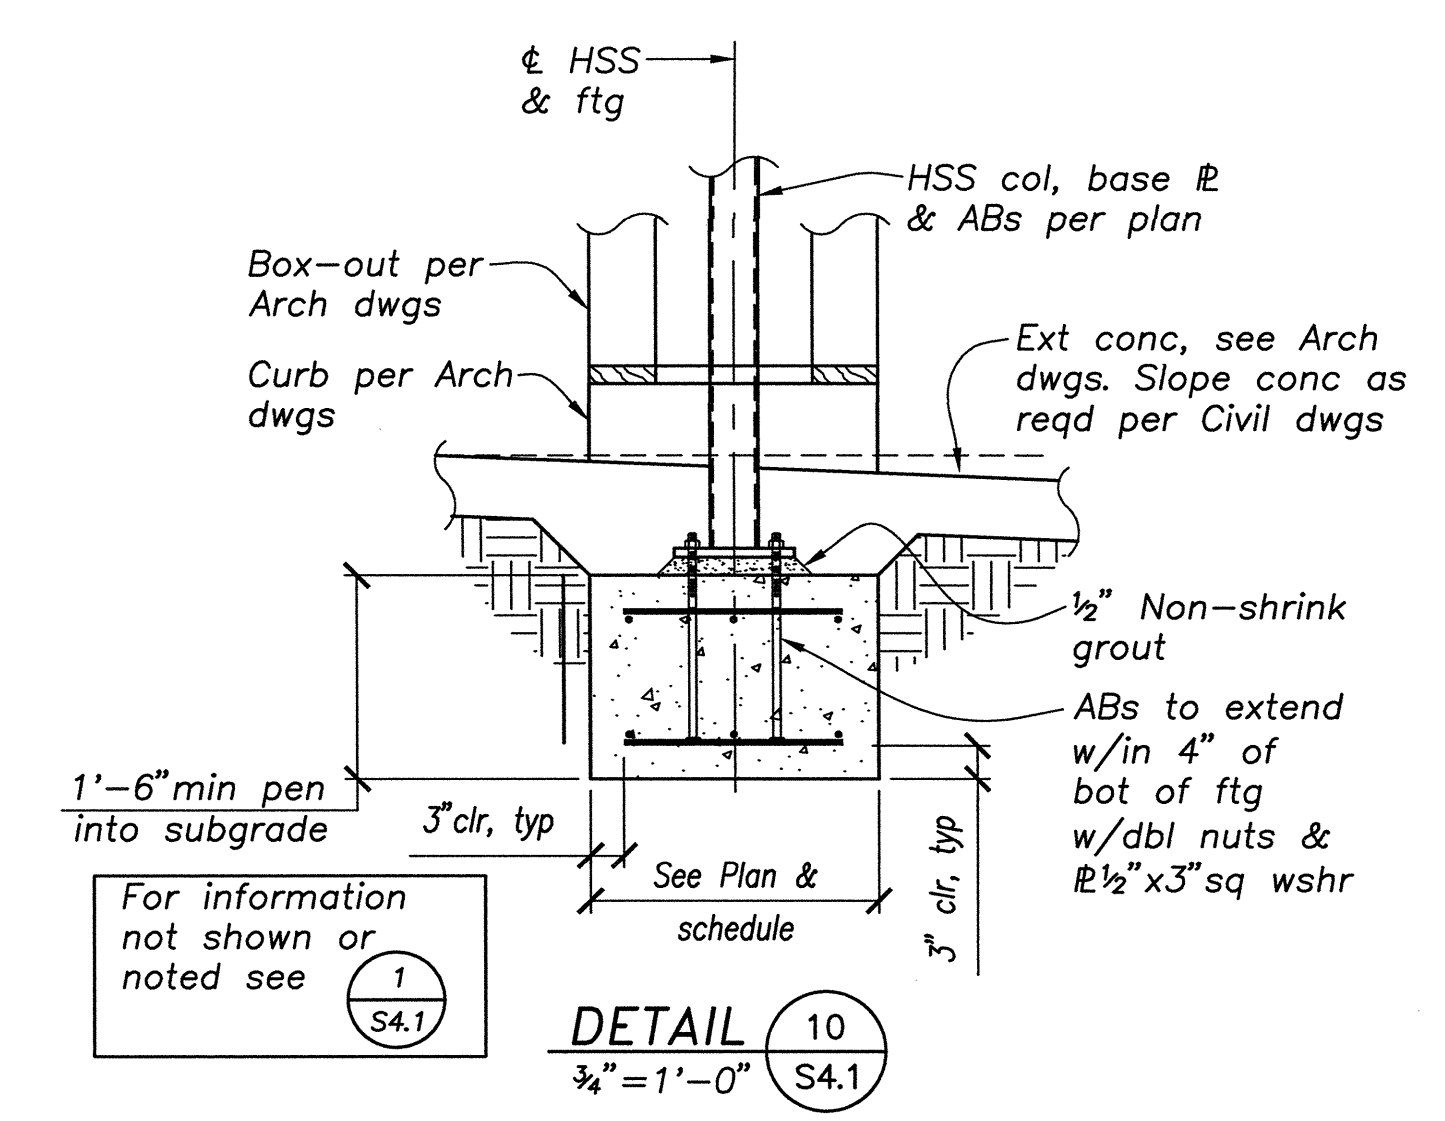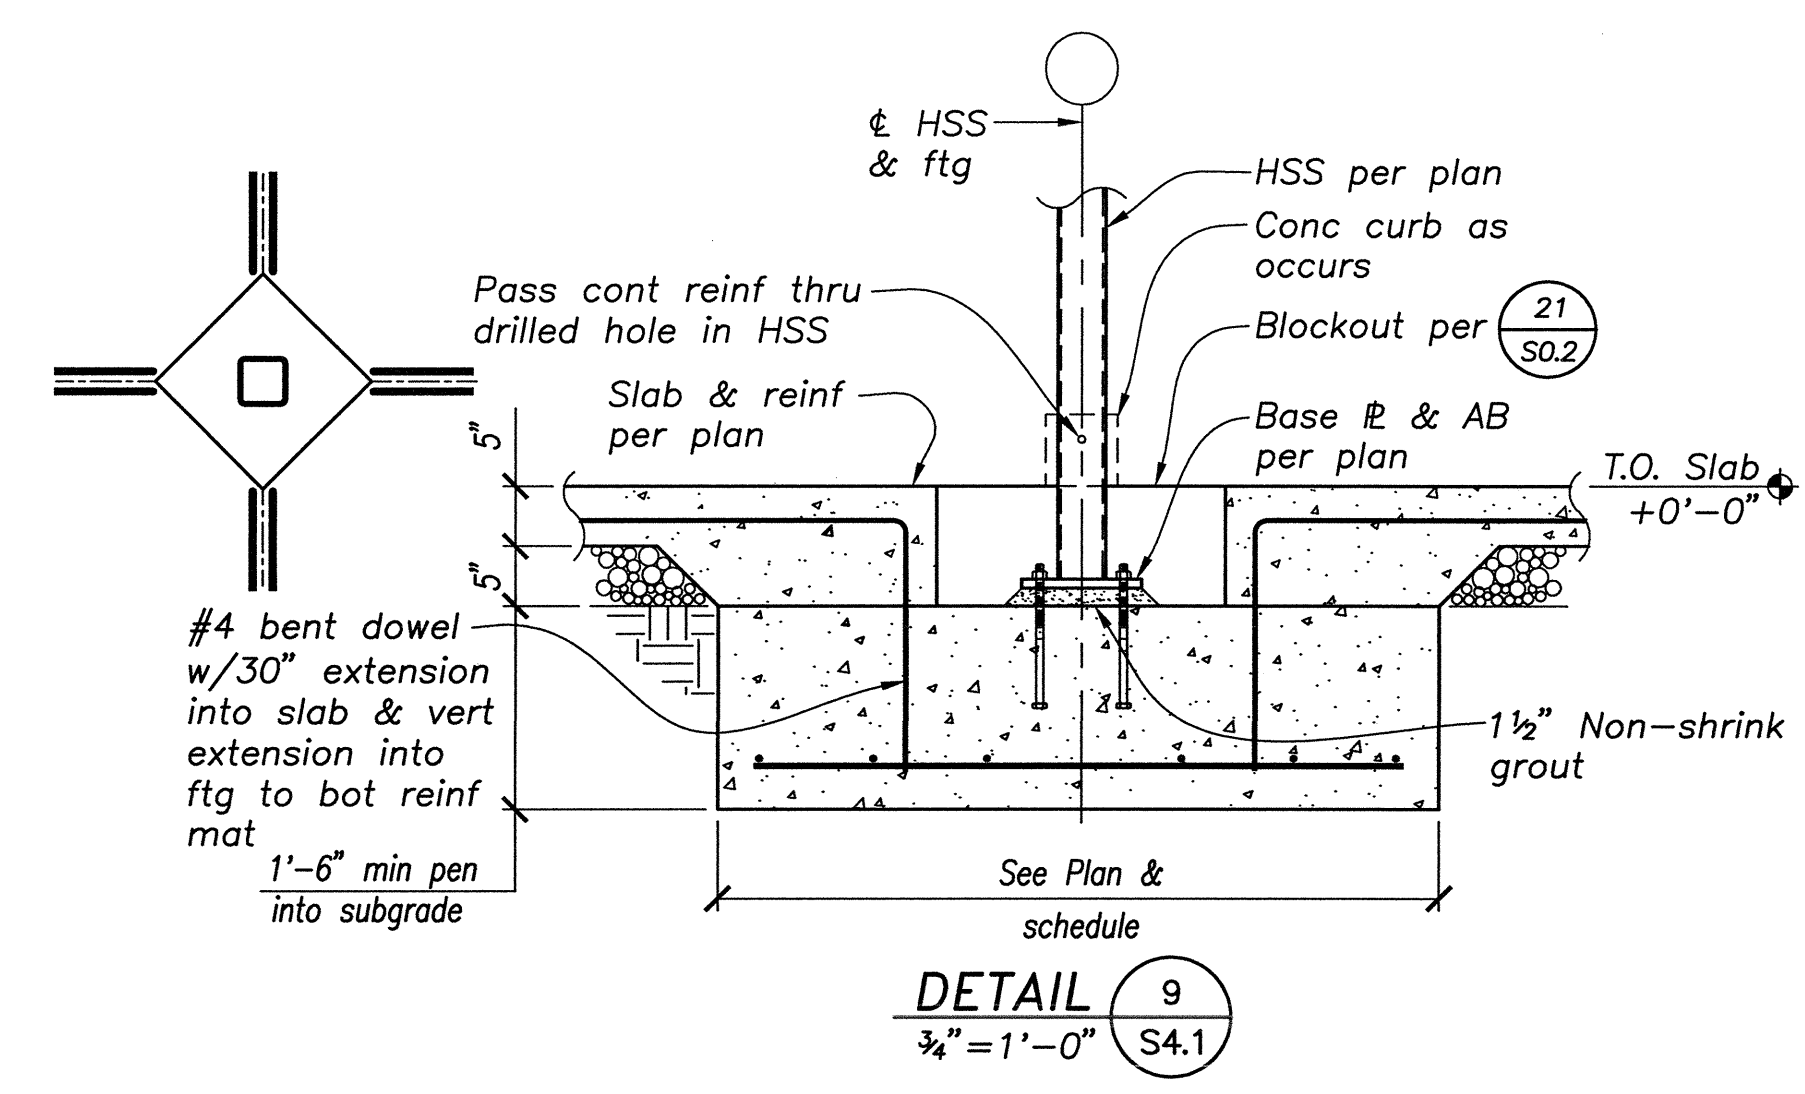

Dry Creek Joint Elementary School District District Education Center

8849 Cook Riolo Road, Roseville, CA 95747
Dry Creek Joint Elementary School District

FILE NO. 31-15
IDENTIFICATION STAMP DIV. OF THE
STATE ARCHITECT OFFICE OF
REGULATION SERVICES
APPLICATION NO. 02-115456
AC FLS SS
DATE 2/23/17

DIVISION OF THE STATE ARCHITECT
revision date: by:

www.barrish.com
barrish pelham
Consulting Engineers
Sacramento, Walnut Creek, Tahoe/Reno
CONSULTANT

nacht&lewis
600 G Street, Suite 100
Sacramento, CA 95811
www.nachtandlewis.com
916.329.4000

RENEWAL DATE: 1/31/19
DATE OF CALIFORNIA

INITIAL BOX			
NO.	DWG BY	DATE	REVIEWED


REVISIONS		
NO.	DESCRIPTION	DATE

DATE February 23, 2017
JOB NO. Y1538.00
SHEET TITLE


Foundation Details

SHEET NO.
S4.1


ONE AND ONE-HALF INCH = ONE FOOT
THREE-QUARTERS INCH = ONE FOOT
ONE-HALF INCH = ONE FOOT
ONE-QUARTER INCH = ONE FOOT
ONE-EIGHTH INCH = ONE FOOT
ONE-SIXTEENTH INCH = ONE FOOT
ONE INCH = TWENTY FEET

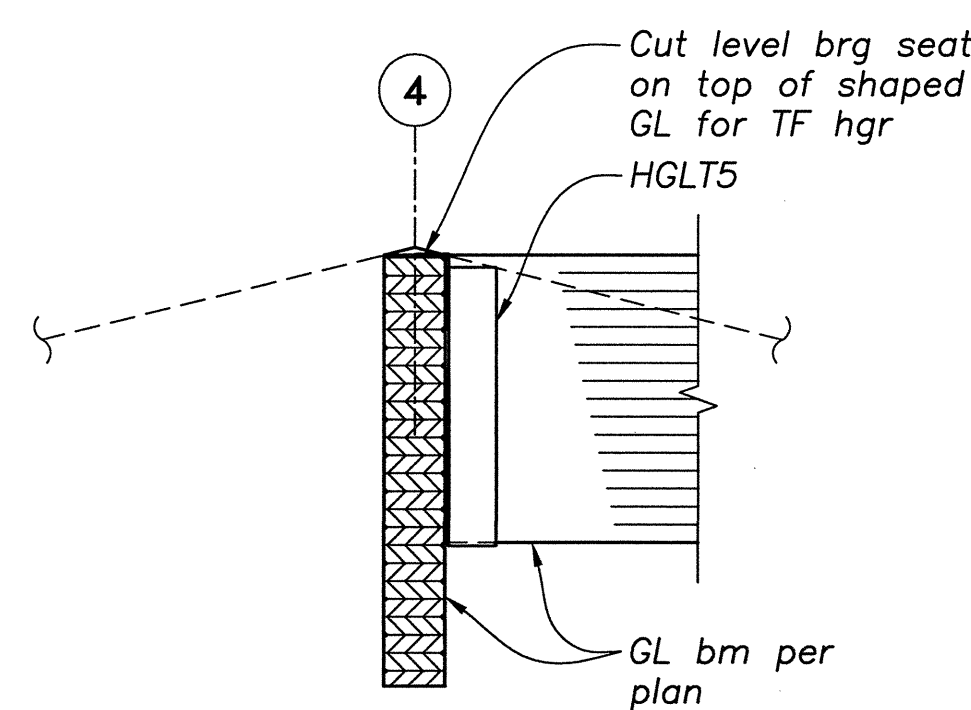


DETAIL 13
3/4"=1'-0" S4.2

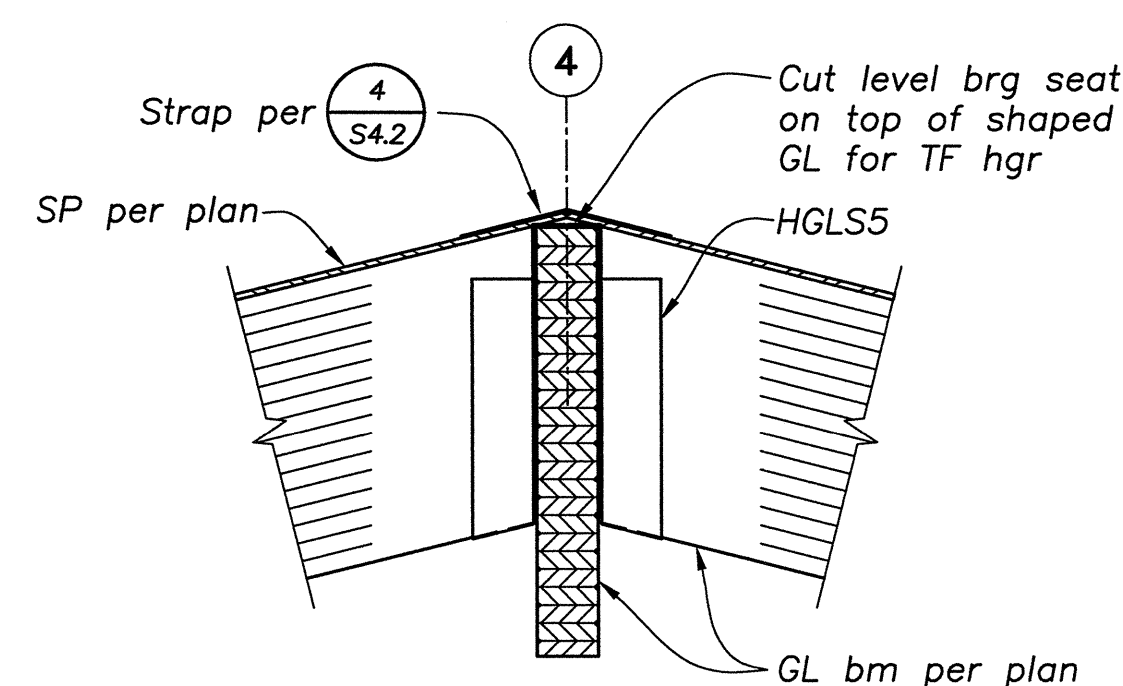


DETAIL 14
3/4"=1'-0" S4.2

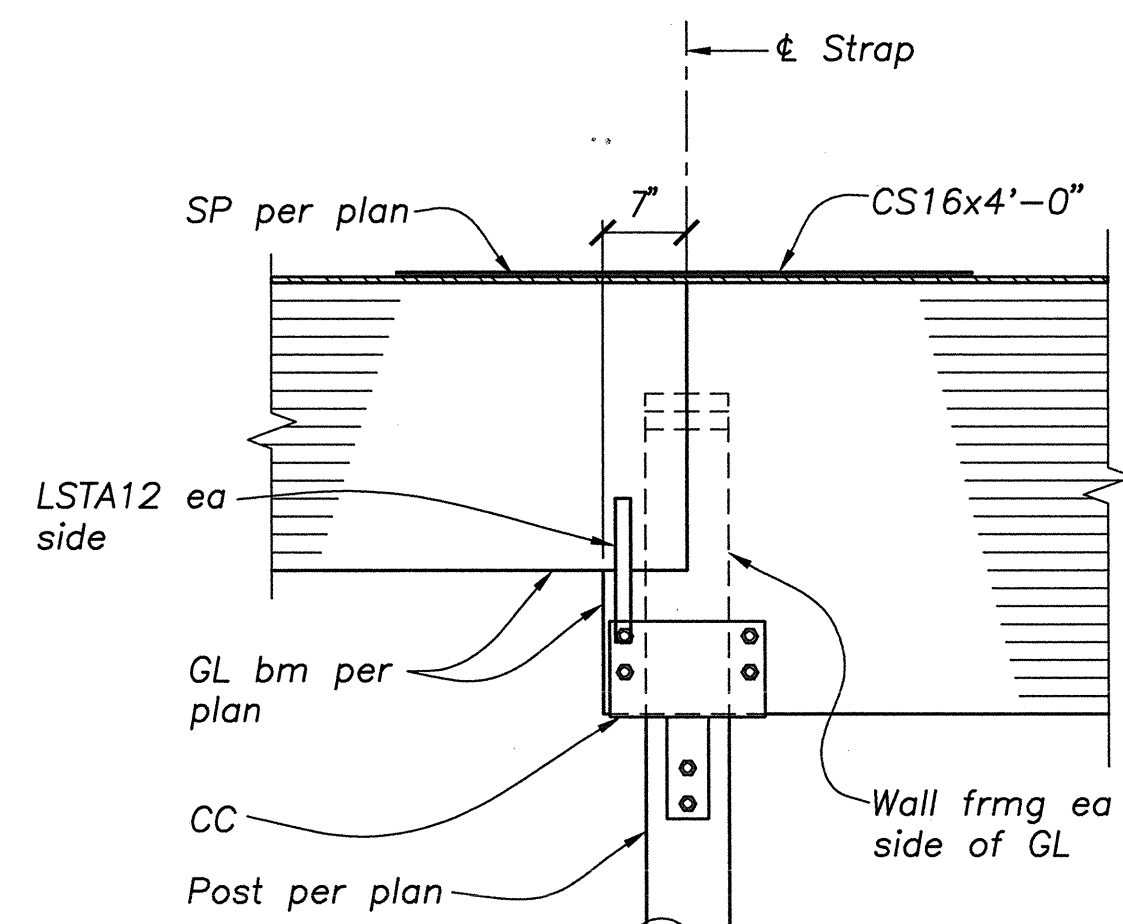


DETAIL 15
3/4"=1'-0" S4.2

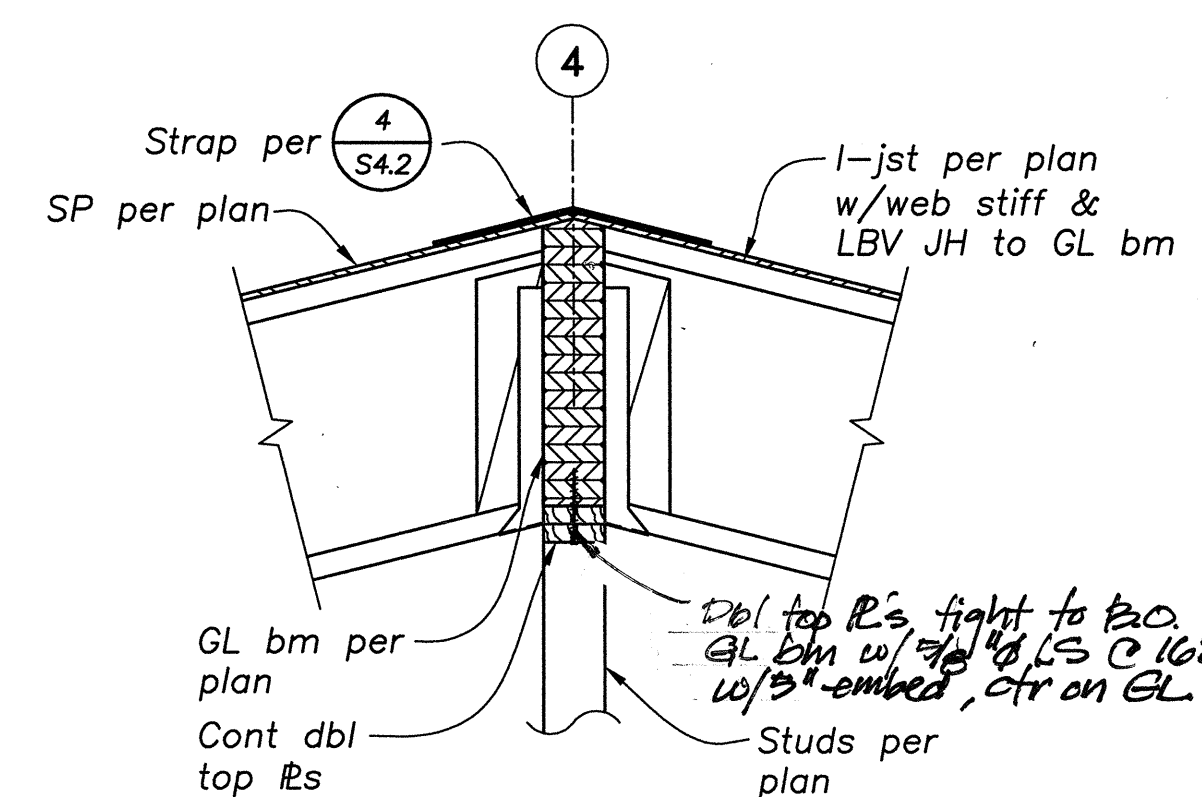


DETAIL 16
3/4"=1'-0" S4.2

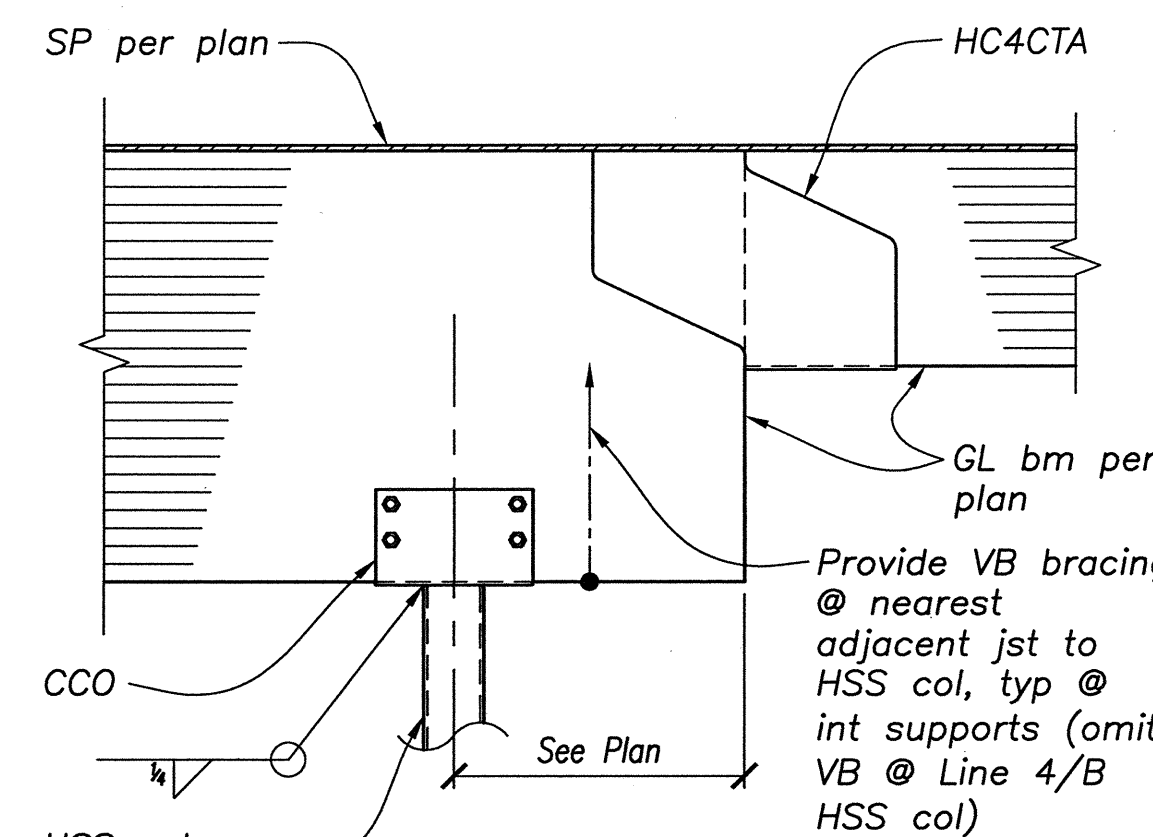


DETAIL 9
3/4"=1'-0" S4.2

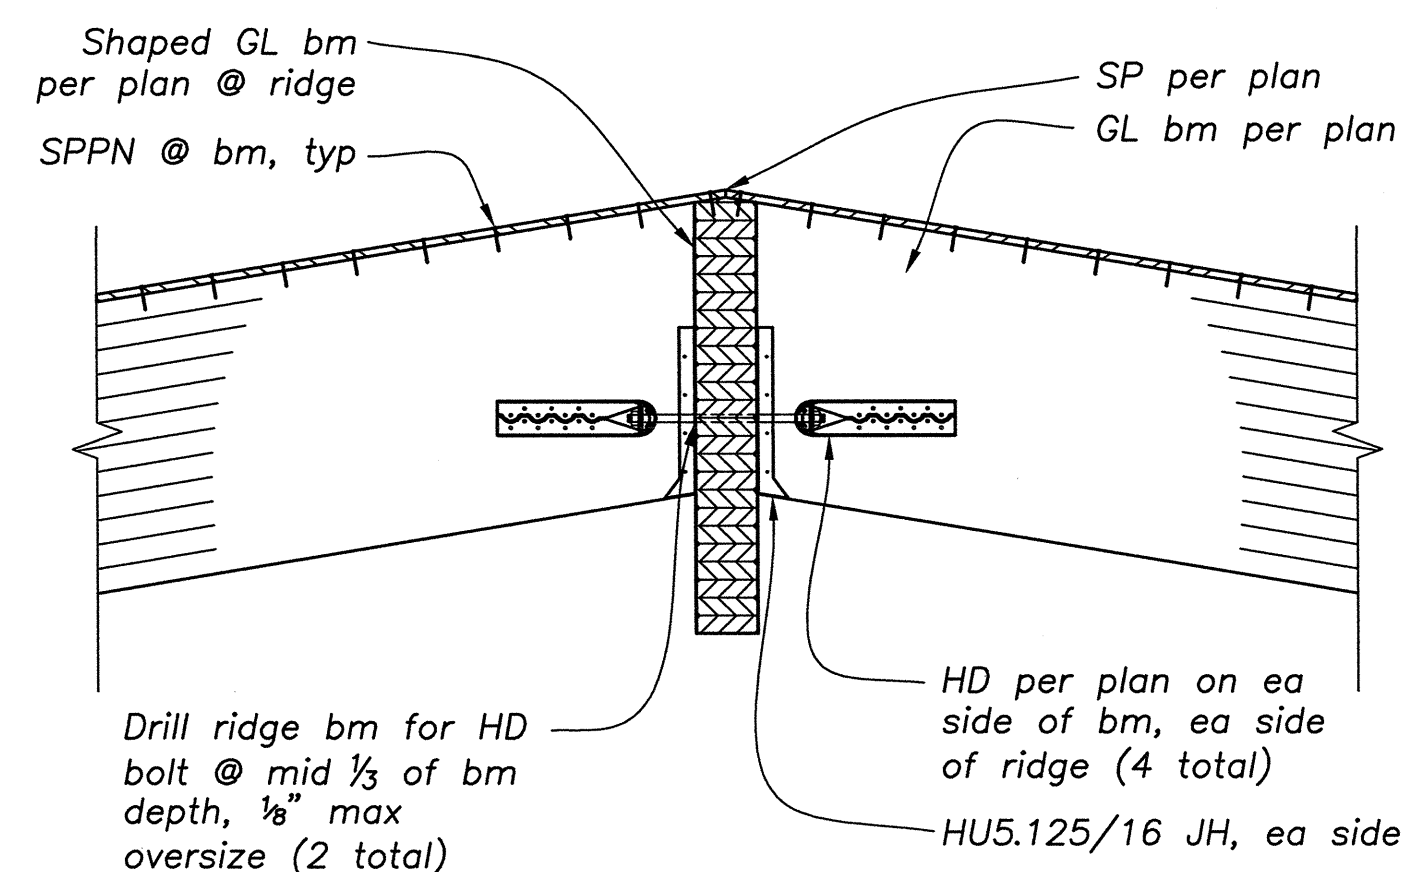


DETAIL 10
3/4"=1'-0" S4.2

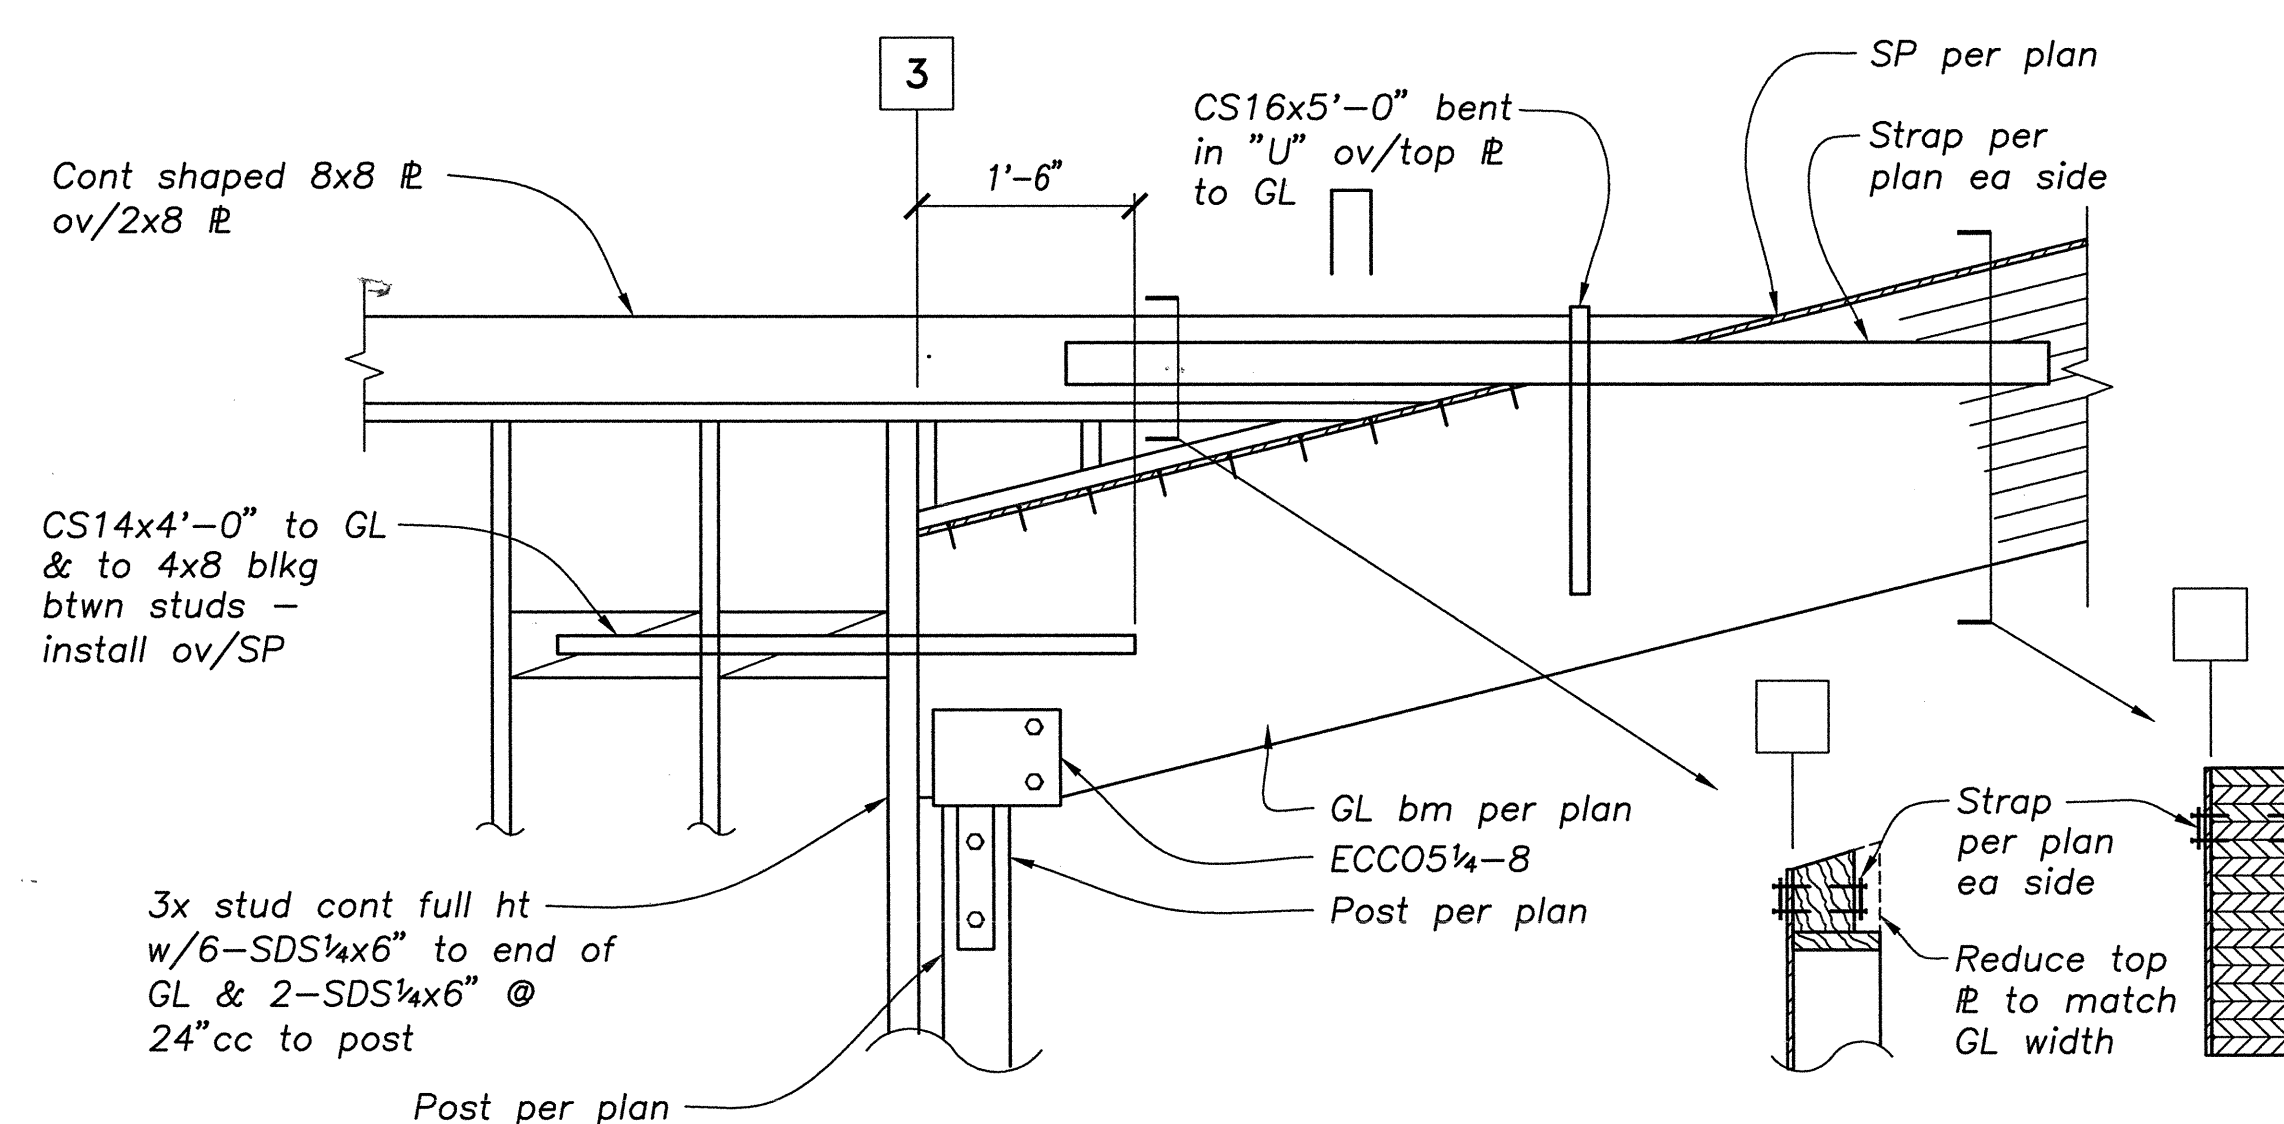


DETAIL 11
3/4"=1'-0" S4.2

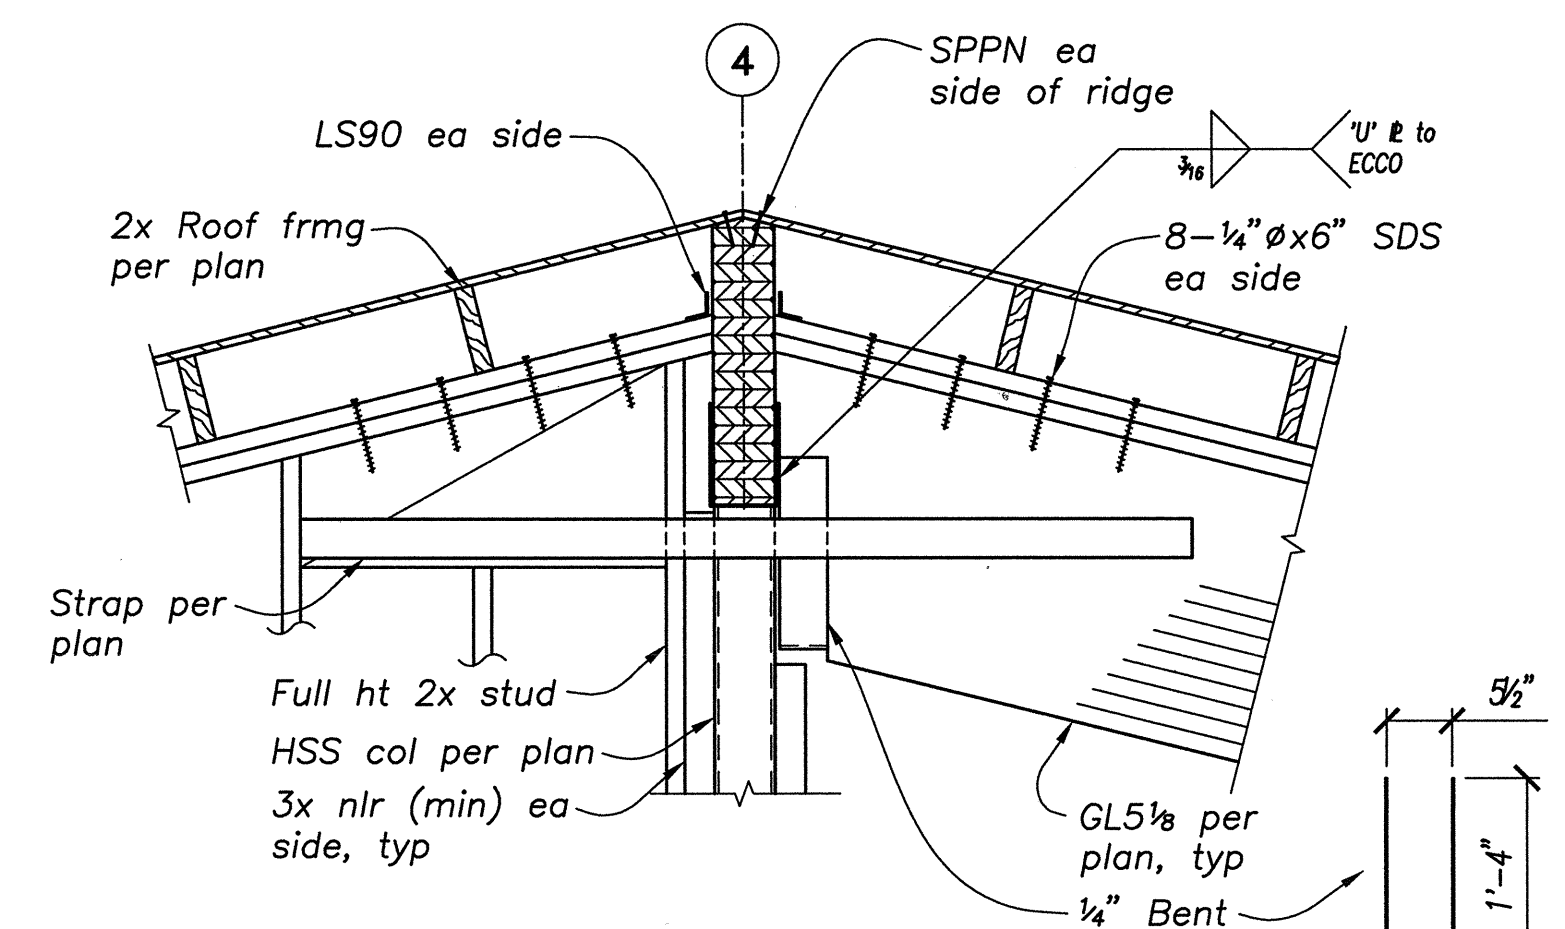


DETAIL 12
3/4"=1'-0" S4.2

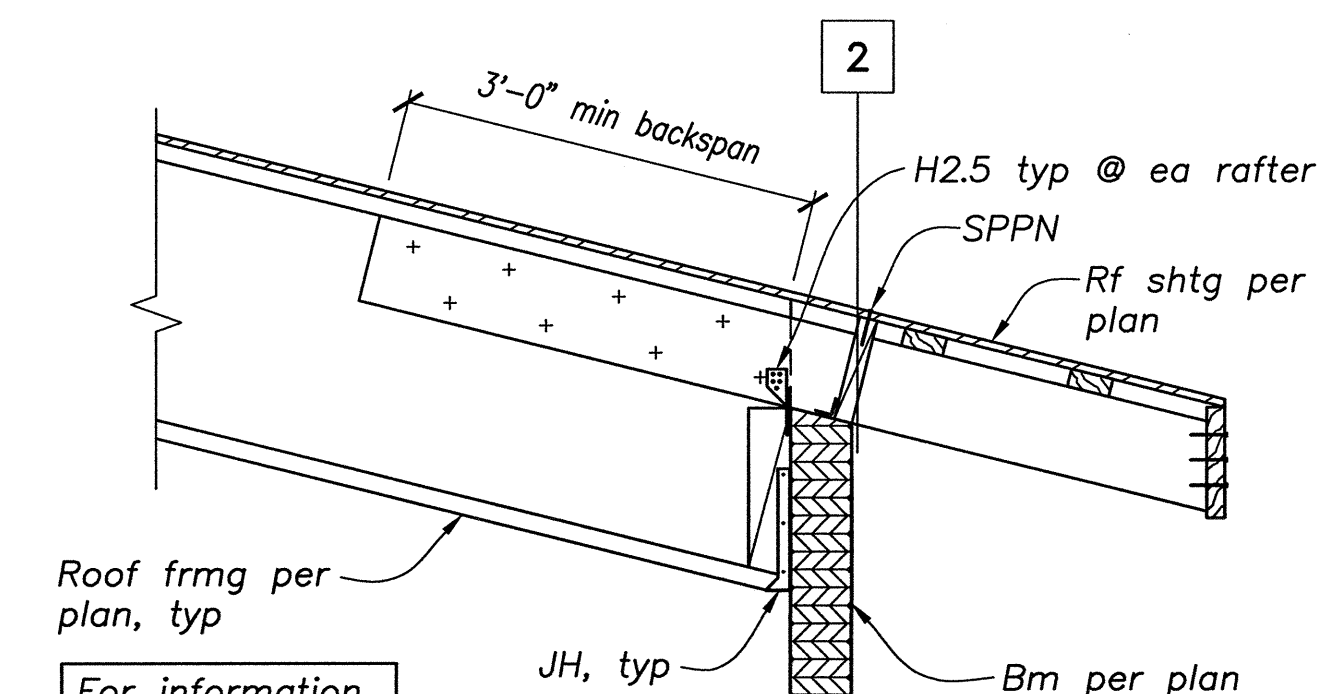


DETAIL 5
3/4"=1'-0" S4.2

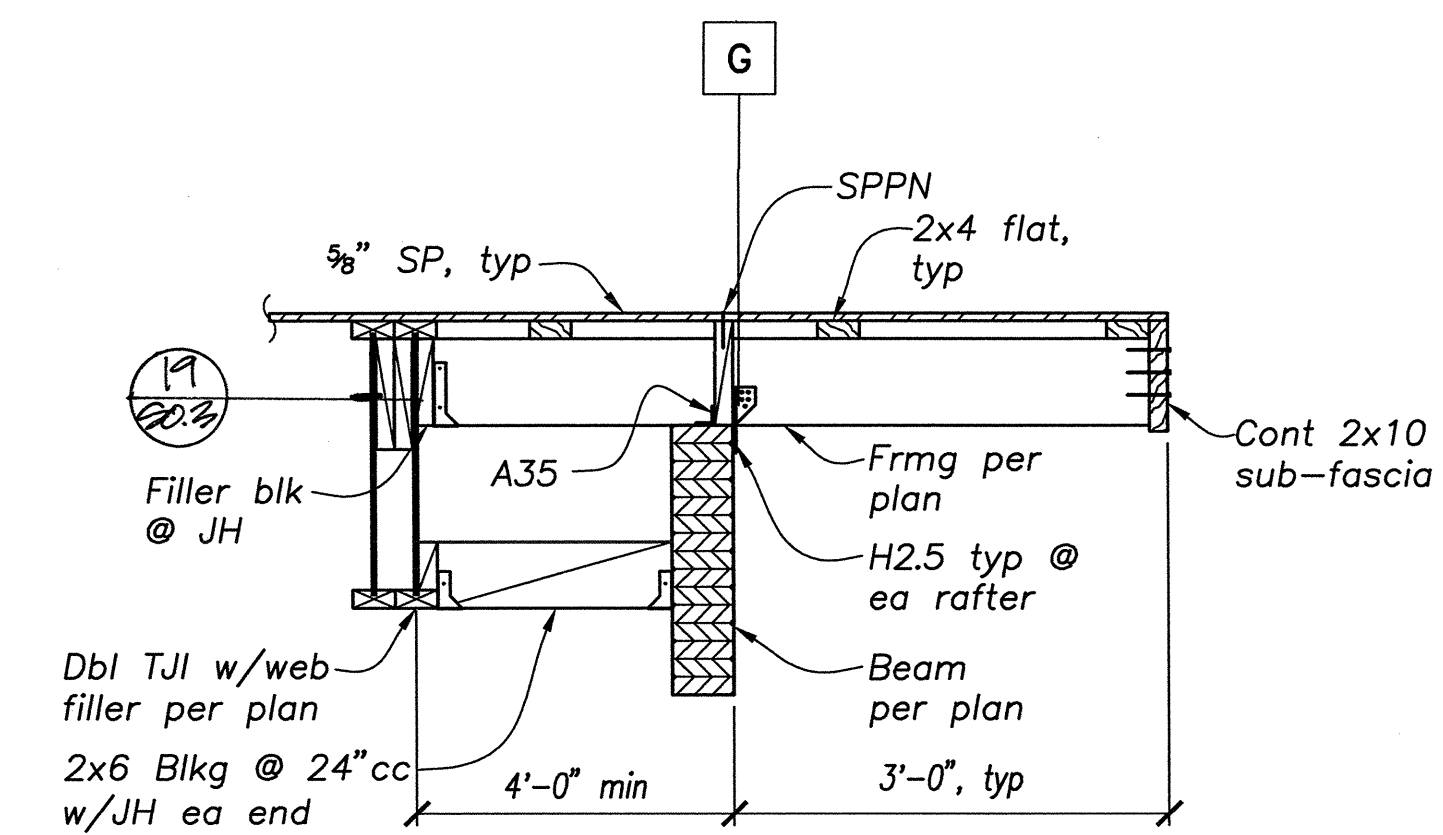


DETAIL 6
3/4"=1'-0" S4.2

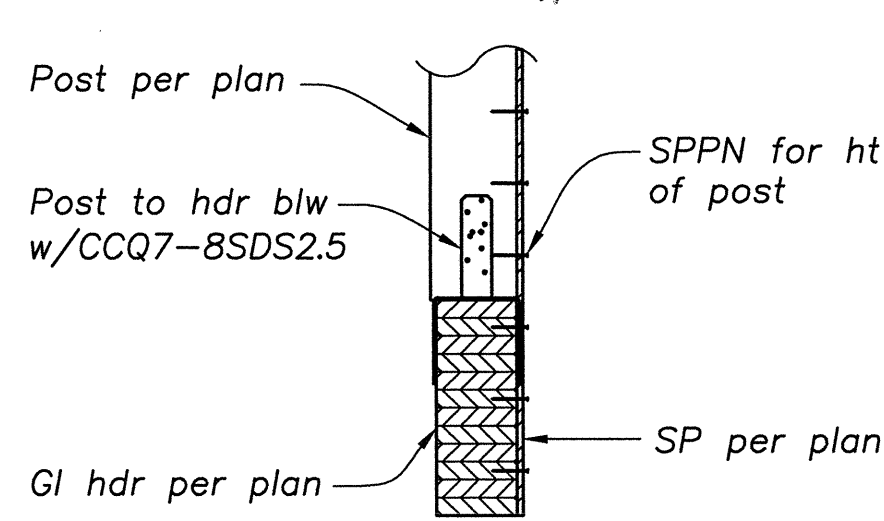


DETAIL 7
3/4"=1'-0" S4.2

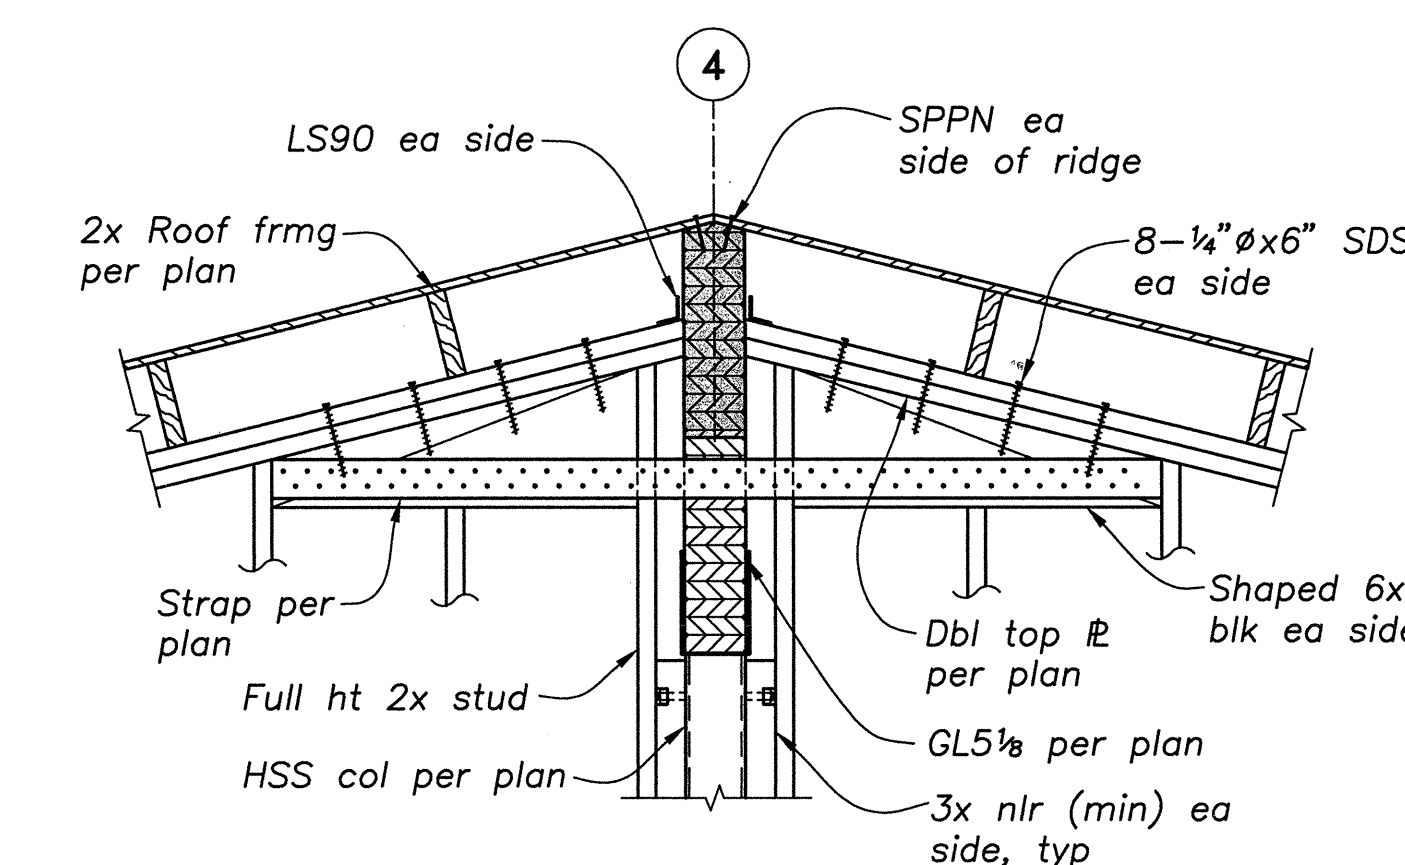


DETAIL 8
3/4"=1'-0" S4.2

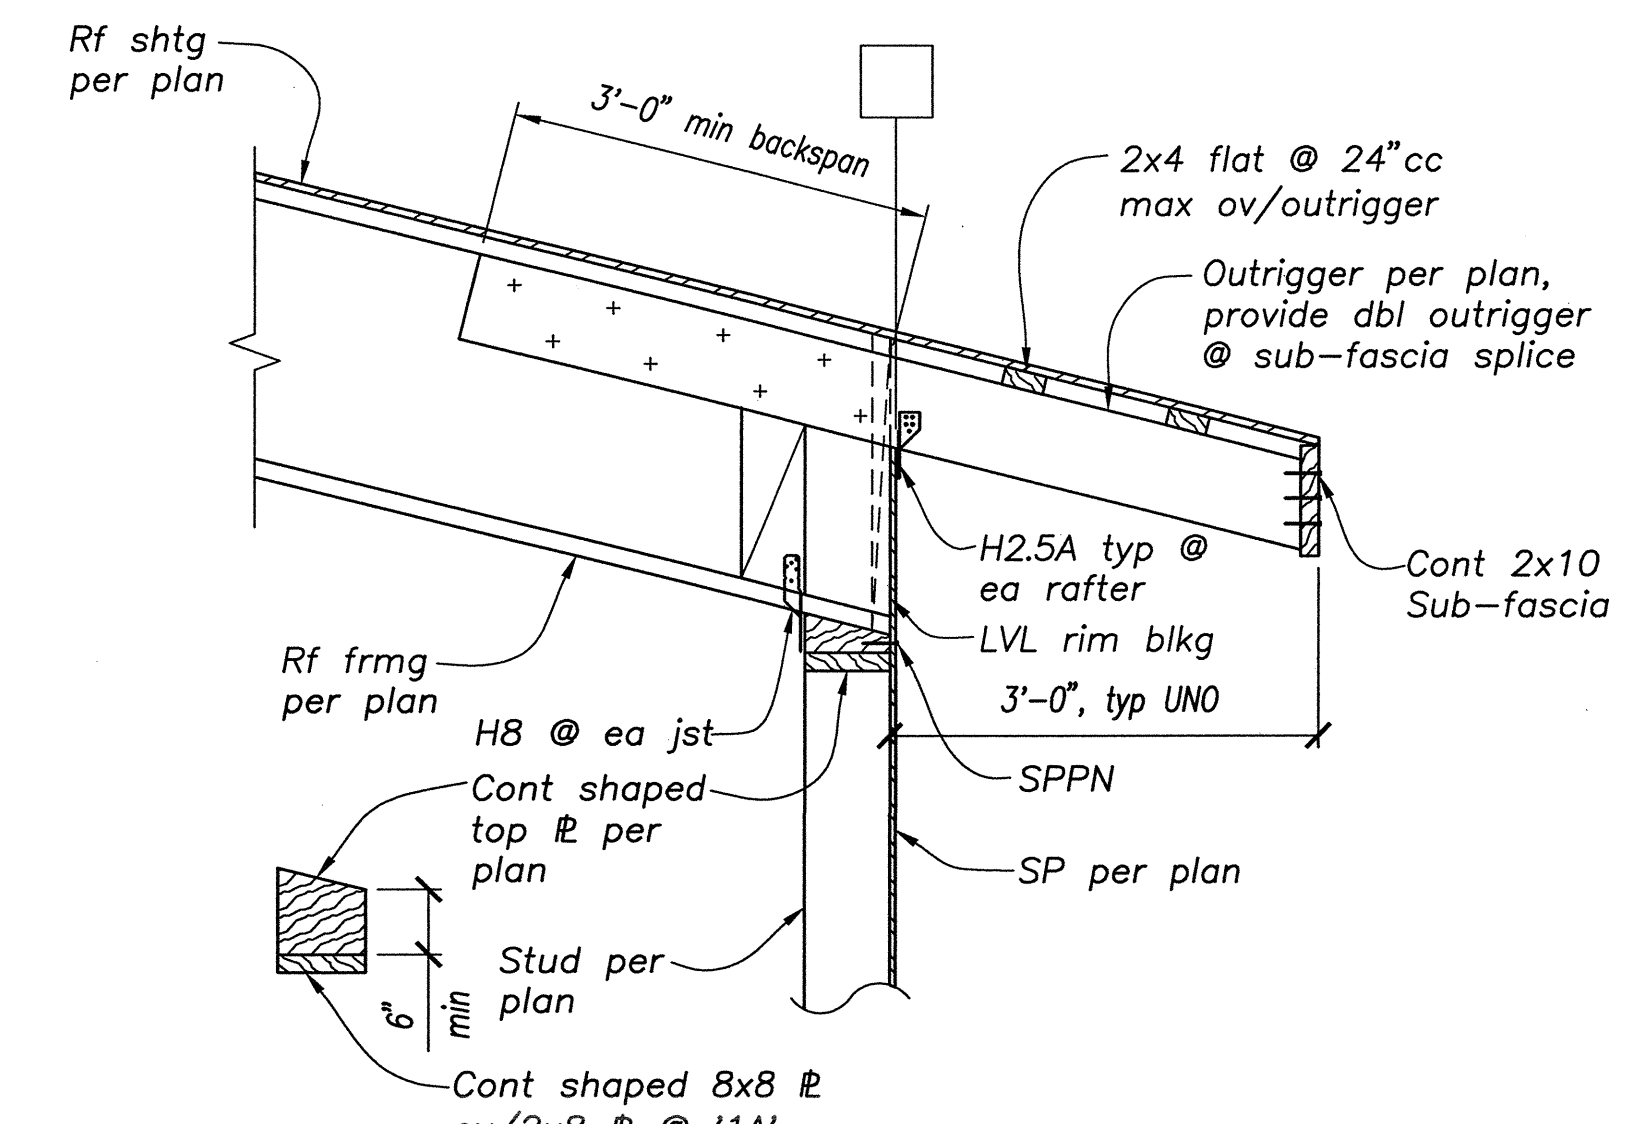


DETAIL 1
3/4"=1'-0" S4.2

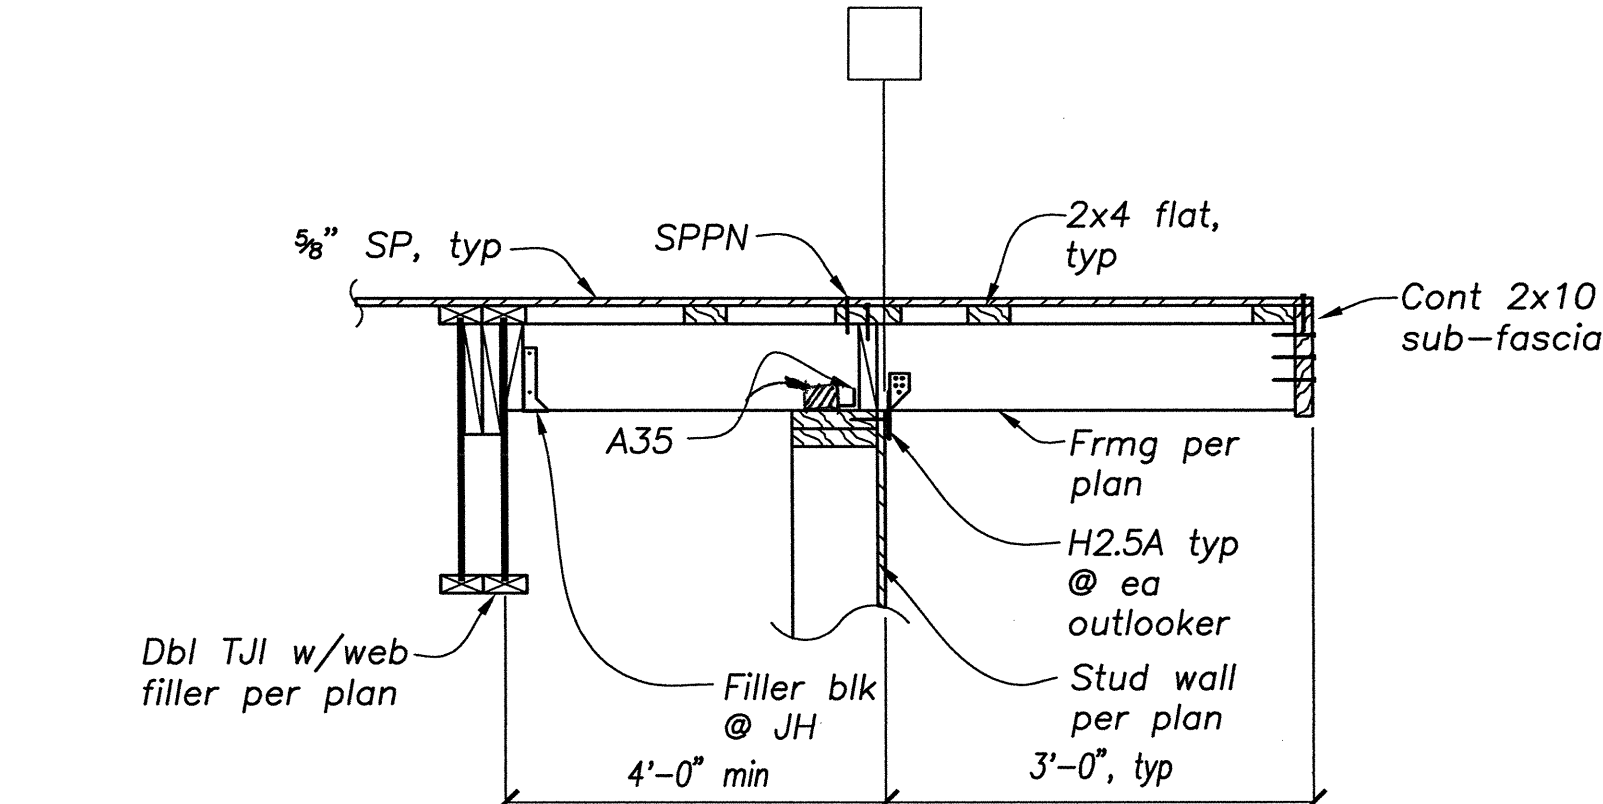

DETAIL 2
3/4"=1'-0" S4.2

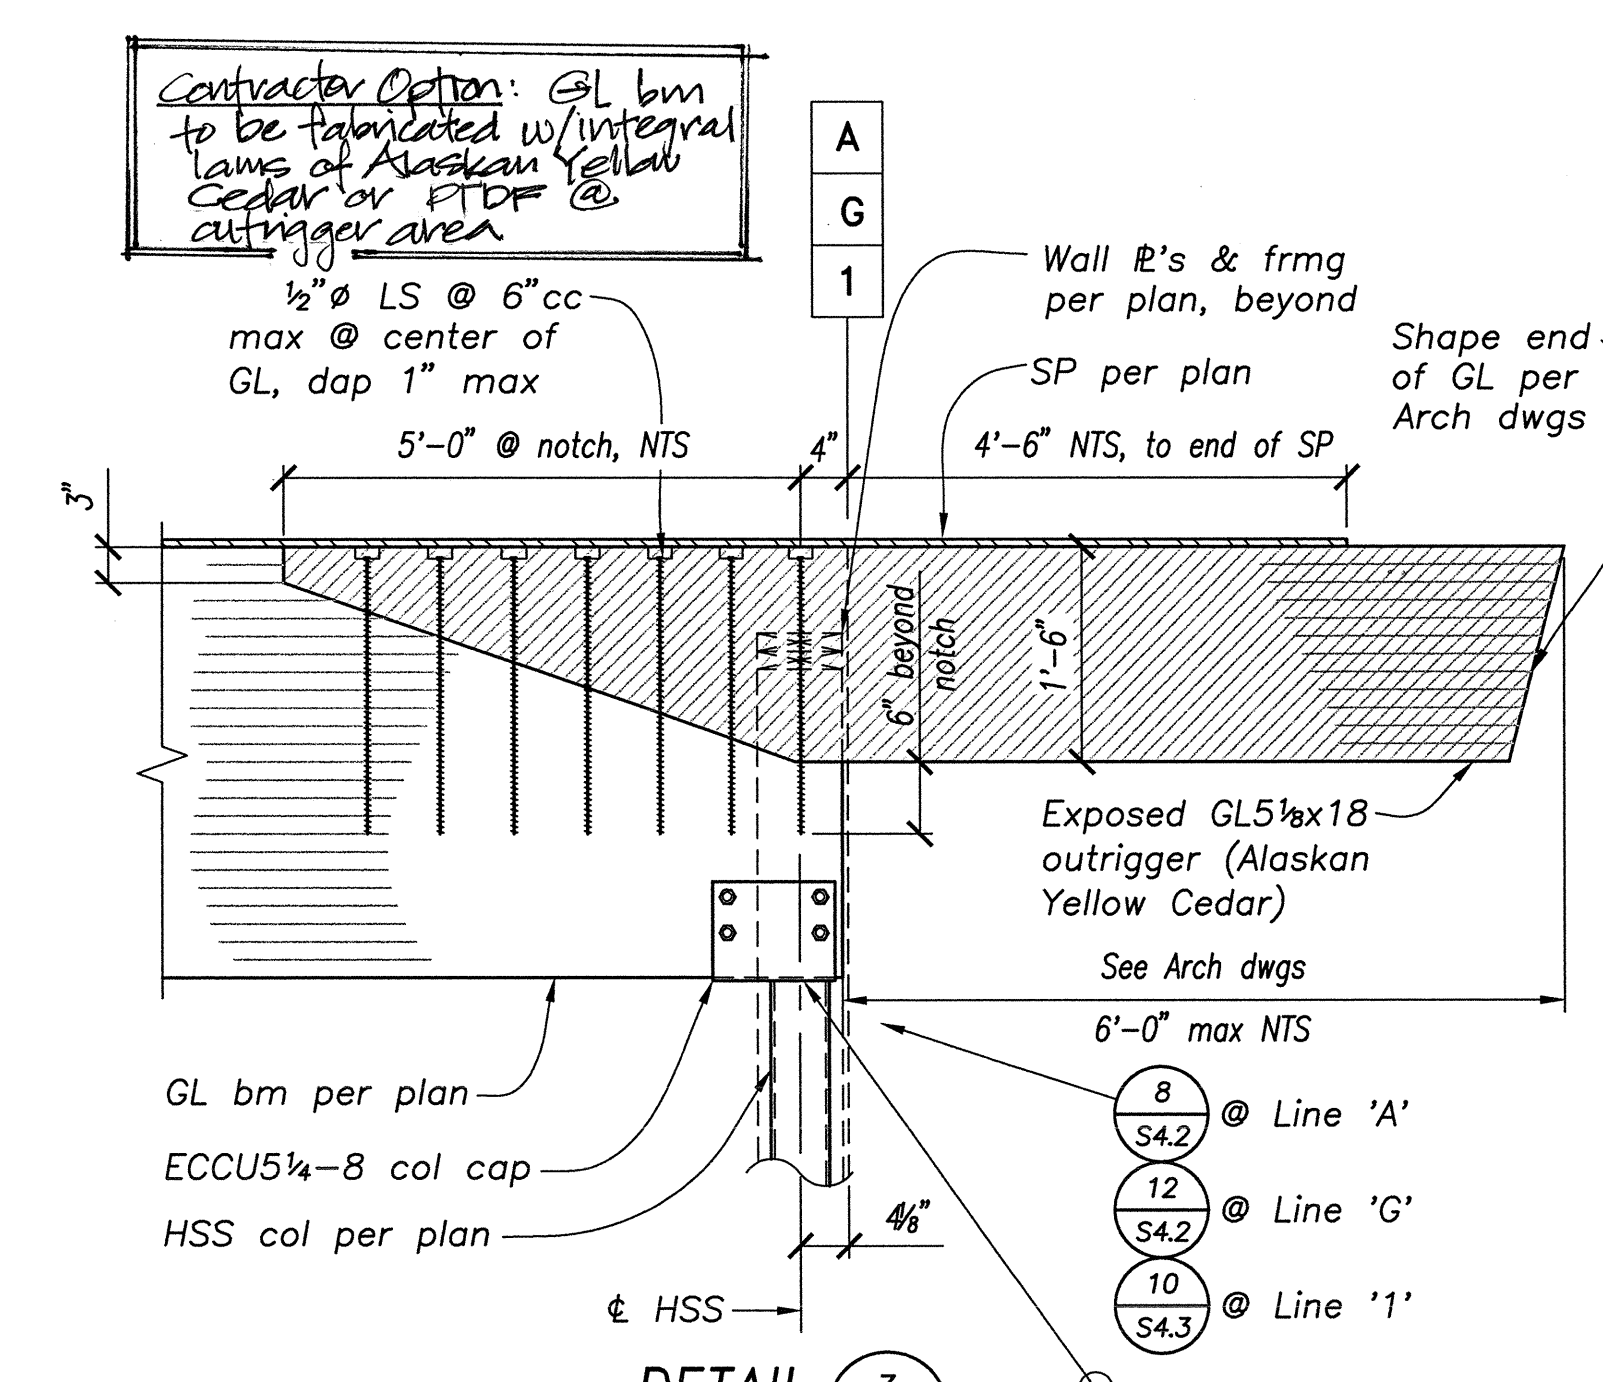

DETAIL 3
3/4"=1'-0" S4.2

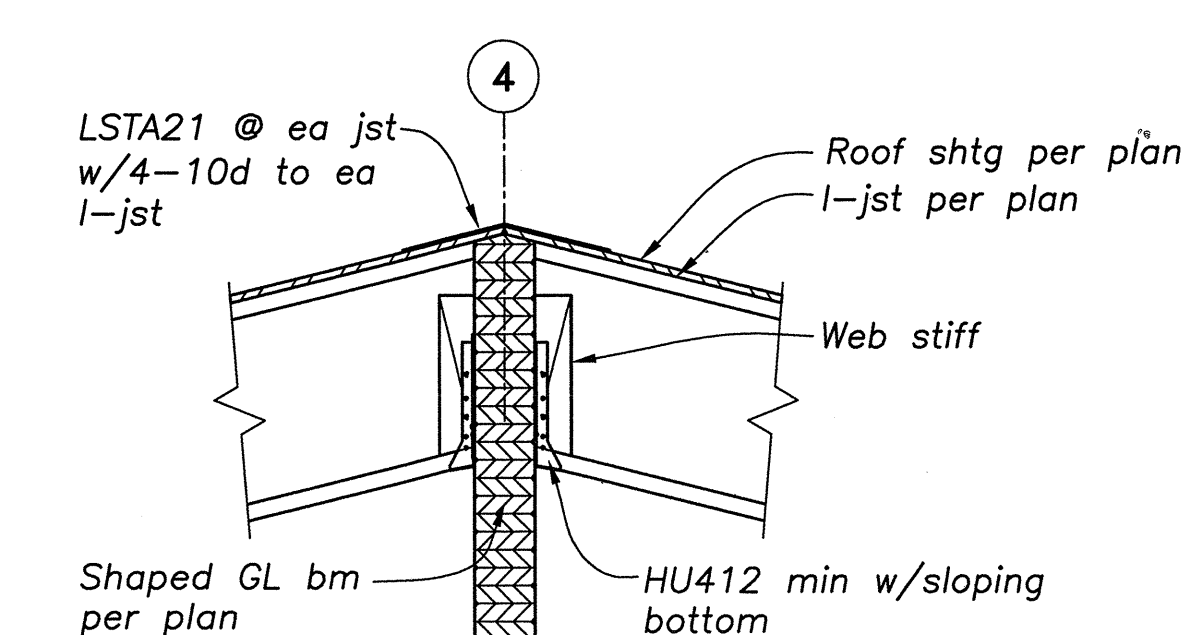

DETAIL 4
3/4"=1'-0" S4.2

Dry Creek Joint Elementary School District District Education Center

8849 Cook Riolo Road, Roseville, CA 95747


Dry Creek Joint Elementary School District

FILE NO. 31-15
IDENTIFICATION STAMP DIV. OF THE
STATE ARCHITECT OFFICE OF
REGULATION SERVICES
APPLICATION NO.
02-115456
AC FLS SS
DATE 2/22/19 CEA

DIVISION OF THE STATE ARCHITECT
revision date: by:

www.barrish.com


barrish pelham
Consulting Engineers
Sacramento-Walnut Creek-Tahoe/Reno

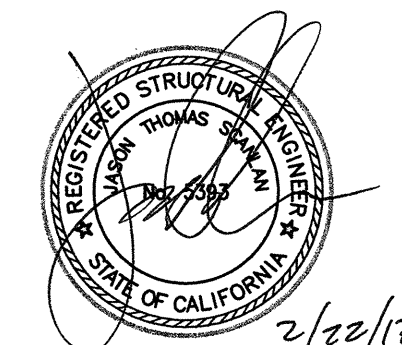

CONSULTANT

nacht&lewis

600 G Street, Suite 100
Sacramento, CA 95811
www.nachtandlewis.com
916.329.4000

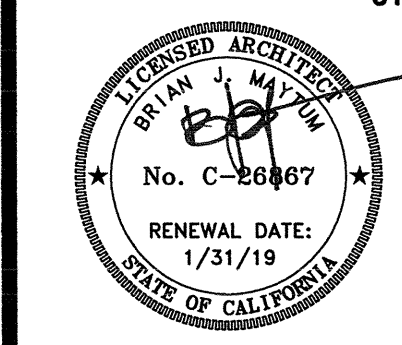

ARCHITECT

INITIAL BOX

NO.	DWG BY	DATE	REVIEWED

REVISIONS

NO.	DESCRIPTION	DATE	REV
1	100% design development	7/6/16	
2	75% construction documents	9/20/16	
3	DSA Submittal	12/31/16	
4	DSA Backcheck	02/23/17	

DATE February 23, 2017

JOB NO. Y1538.00


SHEET TITLE

Roof Framing
Details


SHEET NO.

S4.2


ONE AND ONE-HALF INCH = ONE FOOT
THREE-QUARTERS INCH = ONE FOOT
ONE-HALF INCH = ONE FOOT
ONE-QUARTER INCH = ONE FOOT
ONE-EIGHTH INCH = ONE FOOT
ONE-SIXTEENTH INCH = ONE FOOT
ONE INCH = TWENTY FEET

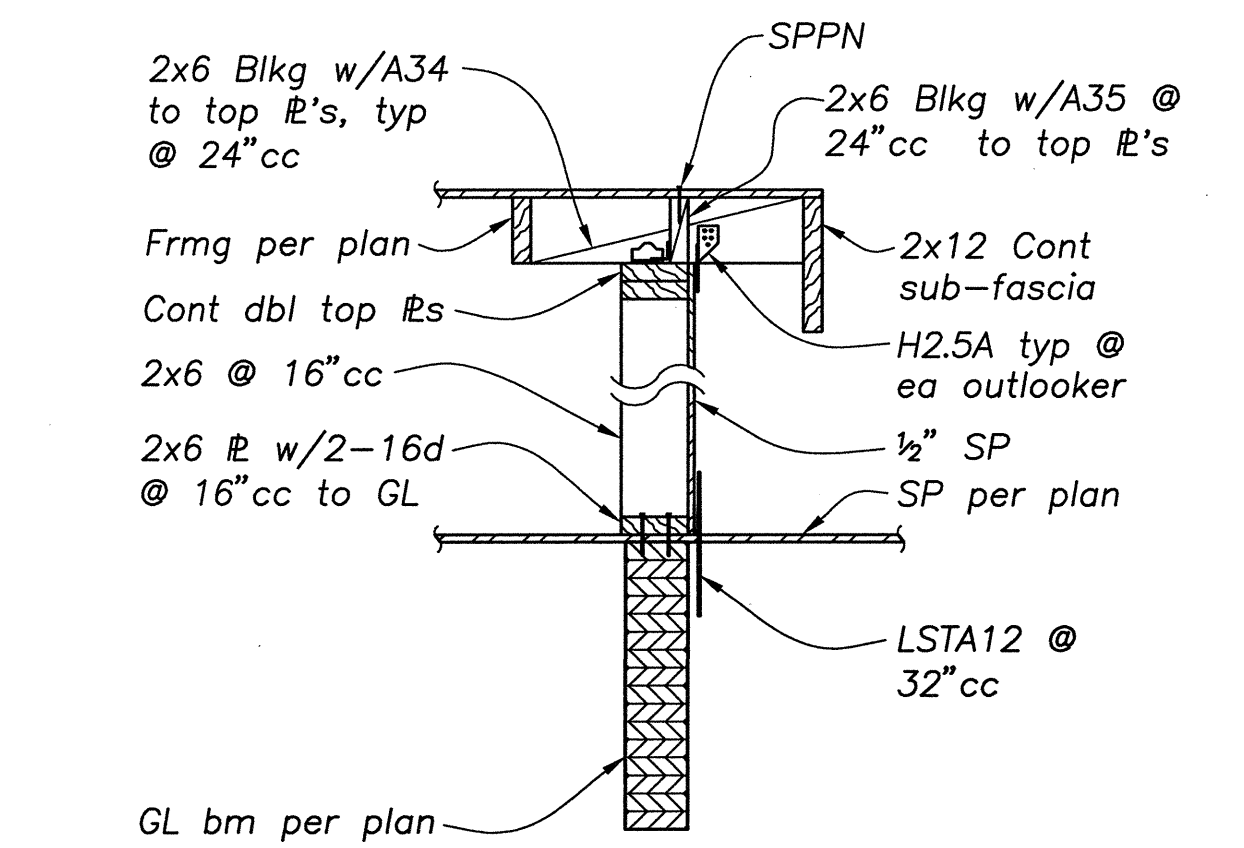


DETAIL 13
3/4" = 1'-0" S4.3

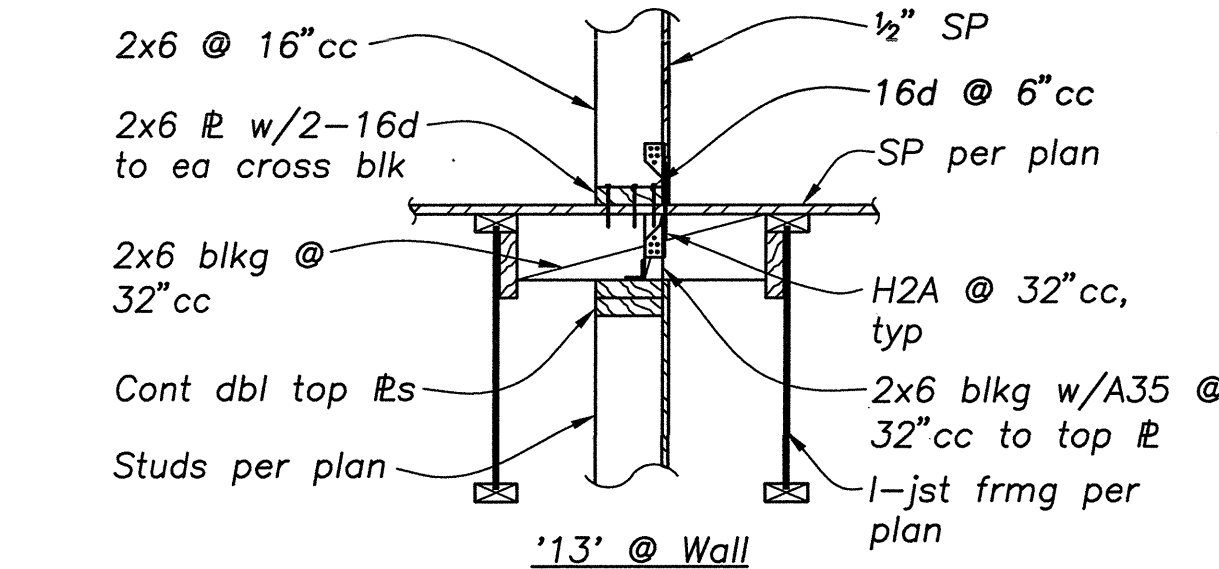


DETAIL 13A
3/4" = 1'-0" S4.3

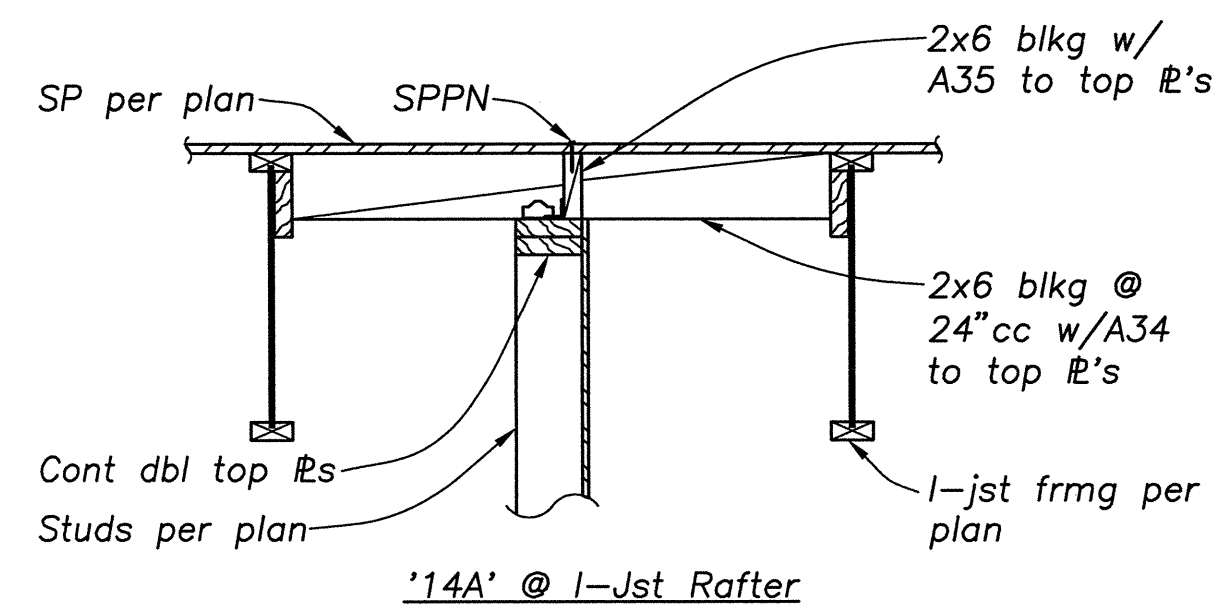


DETAIL 14
3/4" = 1'-0" S4.3

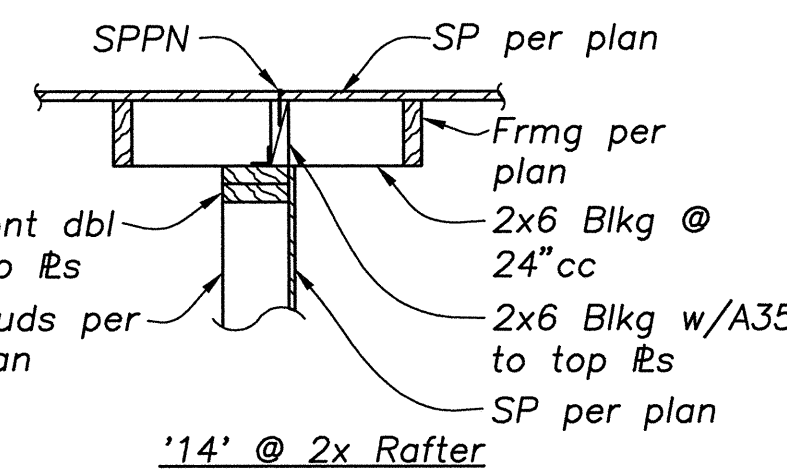


DETAIL 14A
3/4" = 1'-0" S4.3

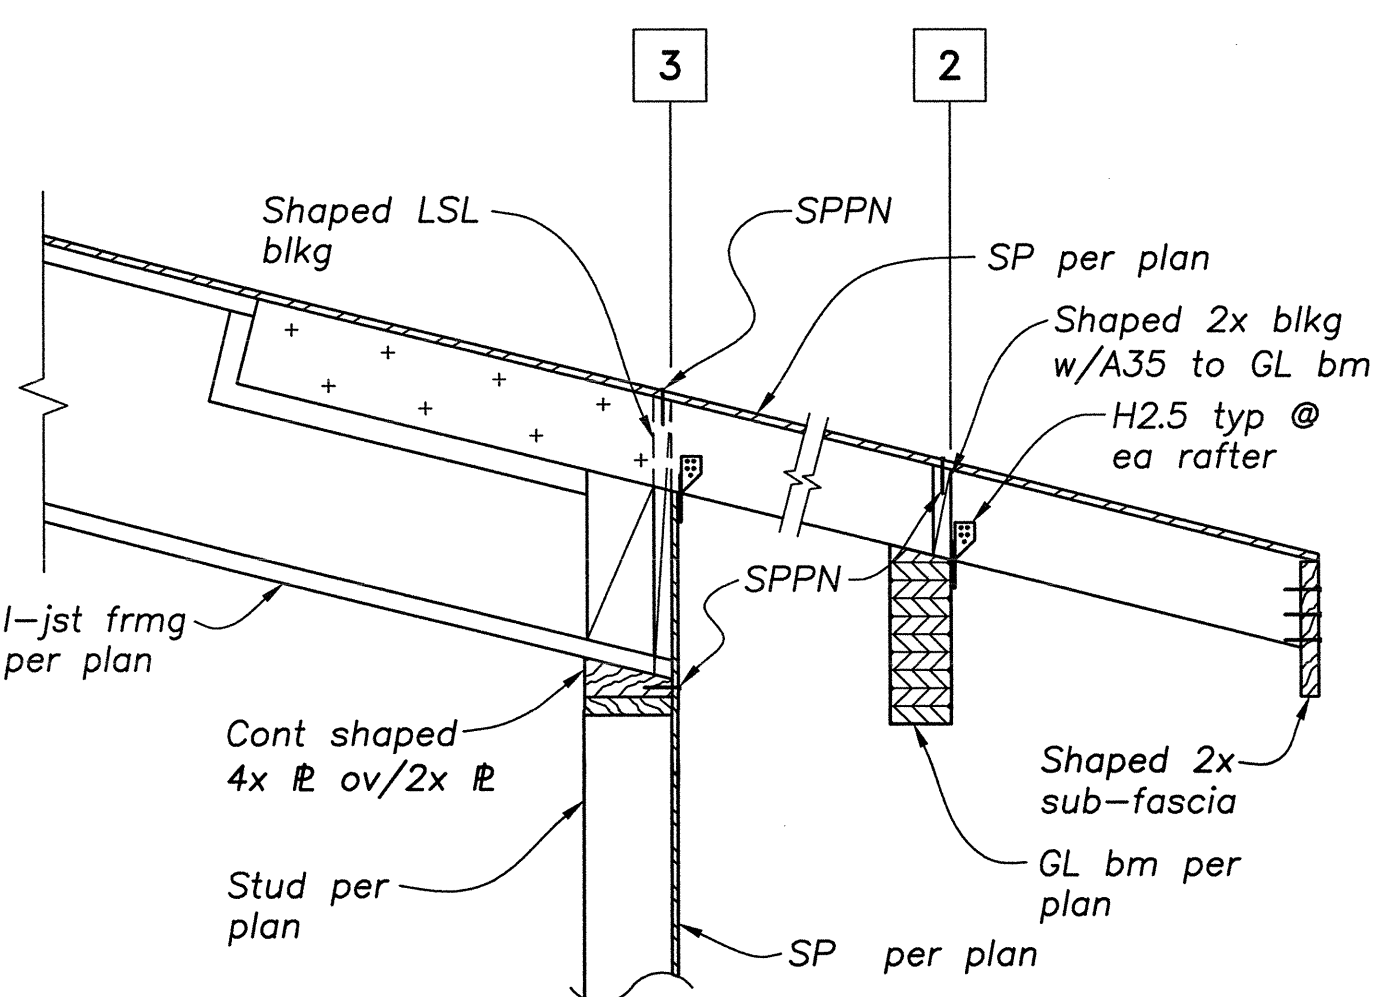


DETAIL 15
3/4" = 1'-0" S4.3

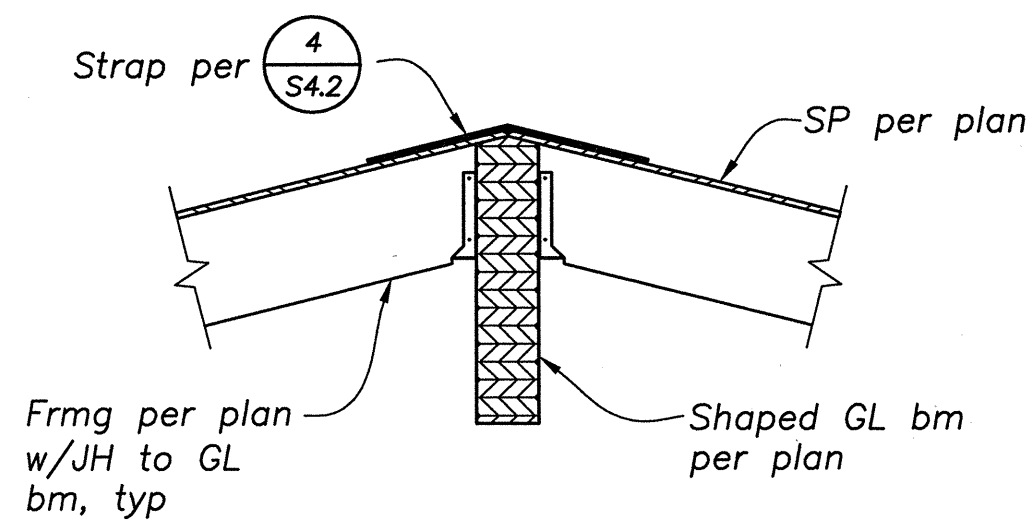


DETAIL 16
3/4" = 1'-0" S4.3

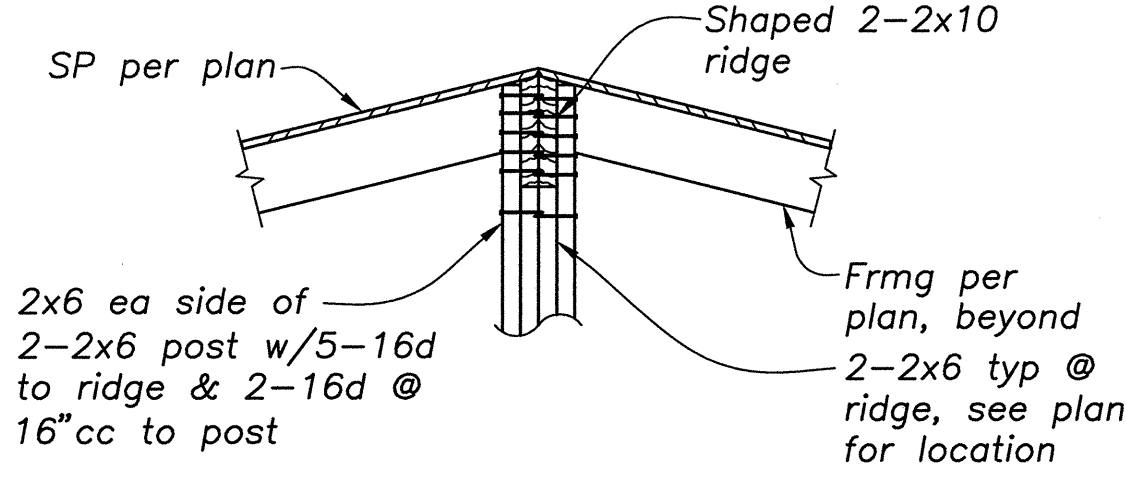


DETAIL 9
3/4" = 1'-0" S4.3

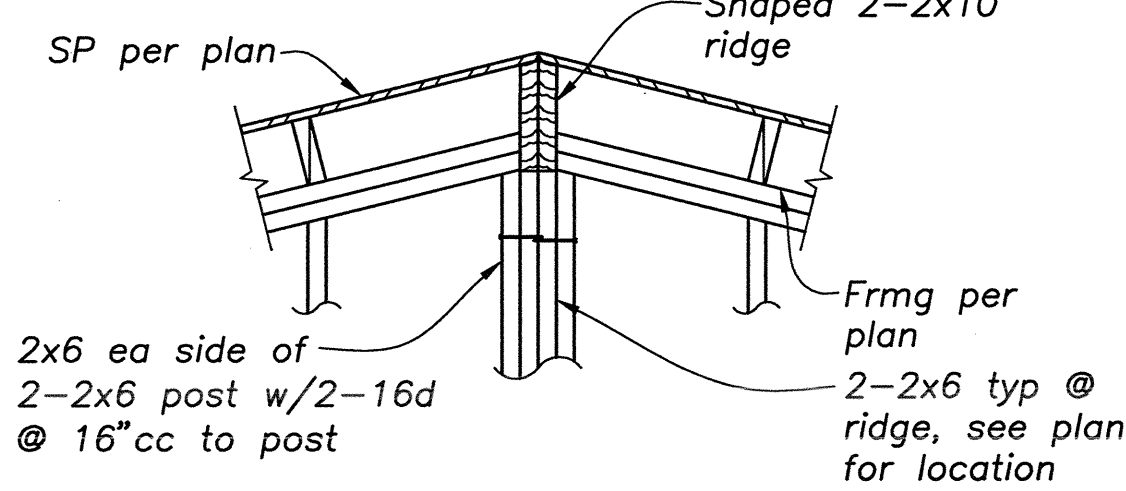


DETAIL 9A
3/4" = 1'-0" S4.3

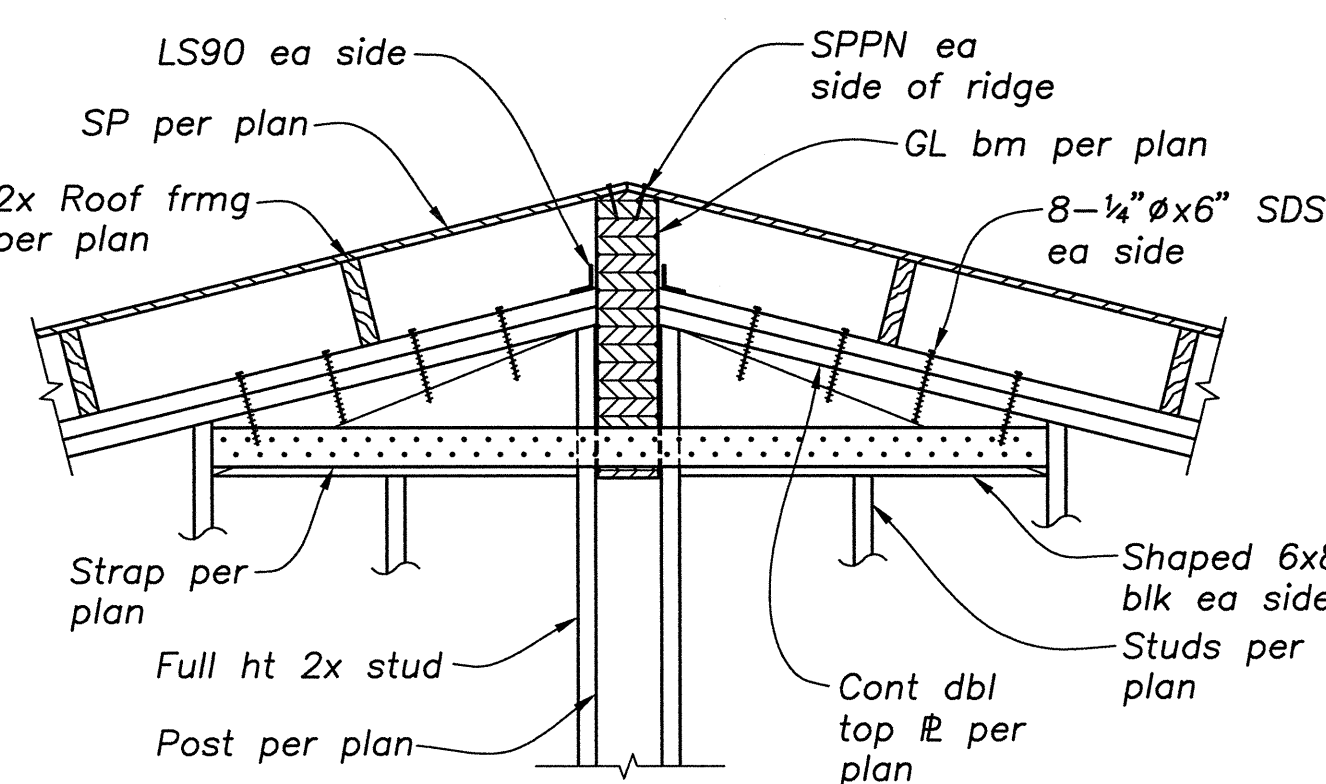


DETAIL 10
3/4" = 1'-0" S4.3

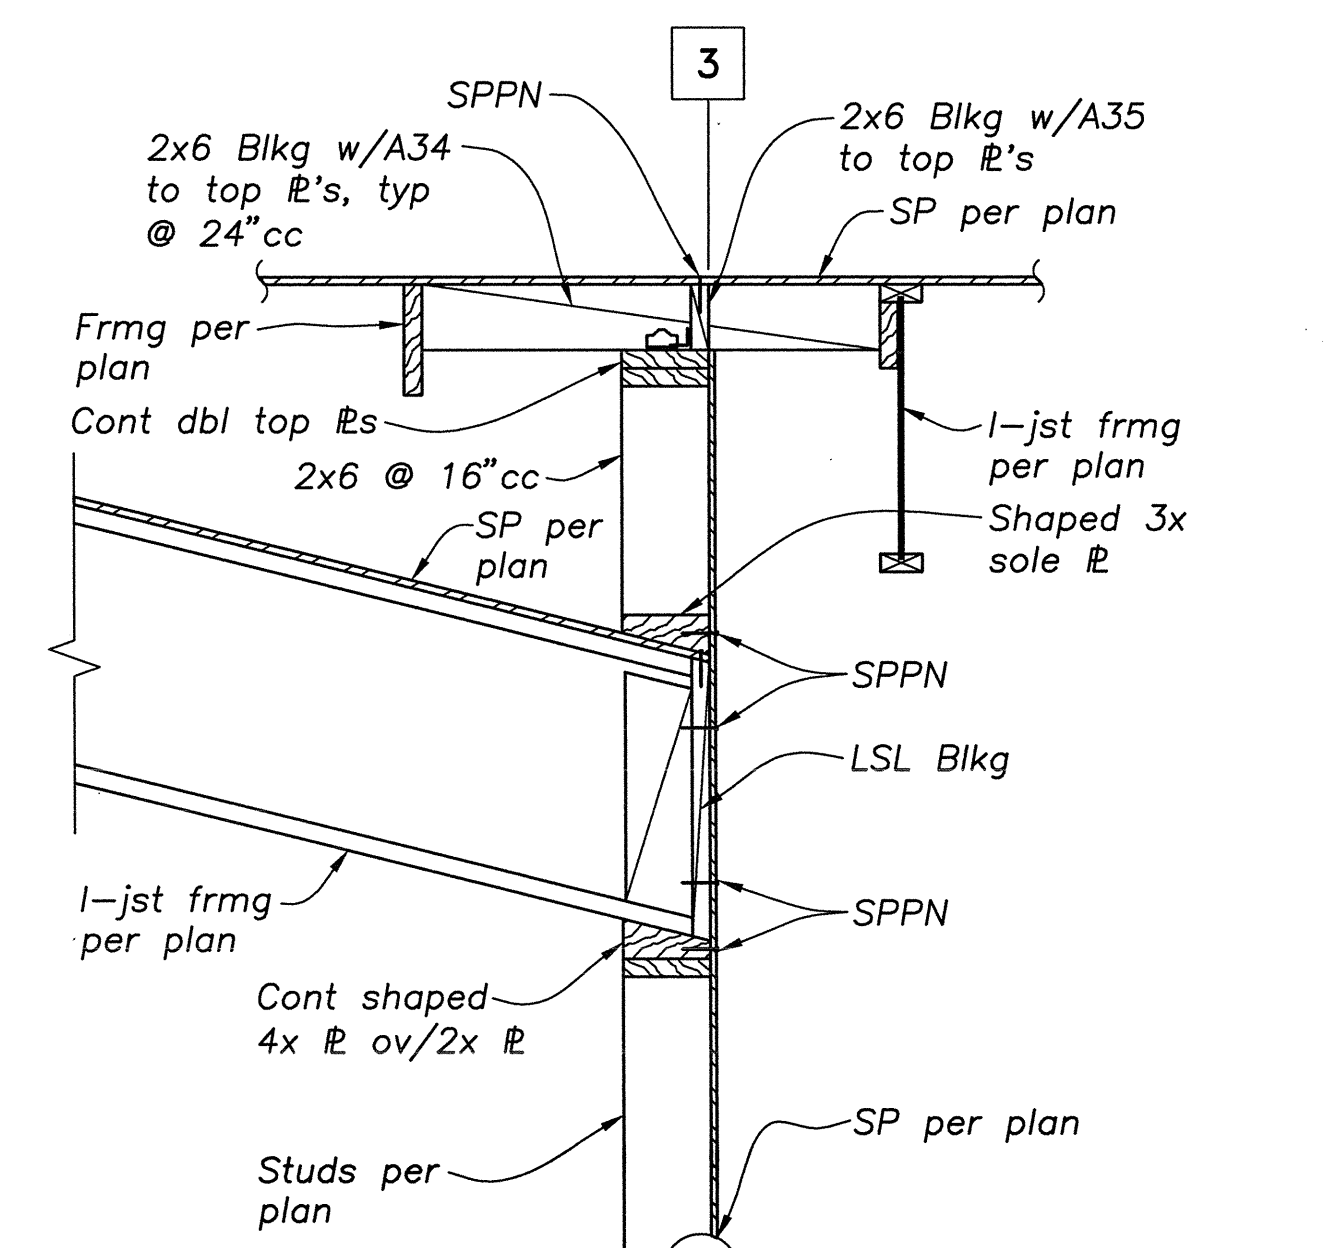


DETAIL 11
3/4" = 1'-0" S4.3

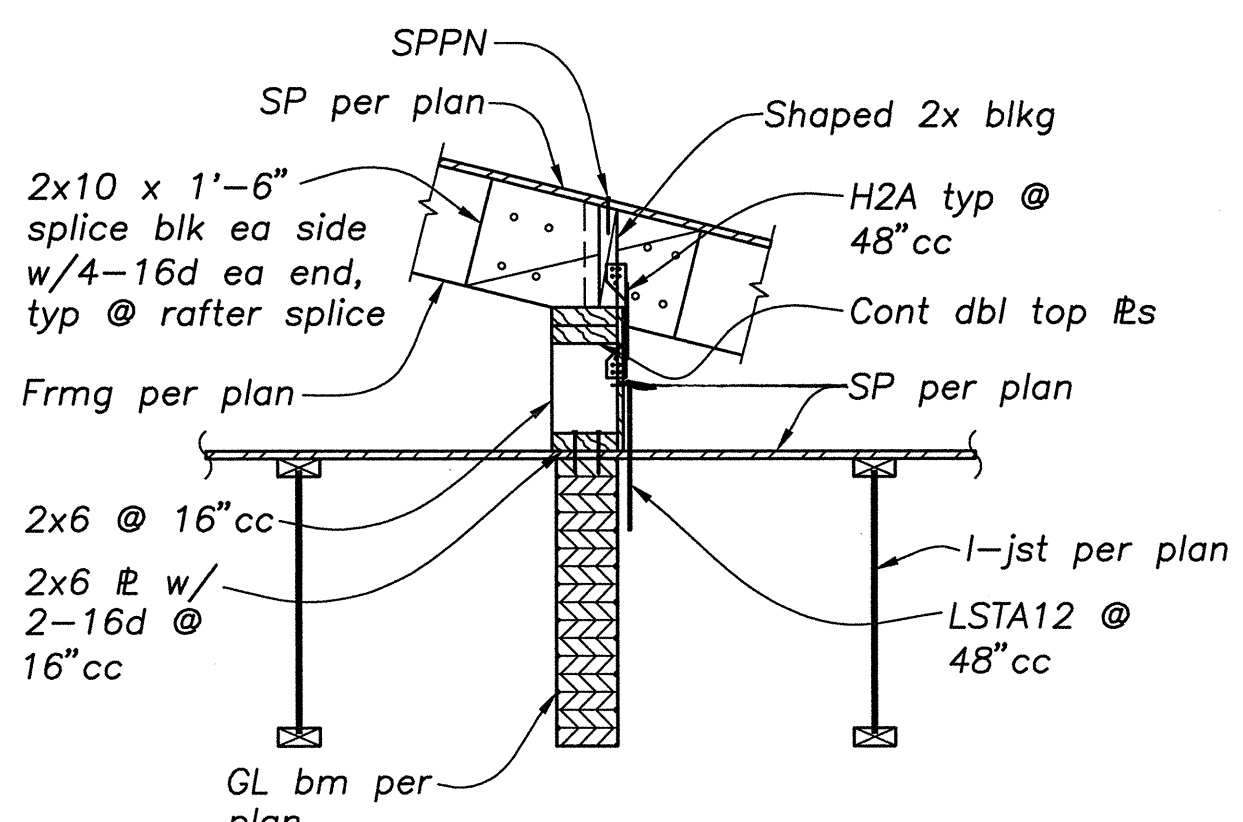


DETAIL 12
3/4" = 1'-0" S4.3

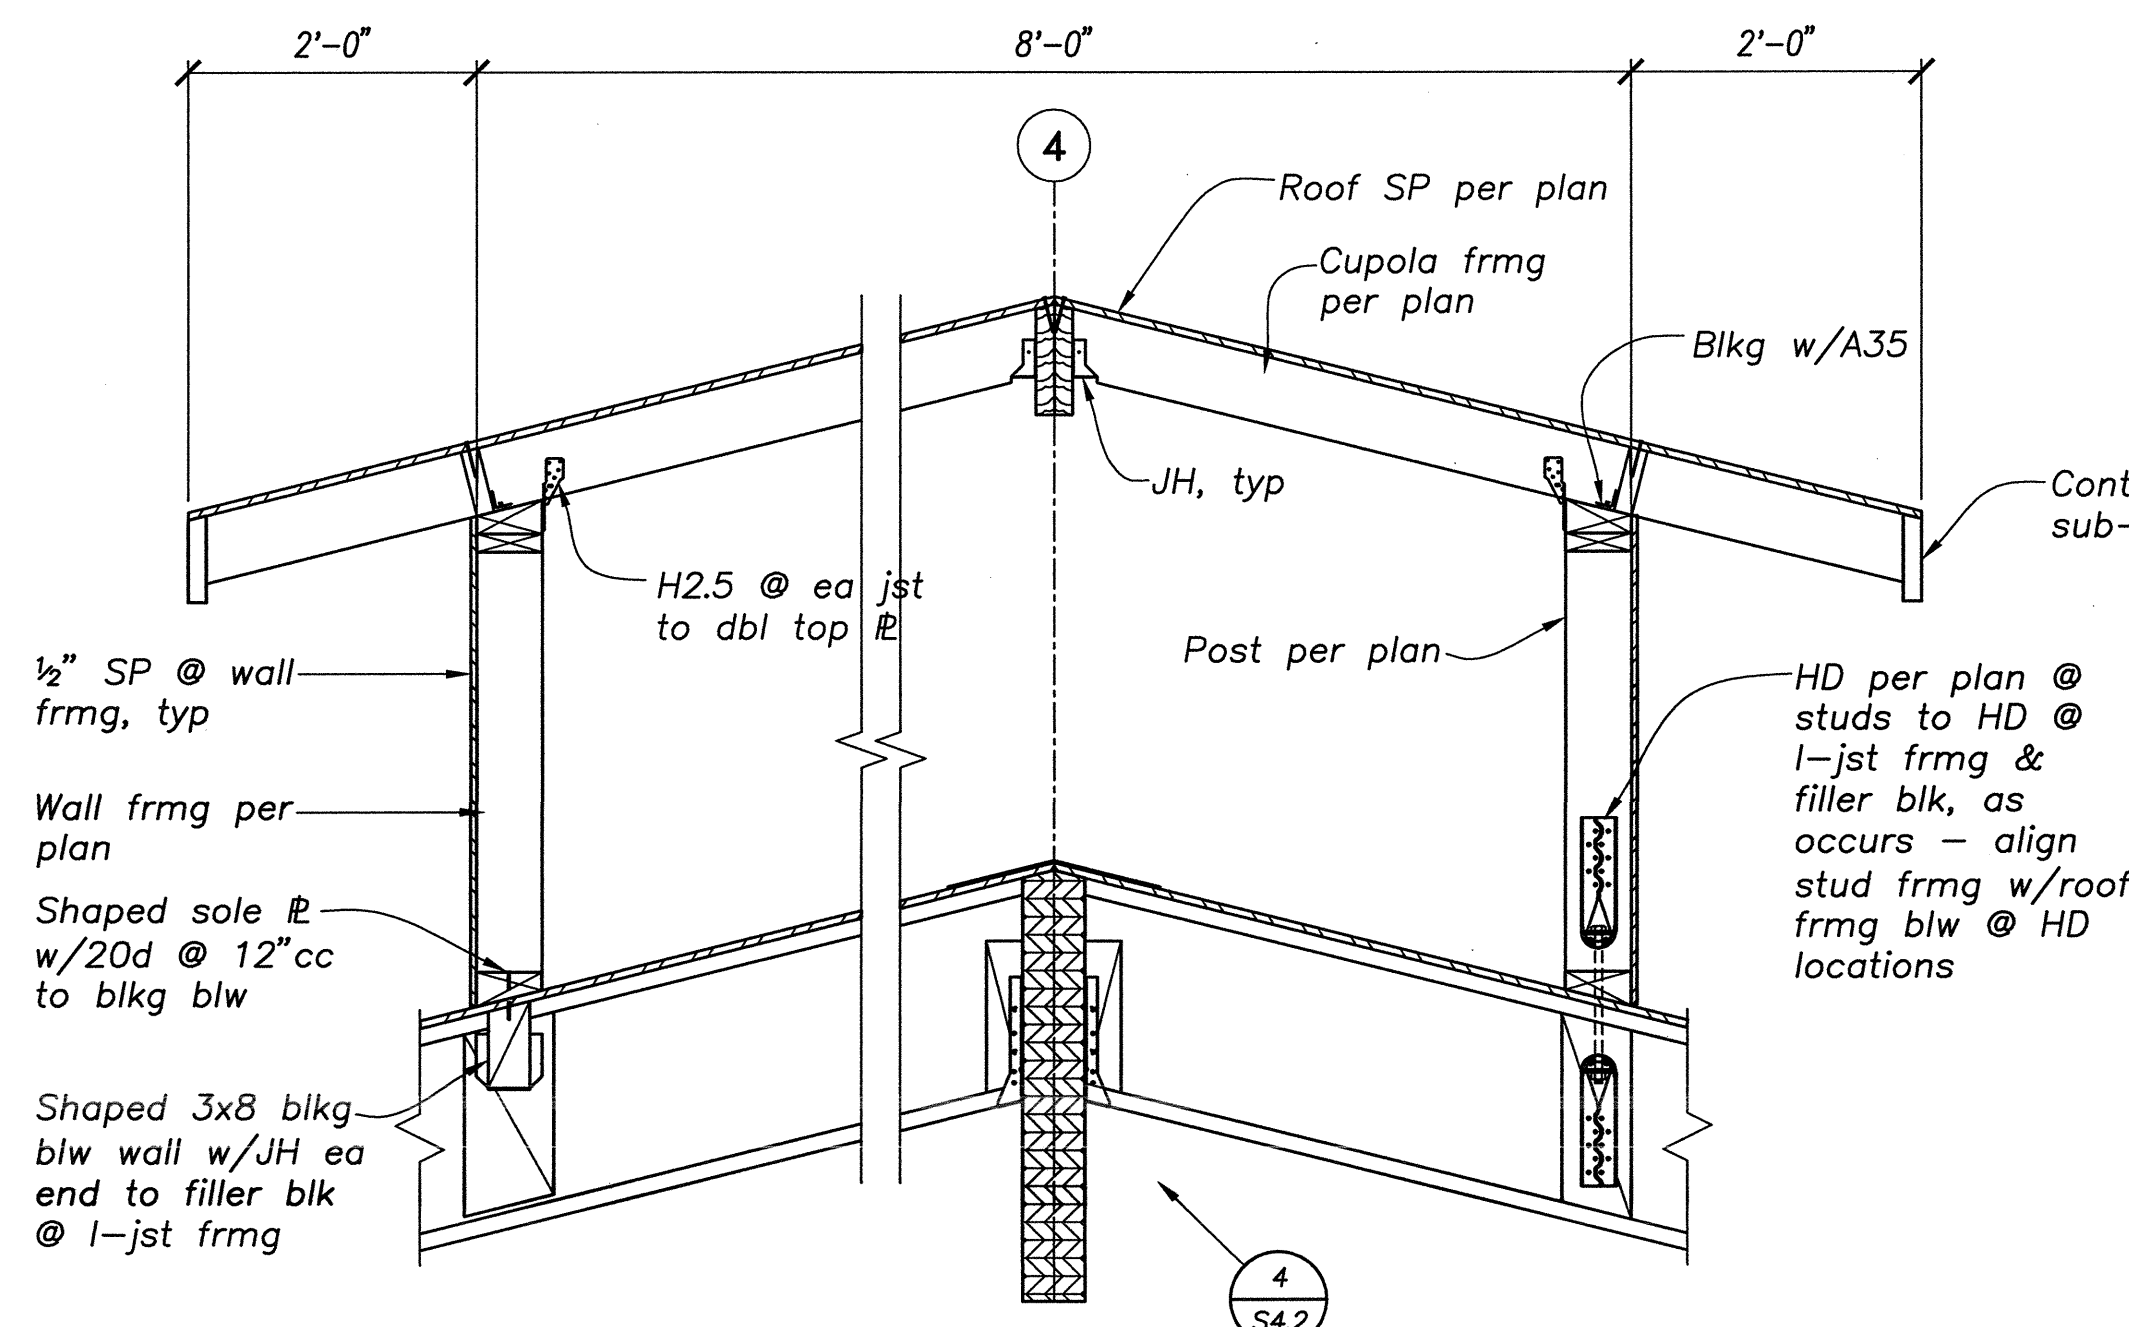


DETAIL 5
3/4" = 1'-0" S4.3

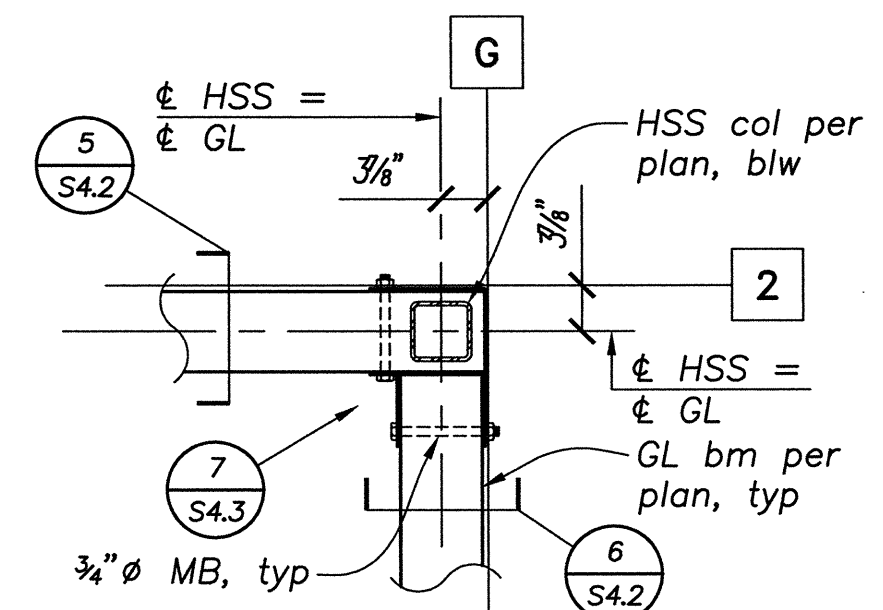


DETAIL 6
3/4" = 1'-0" S4.3

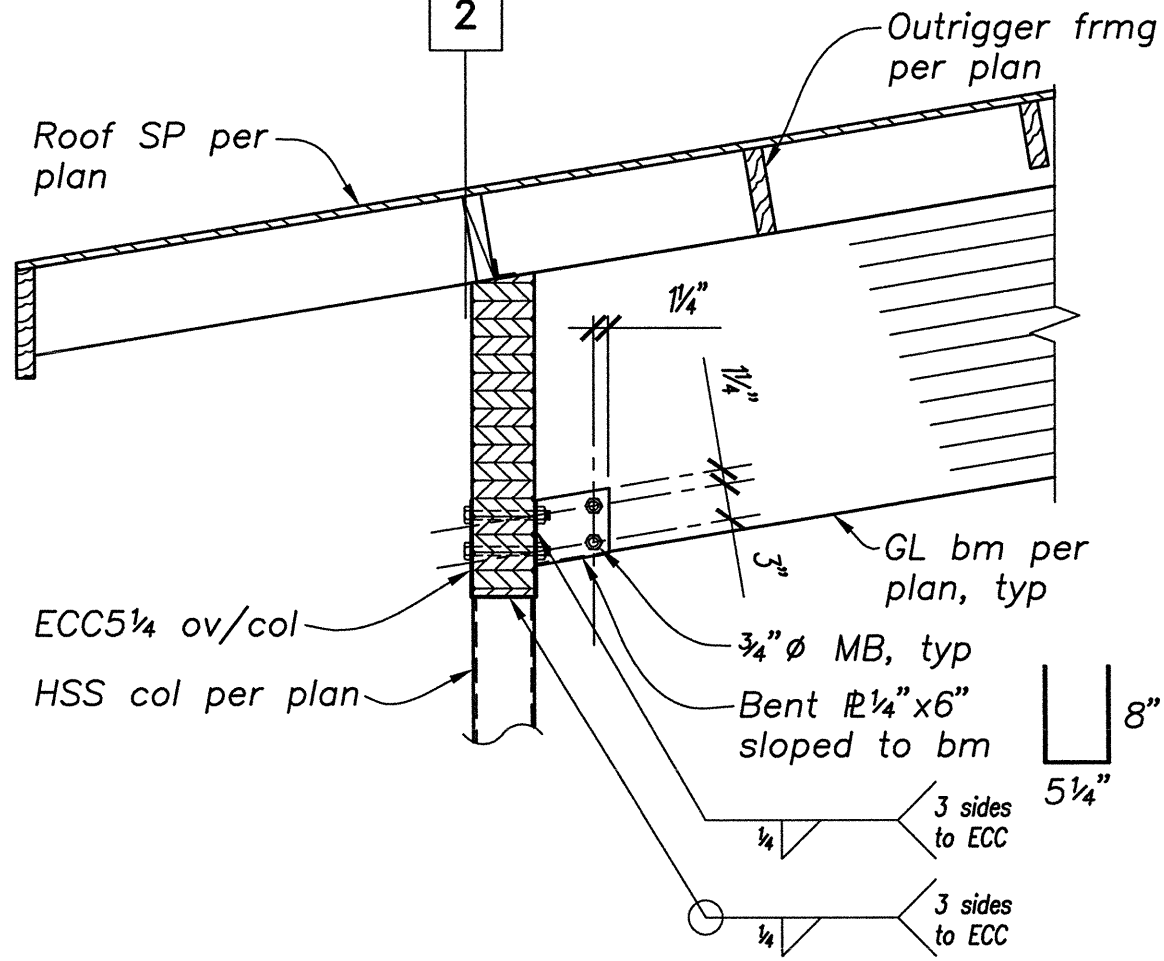


DETAIL 7
3/4" = 1'-0" S4.3

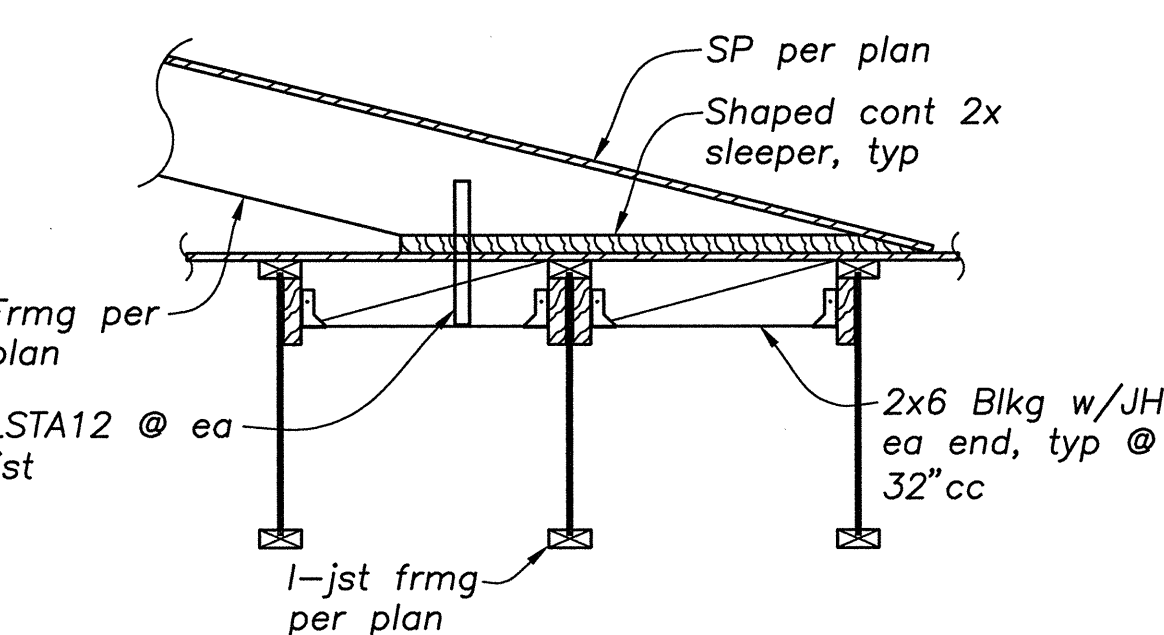


DETAIL 8
3/4" = 1'-0" S4.3

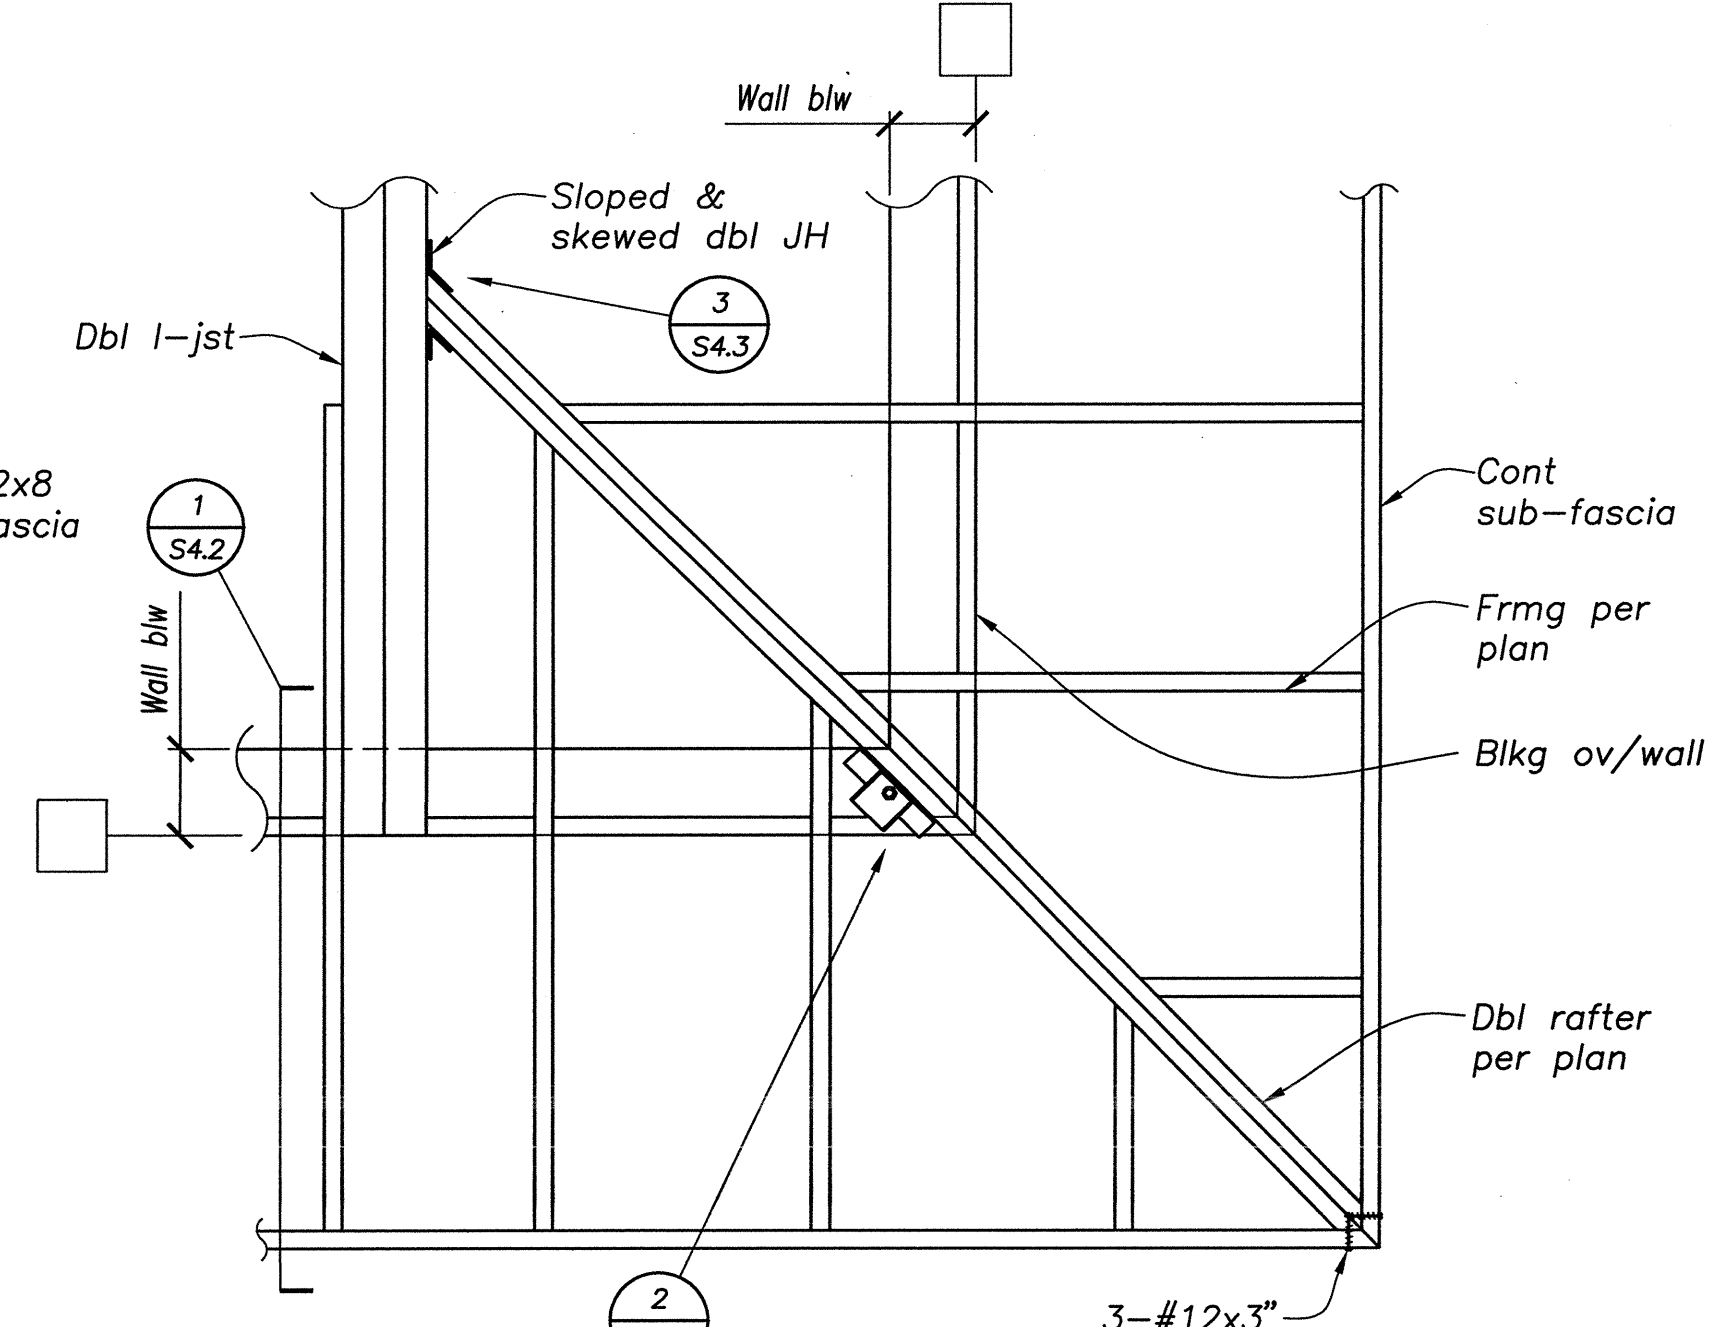


DETAIL 1
3/4" = 1'-0" S4.3

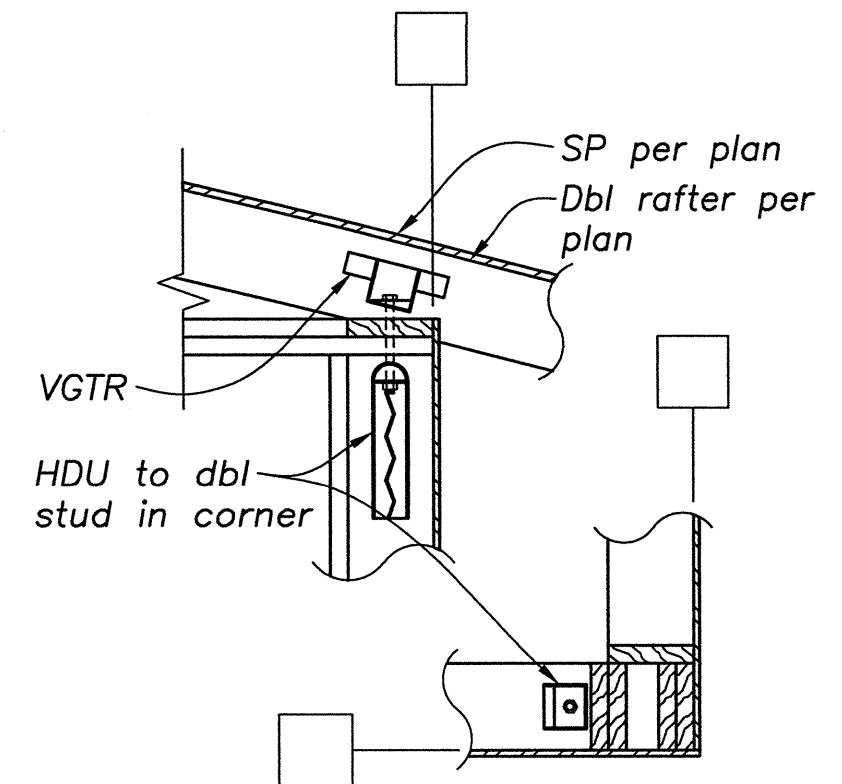

DETAIL 2
3/4" = 1'-0" S4.3

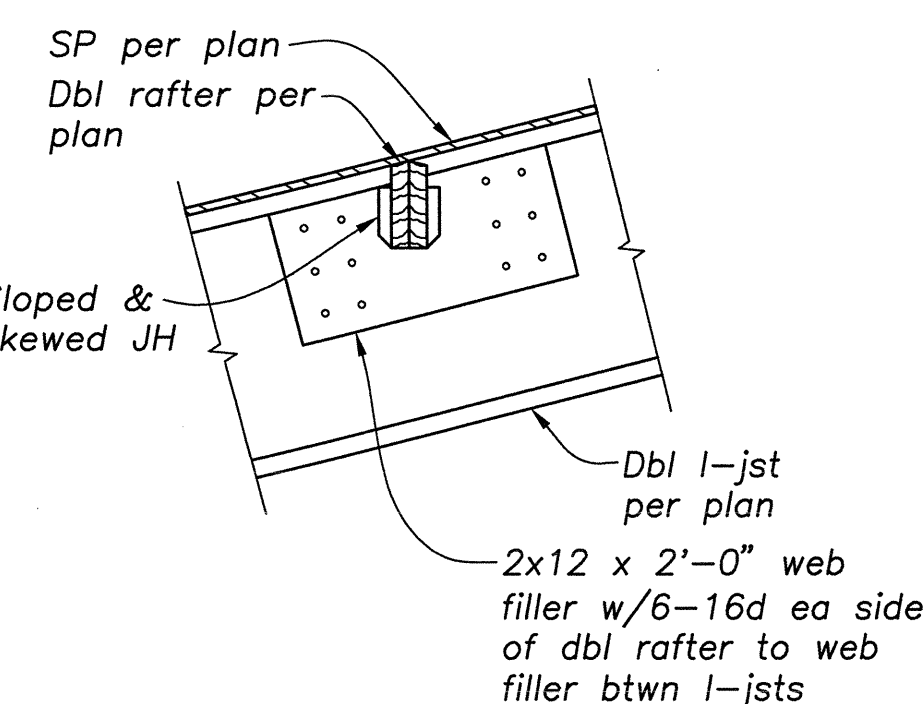

DETAIL 3
3/4" = 1'-0" S4.3

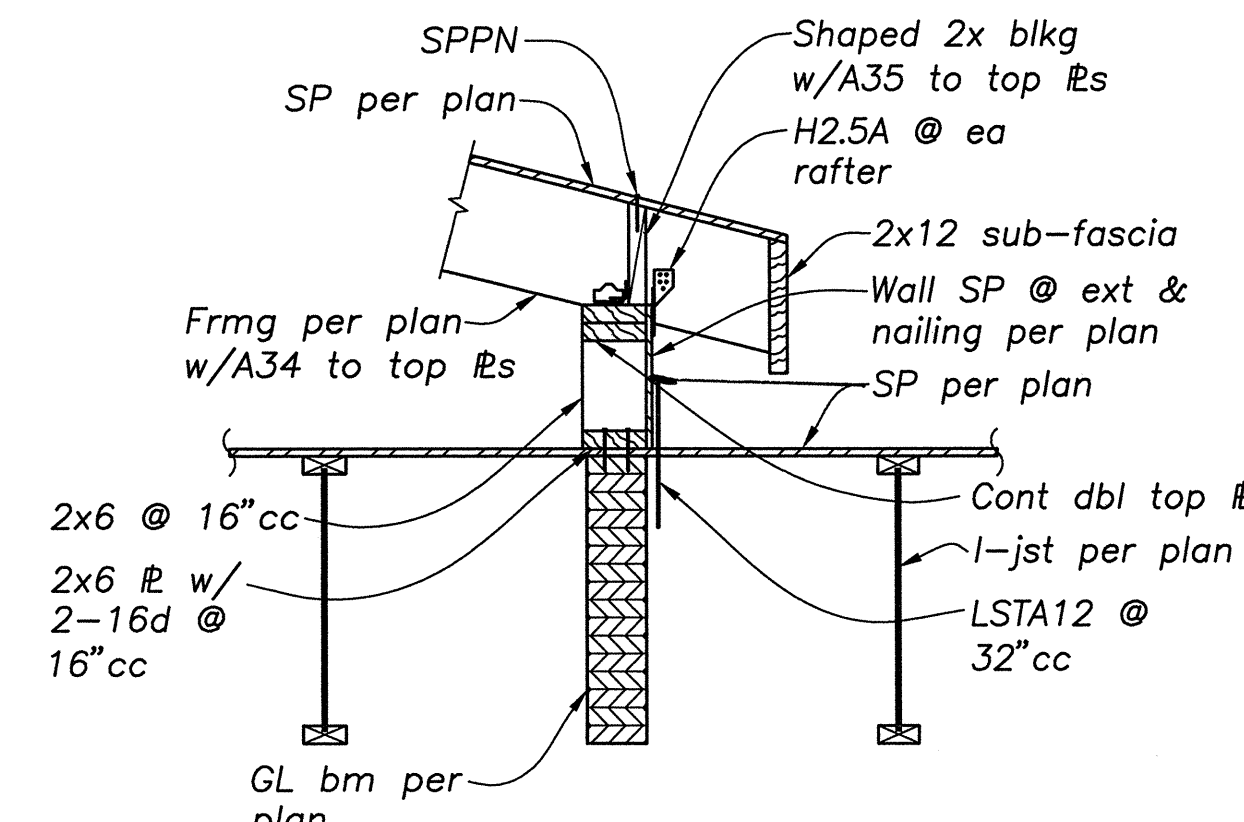

DETAIL 4
3/4" = 1'-0" S4.3

Dry Creek Joint Elementary School District
District Education Center
8849 Cook Riolo Road, Roseville, CA 95747
Dry Creek Joint Elementary School District

FILE NO. 31-15
IDENTIFICATION STAMP DIV. OF THE
STATE ARCHITECT OFFICE OF
REGULATION SERVICES
APPLICATION NO.
02-115456
AC FLS SS
DATE 2/22/17

DIVISION OF THE STATE ARCHITECT
revision date: by:

www.barrish.com

barrish pelham
Consulting Engineers
Sacramento-Walnut Creek-Tygh/Redo

CONSULTANT

nacht&lewis
600 G Street, Suite 100
Sacramento, CA 95811
www.nachtandlewis.com
916.329.4000

ARCHITECT

INITIAL BOX

NO.	DWG BY	DATE	REVIEWED

REVISIONS

NO.	DESCRIPTION	DATE	REV

DATE February 23, 2017

JOB NO. Y1538.00












SHEET TITLE

Roof Framing Details

SHEET NO.

S4.3

ONE AND ONE-HALF INCH = ONE FOOT
THREE-QUARTERS INCH = ONE FOOT
ONE-HALF INCH = ONE FOOT
ONE-QUARTER INCH = ONE FOOT
ONE-EIGHTH INCH = ONE FOOT
ONE-SIXTEENTH INCH = ONE FOOT
ONE INCH = TWENTY FEET

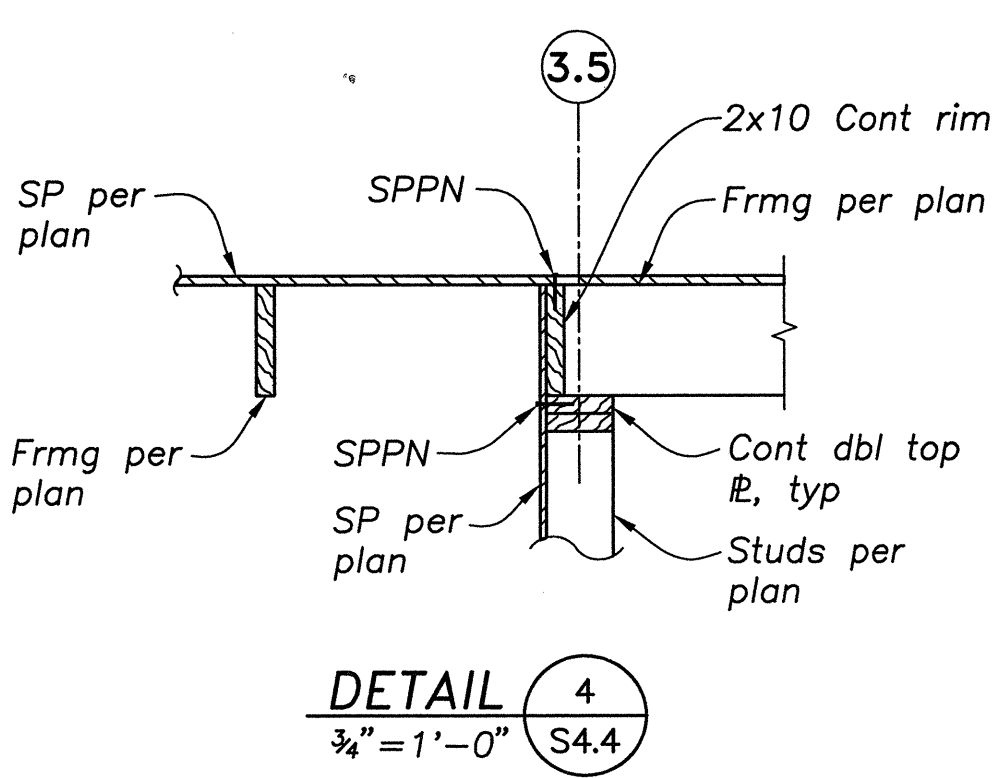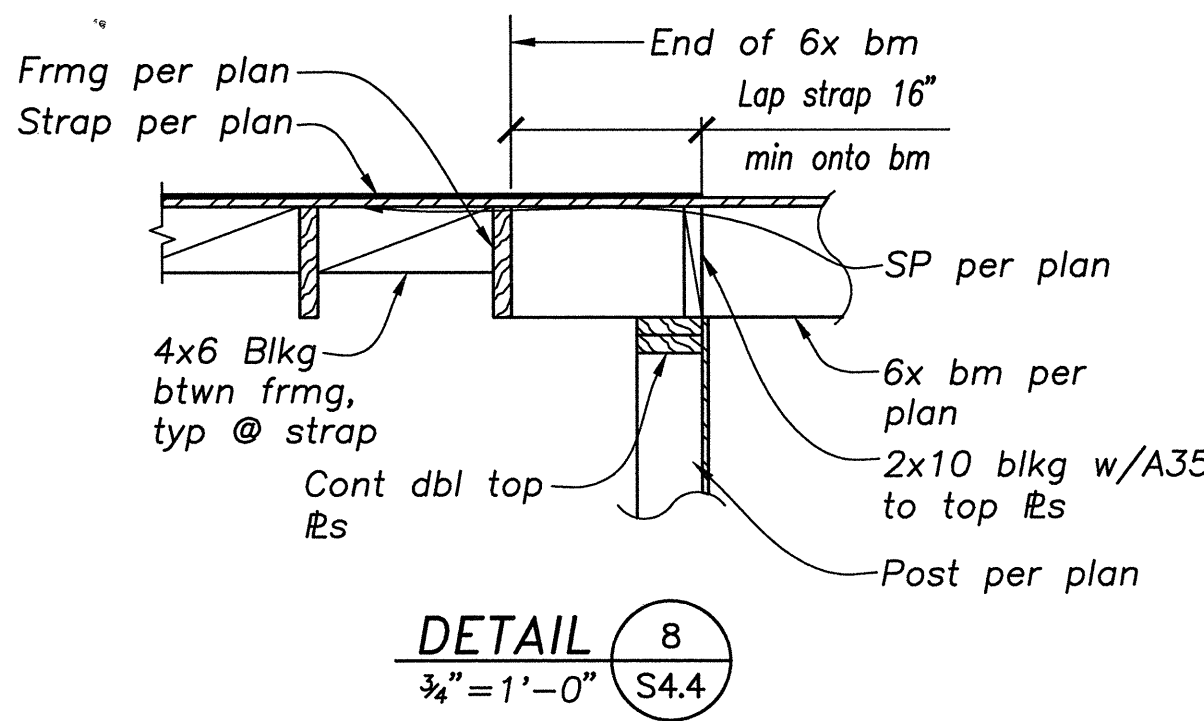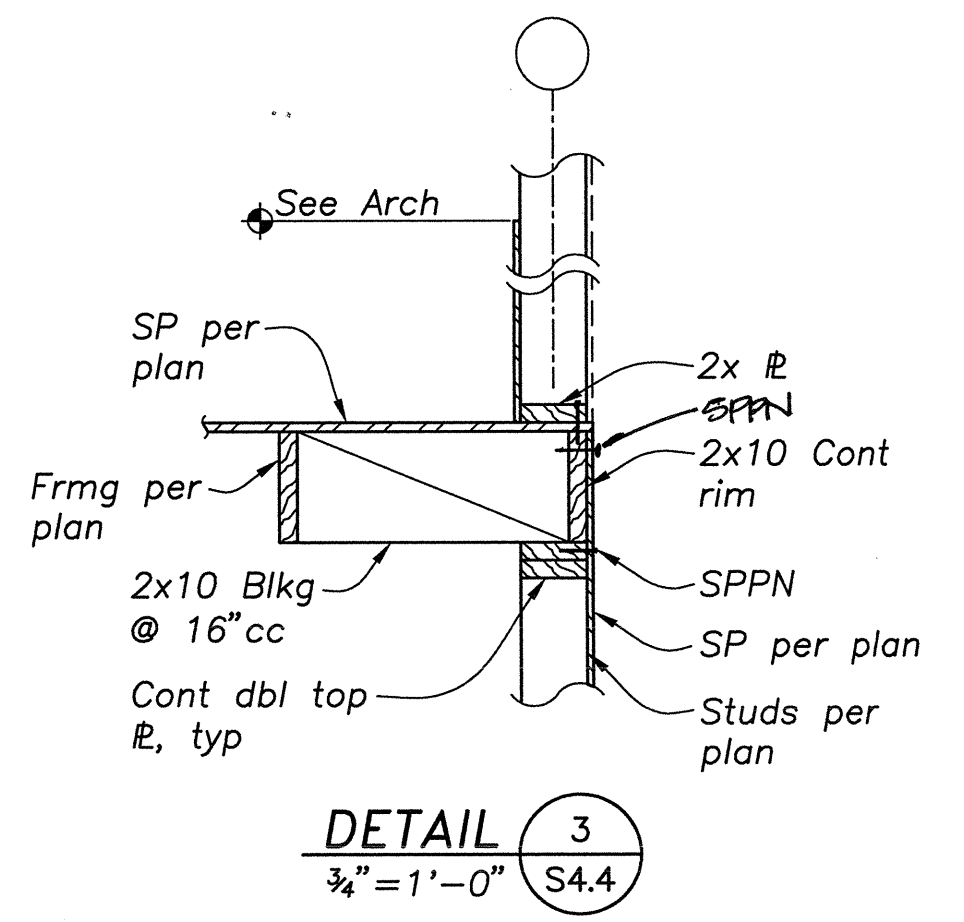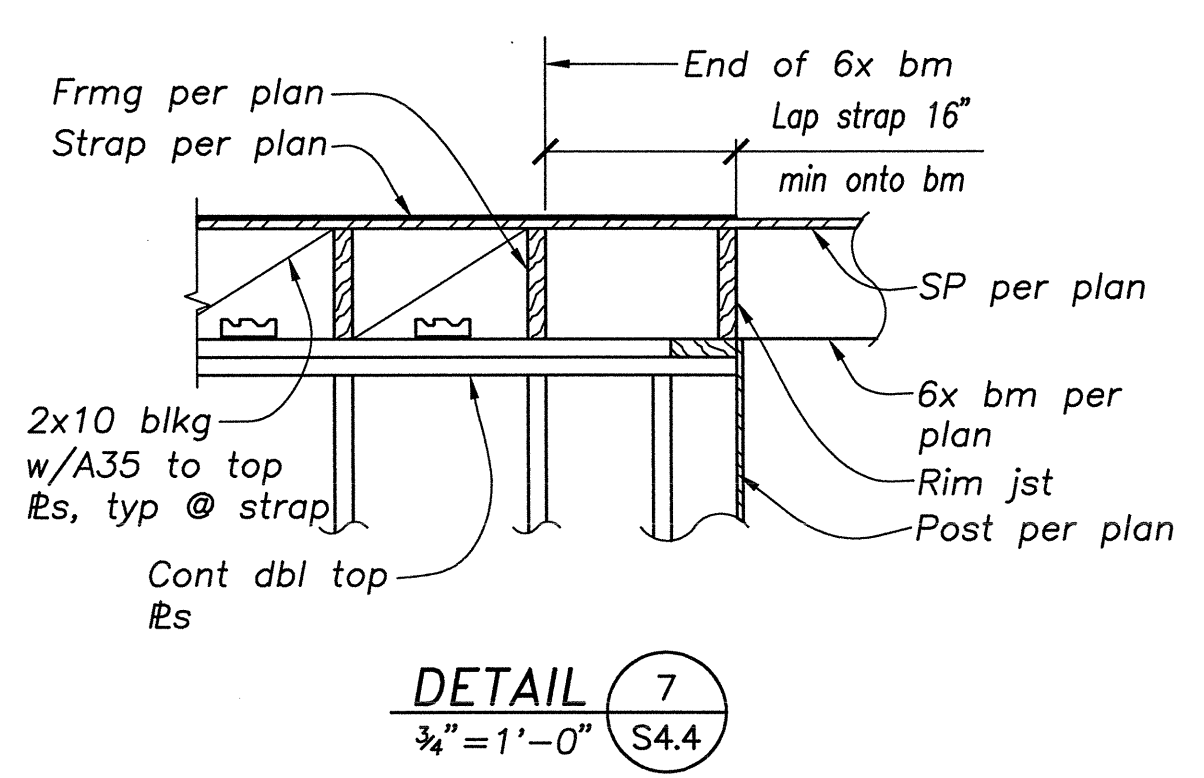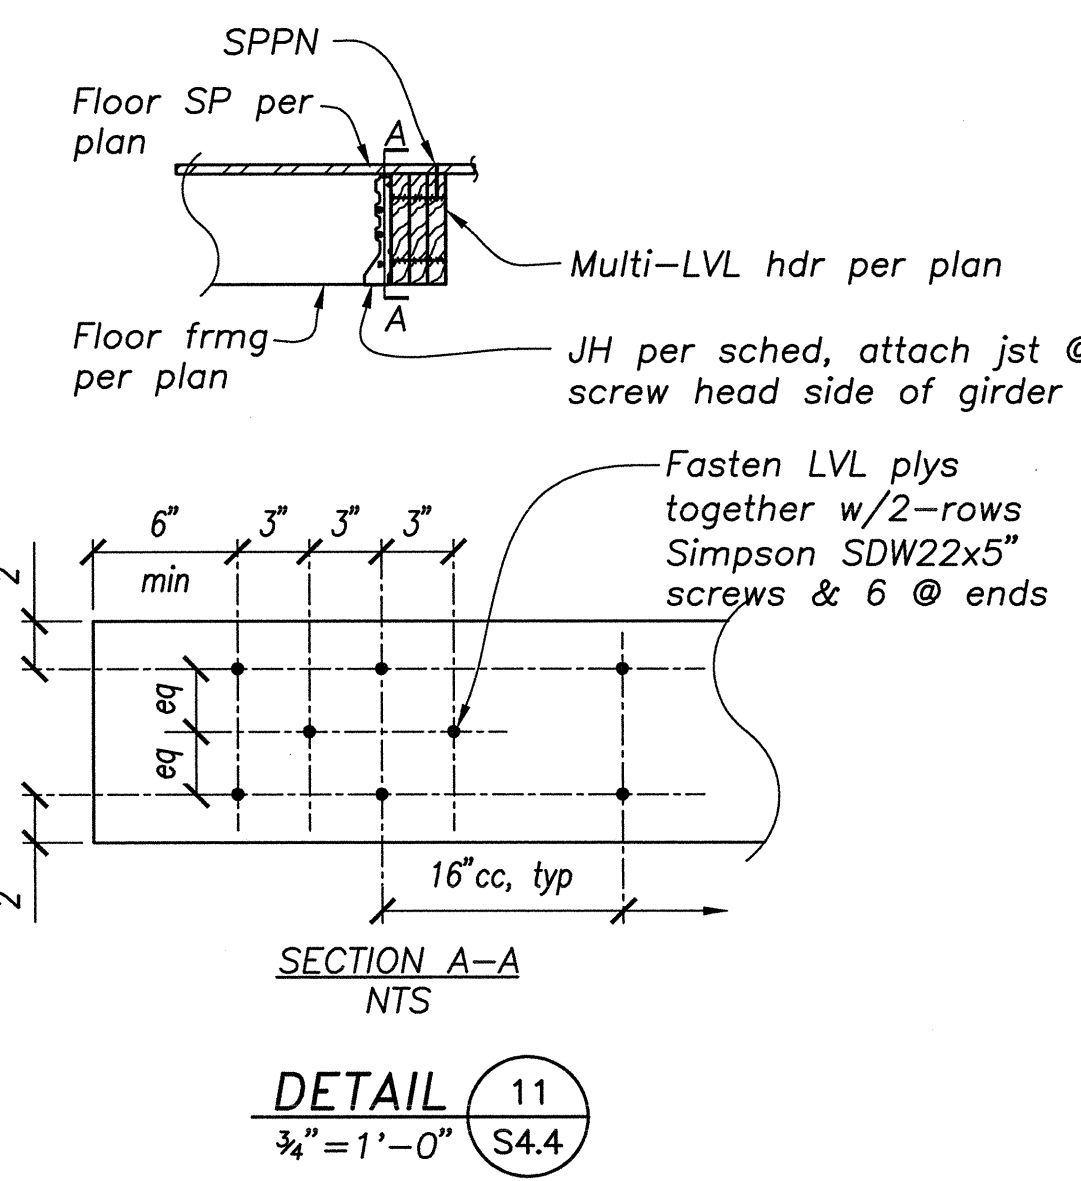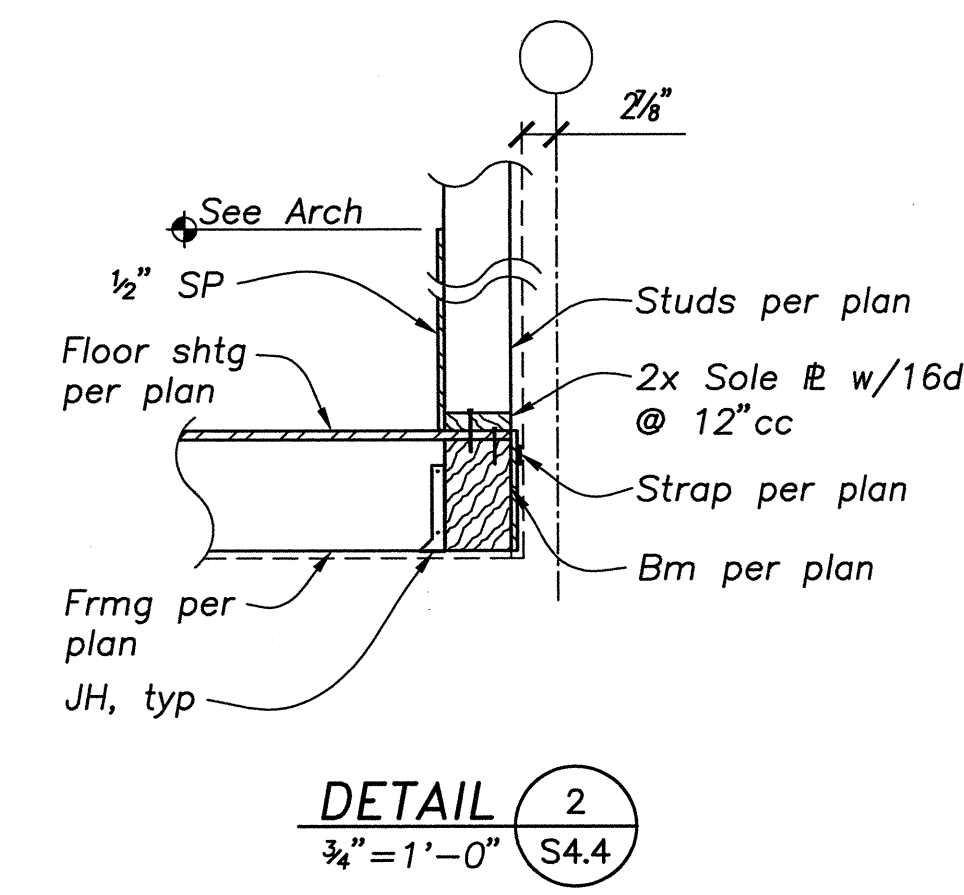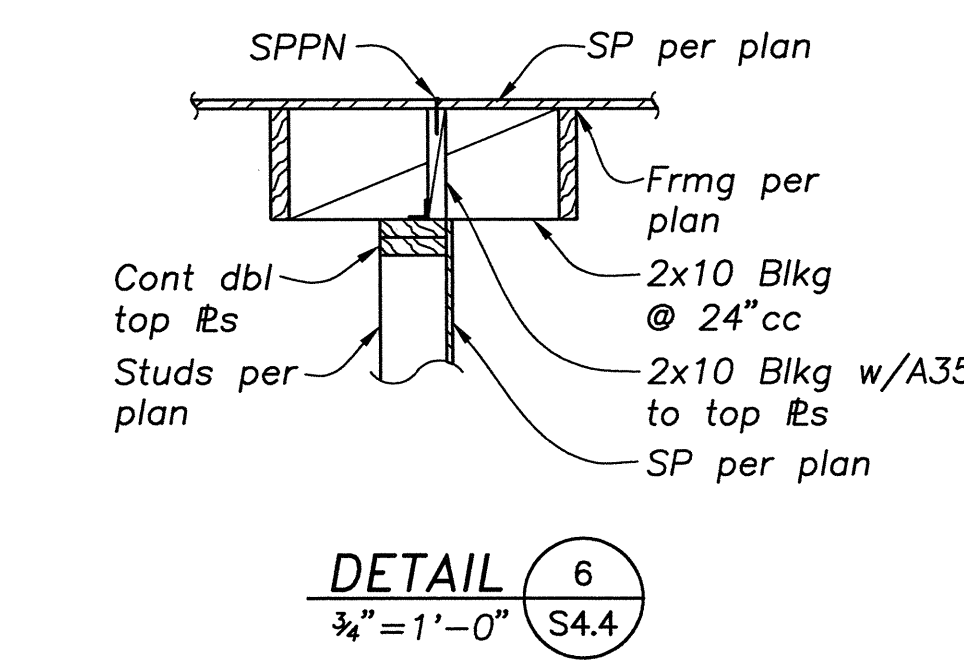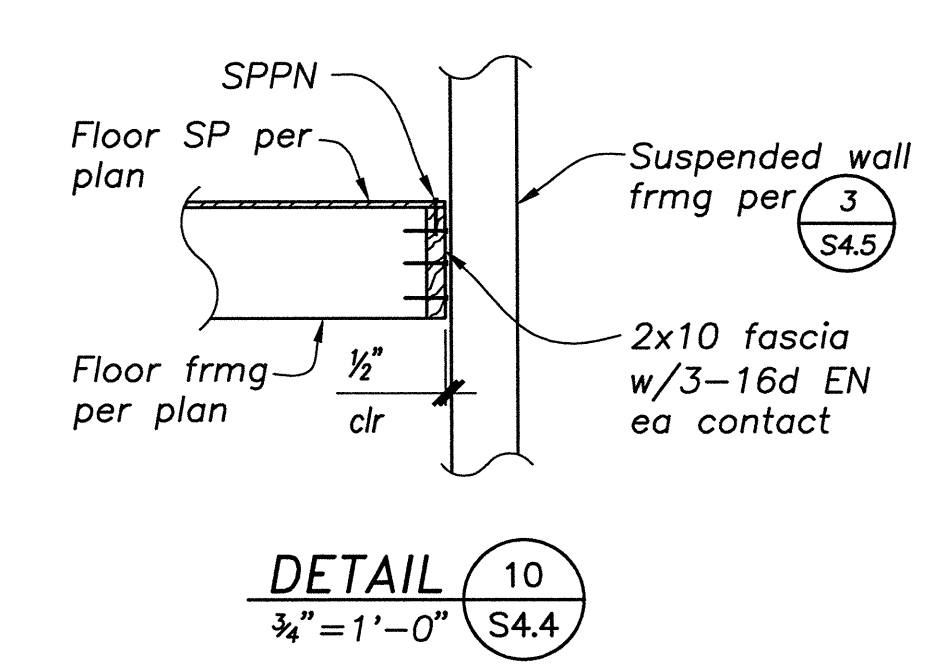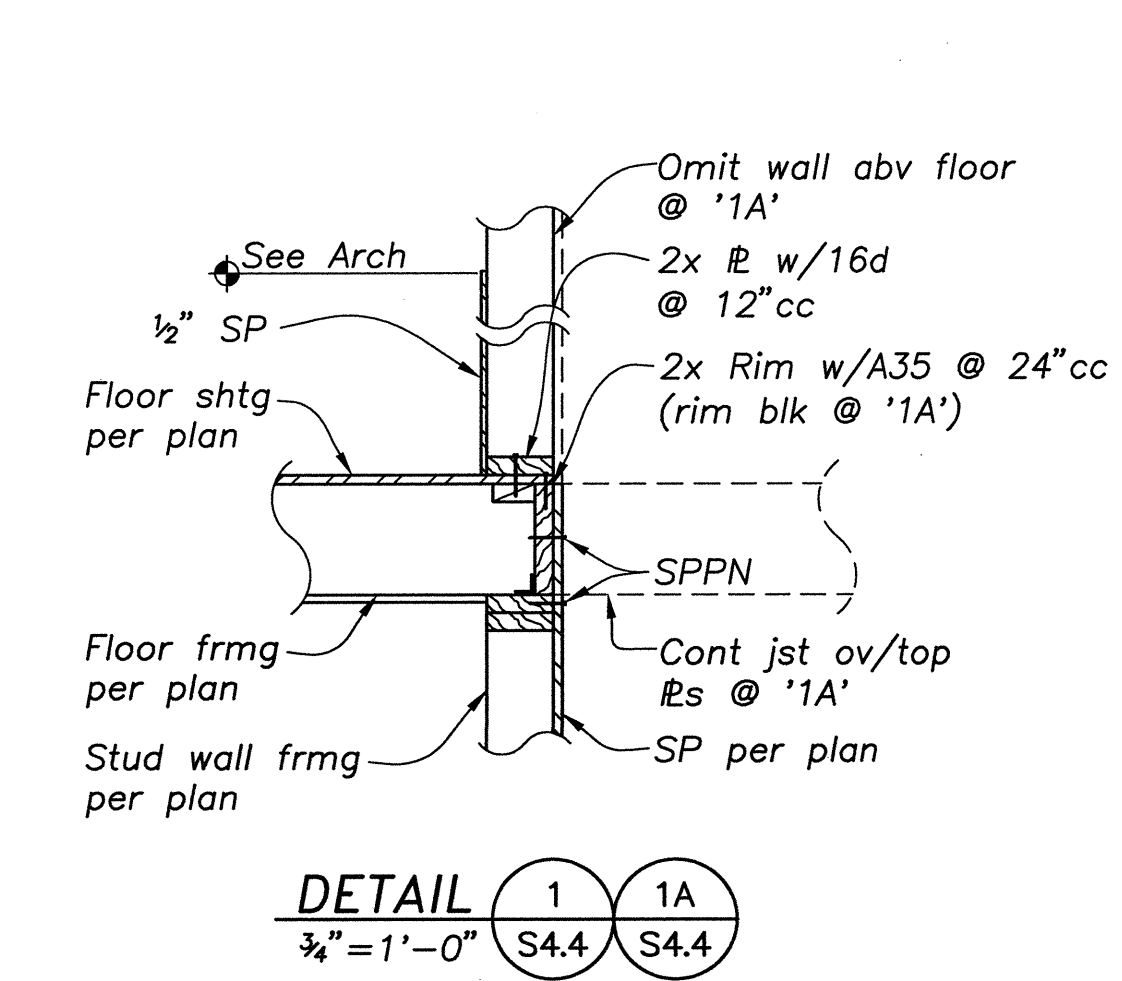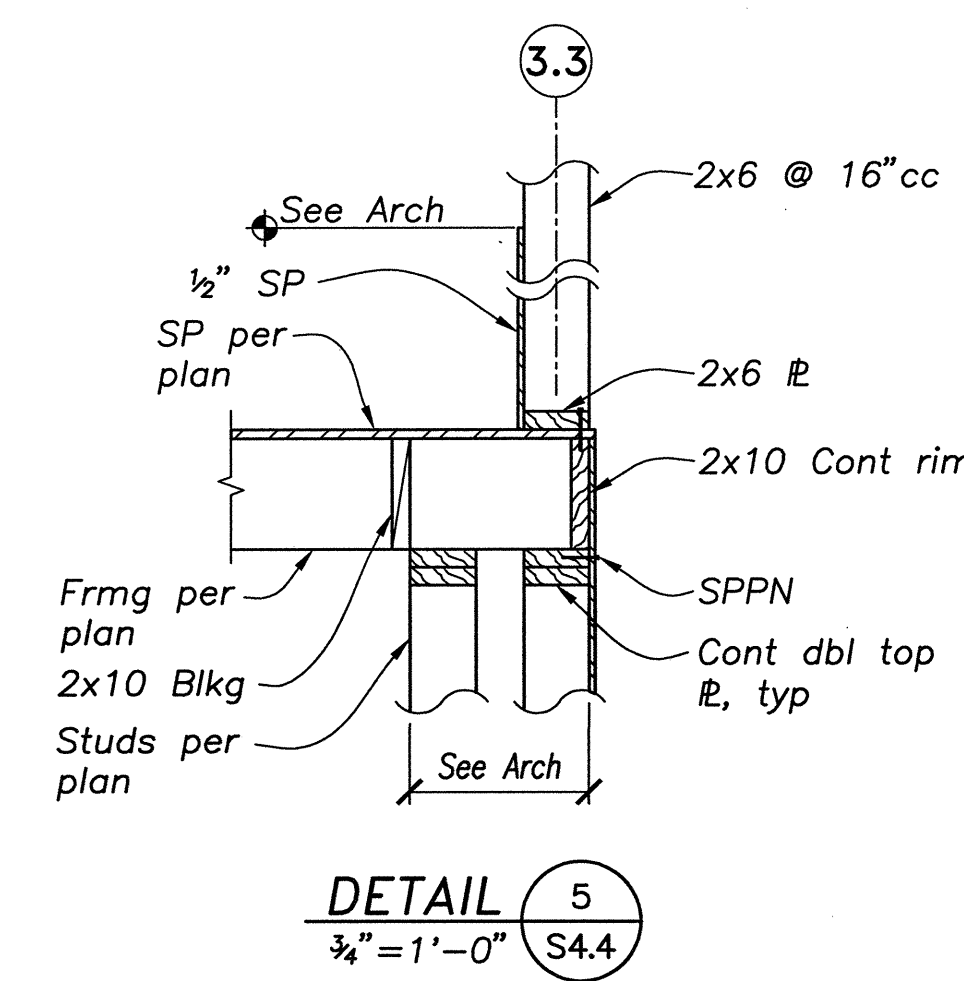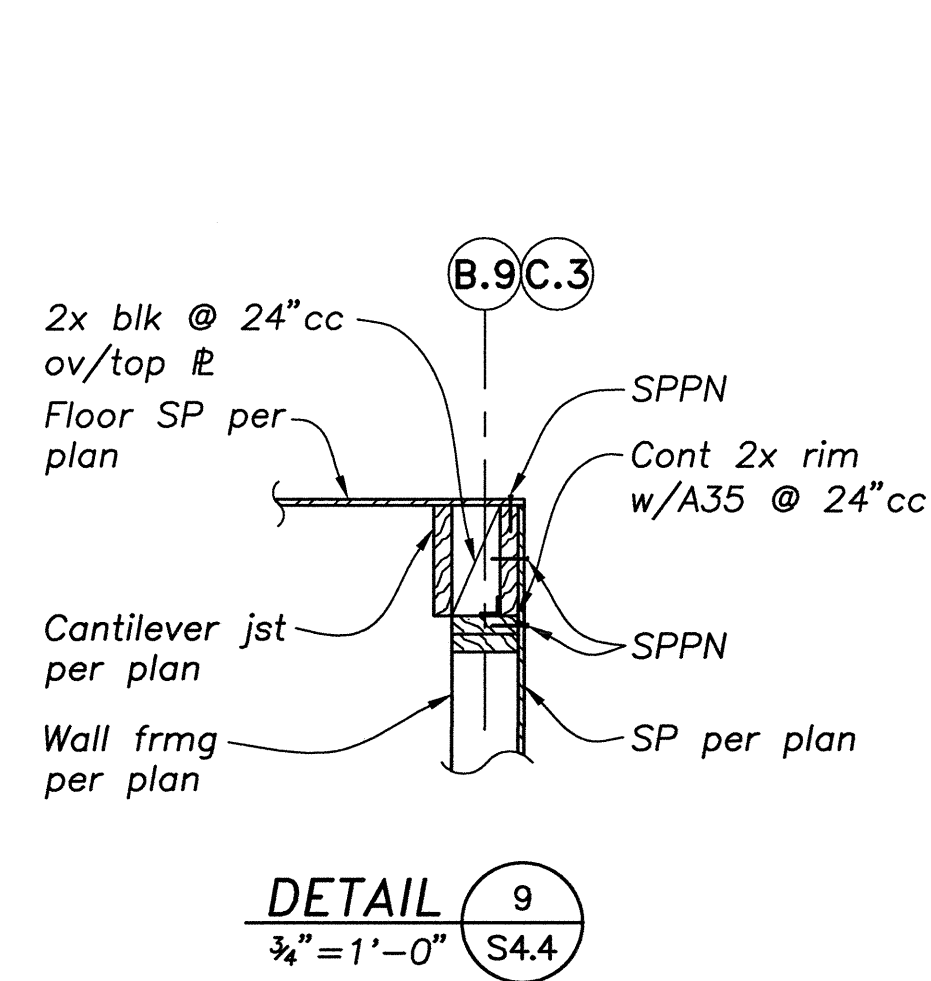

Dry Creek Joint Elementary School District
District Education Center

8849 Cook Riolo Road, Roseville, CA 95747
Dry Creek Joint Elementary School District

FILE NO. 31-15
IDENTIFICATION STAMP DIV. OF THE
STATE ARCHITECT OFFICE OF
REGULATION SERVICES
APPLICATION NO.
02-115456
AC FLS SS
DATE 2/23/17 CCA

DIVISION OF THE STATE ARCHITECT
revision date: by:

www.barrish.com
barrish pelham
Consulting Engineers
Sacramento-Walnut Creek-Yuba/Reno
2/22/17

CONSULTANT

nacht&lewis
600 G Street, Suite 100
Sacramento, CA 95811
www.nachtandlewis.com
916.329.4000

RENEWAL DATE:
1/31/18
No. C-24987
STATE OF CALIFORNIA

ARCHITECT

INITIAL BOX			
NO.	DWG BY	DATE	REVIEWED


REVISIONS			
NO.	DESCRIPTION	DATE	REV
	100% design development	7/6/16	
	75% construction documents	9/23/16	
	DSA Submittal	12/31/16	
	DSA Backcheck	02/23/17	

DATE February 23, 2017
JOB NO. Y1538.00
SHEET TITLE


Floor Framing
Details

SHEET NO.


S4.4

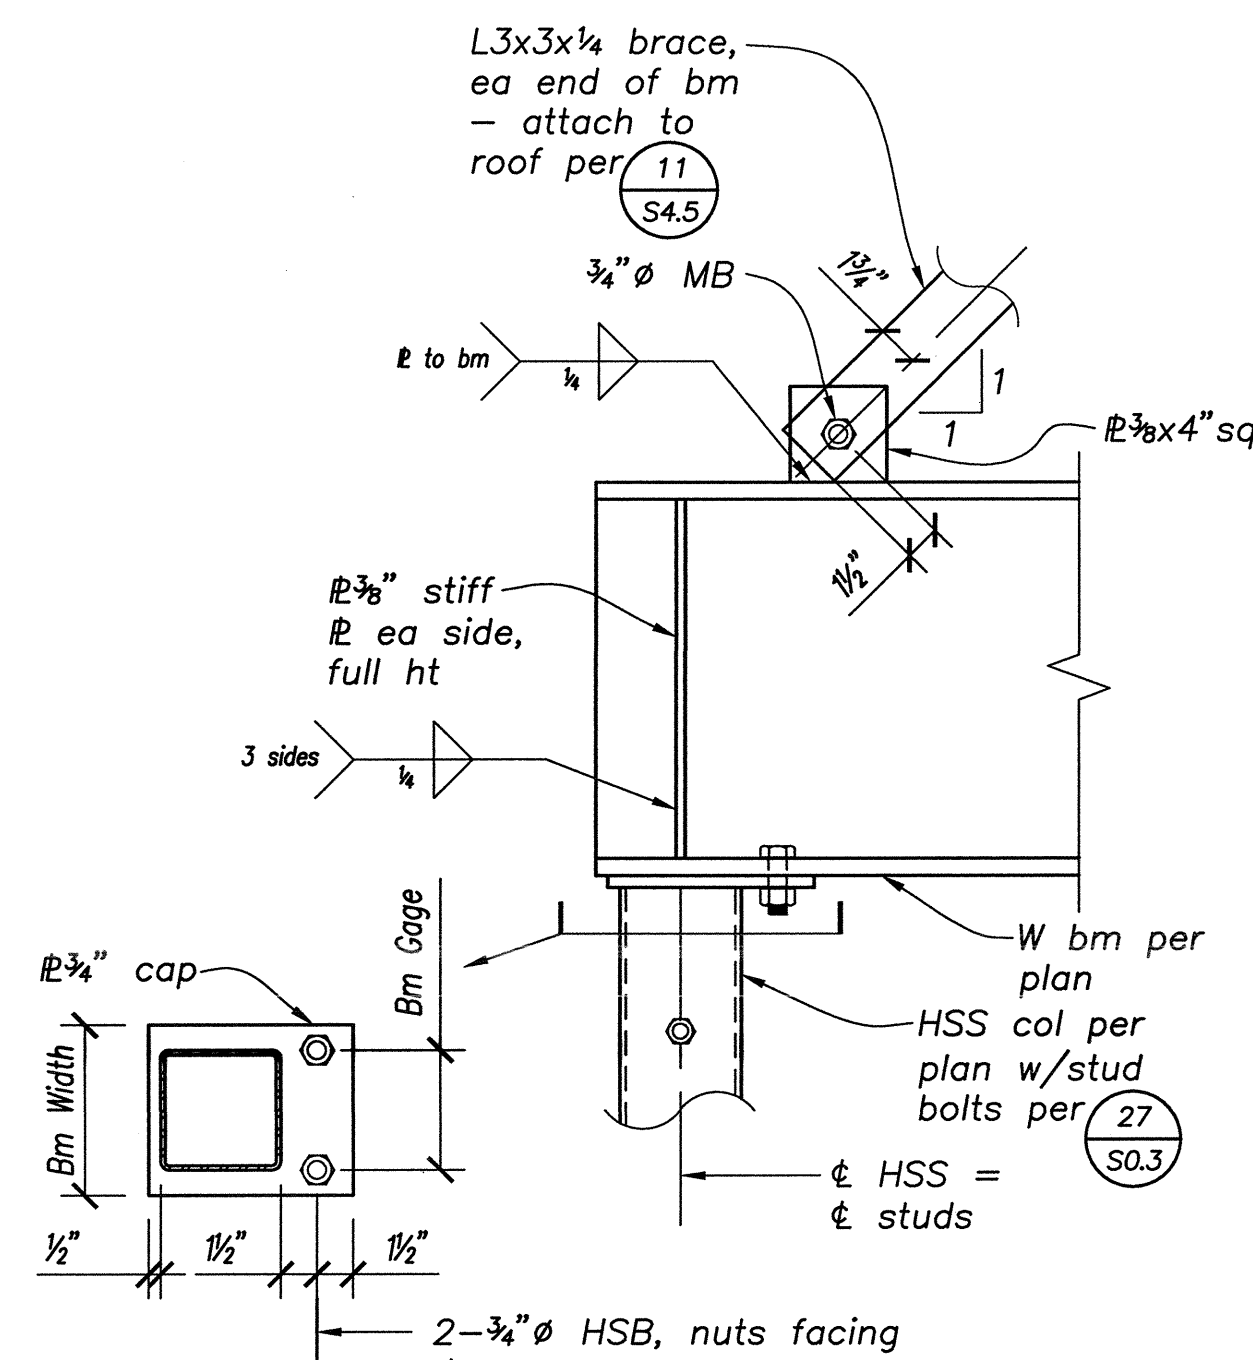


DETAIL 9
1 1/2\"/>

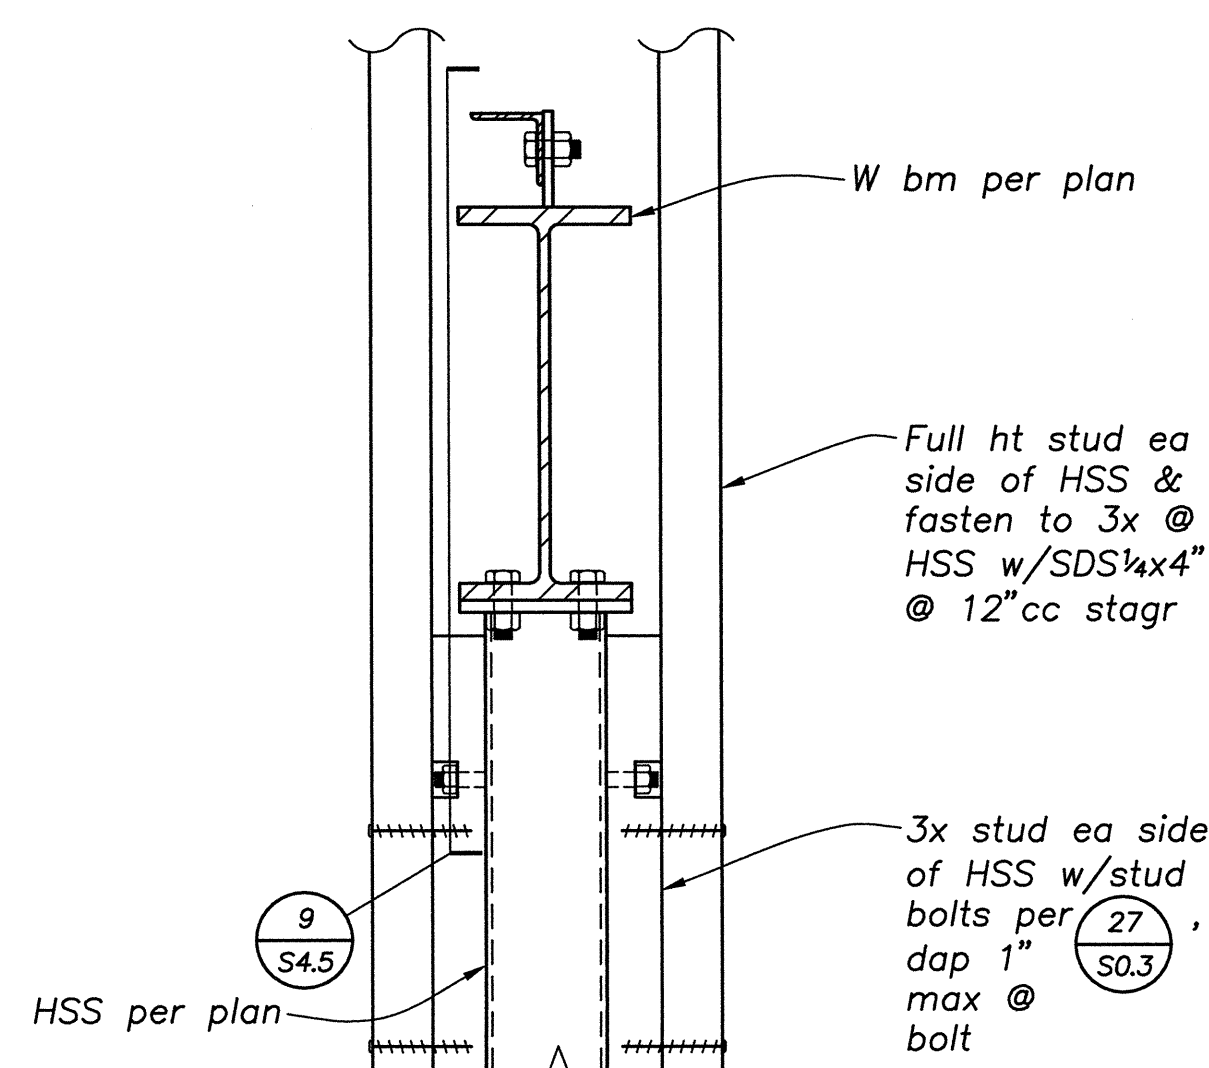


DETAIL 10
1 1/2\"/>

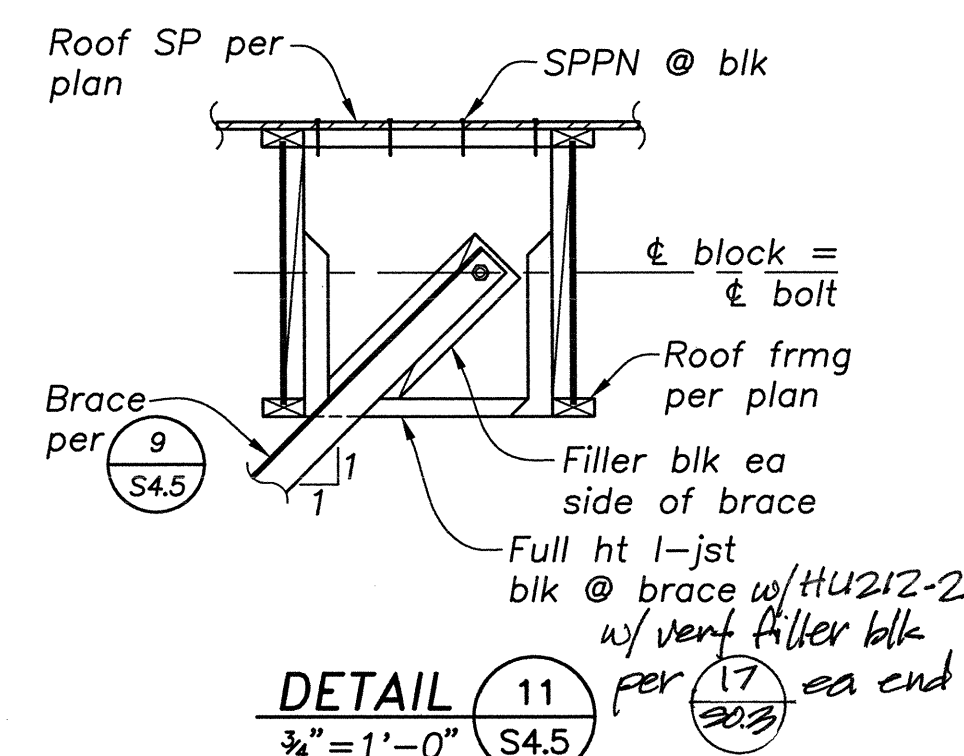


DETAIL 11
3/4\"/>

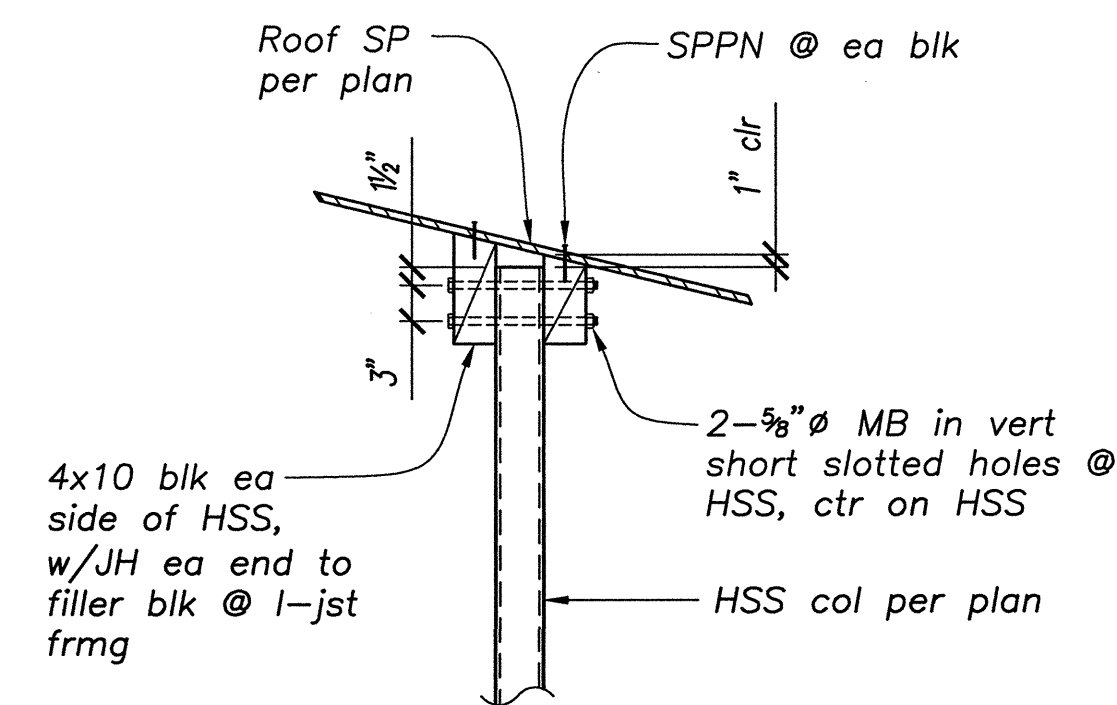


DETAIL 5
3/4\"/>

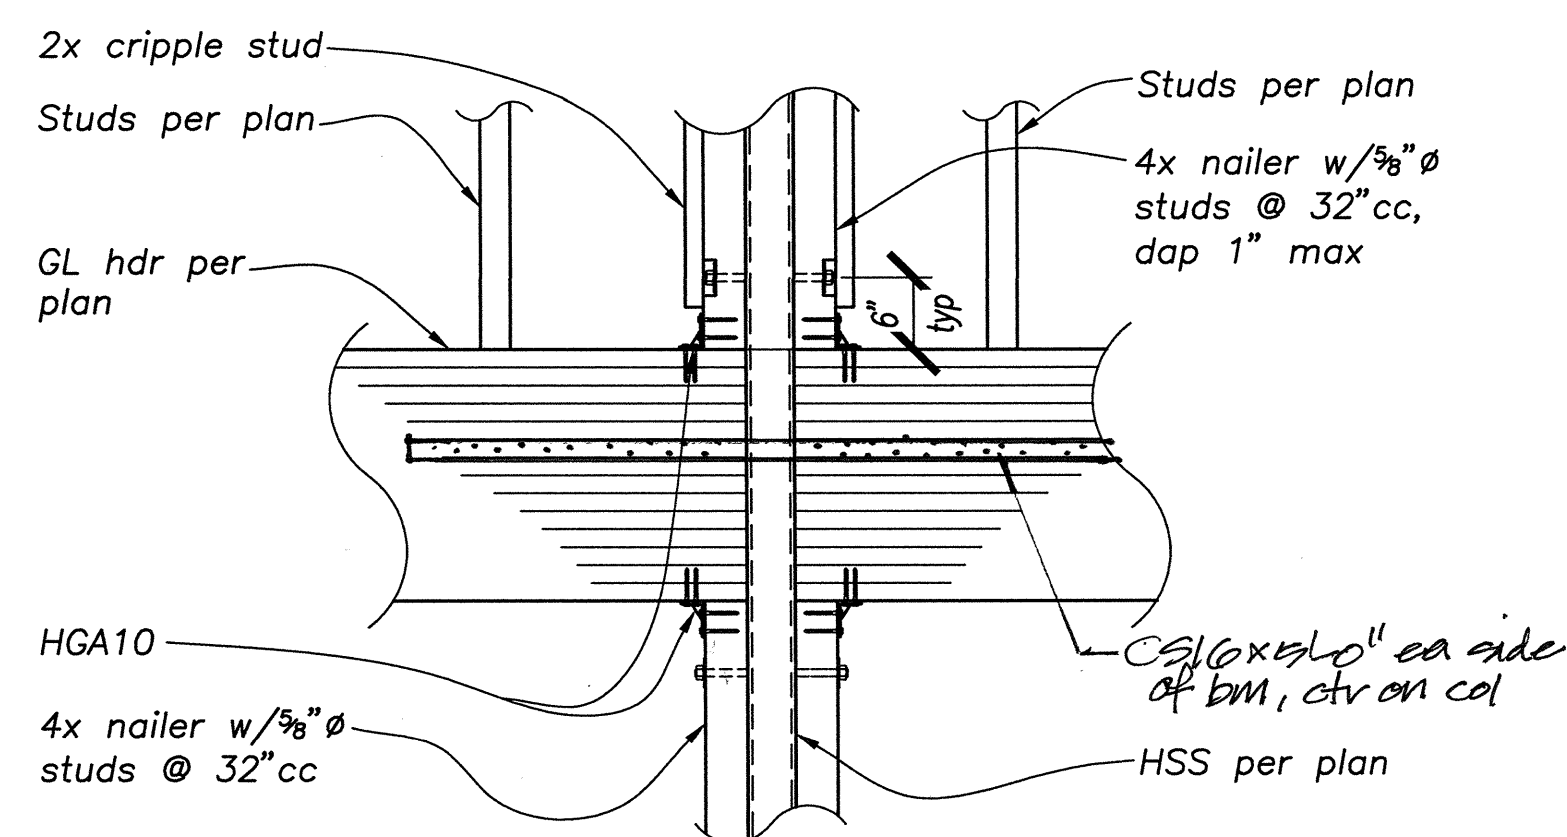


DETAIL 6
3/4\"/>

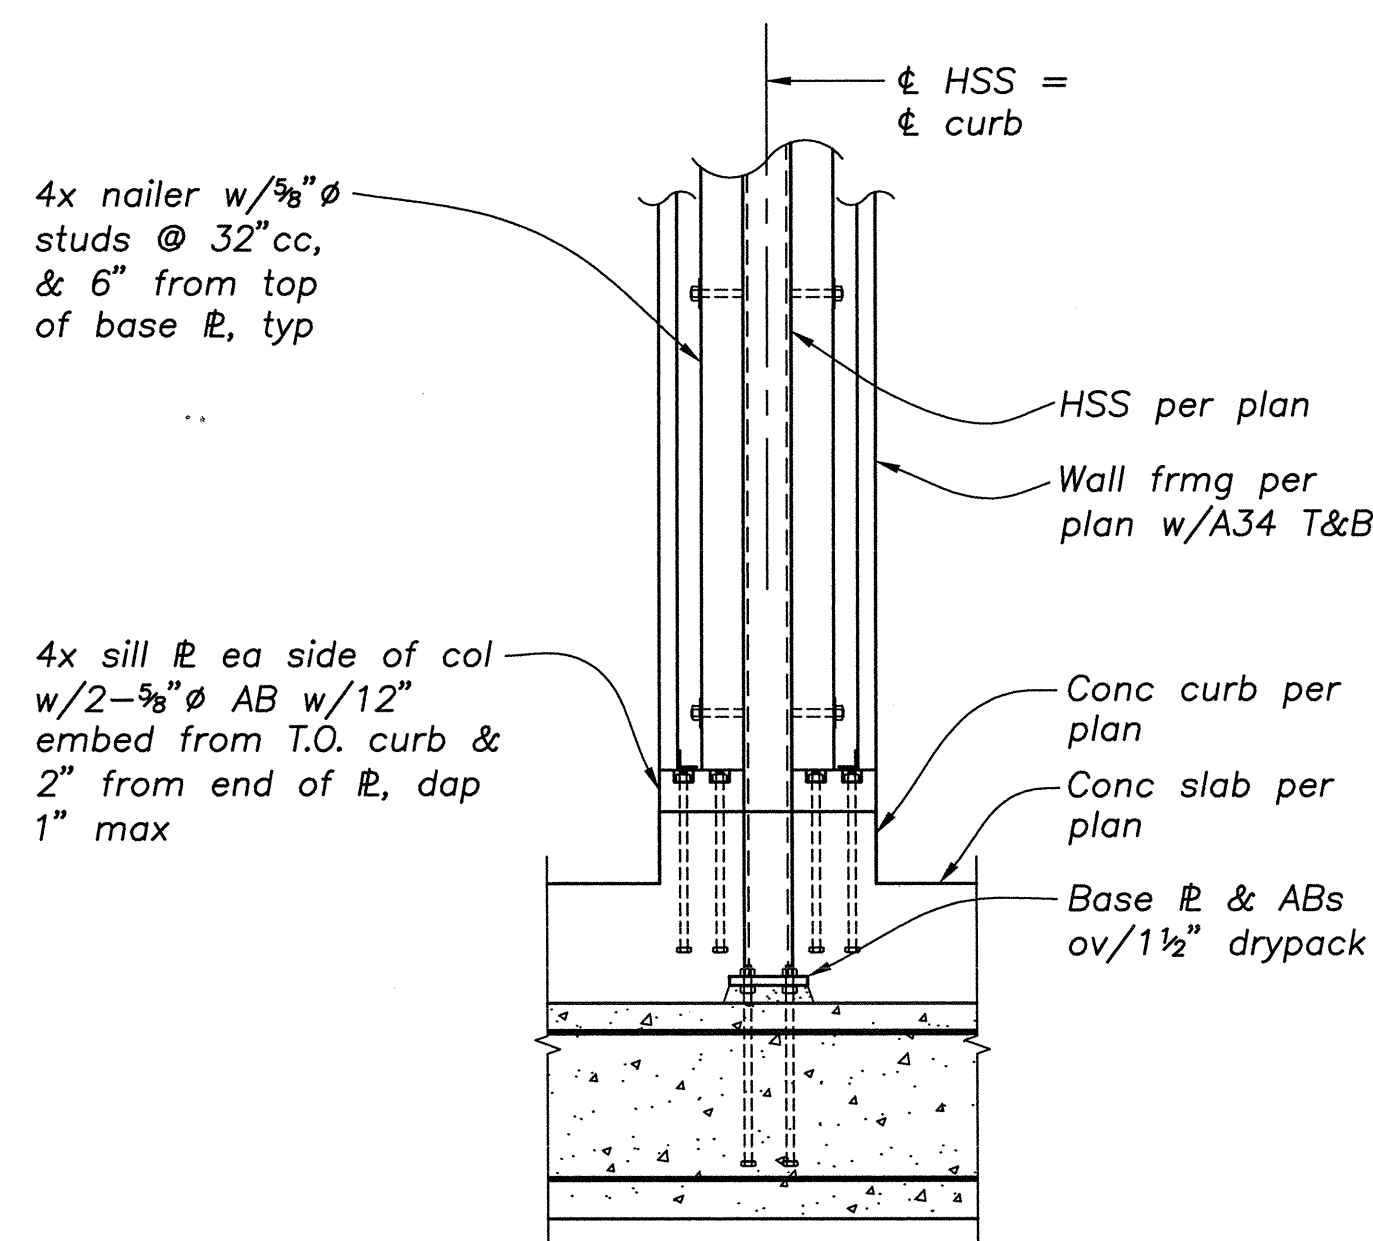


DETAIL 7
3/4\"/>

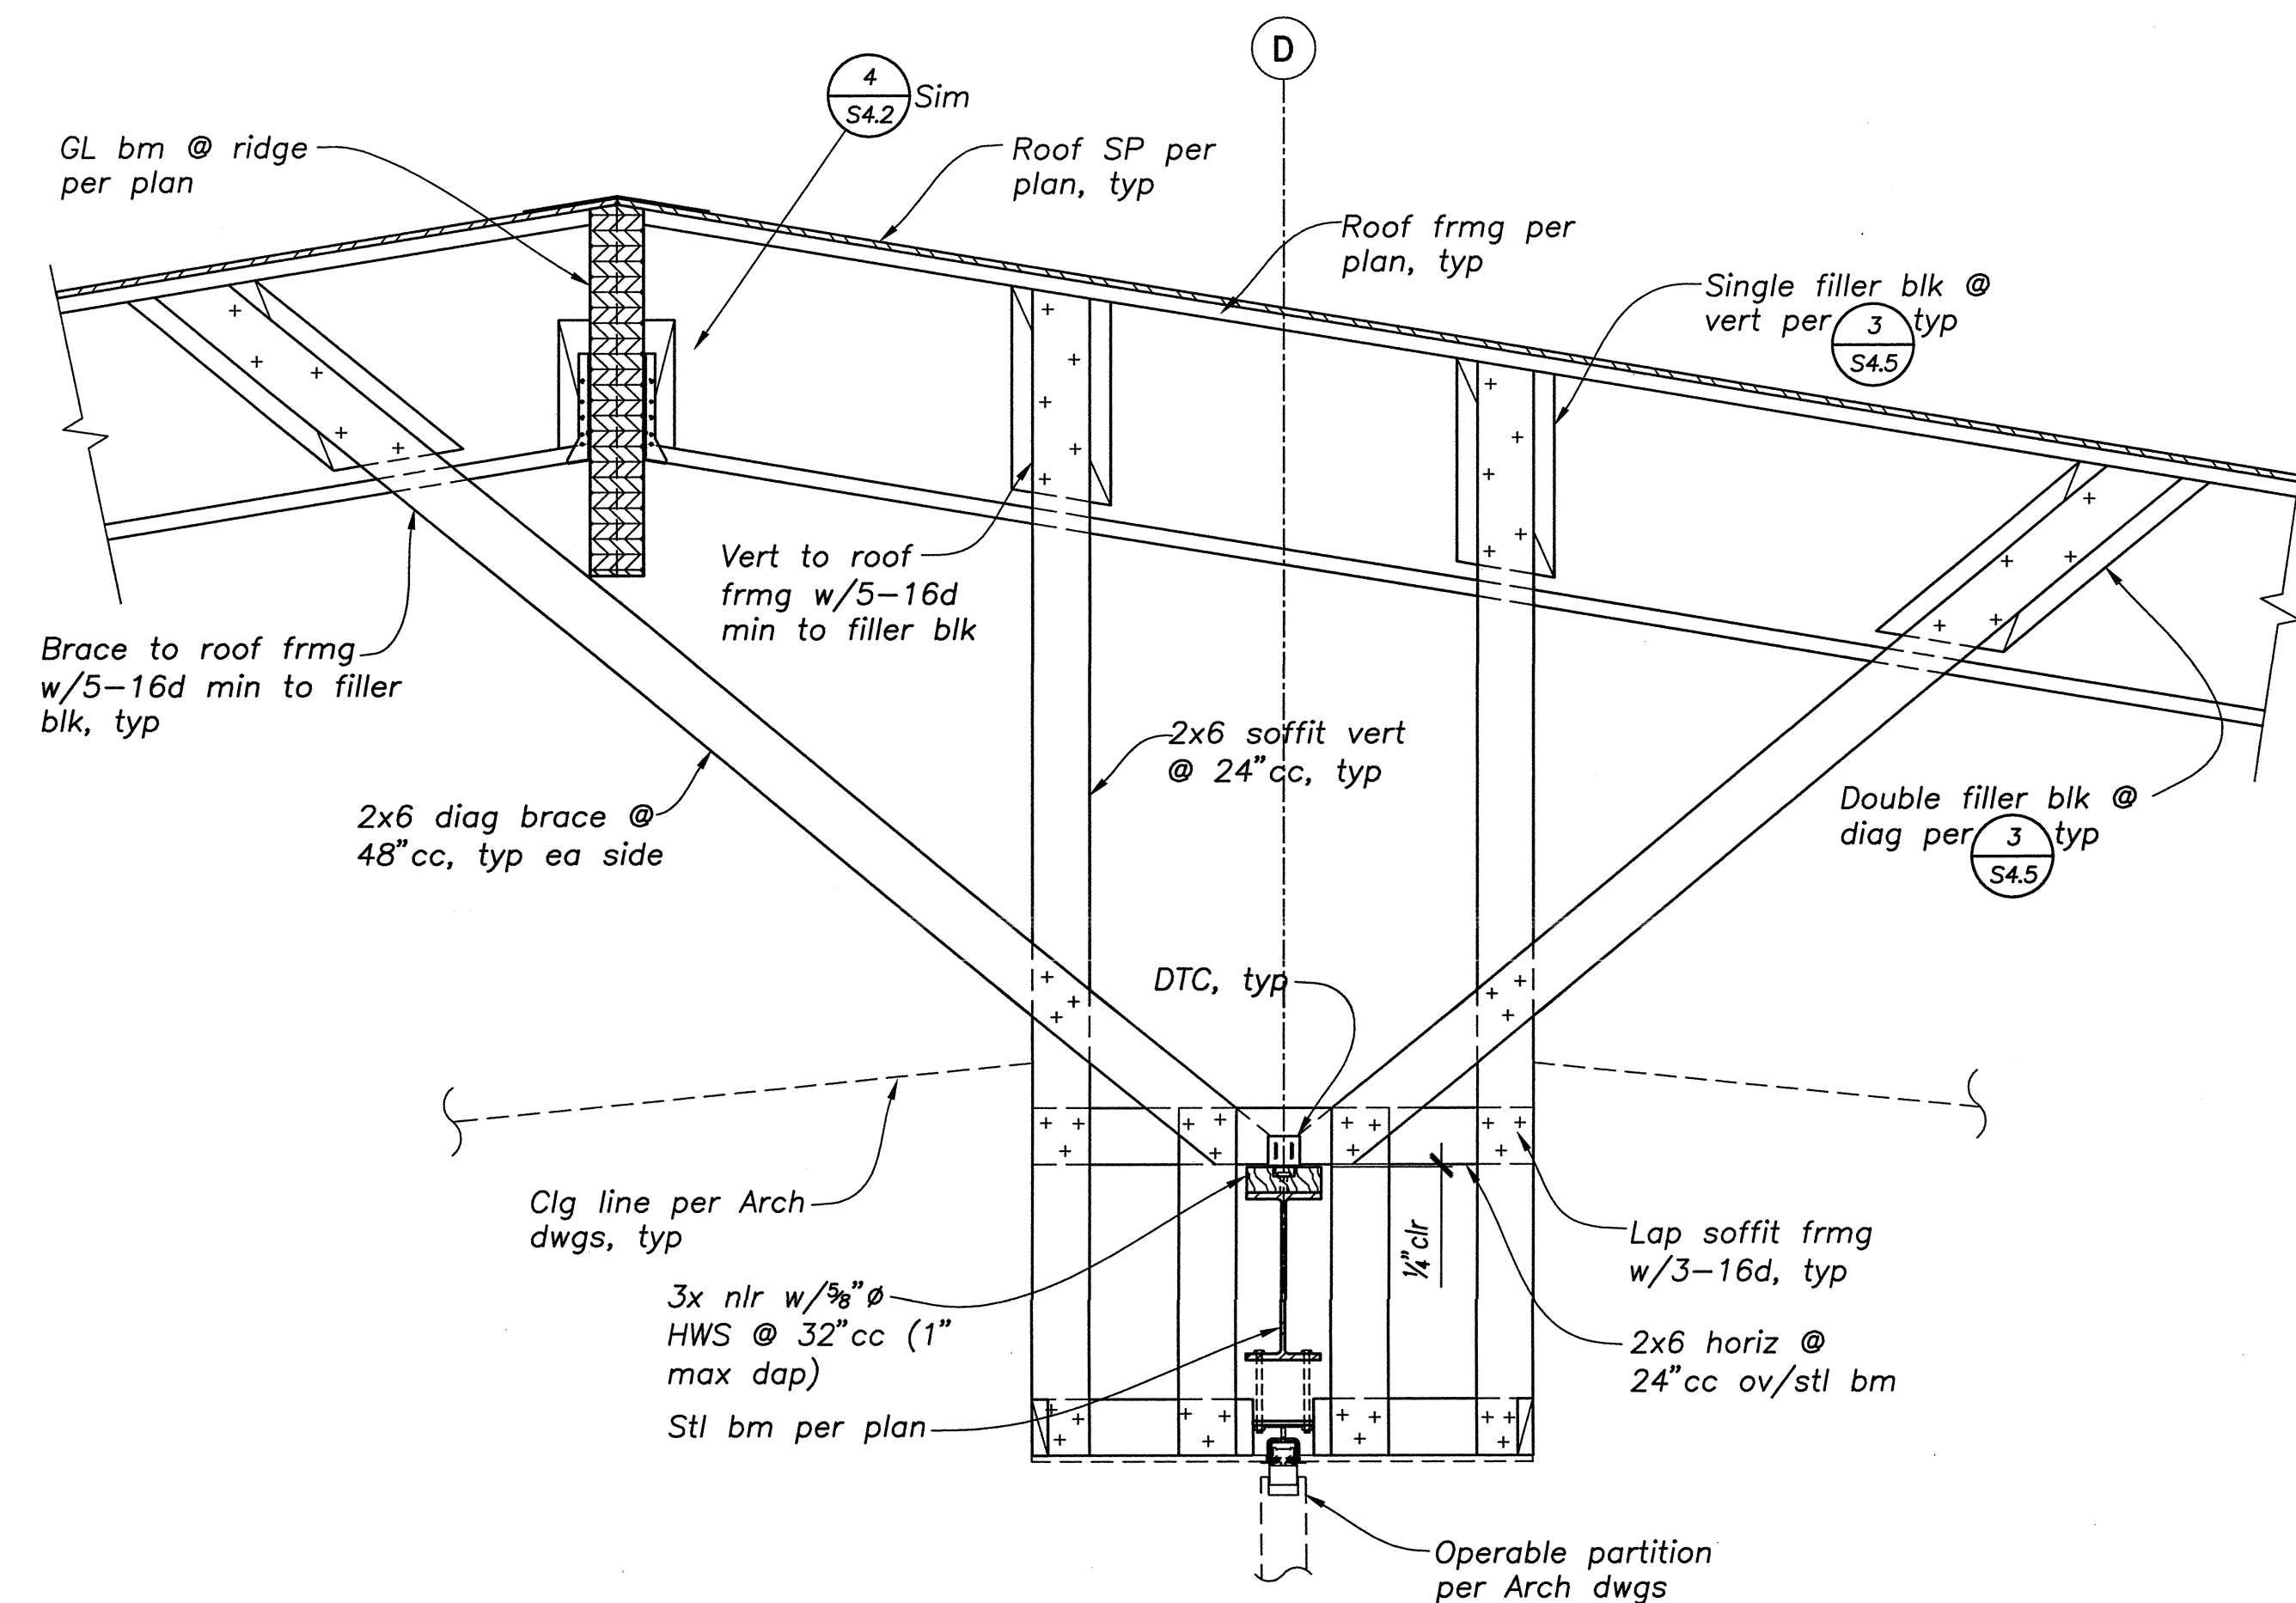

DETAIL 1
3/4\"/>

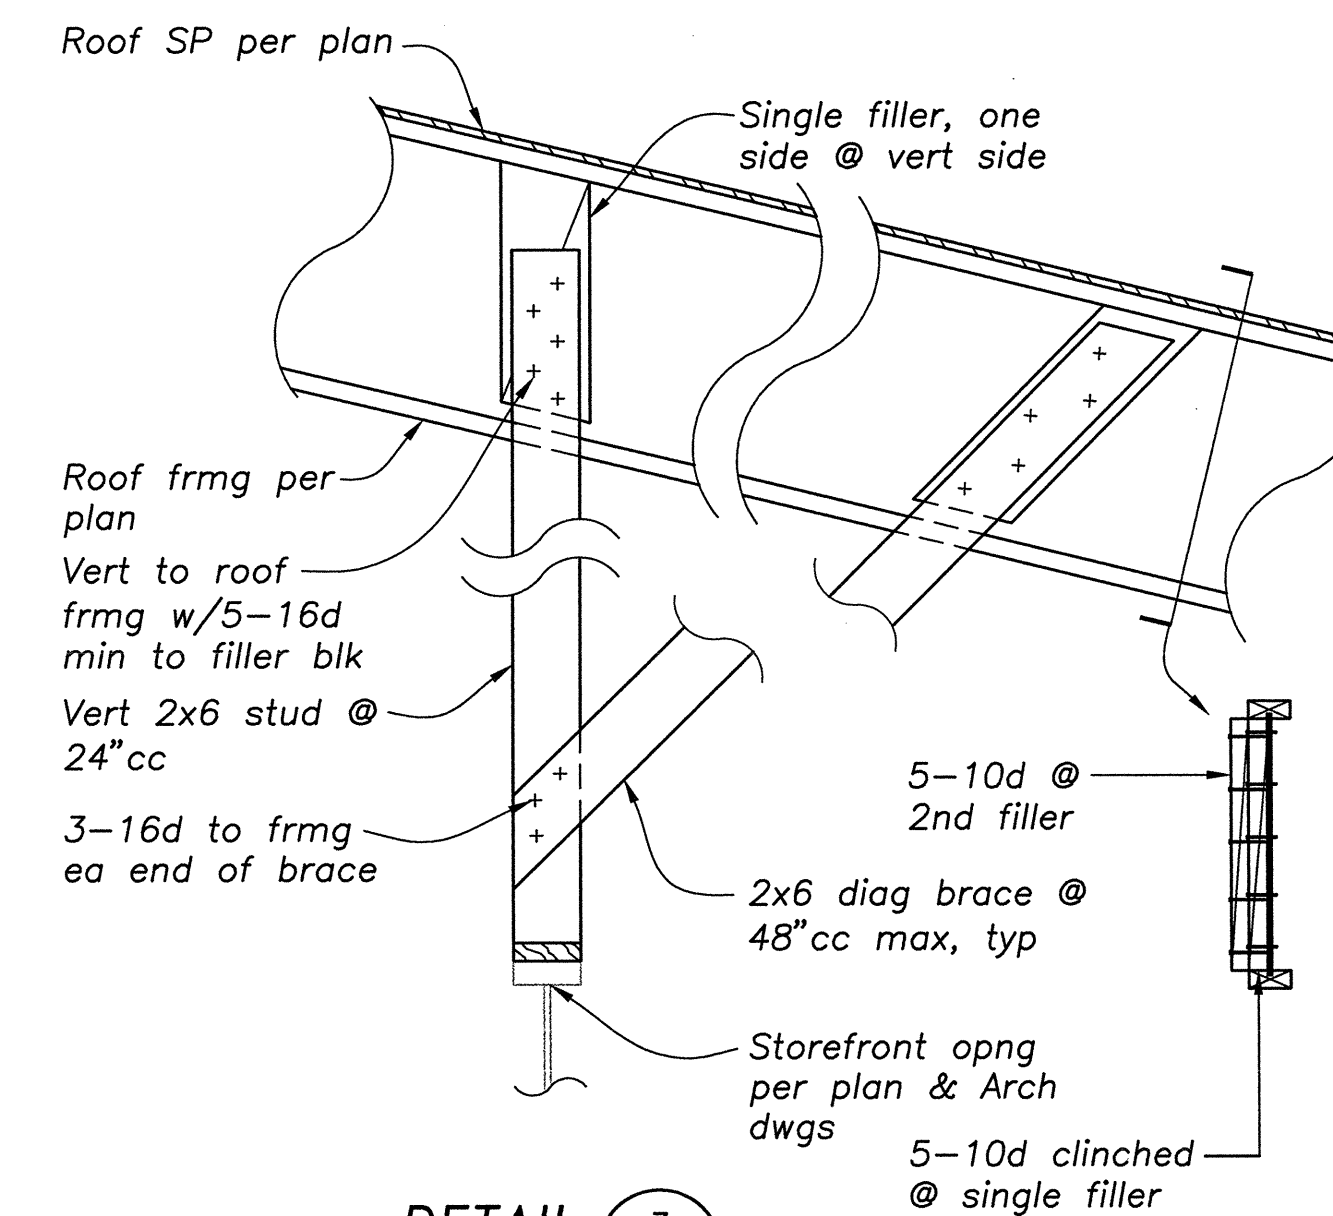

DETAIL 3
3/4\"/>

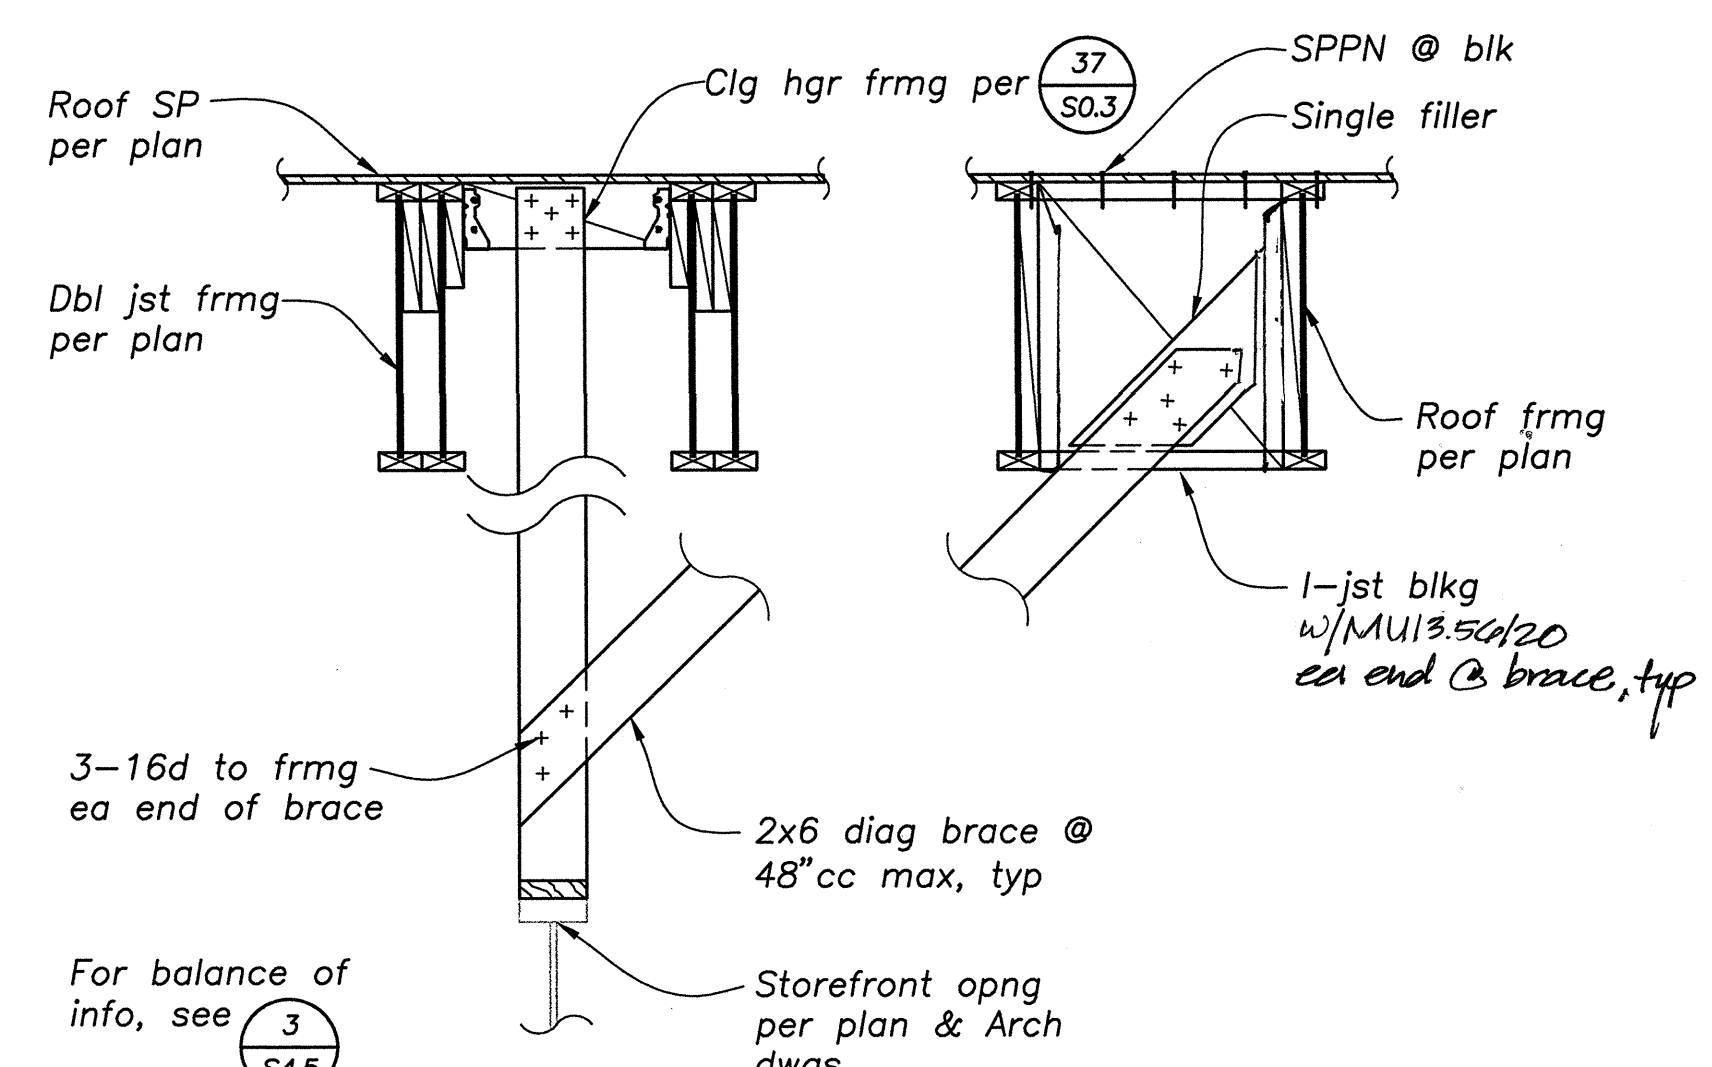


DETAIL 4
3/4\"/>

Dry Creek Joint Elementary School District District Education Center

8849 Cook Riolo Road, Roseville, CA 95747

Dry Creek Joint Elementary School District


FILE NO. 31-15

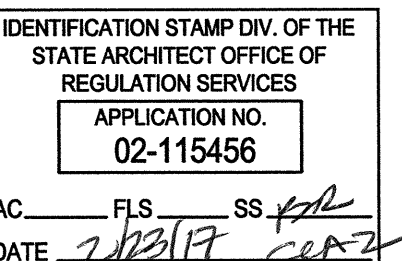

DIVISION OF THE STATE ARCHITECT
revision date: by:

www.barrish.com


barrish pelham
Consulting Engineers
Sacramento, Walnut Creek, Tahoe/Reno

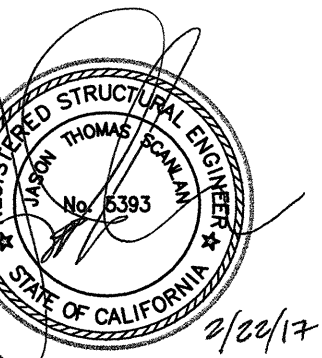

CONSULTANT

nacht&lewis

600 G Street, Suite 100
Sacramento, CA 95811
www.nachtlewis.com
916.329.4000

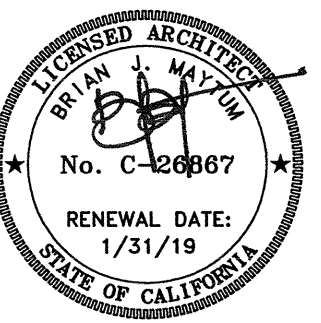

ARCHITECT

INITIAL BOX			
NO.	DWG BY	DATE	REVIEWED

REVISIONS			
NO.	DESCRIPTION	DATE	REV

DATE February 23, 2017

JOB NO. Y1538.00

SHEET TITLE

Miscellaneous
Details

SHEET NO.

S4.5

ONE INCH = TWENTY FEET
ONE-SIXTEENTH INCH = ONE FOOT
ONE-EIGHTH INCH = ONE FOOT
ONE-FOURTH INCH = ONE FOOT
ONE-HALF INCH = ONE FOOT
THREE-FOURTHS INCH = ONE FOOT
ONE INCH = ONE FOOT
ONE AND ONE-HALF INCH = ONE FOOT

ABBREVIATIONS

NOTE: NOT ALL ABBREVIATIONS MAY BE USED ON THESE PLANS.

AB AGGREGATE BASE
AC ASPHALTIC CONCRETE
AD AREA DRAIN
APN ASSESSOR'S PARCEL NUMBER
ARV AIR RELEASE VALVE
ASB AGGREGATE SUB-BASE
BO BLOW-OFF VALVE
BV BUTTERFLY VALVE
BW BACK OF WALK
C/L CENTERLINE
CB CATCH BASIN
CL CLASS
C/M CORRUGATED METAL PIPE
C/TV CABLE TELEVISION
CO CLEANOUT
COMM COMMUNICATION
CONC CONCRETE
CONST. CONSTRUCT
CR CURB RETURN
CS CONCRETE SURFACE
DC DOUBLE CHECK VALVE
DDC DOUBLE DETECTOR CHECK VALVE
DG DECOMPOSED GRANITE
DI DROP INLET
DIA DIAMETER
DIP DUCTILE IRON PIPE
DWS DRAWING
DS DOWNSPOUT
EP ELECTRIC
EP EASEMENT
ESMT EXISTING
FS FIRE SERVICE LINE
FDC FIRE DEPARTMENT CONNECTION
FM FINISHED FLOOR ELEVATION
FH FIRE HYDRANT
GR GAS
GRD GRADE ELEVATION
GV GATE VALVE
HB HOSE BIBB
HDB HEADER BOARD
HDPE HIGH DENSITY POLYETHYLENE PIPE
HP HIGH POINT
INV PIPE INVERT ELEVATION
JP JOINT UTILITY POLE
LF LINEAL FEET
LIP LIP OF GUTTER
LIT LEFT
MS MOWSTRIP
NTS NOT TO SCALE
OH OVERHEAD
PCC PORTLAND CEMENT CONCRETE
PD PLANTER DRAIN
PIV POST INDICATOR VALVE
PL PROPERTY LINE
PP POWER POLE
PUE PUBLIC UTILITY EASEMENT
PVC POLYVINYL CHLORIDE
RCP REINFORCED CONCRETE PIPE
R RADIUS
RIM MANHOLE RIM ELEVATION (SOLID COVER)
RP REDUCED PRESSURE BACKFLOW PREVENTER
RW RIGHT OF WAY
SCH SCHEDULE
SD STORM DRAIN
SDMH STORM DRAIN MANHOLE
SG SUBGRADE ELEVATION
SS SANITARY SEWER
SSMH SANITARY SEWER MANHOLE
STD STANDARD
S/W SIDEWALK
TEL TELEPHONE
TC TOP OF CURB
TD TRENCH DRAIN
TDCB TRENCH DRAIN CATCH BASIN
TP TELEPHONE POLE
TRW TOP OF RETAINING WALL
TSW TOP OF SEAT WALK
TW TOP OF WALK ELEVATION
U UTILITY
UG UNDERGROUND
UON UNLESS OTHERWISE NOTED
VCP VITRIFIED CLAY PIPE
W WATER
W/O WITHOUT
WV WATER VALVE

LEGEND

NOTE: NOT ALL SYMBOLS MAY BE USED ON THESE PLANS.

PROPOSED GRADING & DRAINAGE SYMBOLS:

8" SD STORM DRAIN LINE (SIZE AND FLOW SHOWN)
● STORM DRAIN MANHOLE (SDMH)
— CATCH BASIN (CB)
— DROP INLET (DI)
— AREA DRAIN (AD)
— PLANTER DRAIN (PD) OR FLOOR DRAIN (FD)
— STORM DRAIN CLEANOUT
99.99 ELEVATION
FF=100.00 FINISHED FLOOR ELEVATION
PAD=99.33 BUILDING PAD ELEVATION
CONCRETE SIDEWALK
GRADED DIRECTION FOR DRAINAGE FLOW
SWALE
SLOPE
TREE TO BE REMOVED
RETAINING WALL

PROPOSED SANITARY SEWER SYMBOLS:

8" SS SANITARY SEWER LINE (SIZE AND FLOW SHOWN)
● SANITARY SEWER MANHOLE (SSMH)
— CO SEWER CLEANOUT
— FLUSHER BRANCH


PROPOSED WATER SYMBOLS:

8" W WATER LINE & SIZE
8" FS FIRE LINE & SIZE
— GATE VALVE
— WATER METER
— FIRE HYDRANT ASSEMBLY
— FIRE DEPARTMENT CONNECTION
— DETECTOR CHECK VALVE
— DOUBLE DETECTOR CHECK VALVE
— REDUCED PRESSURE BACKFLOW PREVENTER
— BUTTERFLY VALVE
— AIR RELEASE VALVE + SIZE
— BLOW-OFF VALVE + SIZE
— POST INDICATOR VALVE


PROPOSED GAS SYMBOLS:

8" G GAS LINE & SIZE
— GAS VALVE
— GAS METER

DISTRICT EDUCATION CENTER
8849 COOK RIOLO ROAD
ROSEVILLE, CA 95747
APN 474-080-017

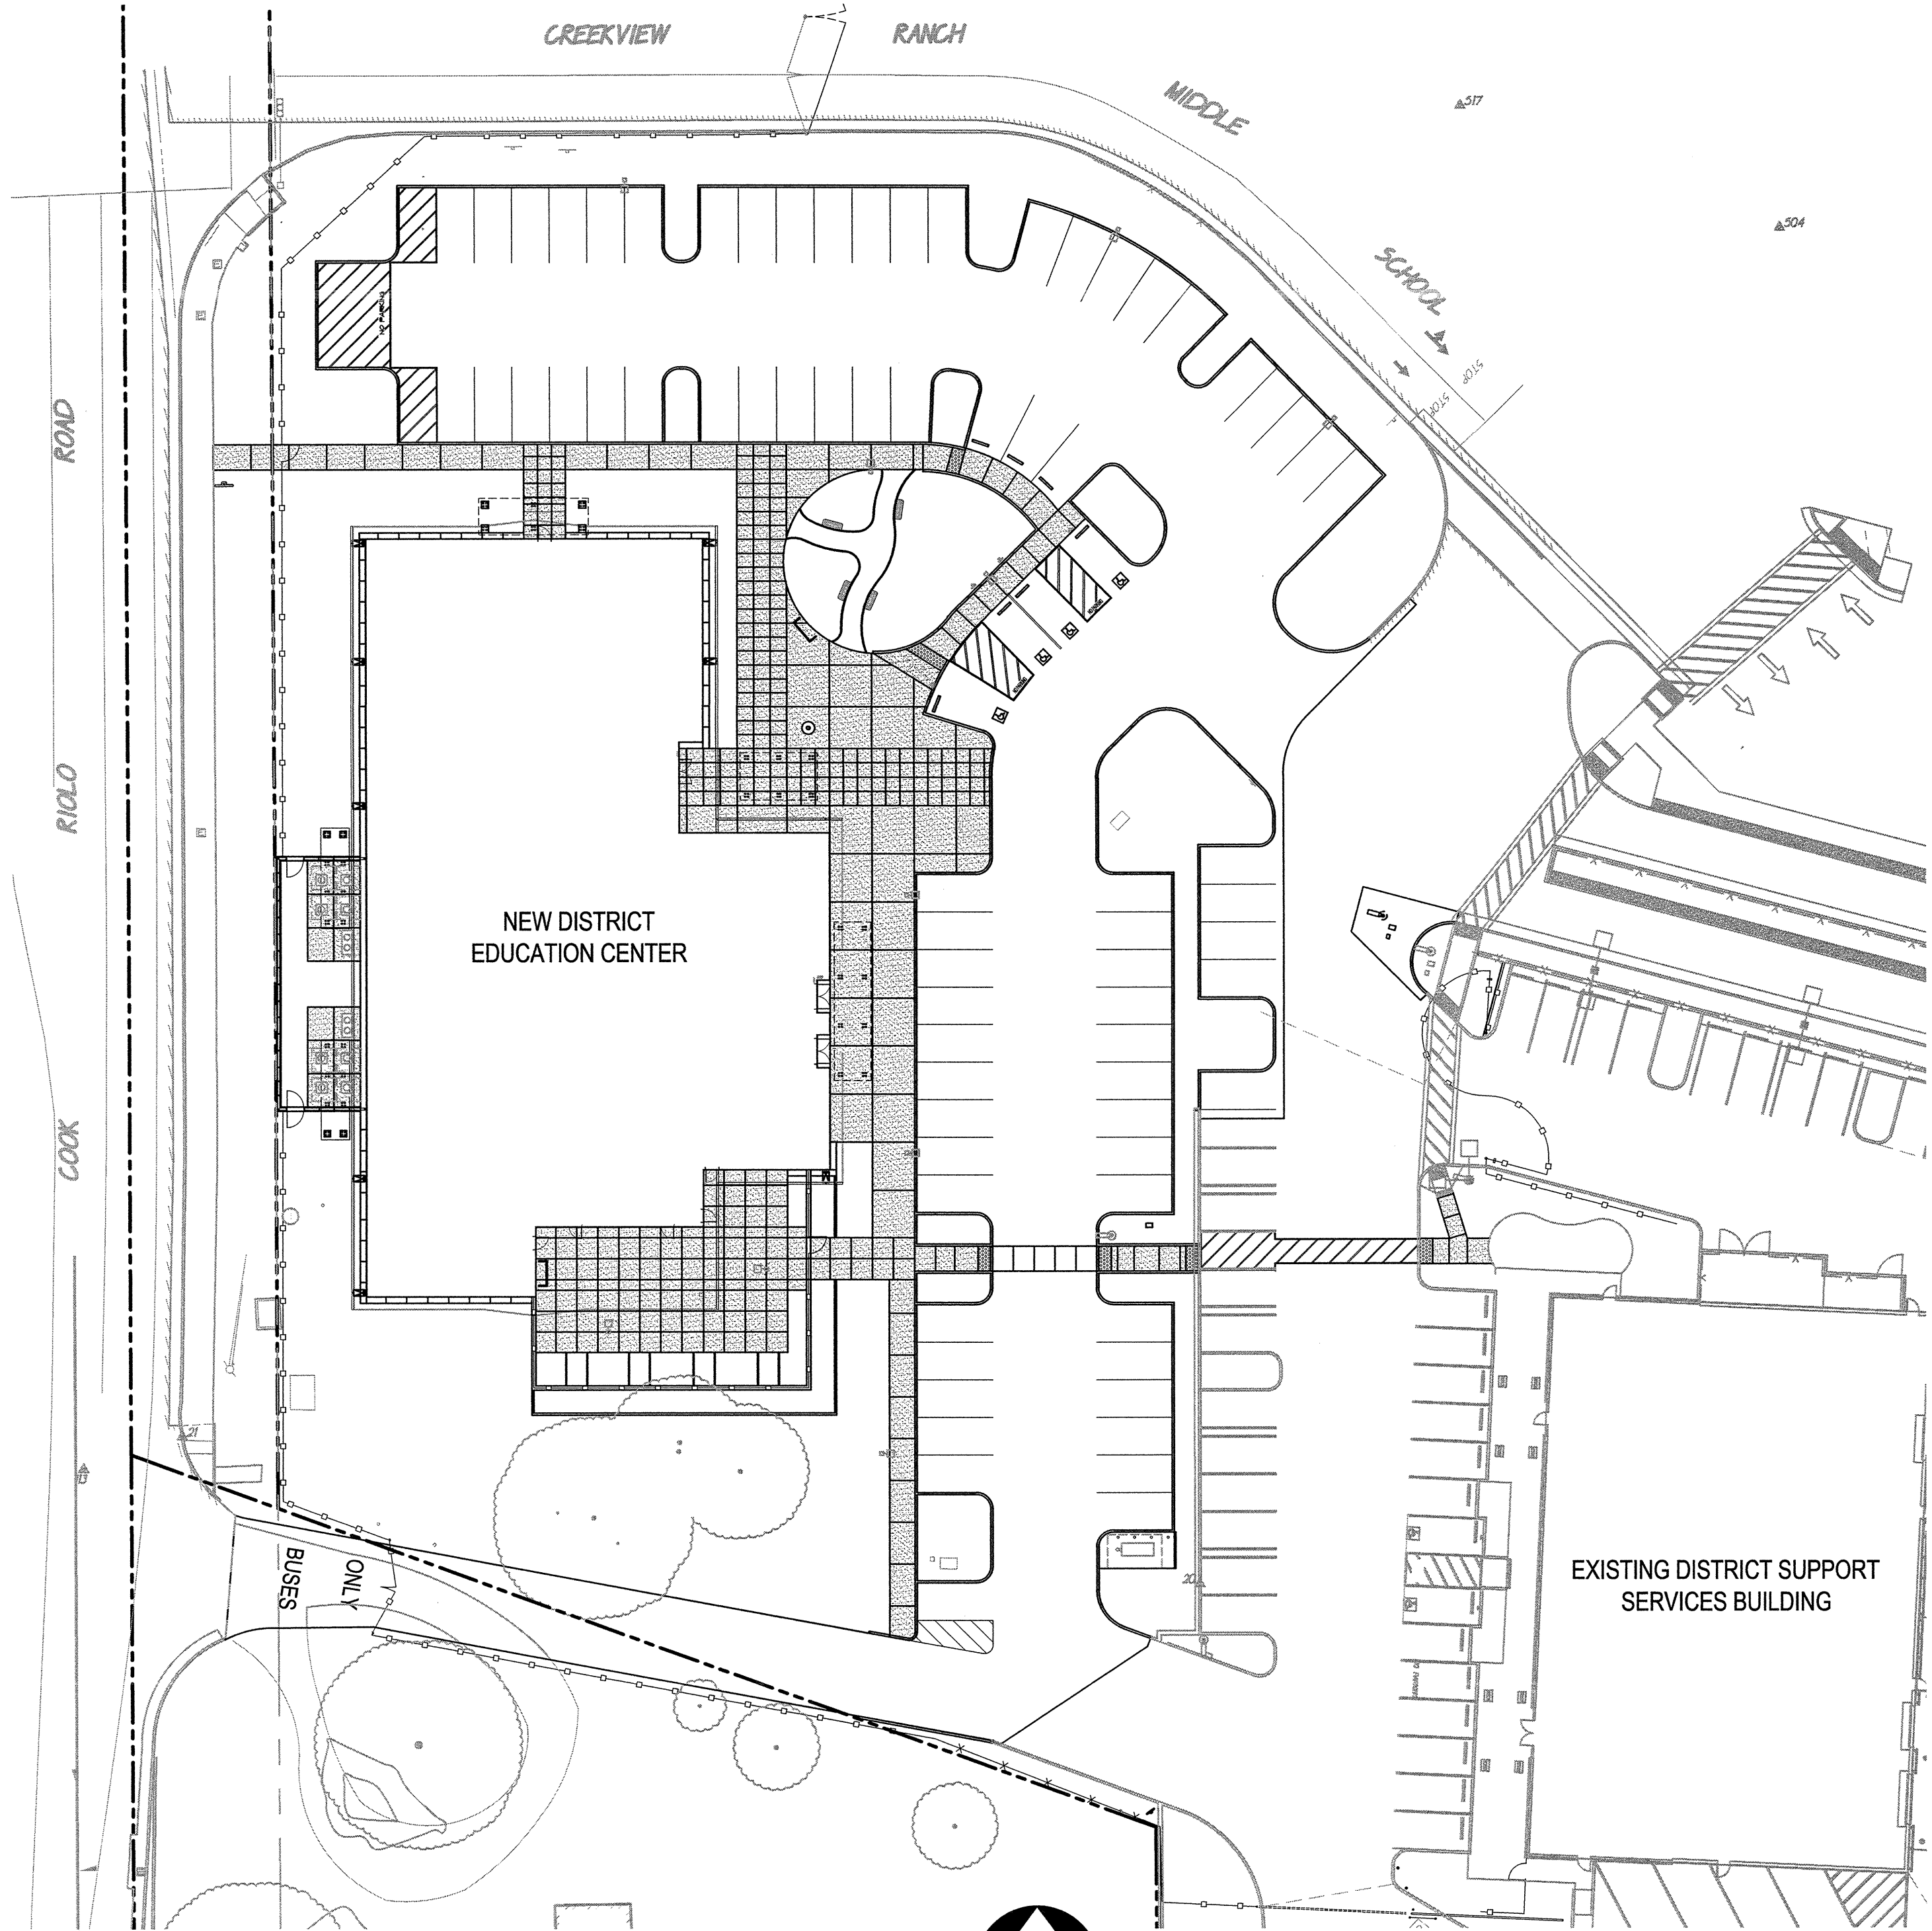

SITE

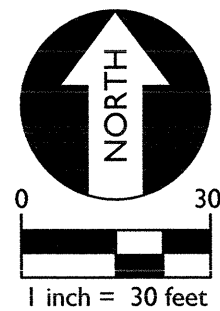

SHEET INDEX

C0.1 COVER SHEET
C0.2 TOPOGRAPHIC SURVEY
C1.1 DEMOLITION PLAN
C1.2 ENGINEERED FILL PLAN
C2.1 GRADING PLAN
C3.1 UTILITY PLAN
C4.1 PAVING PLAN
C4.2 STRIPING PLAN
C4.3 FIRE PROTECTION PLAN
C5.1 EROSION CONTROL PLAN
C6.1 DETAILS
C6.2 DETAILS AND SECTIONS

Dry Creek Joint Elementary School District
District Education Center

8849 Cook Riolo Road, Roseville, CA 95747


Dry Creek Joint Elementary School District

FILE NO. 31-15

IDENTIFICATION STAMP DIV. OF THE
STATE ARCHITECT OFFICE OF
REGULATION SERVICES
APPLICATION NO.
02-115456
DATE 2/10/2017

DIVISION OF THE STATE ARCHITECT


revision date: by:

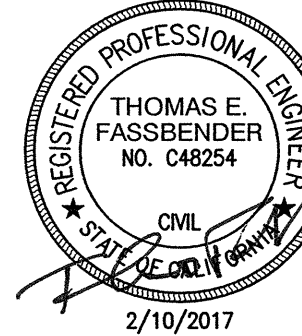

WCE
WARREN CONSULTING ENGINEERS, INC.
1117 WINDFIELD WAY, SUITE 110
EL DORADO HILLS, CA 95672
CONSULTANT

nacht&lewis

600 Q Street, Suite 100
Sacramento, CA 95811
www.nachtandlewis.com
916.329.4000

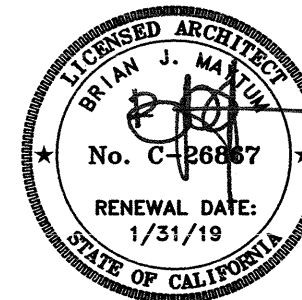

ARCHITECT

INITIAL BOX

NO.	DWG BY	DATE	REVIEWED

REVISIONS

NO.	DESCRIPTION	DATE	REV

DATE February 23, 2017

JOB NO. Y1538.00

SHEET TITLE

Cover Sheet

SHEET NO.

C0.1


SHEET OF TOTAL

ONE INCH = TWENTY FEET
ONE-SIXTEENTH INCH = ONE FOOT
ONE-EIGHTH INCH = ONE FOOT
ONE-FOURTH INCH = ONE FOOT
ONE-HALF INCH = ONE FOOT
THREE-QUARTERS INCH = ONE FOOT
ONE INCH = ONE FOOT
ONE AND ONE-HALF INCH = ONE FOOT

DRY CREEK JOINT ELEMENTARY SCHOOL DISTRICT DISTRICT EDUCATION CENTER

8849 COOK RIOLO ROAD, ROSEVILLE, CA 95747

DRY CREEK JOINT ELEMENTARY SCHOOL DISTRICT

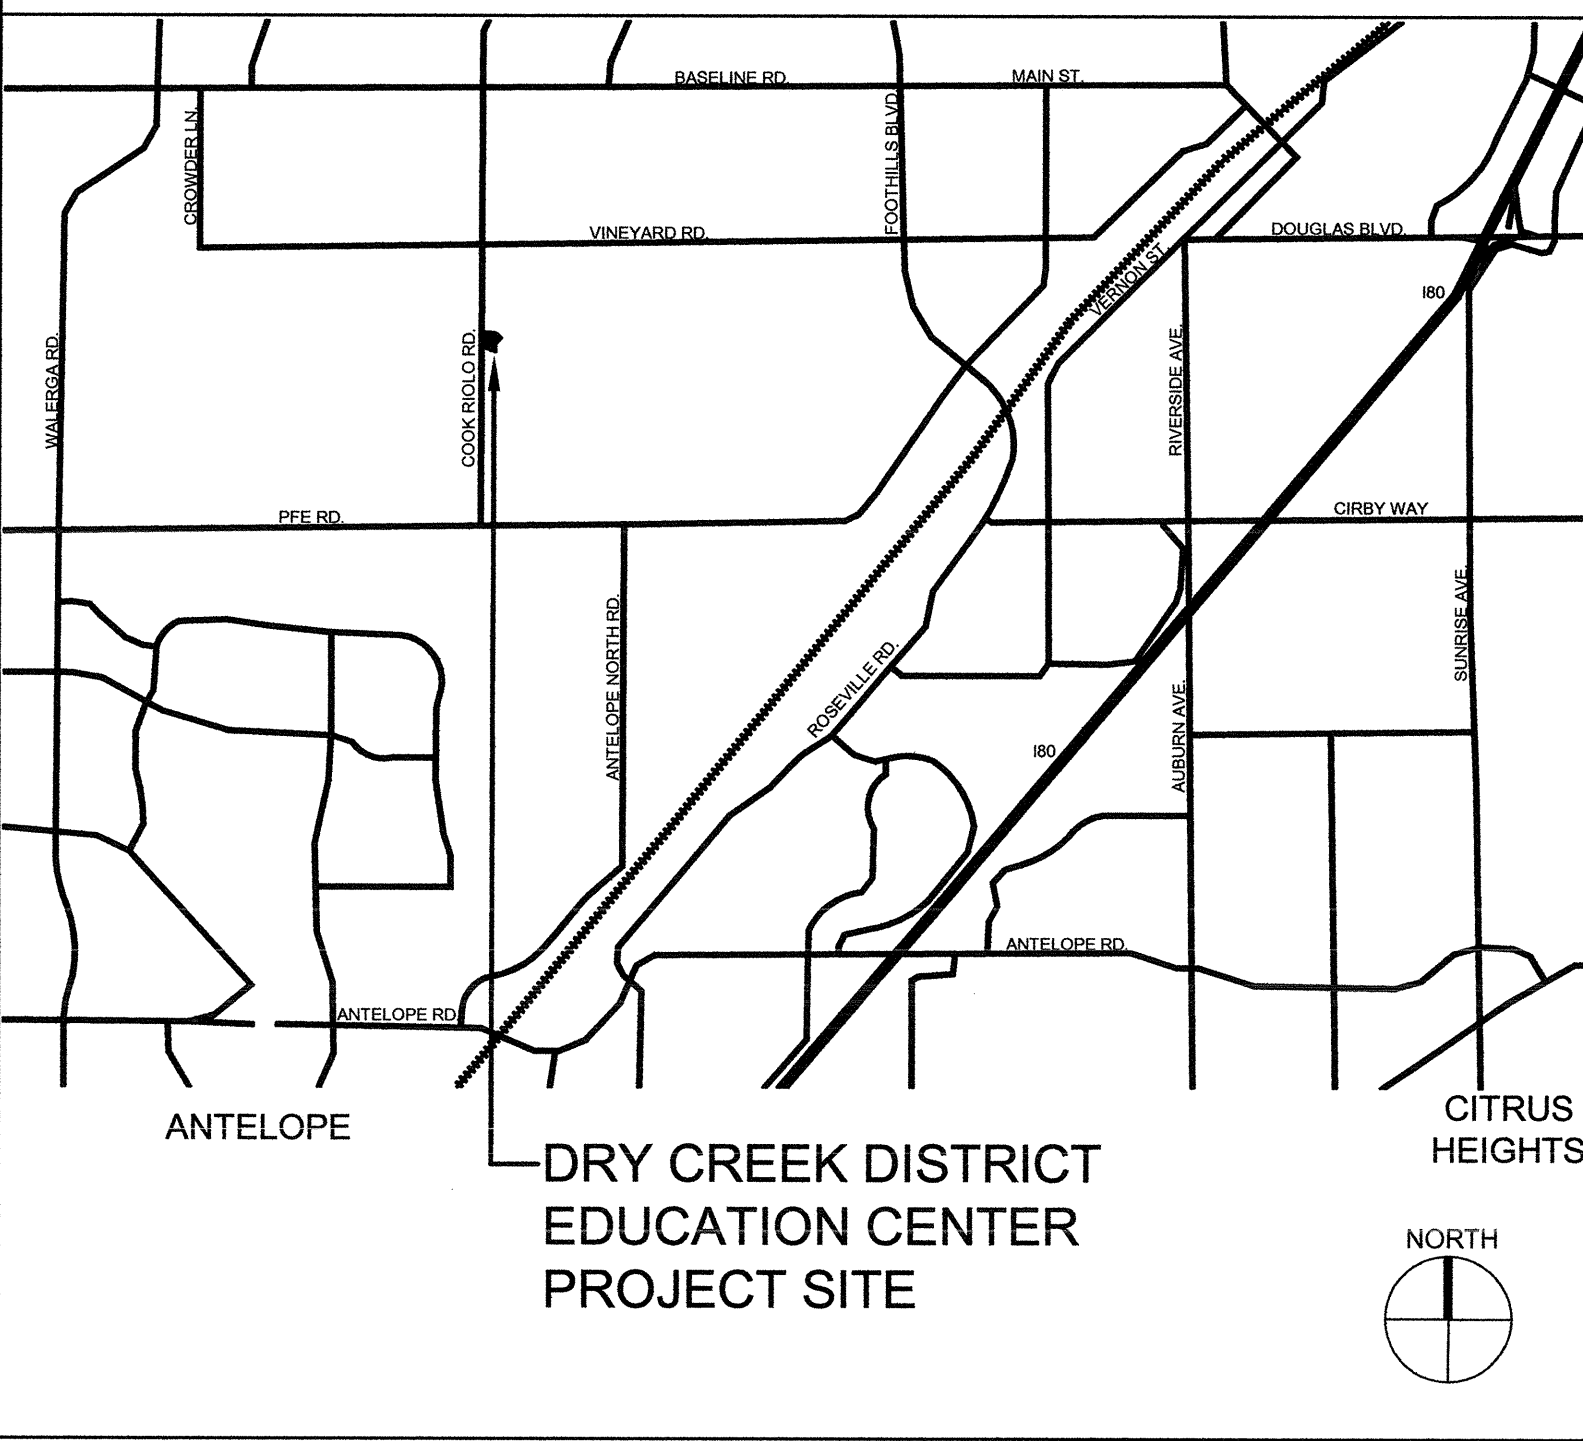APPLICABLE CODES	GENERAL SCOPE OF WORK	PROJECT TEAM	SHEET INDEX
ALL WORK SHALL CONFORM TO THE FOLLOWING AND ALL OTHER APPLICABLE CODES AND ORDINANCES: 2013 BUILDING STANDARDS ADMINISTRATIVE CODE, PART 1, TITLE 24 C.C.R. 2013 CALIFORNIA BUILDING CODE (CBC), PART 2, TITLE 24 C.C.R. (2012 INTERNATIONAL BUILDING CODE WITH 2013 CALIFORNIA AMENDMENTS) 2013 CALIFORNIA ELECTRICAL CODE (CEC), PART 3, TITLE 24 C.C.R. (2011 NATIONAL ELECTRICAL CODE WITH 2013 CALIFORNIA AMENDMENTS) 2013 CALIFORNIA MECHANICAL CODE (CMC), PART 4, TITLE 24 C.C.R. (2012 UNIFORM MECHANICAL CODE WITH 2013 CALIFORNIA AMENDMENTS) 2013 CALIFORNIA PLUMBING CODE (CPC), PART 5, TITLE 24 C.C.R. (2012 UNIFORM PLUMBING CODE WITH 2013 CALIFORNIA AMENDMENTS) 2013 CALIFORNIA ENERGY CODE, PART 6, TITLE 24, C.C.R. 2013 CALIFORNIA FIRE CODE, PART 9 & 11, TITLE 24 C.C.R. (2012 INTERNATIONAL FIRE CODE & 2013 CALIFORNIA AMENDMENTS) 2013 CALIFORNIA REFERENCED STANDARDS, PART 12, TITLE 24 C.C.R. - TITLE 19 C.C.R., PUBLIC SAFETY, STATE FIRE MARSHAL REGULATIONS - CFC CHAPTER 33 - FIRE SAFETY DURING CONSTRUCTION AND DEMOLITION.	CONSTRUCTION OF NEW DISTRICT EDUCATION BUILDING AND ASSOCIATED SITE DEVELOPMENT WORK ON EXISTING DISTRICT-OWNED SITE. BUILDING WILL SERVE AS THE CENTRAL ADMINISTRATIVE OFFICES AND BOARD OF TRUSTEE'S MEETING FACILITIES FOR THE DISTRICT. BUILDING IS NOT REGULARLY USED BY STUDENTS BUT WILL BE USED FOR DISTRICT EDUCATION STAFF TRAINING AND MEETINGS AND OPEN TO THE PUBLIC FOR COMMUNITY MEETINGS AND ACTIVITIES. TOTAL NEW BUILDING AREA: 16,245 S.F. TOTAL SITE AREA: 1.8 ACRES VICINITY MAP  DRY CREEK DISTRICT EDUCATION CENTER PROJECT SITE	OWNER: DRY CREEK JOINT ELEMENTARY SCHOOL DISTRICT 9707 COOK RIOLO ROAD ROSEVILLE, CA 95747 PHONE: (916) 770-8883 CONTACT: SHAUN SCHONDELMAYER ARCHITECT: NACHT & LEWIS ARCHITECTS 600 Q STREET, SUITE 100 SACRAMENTO, CALIFORNIA 95811 PHONE: (916) 329-4000 CONTACT: BRIAN MAYTUM (ARCH. OF REC.) CHRIS FLATT (SR. PROJ. ARCH.) STRUCTURAL ENGINEER: BARRISH PELHAM & ASSOCIATES, INC. 3001 E STREET SACRAMENTO, CALIFORNIA 95816 PHONE: (916) 418-9100 CONTACT: JASON SCANLAN CIVIL ENGINEER: WARREN CONSULTING ENGINEERS, INC. 1117 WINDFIELD WAY, SUITE 110 EL DORADO HILLS, CALIFORNIA 95762 PHONE: (916) 985-1870 CONTACT: TOM FASSBENDER MECHANICAL/PLUMBING ENGINEER: CAPITAL ENGINEERING CONSULTANTS, INC. 11020 SUN CENTER DRIVE, SUITE 100 RANCHO CORDOVA, CALIFORNIA 95670 PHONE: (916) 851-3528 CONTACT: MIKE MINGE ELECTRICAL ENGINEER: HARRY A. YEE & ASSOCIATES 4920 FREEPORT BLVD. SACRAMENTO, CALIFORNIA 95822 PHONE: (916) 454-5319 CONTACT: DAVID YU LANDSCAPE ARCHITECT: MTW GROUP 10411 OLD PLACERVILLE ROAD, SUITE 205 SACRAMENTO, CALIFORNIA 95827 PHONE: (916) 369-3990 CONTACT: BRYAN WALKER	T0 TITLE SHEET CIVIL C0.1 COVER SHEET C0.2 TOPOGRAPHIC SURVEY C1.1 DEMOLITION PLAN C1.2 ENGINEERED FILL PLAN C2.1 GRADING PLAN C3.1 UTILITY PLAN C4.1 PAVING PLAN C4.2 STRIPING PLAN C4.3 FIRE PROTECTION PLAN C5.1 EROSION CONTROL PLAN C6.1 DETAILS C6.2 DETAILS LANDSCAPE L0.1 LANDSCAPE AND IRRIGATION DEMOLITION PLAN L1.1 TREE PLANTING PLAN L2.1 SHRUB & GROUNDCOVER PLANTING PLAN L3.1 SPRINKLER IRRIGATION PLAN L4.1 LANDSCAPE PLANTING DETAILS L4.2 SPRINKLER IRRIGATION DETAILS L4.3 SPRINKLER IRRIGATION CHARTS ARCHITECTURAL A0.0 BUILDING CODE ANALYSIS PLAN A0.1 OVERALL SITE PLAN A0.2 DEMOLITION SITE PLAN A0.3 DETAILED SITE PLAN A0.4 ENLARGED SITE PLANS A0.5 ENLARGED SITE PLANS & DETAILS A0.6 SITE & GATE DETAILS A0.7 ENLARGED PERGOLA PLANS & DETAILS A0.8 ENLARGED PERGOLA PLANS & DETAILS A1.0 FLOOR PLAN A2.0 REFLECTED CEILING PLAN A2.1 ACOUSTIC CEILING DETAILS A2.2 ACOUSTIC CEILING DETAILS A3.0 EXTERIOR ELEVATIONS A3.1 ENLARGED EXTERIOR ELEVATIONS A4.0 BUILDING SECTIONS A4.1 BUILDING SECTIONS A4.2 BUILDING SECTIONS A5.0 ROOF PLAN A6.1 OPENING SCHEDULE A7.0 ENLARGED PLANS A7.1 INTERIOR FINISH PLAN A7.1.1 FLOOR PATTERN FINISH PLAN A7.2 CASEWORK & EQUIPMENT PLAN A7.3 CASEWORK ELEVATIONS & DETAILS A7.4 INTERIOR ELEVATIONS A7.5 INTERIOR ELEVATIONS A8.0 WALL TYPES & DETAILS A8.1 DETAILS A8.2 DETAILS A8.3 DETAILS A8.4 WALL TYPES AND DETAILS A8.5 WALL TYPES AND DETAILS MECHANICAL M0.1 MECHANICAL SCHEDULES, LEGEND & NOTES M0.2 MECHANICAL SCHEDULES M0.3 MECHANICAL SCHEDULES M0.4 CA ENERGY COMPLIANCE FORMS M0.5 CA ENERGY COMPLIANCE FORMS M0.6 CA ENERGY COMPLIANCE FORMS M0.7 CA ENERGY COMPLIANCE FORMS M1.0 MECHANICAL FLOOR PLAN M1.1 MECHANICAL REFRIGERANT PIPING FLOOR PLAN M1.2 MECHANICAL PARTIAL FLOOR PLAN M4.0 MECHANICAL SECTIONS M4.1 MECHANICAL SECTIONS M5.1 MECHANICAL DETAILS M5.2 MECHANICAL DETAILS M5.3 MECHANICAL DETAILS M7.1 MECHANICAL CONTROLS M7.2 MECHANICAL CONTROL/PIPING DIAGRAM M7.3 MECHANICAL CONTROL/PIPING DIAGRAM M7.4 MECHANICAL WIRING DIAGRAM M7.5 MECHANICAL WIRING DIAGRAM CONTINUED PLUMBING P0.1 PLUMBING LEGENDS, & NOTES P0.2 PLUMBING FIXTURE SPEC. & CONNECTION SCHEDULE P1.0 PLUMBING SITE PLAN P1.1 PLUMBING GAS SITE CONNECTION PLAN P2.0 PLUMBING FLOOR PLAN P2.1 PLUMBING PARTIAL BELOW FLOOR PIPING PLAN P2.2 PLUMBING PARTIAL MECHANICAL ATTIC PLAN P5.1 PLUMBING DETAILS P5.2 PLUMBING DETAILS FIRE PROTECTION FP0.1 FIRE PROTECTION NOTES, LEGEND FP0.2 FIRE PROTECTION DETAILS FP0.3 FIRE PROTECTION SITE PLAN FP1.0 FIRE PROTECTION FLOOR PLAN FP2.0 FIRE PROTECTION REFLECTED CEILING PLAN FP4.0 FIRE PROTECTION SECTIONS ELECTRICAL E0.1 ELECTRICAL SYMBOLS, LISTS, ABBREVIATIONS & NOTES E0.2 ELECTRICAL INTERIOR TITLE 24 E0.3 ELECTRICAL EXTERIOR TITLE 24 E1.1 DEMOLITION SITE PLAN E1.2 ELECTRICAL SITE PLAN E2.1 LIGHTING FLOOR PLAN E3.1 POWER FLOOR PLAN E3.1.1 POWER EQUIPMENT PLAN E4.1 SIGNAL FLOOR PLAN E5.1 FIRE ALARM FLOOR PLAN E5.2 FIRE ALARM SCHEDULES, CALCULATIONS, NOTES & DETAILS E5.3 FIRE ALARM RISER DIAGRAM, SCHEDULE, CALCS E5.4 FIRE ALARM DETAILS & DIAGRAMS E7.1 ONE LINE DIAGRAM & SCHEDULES E8.1 LIGHT FIXTURE SCHEDULE, NOTES & DETAILS E8.2 LIGHT FIXTURE DETAILS E9.1 ELECTRICAL SCHEDULES E9.2 ELECTRICAL DETAILS STRUCTURAL S0.1 GENERAL NOTES S0.2 TYPICAL DETAILS S0.3 TYPICAL DETAILS S2.1 FOUNDATION PLAN & SHEAR WALL DIAGRAM S2.2 ROOF FRAMING PLANS S2.3 MECH ATTIC FLOOR, PARTIAL ROOF AND CEILING FRAMING PLANS S3.1 BUILDING SECTIONS S3.2 WALL FRAMING ELEVATIONS S3.3 WALL FRAMING ELEVATIONS S4.1 FOUNDATION DETAILS S4.2 ROOF FRAMING DETAILS S4.3 ROOF FRAMING DETAILS S4.4 FLOOR FRAMING DETAILS S4.5 MISCELLANEOUS DETAILS
GENERAL NOTES - CONTRACTOR SHALL FIELD VERIFY ALL DIMENSIONS AND EXISTING CONDITIONS AT THE SITE AND SHALL REPORT ANY DISCREPANCIES IN WRITING TO THE CONSTRUCTION MANAGER BY THE MEANS OF AN REQUEST FOR INFORMATION (RFI) OR AS PART OF THE APPLICABLE SHOP DRAWING/SUBMITTAL. - SPECIFIC ITEMS NOTED TO BE VERIFIED OR FIELD VERIFIED ARE REQUIRED TO BE VERIFIED PRIOR TO ORDERING MATERIALS OR PROCEEDING WITH THE WORK. - CONTRACTOR IS RESPONSIBLE FOR ALL INCIDENTAL WORK NECESSARY TO COMPLETE THE INSTALLATION OF NEW WORK. THIS INCLUDES, BUT IS NOT LIMITED TO, THE REMOVAL AND/OR REINSTALLATION OR ALL EXISTING ITEMS, OF PORTIONS OF THE EXISTING CONSTRUCTION WHETHER SHOWN OR NOT. - THE EXISTING FACILITY HAS LEAD CONTAINING MATERIAL IN VARIOUS LOCATIONS. ANY PART OF THE WORK REQUIRING REMOVAL OF LEAD CONTAINING MATERIAL SHALL BE PERFORMED IN ACCORDANCE WITH THE LEAD ABATEMENT SPECIFICATIONS IN THE PROJECT MANUAL. - ALL WORK, MATERIALS, METHODS, ETC. SHALL CONFORM TO ALL GOVERNING BUILDING CODES AND REGULATIONS. - ANY CONFLICT BETWEEN THESE PLANS AND EXISTING CONDITIONS SHALL BE BROUGHT TO THE IMMEDIATE ATTENTION OF THE ARCHITECT. - ALL WORK SHALL BE IN COMPLETE CONFORMANCE WITH MANUFACTURER'S SPECIFICATIONS AND RECOMMENDATIONS OR AS OTHERWISE OUTLINED IN THE SPECIFICATIONS. - USE OF ANY NEW MATERIALS CONTAINING LEAD OR ASBESTOS IS PROHIBITED. - DETAILS, MATERIALS AND SCOPE OF WORK SHALL BE CONSIDERED TYPICAL FOR ALL SIMILAR CONDITIONS UNLESS SPECIFICALLY NOTED OTHERWISE. - THE TERM "TYPICAL" OR "(TYP.)" SHALL BE CONSTRUED TO MEAN APPLYING TO ALL LIKE OR SIMILAR CONDITIONS IN THE AREAS DESIGNATED FOR WORK SCOPE. - ALL ITEMS NOTED TO BE DEMOLISHED SHALL BE REMOVED FROM THE SITE AND PROPERLY DISPOSED OF. IF ITEMS ARE INDICATED TO BE SALVAGED BACK TO OWNER, CONTRACTOR SHALL MAKE ARRANGEMENTS WITH OWNER FOR THE SAFE TRANSFER OF THESE ITEMS. IF ITEMS NEED TO BE REMOVED TO PROGRESS WITH WORK, CONTRACTOR SHALL SAFELY STORE SALVAGED ITEMS UNTIL ARRANGEMENTS CAN BE MADE FOR THE OWNER TO COLLECT. - PER CALGREEN STANDARDS CODE, 5.408.1 - CONSTRUCTION WASTE MANAGEMENT, CONTRACTOR SHALL RECYCLE OR SALVAGE FOR RE-USE A MINIMUM OF 65% OF NON-HAZARDOUS CONSTRUCTION AND DEMOLISHED WASTE MATERIALS.			

Dry Creek Joint Elementary School District
District Education Center

8849 Cook Riolo Road, Roseville, CA 95747

Dry Creek Joint Elementary School District

FILE NO. 31-15

IDENTIFICATION STAMP DIV. OF THE
STATE ARCHITECT OFFICE OF
REGULATION SERVICES

APPLICATION NO.
02-115456

DATE 2/23/17 CCSEA 2

DIVISION OF THE STATE ARCHITECT

revision date: _____ by: _____

CONSULTANT

nacht&lewis

600 Q Street, Suite 100
Sacramento, CA 95811
www.nachtlewis.com
916.329.4000

RECORDED ARCHITECT
No. C-22887
RENEWAL DATE: 1/31/19
STATE OF CALIFORNIA

ARCHITECT

INITIAL BOX			
NO.	DWG BY	DATE	REVIEWED

REVISIONS

NO.	DESCRIPTION	DATE	REV'D
	100% design development	7/6/16	
	75% construction documents	8/20/16	
	DSA submittal	12/31/16	
	DSA approval	02/23/17	

DATE February 23, 2017

JOB NO. Y1538.00

SHEET TITLE

Title Sheet

SHEET NO.

T0

SHEET ____ OF ____ TOTAL